


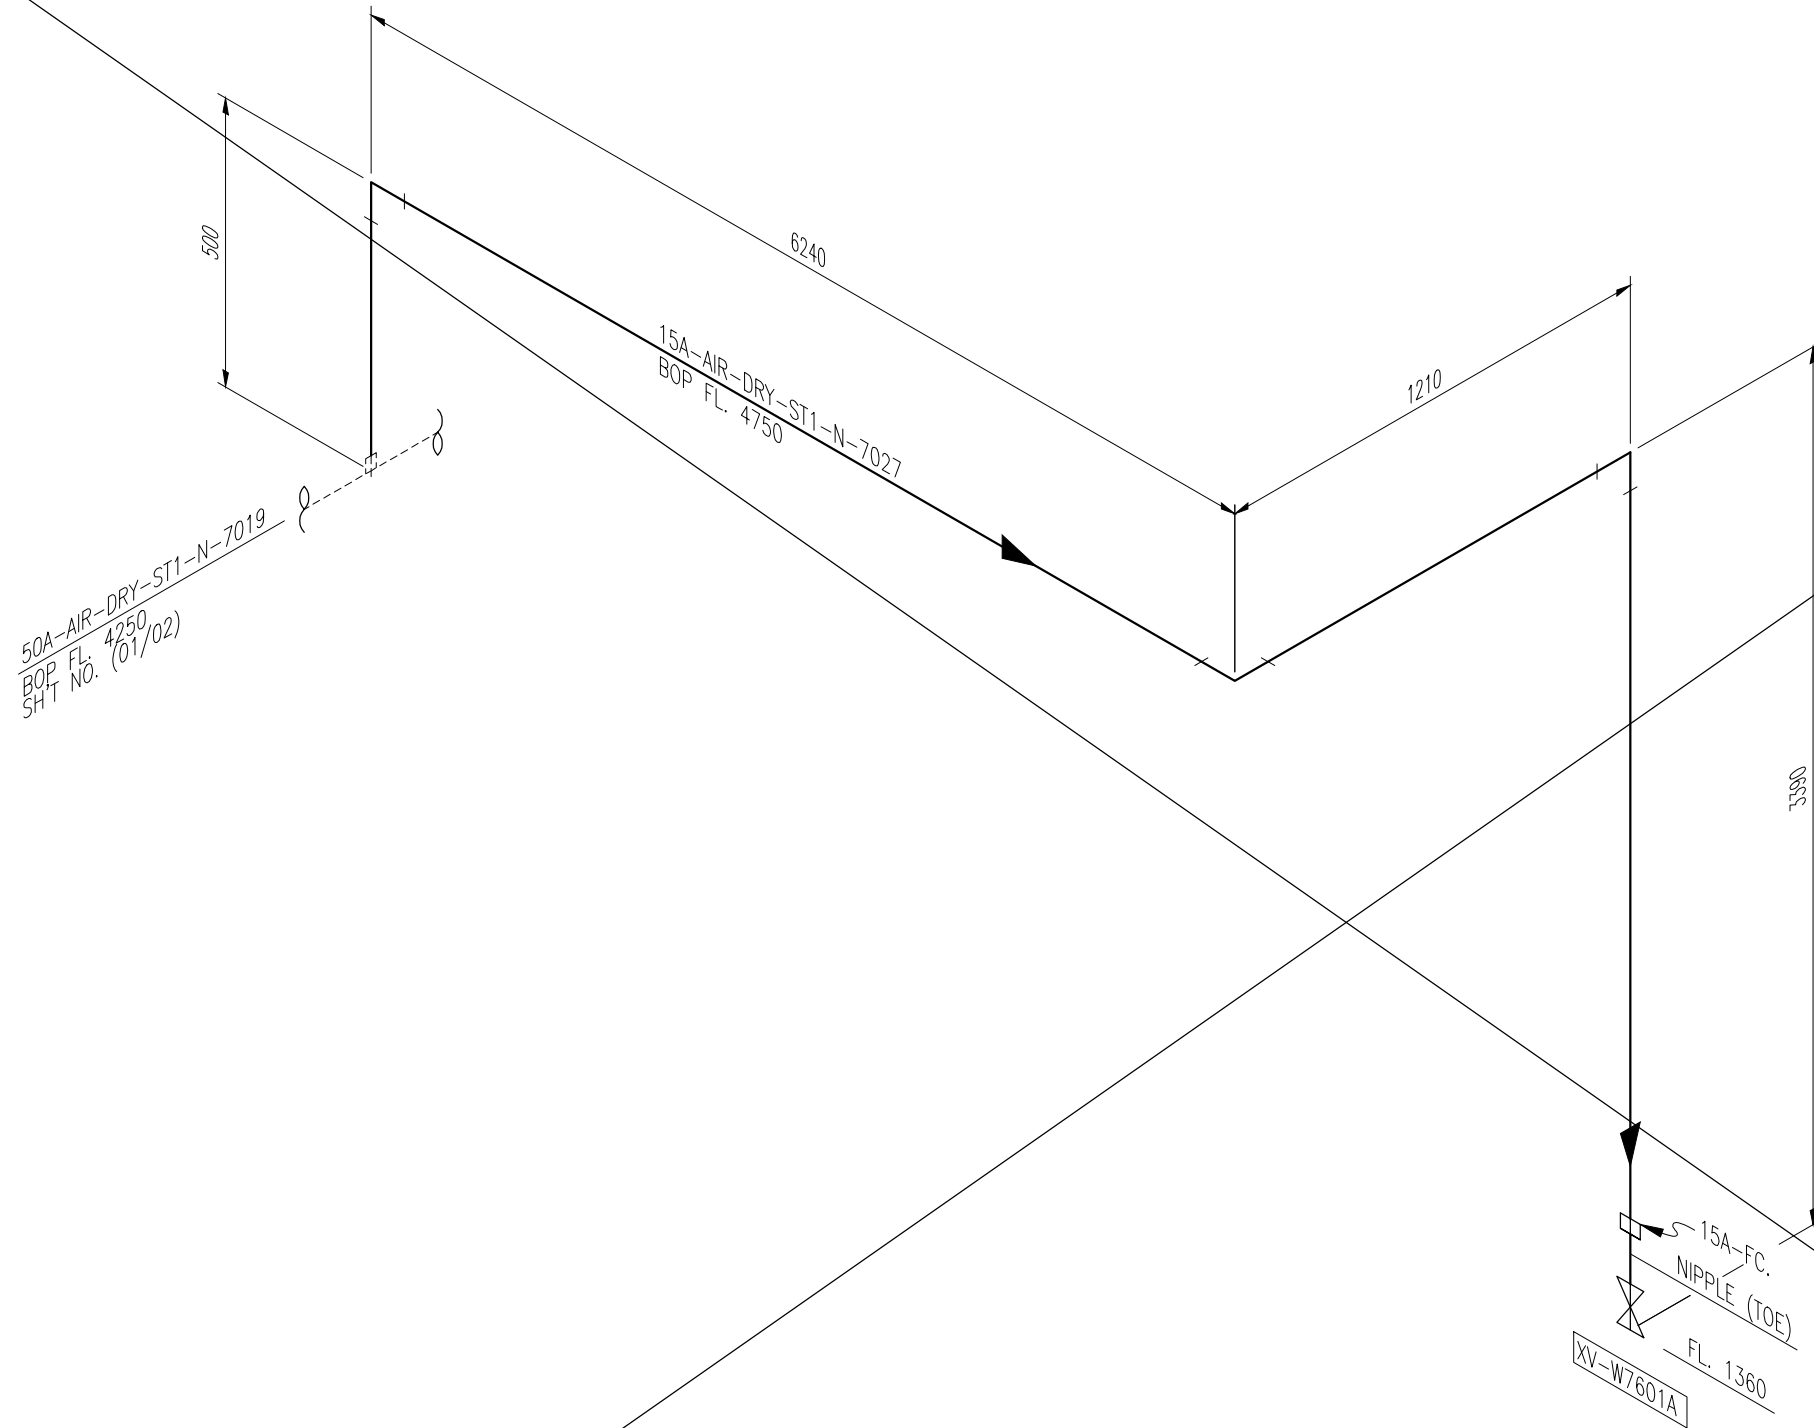

<NOTE>
1. (*) FIELD ADJUST



CONTRACTOR		PROJECT NAME	
		M15X Ph4 Project	
COMMODITY		JOB NO.	
AIR-DRY		22330D	
LINE NO.	SH'T NO.	REV.	
15A-AIR-DRY-ST1-N-7027	01 / 01	0	