


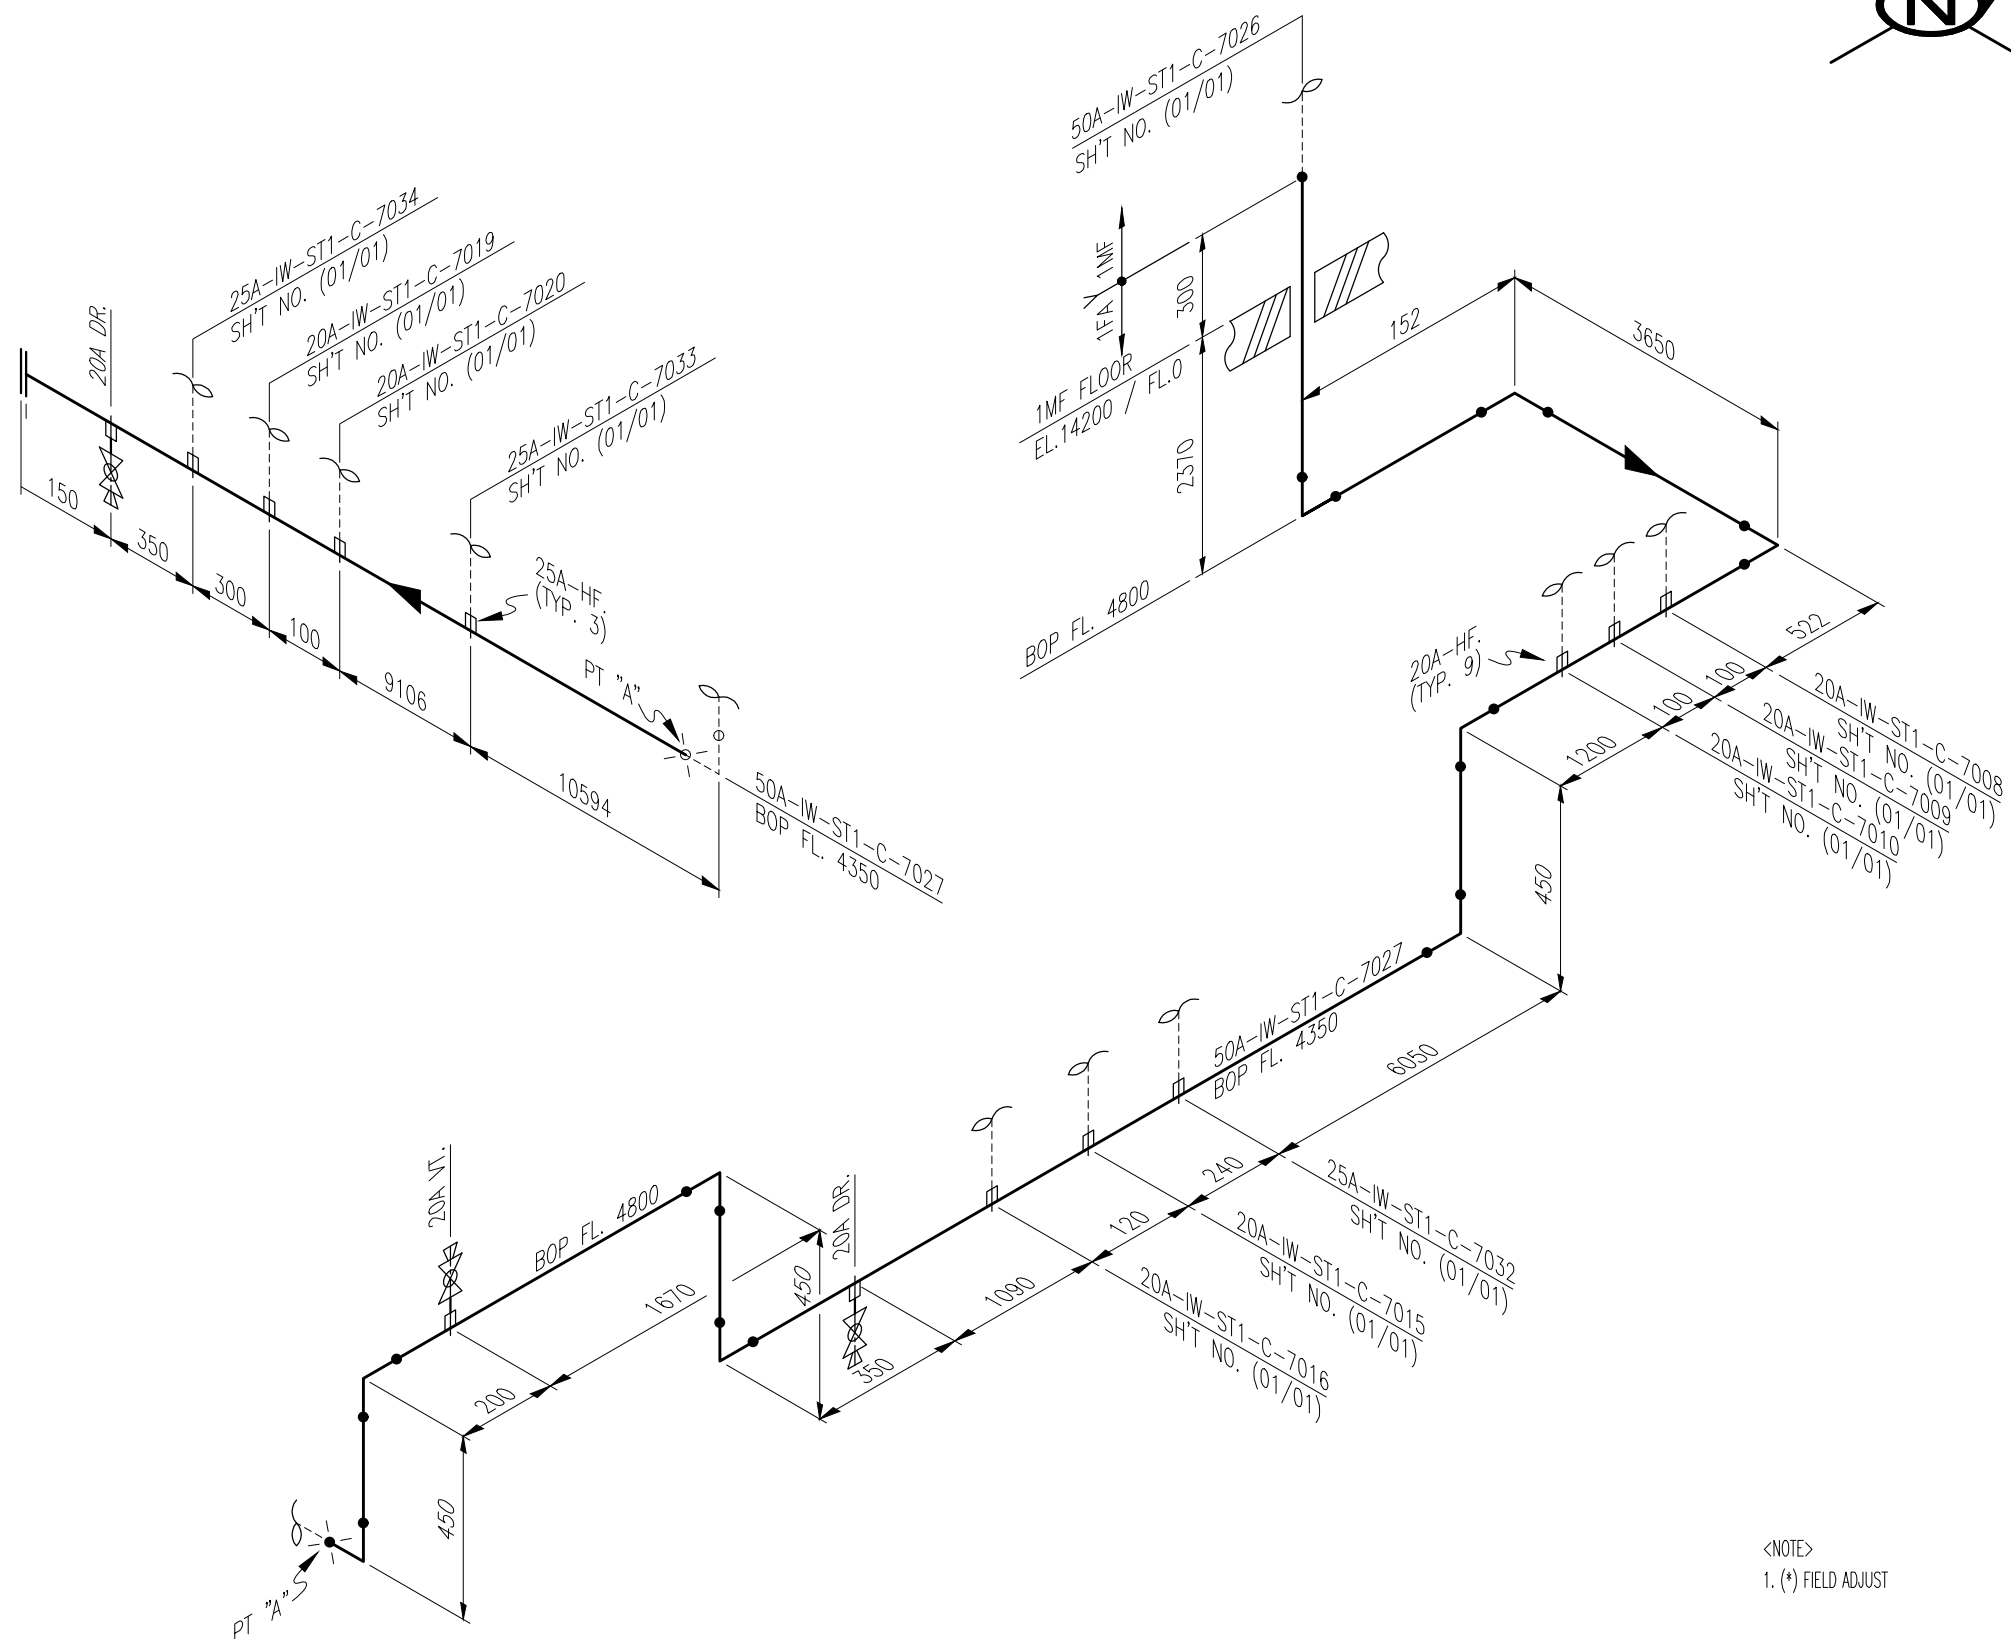

<NOTE>
1. (*) FIELD ADJUST

INSULATION	CODE	C	CONDITION	PRESS. (kg/cm2g)	TEMP. (°C)	AREA W14						CONTRACTOR 	PROJECT NAME	
	THICK.	—	DESIGN	10	60	UNIT 1FA							M15X Ph4 Project	
			OPERATING	7.5	AMB	REF. PLAN DWG. CJ-M15W14-PI-A30-010017-B		25.01.24	APPROVED FOR CONSTRUCTION	황래중	안남후	박동영	COMMODITY IW	JOB NO.
						REF. P & ID CJ-M15W13-PR-A20-000081							22330D	
						REV. NO.	DATE	DESCRIPTION	BY	CHK	APP'D	LINE NO. 50A-IW-ST1-C-7027	SH'T NO. 01 / 01	REV. 0

[illegible]

CONTRACTOR 		PROJECT NAME M15X Ph4 Project	
COMMODITY IW		JOB NO. 22330D	
LINE NO. 50A-IW-ST1-C-7027	SH'T NO. 01 / 01		REV. 0

경고 : 본 도면은 SK HYNIX의 기밀비밀 자료로서, 어떠한 경우에도 목적 외 사용, 복제, 제3자에게 공개, 누설 및 유출할 수 없으며, 회사는 유포자의 불법 사용으로 피해가 발생할 경우 유포자에게 민/형사상 책임을 요구할 수 있음.