


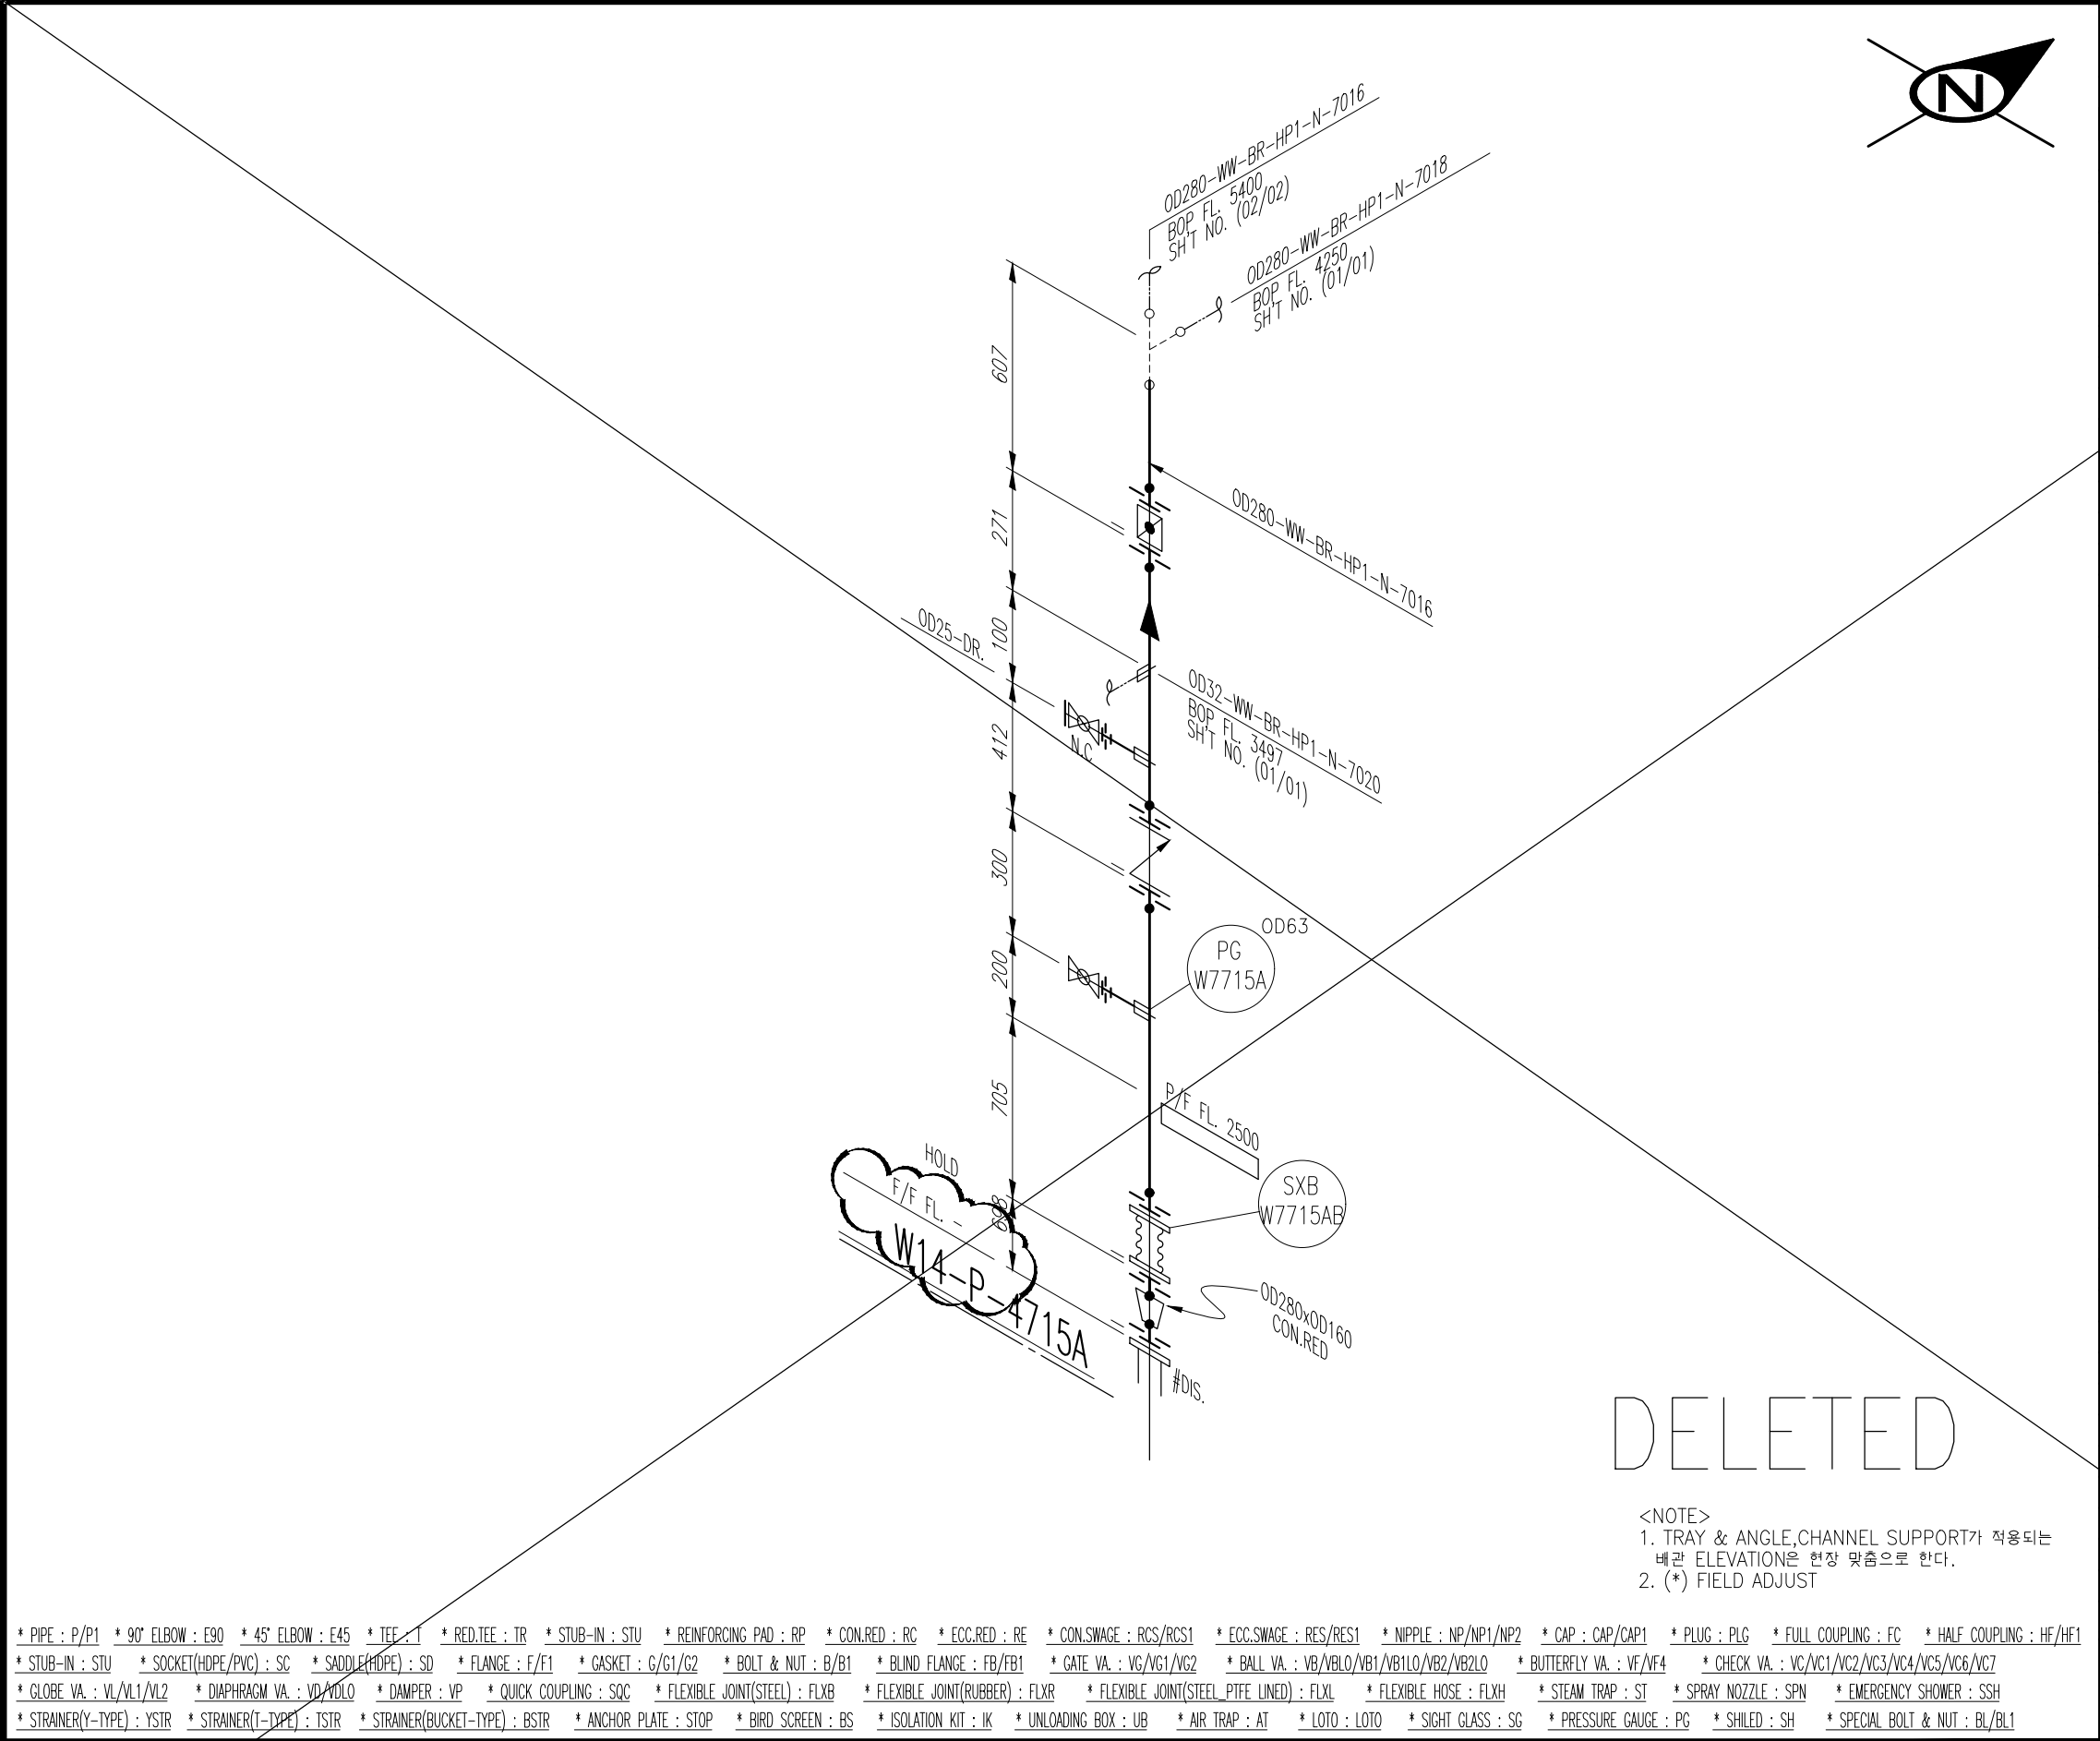

DELETED

<NOTE>
1. TRAY & ANGLE, CHANNEL SUPPORT가 적용되는
배관 ELEVATION은 현장 맞춤으로 한다.
2. (*) FIELD ADJUST

SK ecoplant			
ITEM	SIZE	Q'TY	DESCRIPTION
HP 1			
P	OD280	0.8M	PIPE, HDPE PE100, PE, BUTT FUSION, PN16/SDR11
P	OD63	0.1M	PIPE, HDPE PE100, PE, SOCKET FUSION, PN16/SDR11
P	OD25	0.1M	PIPE, HDPE PE100, PE, SOCKET FUSION, PN16/SDR11
RC	OD280xOD160	1EA	REDUCER CON, HDPE PE100, PE, BUTT FUSION, PN16/SDR11
SD	OD280xOD63	1EA	SADDLE, HDPE PE100, PE, BRANCH-SOCKET FUSION, PN16/SDR11
SD	OD280xOD32	1EA	SADDLE, HDPE PE100, PE, BRANCH-SOCKET FUSION, PN16/SDR11
SD	OD280xOD25	1EA	SADDLE, HDPE PE100, PE, BRANCH-SOCKET FUSION, PN16/SDR11
VB	OD63	1EA	BALL VALVE, KS 10K, FF FLG'D, BODY-PP / TRIM-PP / SEAT-PTFE, FB, LEVER
VB	OD25	1EA	BALL VALVE, KS 10K, FF FLG'D, BODY-PP / TRIM-PP / SEAT-PTFE, FB, LEVER
VC	OD280	1EA	CHECK VALVE, KS 10K, WAFER FF, BODY-PP / TRIM-PP, WAFER SWING
VF	OD280	1EA	BUTTERFLY VALVE, KS 10K, WAFER FF, BODY-PP / TRIM-PP / EPDM-LINED, GEAR
F	OD280	6EA	FLG LAP JOINT / STUB END SET, KS 10K, FF, LAP JOINT-ST304 / STUB END-HDPE PE100
F	OD160	1EA	FLG LAP JOINT / STUB END SET, KS 10K, FF, LAP JOINT-ST304 / STUB END-HDPE PE100
F	OD63	1EA	FLG LAP JOINT / STUB END SET, KS 10K, FF, LAP JOINT-ST304 / STUB END-HDPE PE100
F	OD25	1EA	FLG LAP JOINT / STUB END SET, KS 10K, FF, LAP JOINT-ST304 / STUB END-HDPE PE100
FB	OD25	1EA	FLG BLIND & LINER SET, KS 10K, FF, BLIND-ST304 / LINDER-HDPE PE100 (MIN 5.0MM TH'K)
G	OD280	6EA	GASKET, KS 10K, FF, PTFE+EPDM, 3.0MM TH'K
G	OD160	1EA	GASKET, KS 10K, FF, PTFE+EPDM, 3.0MM TH'K
G	OD63	1EA	GASKET, KS 10K, FF, PTFE+EPDM, 3.0MM TH'K
G	OD25	1EA	GASKET, KS 10K, FF, PTFE+EPDM, 3.0MM TH'K
G2	OD25	1EA	GASKET, KS 10K, FF, PTFE+EPDM, BLIND, 3.0MM TH'K
B	OD280	2SET	MACHINE BOLT & NUTS :STS 304 / W WASHERS
B	OD160	1SET	MACHINE BOLT & NUTS :STS 304 / W WASHERS
B	OD63	1SET	MACHINE BOLT & NUTS :STS 304 / W WASHERS
B	OD25	2SET	MACHINE BOLT & NUTS :STS 304 / W WASHERS
BL	OD280	2SET	MACHINE BOLT & NUTS :STS 304 / W WASHERS(SPECIAL)
FLXR	OD280	1EA	FLEXIBLE JOINT(TPC RUBBER TYPE)
PG	OD63	1EA	PRESSURE GAUGE, KS 10K, FF
LOTO	OD25	1EA	LOTO
CLIENT			
SK hynix			
CONTRACTOR		PROJECT NAME	
SK ecoplant		M15X Ph4 Project	
COMMODITY		JOB NO.	
WW-BR		22330D	
LINE NO.		SH'T NO. REV.	
OD280-WW-BR-HP1-N-7016		01 / 02 0	

INSULATION	CODE	N	CONDITION	PRESS. (kg/cm2g)	TEMP. (°C)	AREA	W14								
	THICK.	-	DESIGN	10	60	UNIT	R1FA								
			OPERATING	7.5	AMB	REF. PLAN DWG.									
						CJ-M15W14-PI-A30-010017-A									
						REF. P & ID									
						CJ-M15W14-PR-A20-000501									
								REV. NO.	25.01.24	APPROVED FOR CONSTRUCTION	황래중	안남후	박동영		
								DATE		DESCRIPTION	BY	CHK	APP'D		