


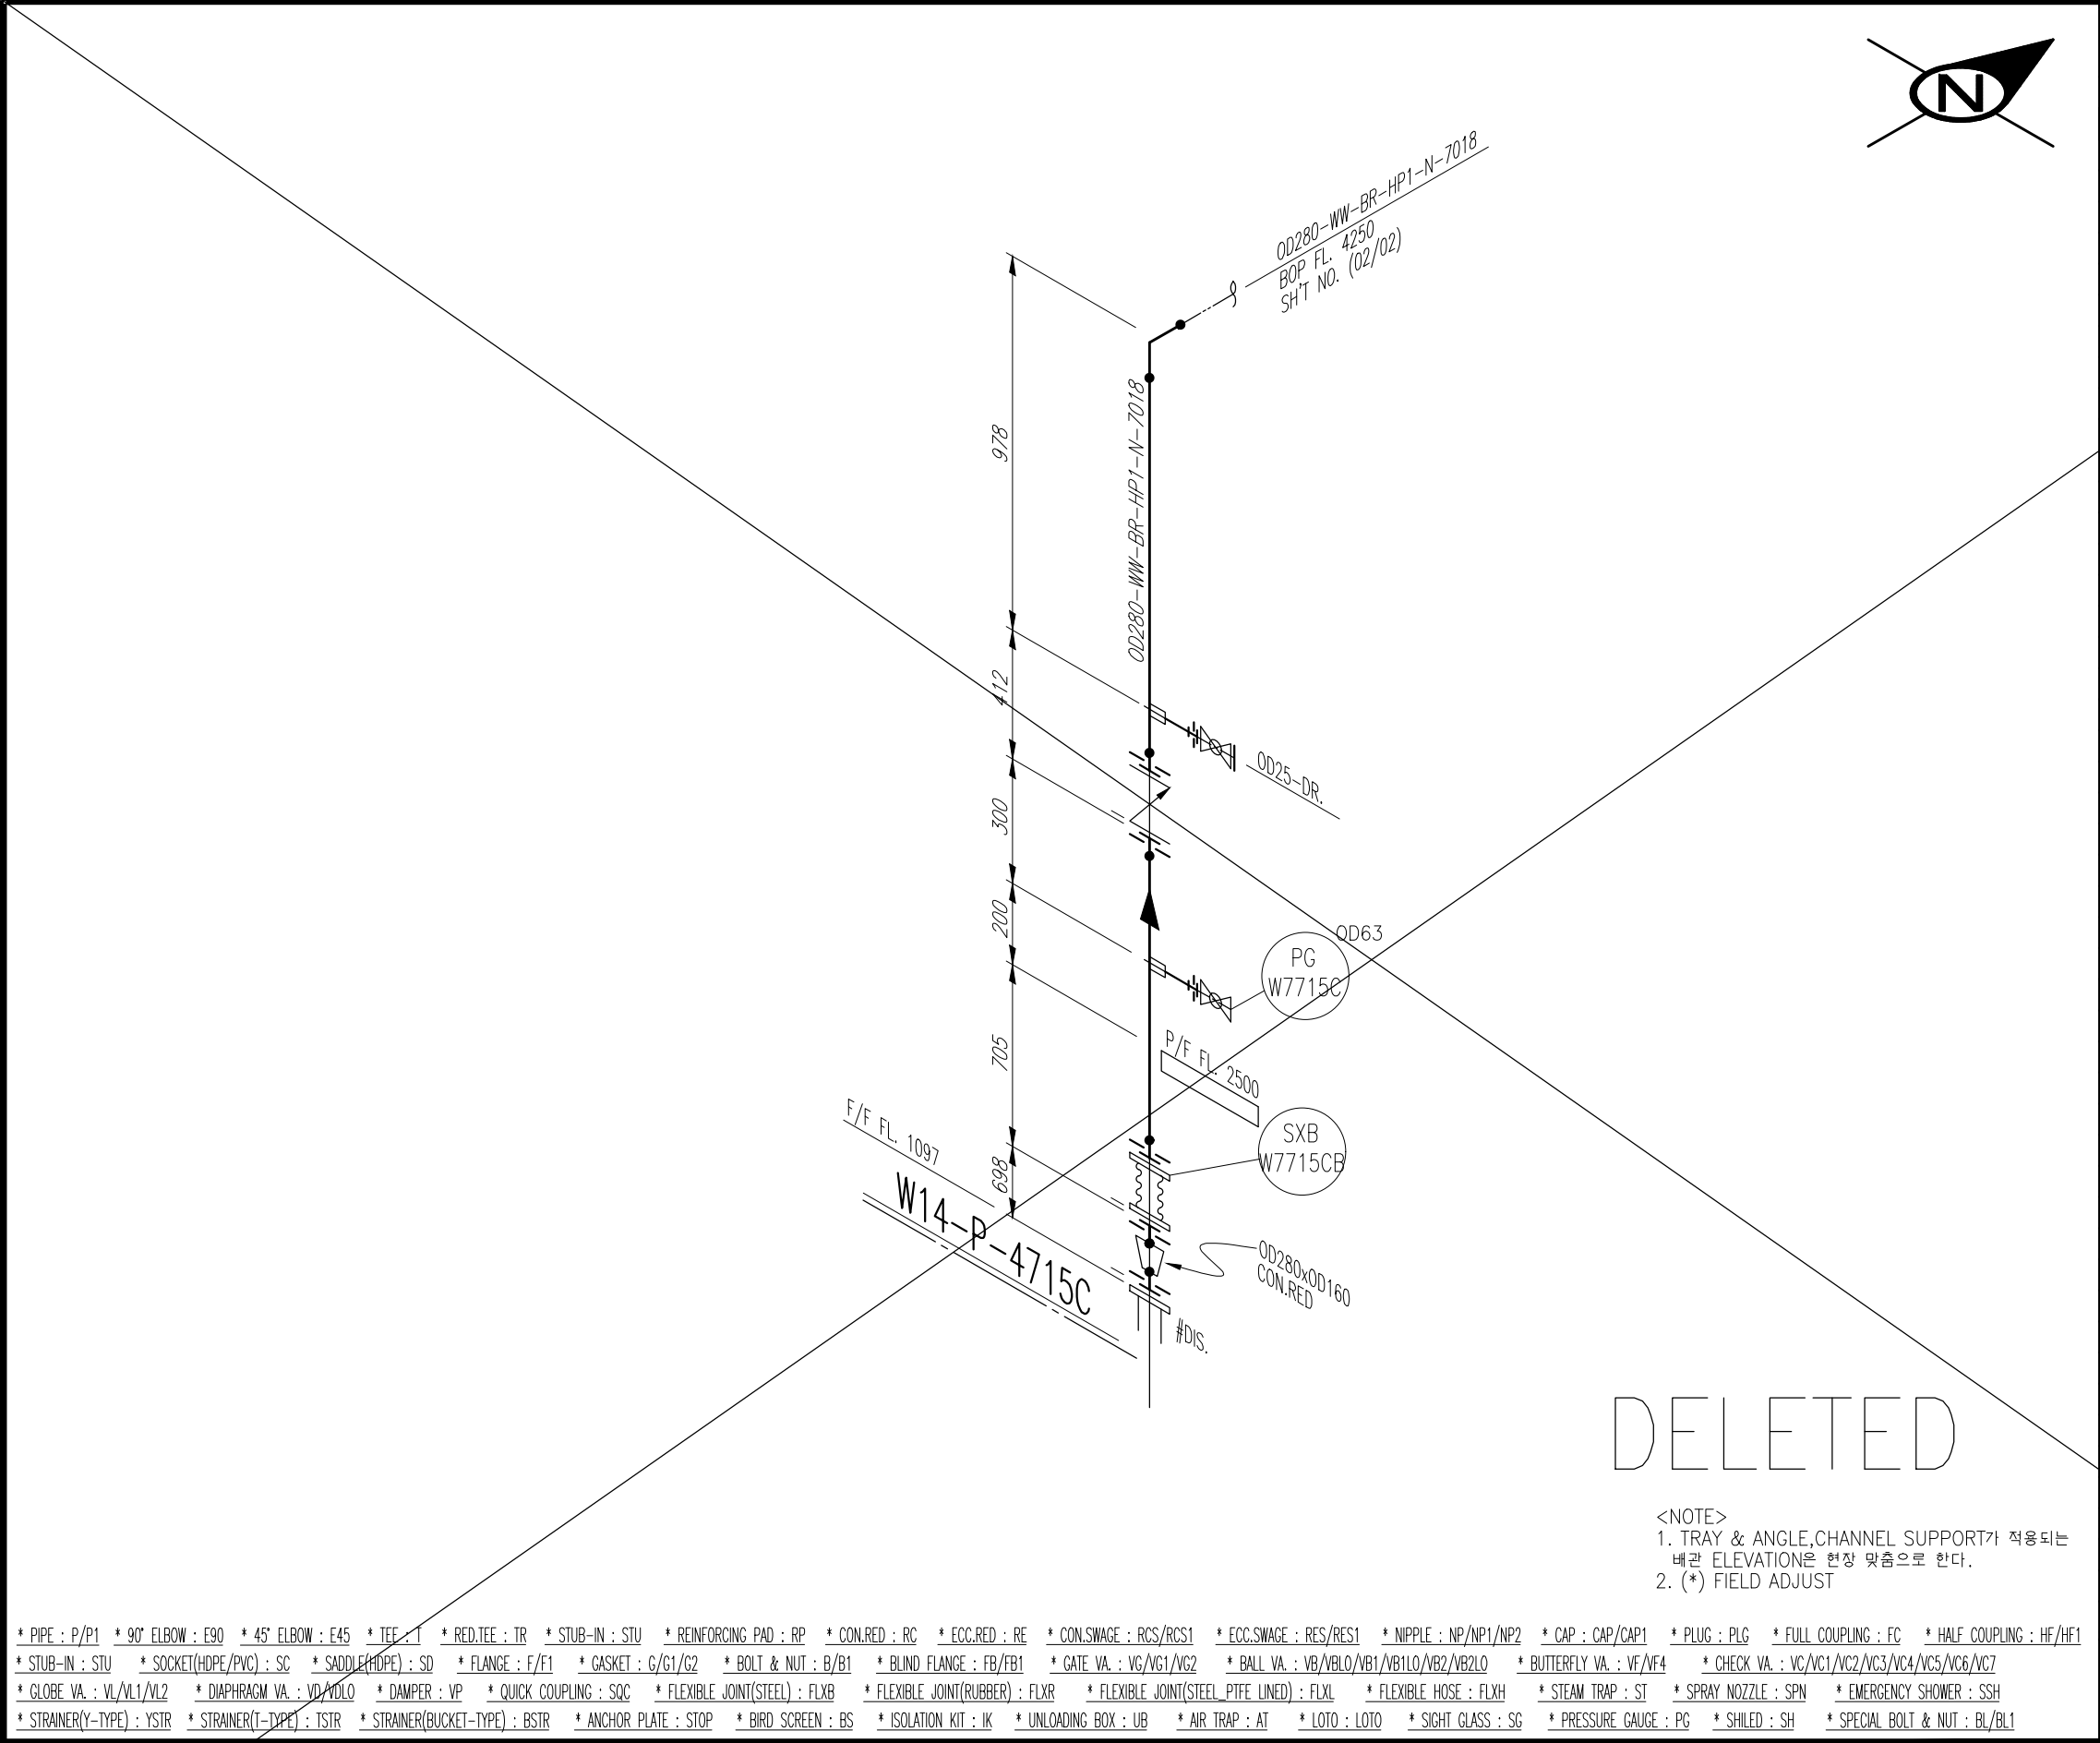

DELETED

<NOTE>
1. TRAY & ANGLE, CHANNEL SUPPORT가 적용되는
배관 ELEVATION은 현장 맞춤으로 한다.
2. (*) FIELD ADJUST

* PIPE : P/P1 * 90° ELBOW : E90 * 45° ELBOW : E45 * TEE : T * RED.TEE : TR * STUB-IN : STU * REINFORCING PAD : RP * CON.RED : RC * ECC.RED : RE * CON.SWAGE : RCS/RCS1 * ECC.SWAGE : RES/RES1 * NIPPLE : NP/NP1/NP2 * CAP : CAP/CAP1 * PLUG : PLG * FULL COUPLING : FC * HALF COUPLING : HF/HF1
* STUB-IN : STU * SOCKET(HDPE/PVC) : SC * SADDLE(HDPE) : SD * FLANGE : F/F1 * GASKET : G/G1/G2 * BOLT & NUT : B/B1 * BLIND FLANGE : FB/FB1 * GATE VA. : VG/VG1/VG2 * BALL VA. : VB/VBLO/VB1/VB1LO/VB2/VB2LO * BUTTERFLY VA. : VF/VF4 * CHECK VA. : VC/VC1/VC2/VC3/VC4/VC5/VC6/VC7
* GLOBE VA. : VL/VL1/VL2 * DIAPHRAGM VA. : VD/VDLO * DAMPER : VP * QUICK COUPLING : SQC * FLEXIBLE JOINT(STEEL) : FLXB * FLEXIBLE JOINT(RUBBER) : FLXR * FLEXIBLE JOINT(STEEL PTFE LINED) : FLXL * FLEXIBLE HOSE : FLXH * STEAM TRAP : ST * SPRAY NOZZLE : SPN * EMERGENCY SHOWER : SSH
* STRAINER(Y-TYPE) : YSTR * STRAINER(T-TYPE) : TSTR * STRAINER(BUCKET-TYPE) : BSTR * ANCHOR PLATE : STOP * BIRD SCREEN : BS * ISOLATION KIT : IK * UNLOADING BOX : UB * AIR TRAP : AT * LOTO : LOTO * SIGHT GLASS : SG * PRESSURE GAUGE : PG * SHILED : SH * SPECIAL BOLT & NUT : BL/BL1

INSULATION	CODE	N	CONDITION	PRESS. (kg/cm2g)	TEMP. (°C)	AREA	REV. NO.	DATE	DESCRIPTION	BY	CHK	APP'D	CONTRACTOR	PROJECT NAME
	THICK.		DESIGN	10	60	UNIT								
			OPERATING	7.5	AMB	REF. PLAN DWG.							COMMODITY	JOB NO.
						CJ-M15W14-PI-A30-010017-A								
						REF. P & ID							LINE NO.	SH'T NO.
						CJ-M15W14-PR-A20-000501								

SK ecoplant			
ITEM	SIZE	Q'TY	DESCRIPTION
HP1			
P	OD280	0.8M	PIPE, HDPE PE100, PE, BUTT FUSION, PN16/SDR11
P	OD63	0.1M	PIPE, HDPE PE100, PE, SOCKET FUSION, PN16/SDR11
P	OD25	0.1M	PIPE, HDPE PE100, PE, SOCKET FUSION, PN16/SDR11
E90	OD280	1EA	ELBOW 90 DEG, HDPE PE100, PE, BUTT FUSION, PN16/SDR11
RC	OD280xOD160	1EA	REDUCER CON, HDPE PE100, PE, BUTT FUSION, PN16/SDR11
SD	OD280xOD63	1EA	SADDLE, HDPE PE100, PE, BRANCH-SOCKET FUSION, PN16/SDR11
SD	OD280xOD25	1EA	SADDLE, HDPE PE100, PE, BRANCH-SOCKET FUSION, PN16/SDR11
VB	OD63	1EA	BALL VALVE, KS 10K, FF FLG'D, BODY-PP / TRIM-PP / SEAT-PTFE, FB, LEVER
VB	OD25	1EA	BALL VALVE, KS 10K, FF FLG'D, BODY-PP / TRIM-PP / SEAT-PTFE, FB, LEVER
VC	OD280	1EA	CHECK VALVE, KS 10K, WAFER FF, BODY-PP / TRIM-PP, WAFER SWING
F	OD280	4EA	FLG LAP JOINT / STUB END SET, KS 10K, FF, LAP JOINT-ST304 / STUB END-HDPE PE100
F	OD160	1EA	FLG LAP JOINT / STUB END SET, KS 10K, FF, LAP JOINT-ST304 / STUB END-HDPE PE100
F	OD63	1EA	FLG LAP JOINT / STUB END SET, KS 10K, FF, LAP JOINT-ST304 / STUB END-HDPE PE100
F	OD25	1EA	FLG LAP JOINT / STUB END SET, KS 10K, FF, LAP JOINT-ST304 / STUB END-HDPE PE100
FB	OD25	1EA	FLG BLIND & LINER SET, KS 10K, FF, BLIND-ST304 / LINDER-HDPE PE100 (MIN 5.0MM TH'K)
G	OD280	6EA	GASKET, KS 10K, FF, PTFE+EPDM, 3.0MM TH'K
G	OD160	1EA	GASKET, KS 10K, FF, PTFE+EPDM, 3.0MM TH'K
G	OD63	1EA	GASKET, KS 10K, FF, PTFE+EPDM, 3.0MM TH'K
G	OD25	1EA	GASKET, KS 10K, FF, PTFE+EPDM, 3.0MM TH'K
G2	OD25	1EA	GASKET, KS 10K, FF, PTFE+EPDM, BLIND, 3.0MM TH'K
B	OD280	2SET	MACHINE BOLT & NUTS :ST3 304 / W WASHERS
B	OD160	1SET	MACHINE BOLT & NUTS :ST3 304 / W WASHERS
B	OD63	1SET	MACHINE BOLT & NUTS :ST3 304 / W WASHERS
B	OD25	2SET	MACHINE BOLT & NUTS :ST3 304 / W WASHERS
BL	OD280	1SET	MACHINE BOLT & NUTS :ST3 304 / W WASHERS(SPECIAL)
FLXR	OD280	1EA	FLEXIBLE JOINT(TPC RUBBER TYPE)
PG	OD63	1EA	PRESSURE GAUGE, KS 10K, FF
CLIENT			
SK hynix			
CONTRACTOR			
SK ecoplant			
COMMODITY			
WW-BR			
PROJECT NAME			
M15X Ph4 Project			
JOB NO.			
22330D			
LINE NO.			
OD280-WW-BR-HP1-N-7018			
SH'T NO.			
01 / 02			
REV.			
0			