


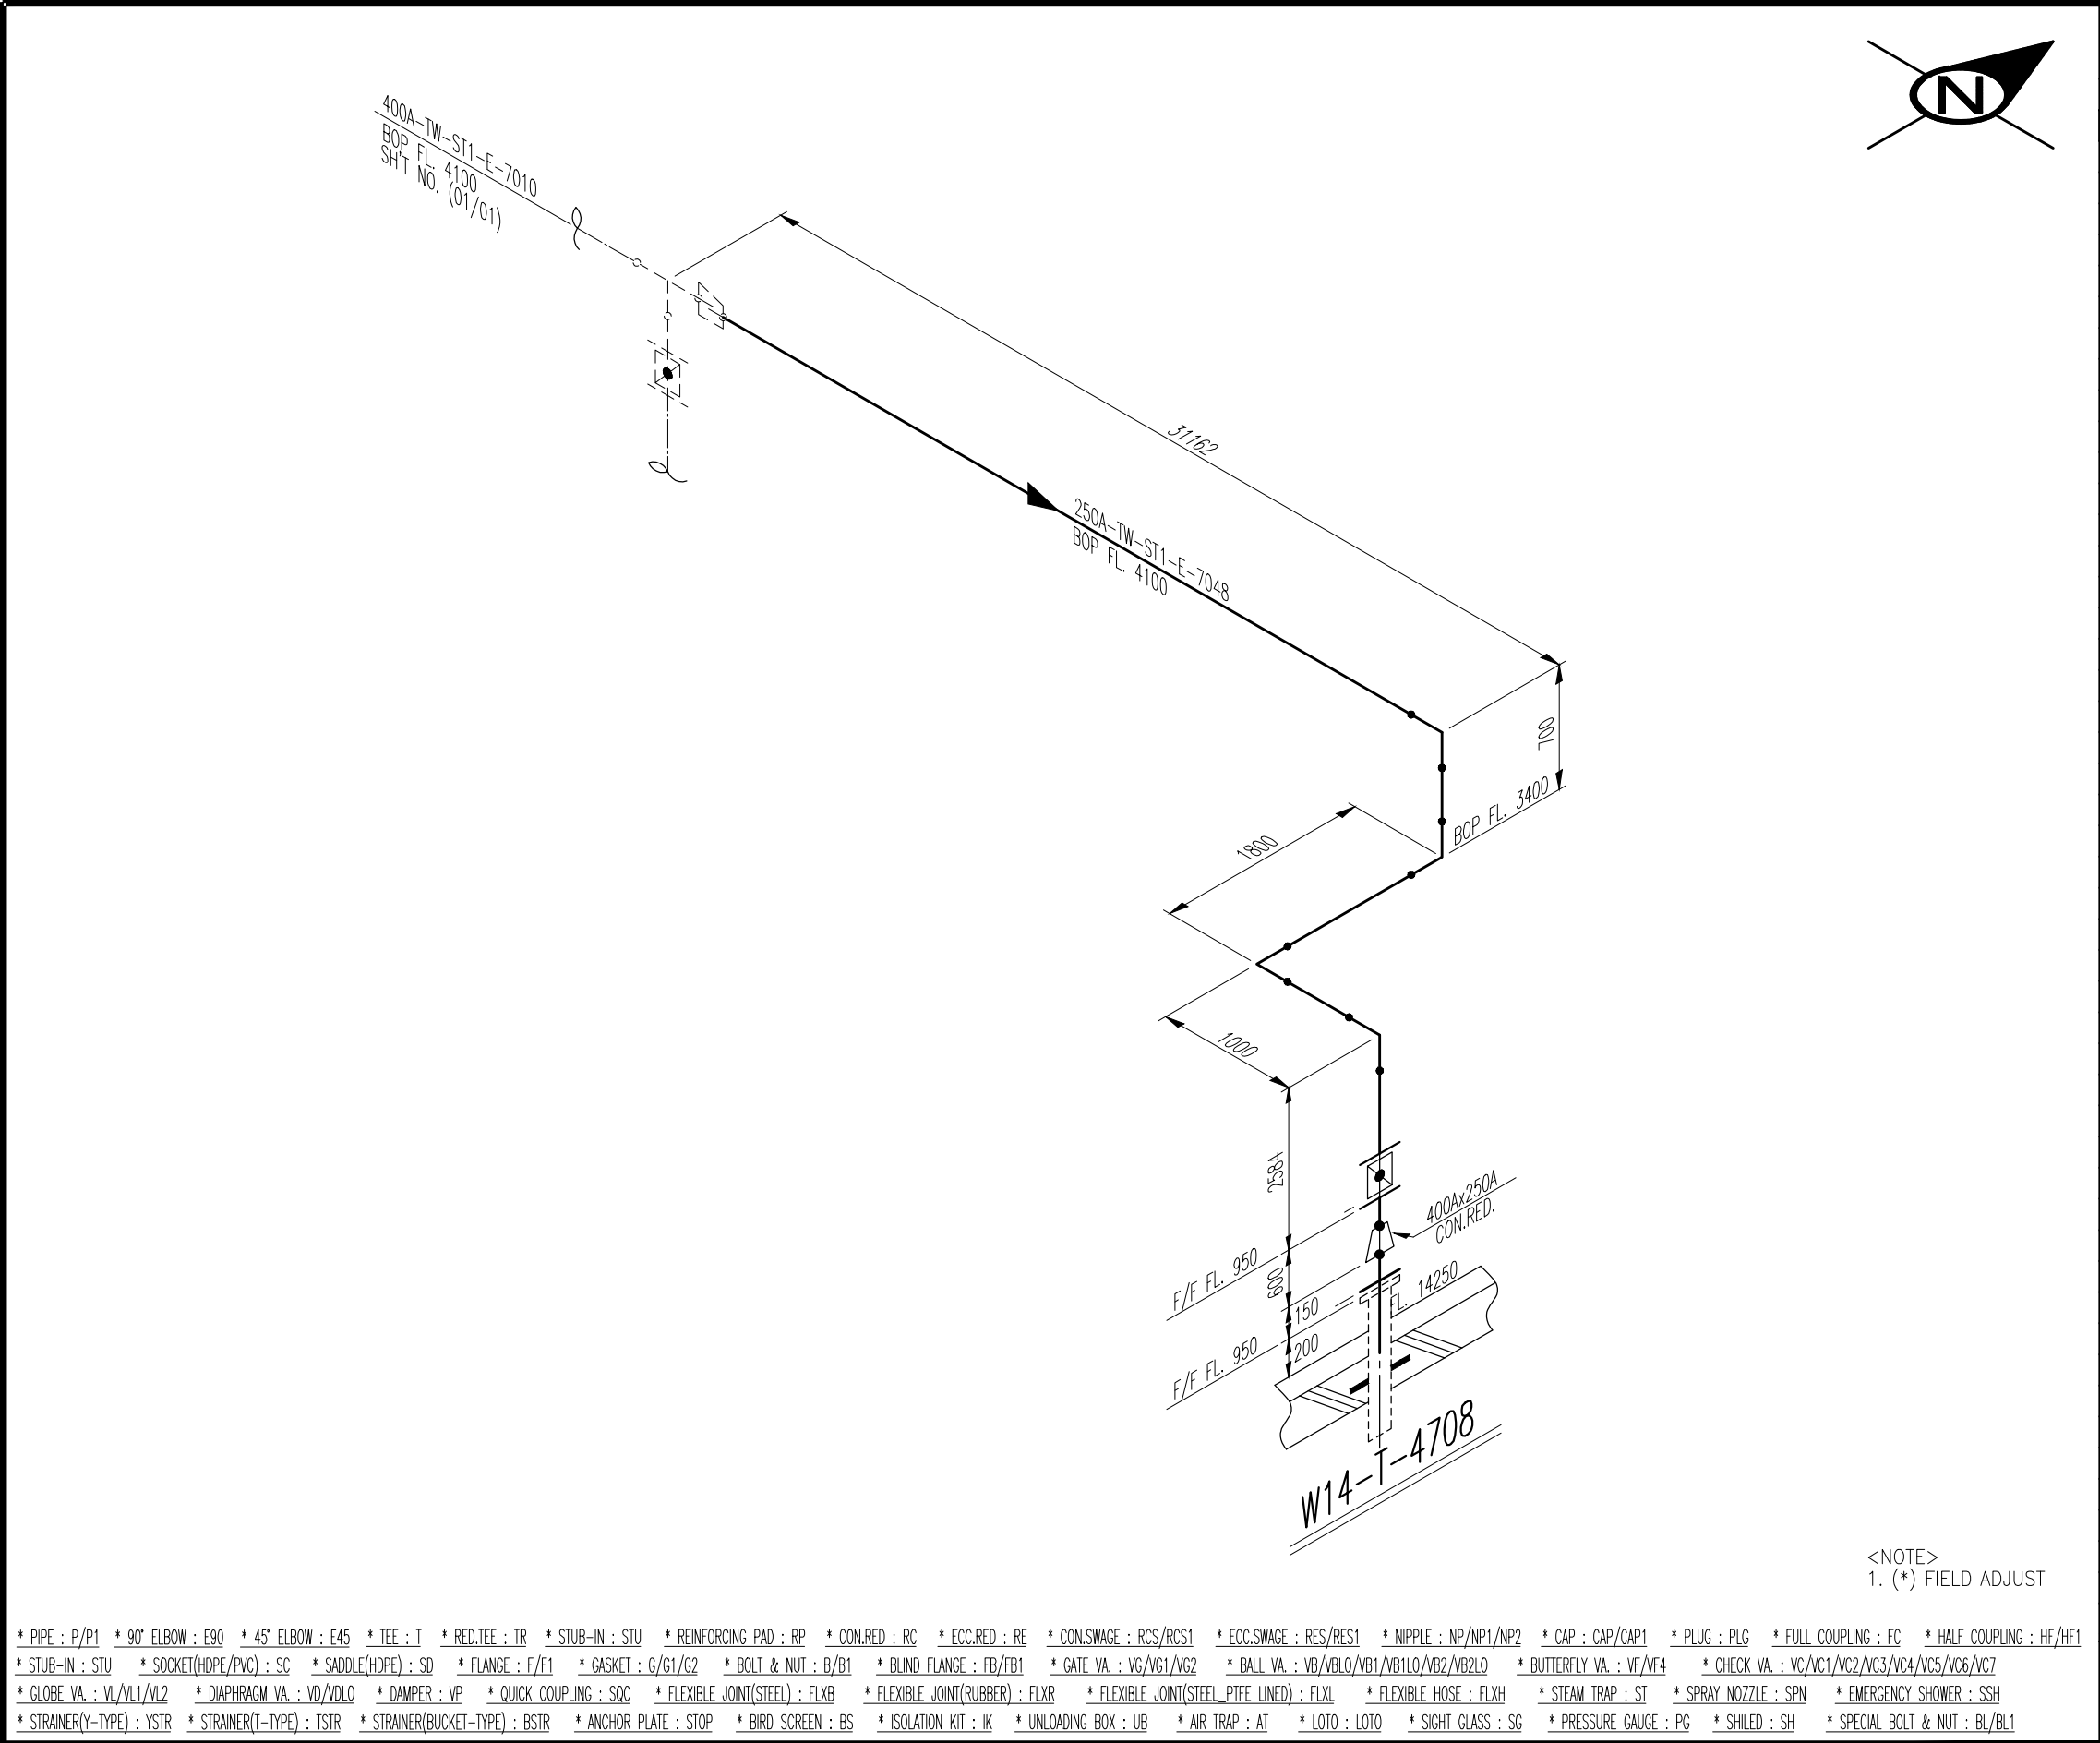

\* PIPE : P/P1 \* 90° ELBOW : E90 \* 45° ELBOW : E45 \* TEE : T \* RED.TEE : TR \* STUB-IN : STU \* REINFORCING PAD : RP \* CON.RED : RC \* ECC.RED : RE \* CON.SWAGE : RCS/RCS1 \* ECC.SWAGE : RES/RES1 \* NIPPLE : NP/NP1/NP2 \* CAP : CAP/CAP1 \* PLUG : PLG \* FULL COUPLING : FC \* HALF COUPLING : HF/HF1  
\* STUB-IN : STU \* SOCKET(HDPE/PVC) : SC \* SADDLE(HDPE) : SD \* FLANGE : F/F1 \* GASKET : G/G1/G2 \* BOLT & NUT : B/B1 \* BLIND FLANGE : FB/FB1 \* GATE VA. : VG/VG1/VG2 \* BALL VA. : VB/VBLO/VB1/VB1LO/VB2/VB2LO \* BUTTERFLY VA. : VF/VF4 \* CHECK VA. : VC/VC1/VC2/VC3/VC4/VC5/VC6/VC7  
\* GLOBE VA. : VL/VL1/VL2 \* DIAPHRAGM VA. : VD/VDLO \* DAMPER : VP \* QUICK COUPLING : SQC \* FLEXIBLE JOINT(STEEL) : FLXB \* FLEXIBLE JOINT(RUBBER) : FLXR \* FLEXIBLE JOINT(STEEL PTFE LINED) : FLXL \* FLEXIBLE HOSE : FLXH \* STEAM TRAP : ST \* SPRAY NOZZLE : SPN \* EMERGENCY SHOWER : SSH  
\* STRAINER(Y-TYPE) : YSTR \* STRAINER(T-TYPE) : TSTR \* STRAINER(BUCKET-TYPE) : BSTR \* ANCHOR PLATE : STOP \* BIRD SCREEN : BS \* ISOLATION KIT : IK \* UNLOADING BOX : UB \* AIR TRAP : AT \* LOTO : LOTO \* SIGHT GLASS : SG \* PRESSURE GAUGE : PG \* SHILED : SH \* SPECIAL BOLT & NUT : BL/BL1

|            |        |   |           |                     |               |                                               |                                                                                       |          |                           |     |     |       |                                                                                       |                     |           |
|------------|--------|---|-----------|---------------------|---------------|-----------------------------------------------|---------------------------------------------------------------------------------------|----------|---------------------------|-----|-----|-------|---------------------------------------------------------------------------------------|---------------------|-----------|
| INSULATION | CODE   | N | CONDITION | PRESS.<br>(kg/cm2g) | TEMP.<br>(°C) | AREA W14                                      |                                                                                       |          |                           |     |     |       | CONTRACTOR                                                                            | PROJECT NAME        |           |
|            | THICK. | — | DESIGN    | 6.4                 | 60            | UNIT R2FA                                     |                                                                                       |          |                           |     |     |       |  | M15X Ph4 Project    |           |
|            |        |   | OPERATING | 4                   | AMB           | REF. PLAN DWG.<br>CJ-M15W14-PI-A30-020014-C   |                                                                                       |          |                           |     |     |       | COMMODITY TW                                                                          | JOB NO.<br>22330D   |           |
|            |        |   |           |                     |               | REF. P & ID<br>CJ-M15W14-PR-A20-000304,000313 |  | 25.03.31 | APPROVED FOR CONSTRUCTION | 황래중 | 안남후 | 박동영   | LINE NO.<br>250A-TW-ST1-E-7048                                                        | SH'T NO.<br>01 / 01 | REV.<br>0 |
|            |        |   |           |                     |               |                                               | REV. NO.                                                                              | DATE     | DESCRIPTION               | BY  | CHK | APP'D |                                                                                       |                     |           |

경고 : 본 도면은 SK HYNIX의 기밀비밀 자료로서, 어떠한 경우에도 목적 외 사용, 복제, 제3자에게 공개, 누설 및 유출할 수 없으며, 회사는 유포자의 불법 사용으로 피해가 발생할 경우 유포자에게 민/형사상 책임을 요구할 수 있음.