


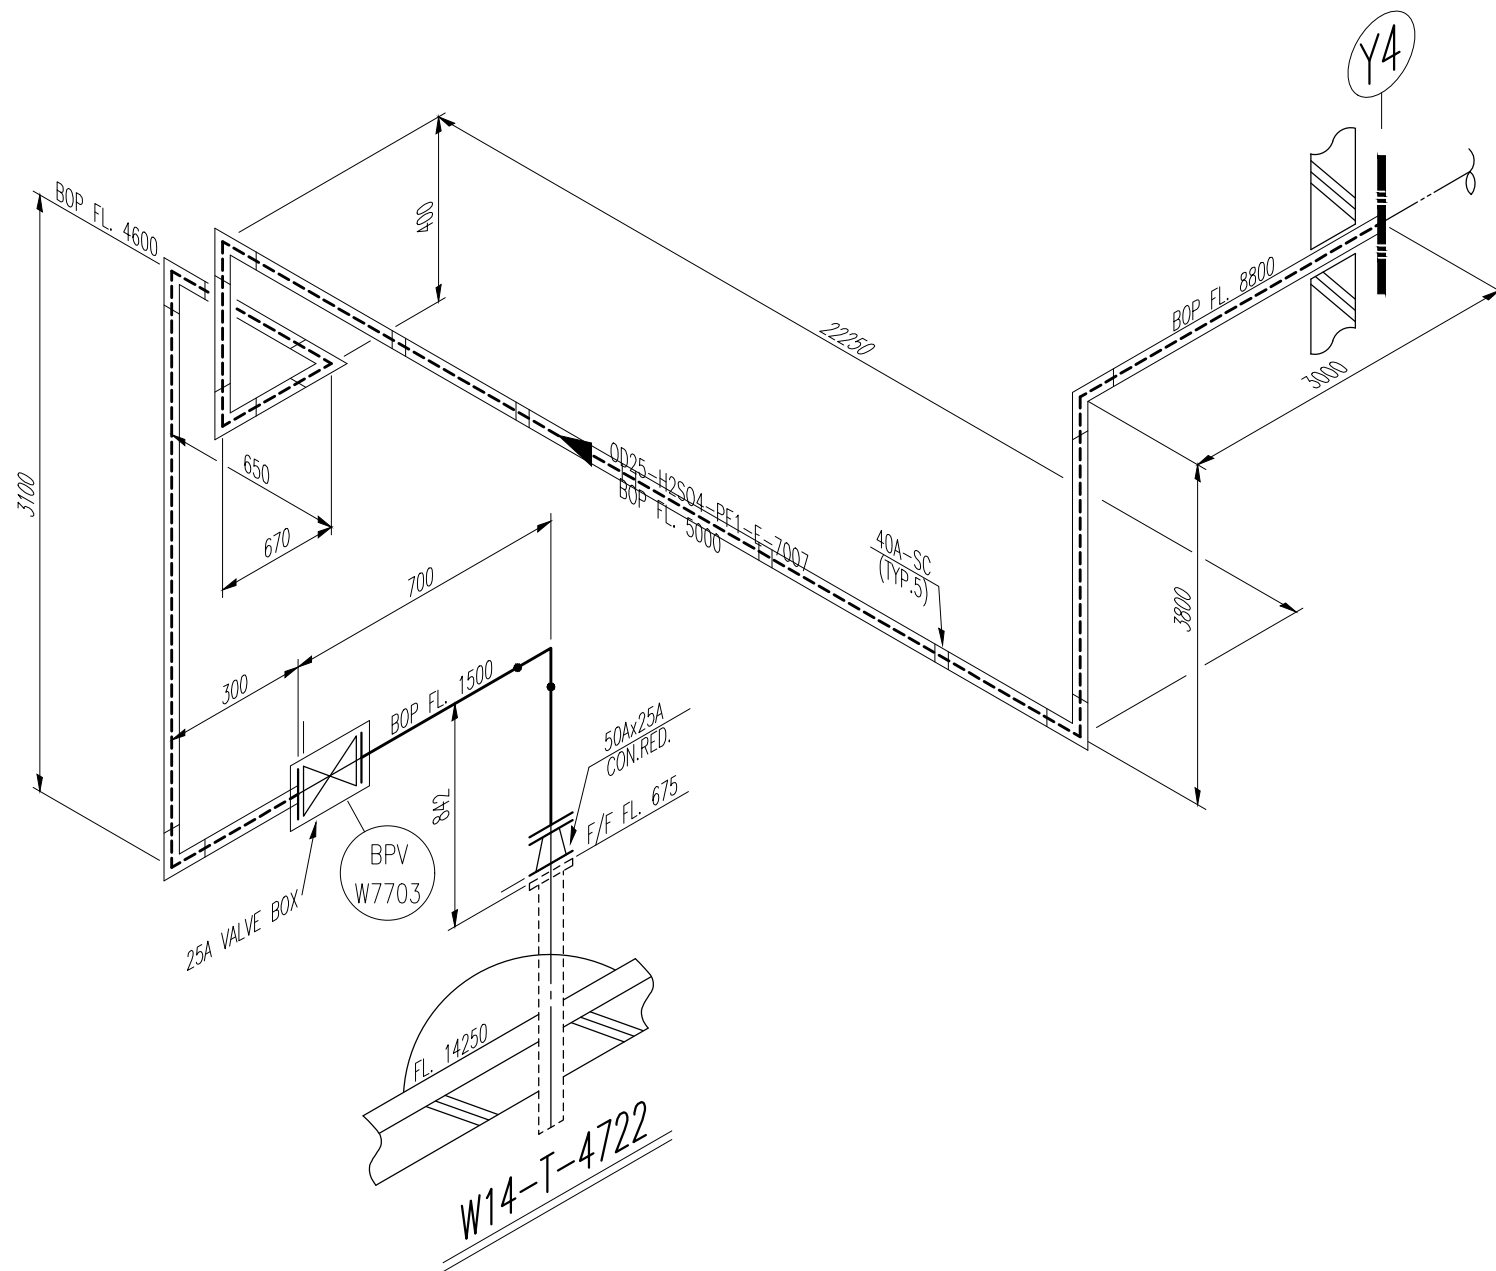

1. TRAY & ANGLE, CHANNEL SUPPORT가 적용되는 배관 ELEVATION은 현장 맞춤으로 한다.
2. H2SO4 배관의 입상/횡관에는 비산/낙수 방지를 위한 투명 PVC 보호판(5T)을 설치하고 누출방지를 위해 Silicon 마감처리를 한다.
3. (*) FIELD ADJUST

ST4

△				
	INC	40A	34.2M	관 보존재 (구무발포) + 일루미늄 CASING
	INC	25A	1.5M	관 보존재 (구무발포) + 일루미늄 CASING



경고 : 본 도면은 SK HYNIX의 기밀비밀 자료로서, 어떠한 경우에도 목적 외 사용, 복제, 제3자에게 공개, 누설 및 유출할 수 없으며, 회사는 유포자의 불법 사용으로 피해가 발생할 경우 유포자에게 민/형사상 책임을 요구할 수 있음.