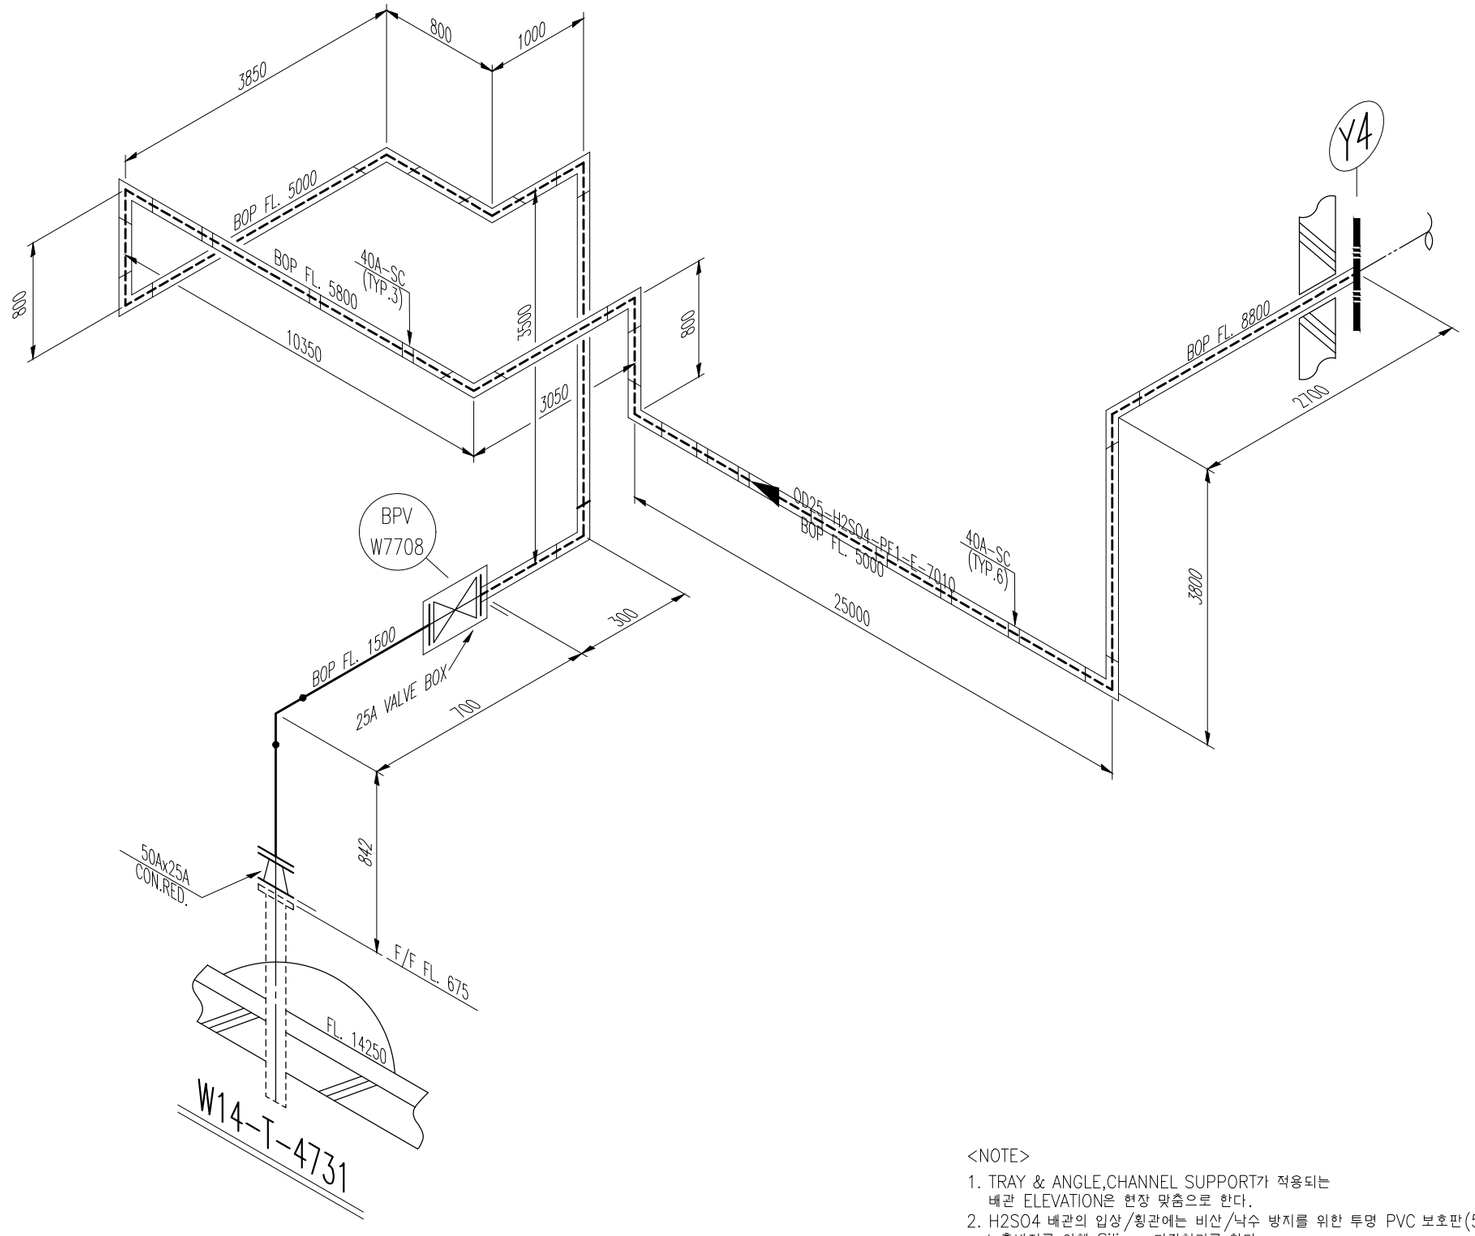

<NOTE>
1. TRAY & ANGLE,CHANNEL SUPPORT가 적용되는
   배관 ELEVATION은 현장 맞춤으로 한다.
2. H2SO4 배관의 입상/횡관에는 비산/낙수 방지를 위한 투명 PVC 보호판(5T)을 설치하고
   누출방지를 위해 Silicon 마감처리를 한다.
3. (*) FIELD ADJUST

ITEM	SIZE	Q'TY	DESCRIPTION
		PF1	
P	OD25	56.0M	PIPE, PFA TUBE, PE, FERRULE, 1.57MM TH'K
P3	40A	56.0M	PIPE, CLEAR PVC, PE, SOCKET BONDING, 4.0MM TH'K
E90A	40A	11EA	ELBOW 90 DEG, CLEAR PVC, PE, SOCKET BONDING, 4.0MM TH'K
SC	40A	9EA	SOCKET, CLEAR PVC, PE, SOCKET BONDING, 4.0MM TH'K
F1	OD25	1EA	FLG, PFA STUB END, BACK RING(PTFE), LAP JOINT(STS 304)
G1	OD25	1EA	GASKET, KS 10K, RF, PTFE+EPDM, 3.0MM TH'K
B1	OD25	1EA	HEX MACHINE BOLT & NYLON NUT :SM45C+HOT DIP GAL'V/W WASHERS
		ST4	
P	25A	1.5M	PIPE, STS 304TP+PTFE Lined, ERW – SCH 10S
E90	25A	1EA	ELBOW 90 DEG, STSF304+PTFE Lined, ERW – SCH 10S
RC	50Ax25A	1EA	REDUCER CON, STS304+PTFE Lined, ERW – SCH 10S
G	25A	1EA	GASKET, KS 10K, RF, PTFE, 3.0MM TH'K
G	50A	1EA	GASKET, KS 10K, RF, PTFE, 3.0MM TH'K
B1	25A	1SET	MACHINE BOLT & NYLON NUTS :STS 304 / W WASHERS
B1	50A	1SET	MACHINE BOLT & NYLON NUTS :STS 304 / W WASHERS
SH	25A	1EA	SHIELD
SH	50A	1EA	SHIELD
BPV	25A	1EA	BACK PRESSURE VALVE
SH1	25A	1EA	CLEAR PVC VALVE BOX
INC	40A	56.0M	관 보온재(고무발포) + 알루미늄 CASING
INC	25A	1.5M	관 보온재(고무발포) + 알루미늄 CASING

* PIPE : P/P1 * 90° ELBOW : E90 * 45° ELBOW : E45 * TEE : T * RED.TEE : TR * STUB-IN : STU * REINFORCING PAD : RP * CON.RED : RC * ECC.RED : RE * CON.SWAGE : RCS/RCS1 * ECC.SWAGE : RES/RES1 * NIPPLE : NP/NP1/NP2 * CAP : CAP/CAP1 * PLUG : PLG * FULL COUPLING : FC * HALF COUPLING : HF/HF1
* STUB-IN : STU * SOCKET(HDPE/PVC) : SC * SADDLE(HDPE) : SD * FLANGE : F/F1 * GASKET : G/G1/G2 * BOLT & NUT : B/B1 * BLIND FLANGE : FB/FB1 * GATE VA. : VG/VG1/VG2 * BALL VA. : VB/VBLO/VB1/VB1LO/VB2/VB2LO * BUTTERFLY VA. : VF/VF4 * CHECK VA. : VC/VC1/VC2/VC3/VC4/VC5/VC6/VC7
* GLOBE VA. : VL/VL1/VL2 * DIAPHRAGM VA. : VD/VDLO * DAMPER : VP * QUICK COUPLING : SQC * FLEXIBLE JOINT(STEEL) : FLXB * FLEXIBLE JOINT(RUBBER) : FLXR * FLEXIBLE JOINT(STEEL_PTFE LINED) : FLXL * FLEXIBLE HOSE : FLXH * STEAM TRAP : ST * SPRAY NOZZLE : SPN * EMERGENCY SHOWER : SSH
* STRAINER(Y-TYPE) : YSTR * STRAINER(T-TYPE) : TSTR * STRAINER(BUCKET-TYPE) : BSTR * ANCHOR PLATE : STOP * BIRD SCREEN : BS * ISOLATION KIT : IK * UNLOADING BOX : UB * AIR TRAP : AT * LOTO : LOTO * SIGHT GLASS : SG * PRESSURE GAUCE : PG * SHILED : SH * SPECIAL BOLT & NUT : BL/BL1

INSULATION	CODE	N
	THICK.	–

CONDITION	PRESS. (kg/cm2g)	TEMP. (°C)
DESIGN	6.4	60
OPERATING	4	AMB

AREA W14
UNIT R2FA
REF. PLAN DWG. CJ-M15W14-PI-A30-020016-C
REF. P & ID CJ-M15W14-PR-A20-000505

REV. NO.	DATE	DESCRIPTION	BY	CHK	APP'D
1	25.03.31	REVISED AS MARKED	황래중	안남후	박동영
0	25.01.24	APPROVED FOR CONSTRUCTION	황래중	안남후	박동영

CLIENT SK hynix

CONTRACTOR SK ecoplant

PROJECT NAME M15X Ph4 Project

COMMODITY H2SO4

JOB NO. 22330D

LINE NO. 0D25-H2SO4-PF1-E-7010

SH'T NO. 01 / 01

REV. 1

경고 : 본 도면은 SK HYNIX의 기업비밀 자료로서, 어떠한 경우에도 목적 외 사용, 복제, 제3자에게 공개, 누설 및 유출할 수 없으며, 회사는 유포자의 불법 사용으로 피해가 발생할 경우 유포자에게 민/형사상 책임을 요구할 수 있음.