


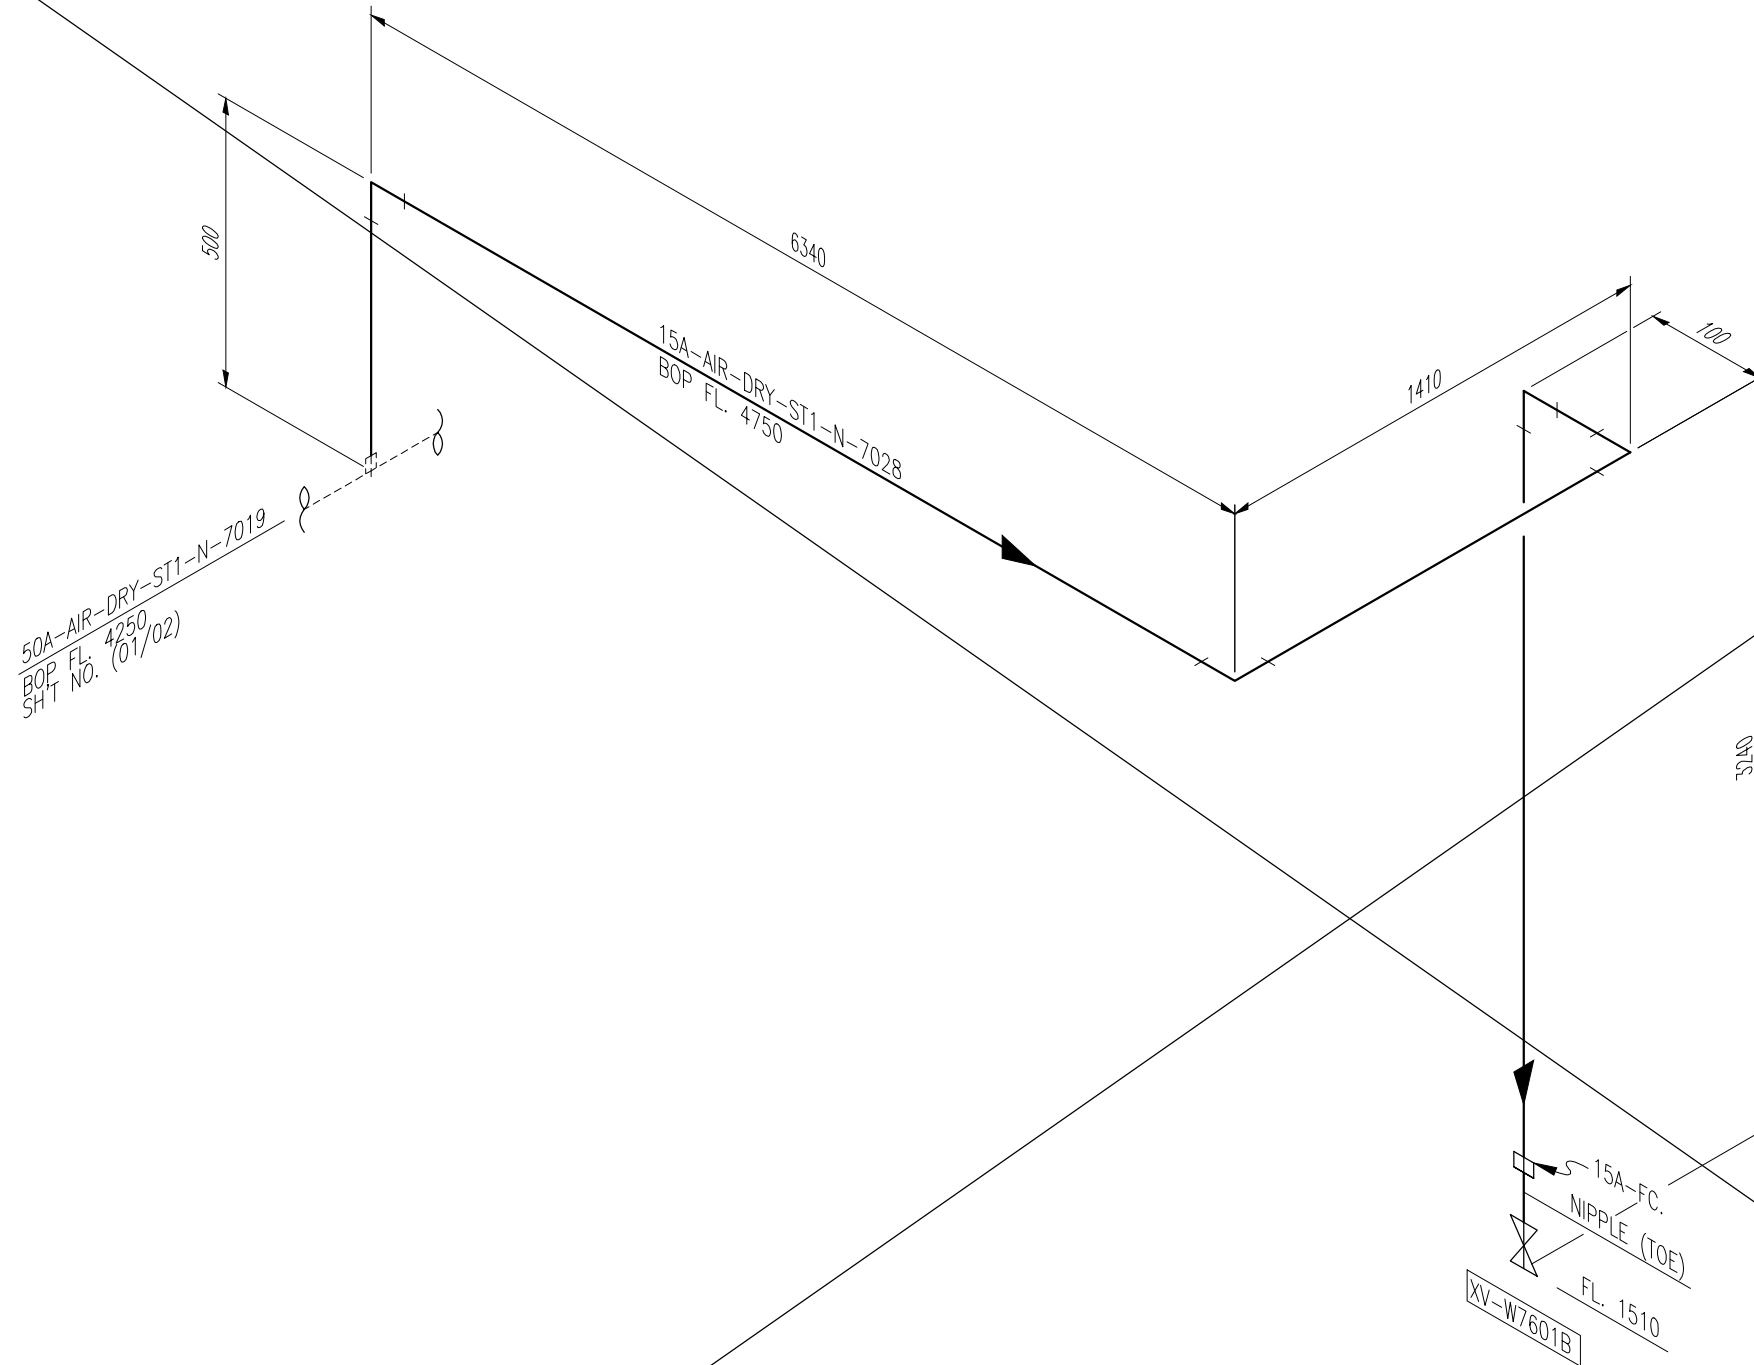

DELETED

1. (*) FIELD ADJUST

INSULATION	CODE	N	CONDITION	PRESS. (kg/cm2g)	TEMP. (°C)	AREA W14						
	THICK.	—	DESIGN	10	60	UNIT R1FA						
			OPERATING	7.5	AMB	REF. PLAN DWG. CJ—M15W14—PI—A30—010016—A		25.01.24	APPROVED FOR CONSTRUCTION	황래중	안남후	박동영
						REF. P & ID CJ—M15W14—PR—A20—000082—B						
						REV. NO.	DATE	DESCRIPTION	BY	CHK	APP	

CLIENT			
CONTRACTOR		PROJECT NAME	
		M15X Ph4 Project	
COMMODITY		JOB NO.	
AIR - DRY		223300	
LINE NO.		SH'T NO.	REV.
15A-AIR-DRY-ST1-N-7028		01 / 01	0