


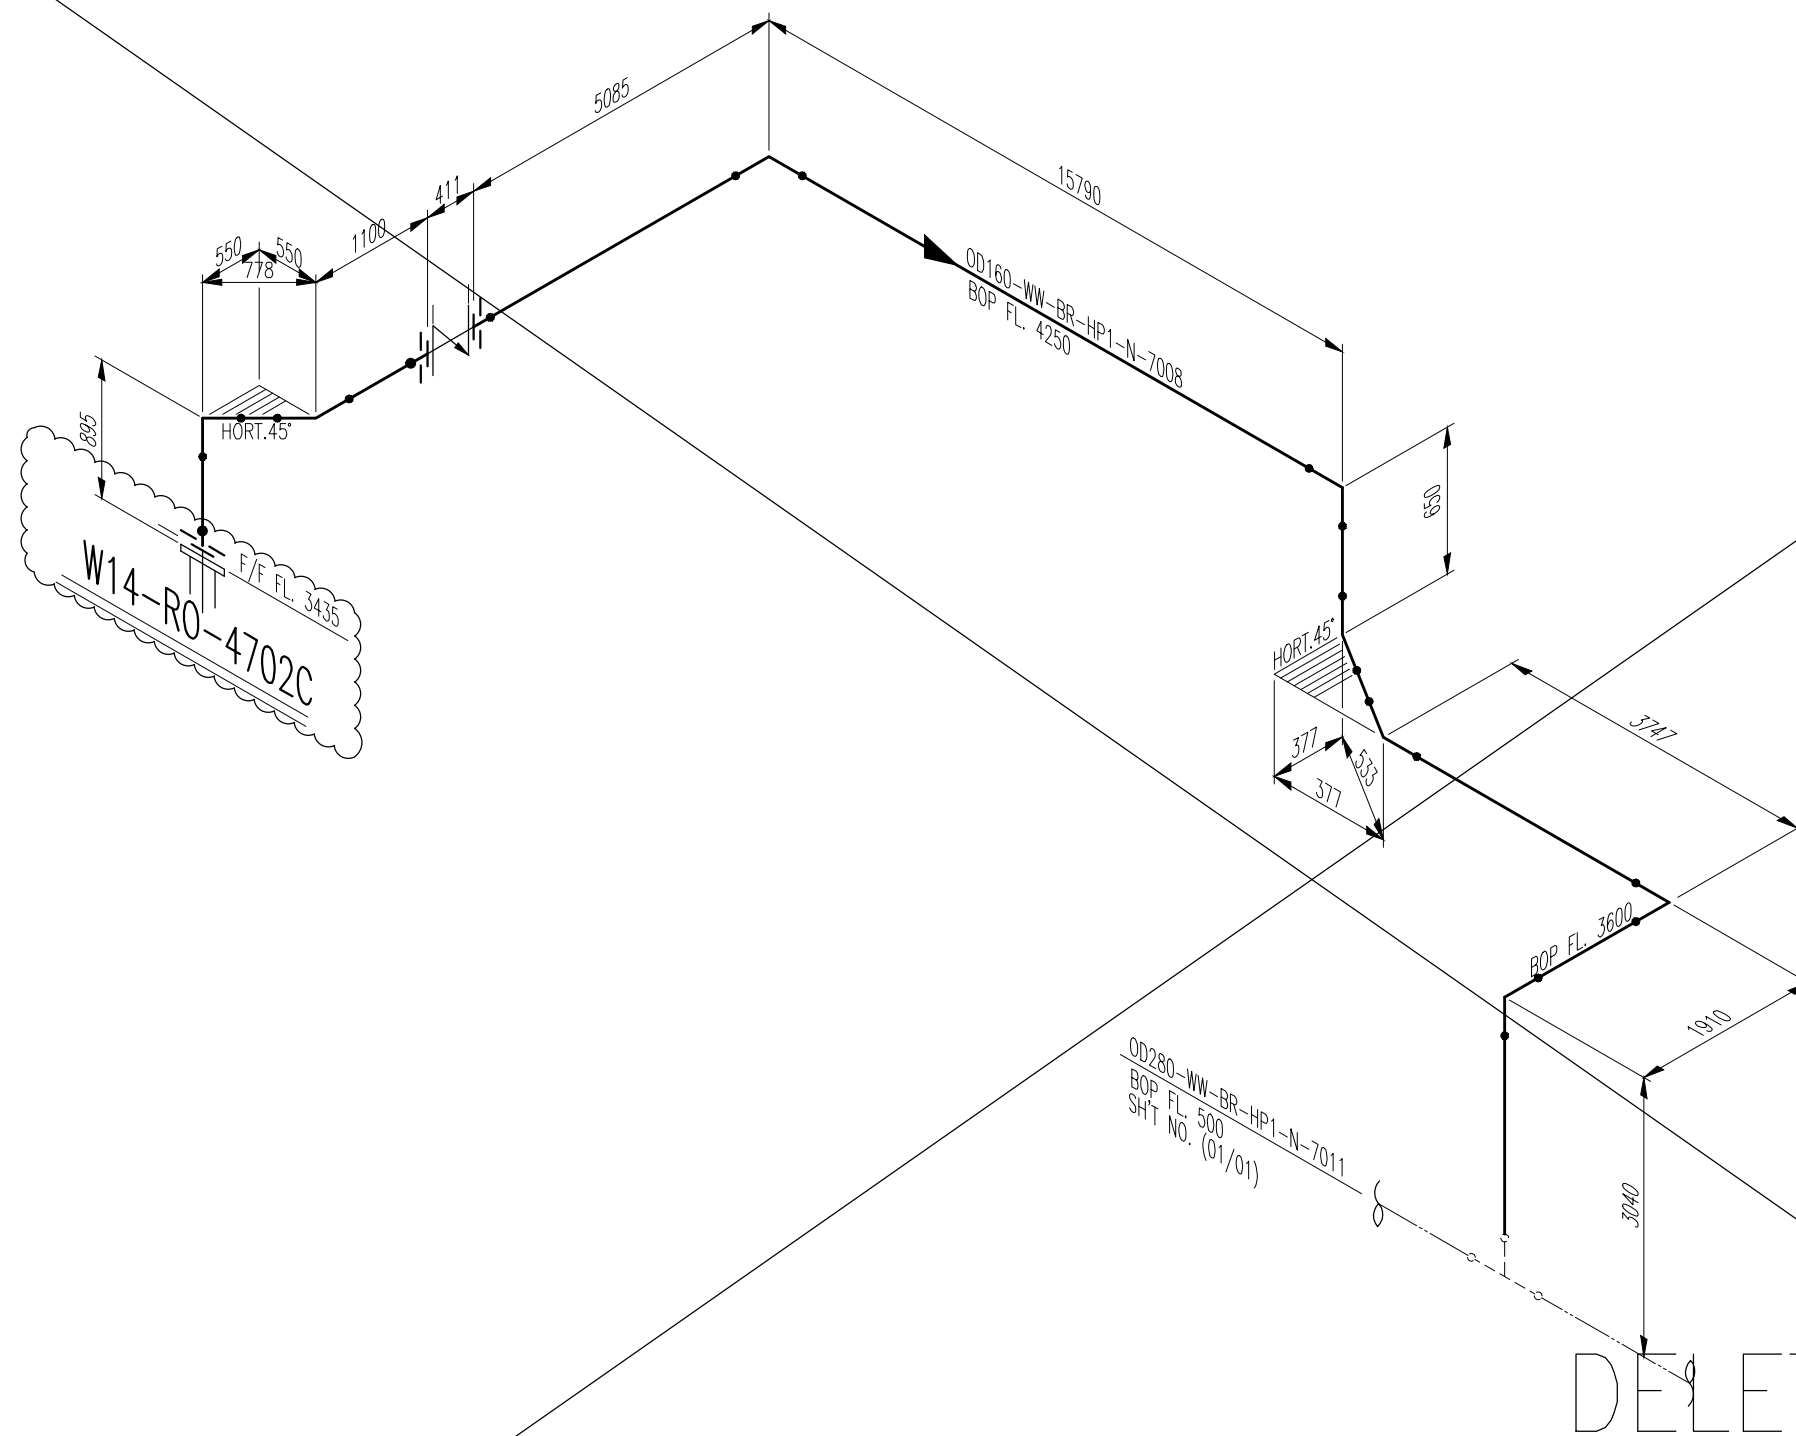

DELETED

[illegible]

CONTRACTOR		PROJECT NAME	
		M15X Ph4 Project	
COMMODITY		JOB NO.	
WW-BR		2239D	
LINE NO.	SH'T NO.	REV.	
OD160-WW-BR-HP1-N-7008	01 / 01	0	

INSULATION	CODE	N	CONDITION	PRESS. (kg/cm2g)	TEMP. (°C)	AREA W14						
	THICK.	-	DESIGN	6.4	60	UNIT R1FA						
			OPERATING	4	AMB	REF. PLAN DWG.						
						CJ-M15W14-PI-A30-010016-B		25.01.24	APPROVED FOR CONSTRUCTION	황래중	안남후	박동영
						REF. P & ID						
						CJ-M15W14-PR-A20-000308,000501	REV. NO.	DATE	DESCRIPTION	BY	CHK	APP'D