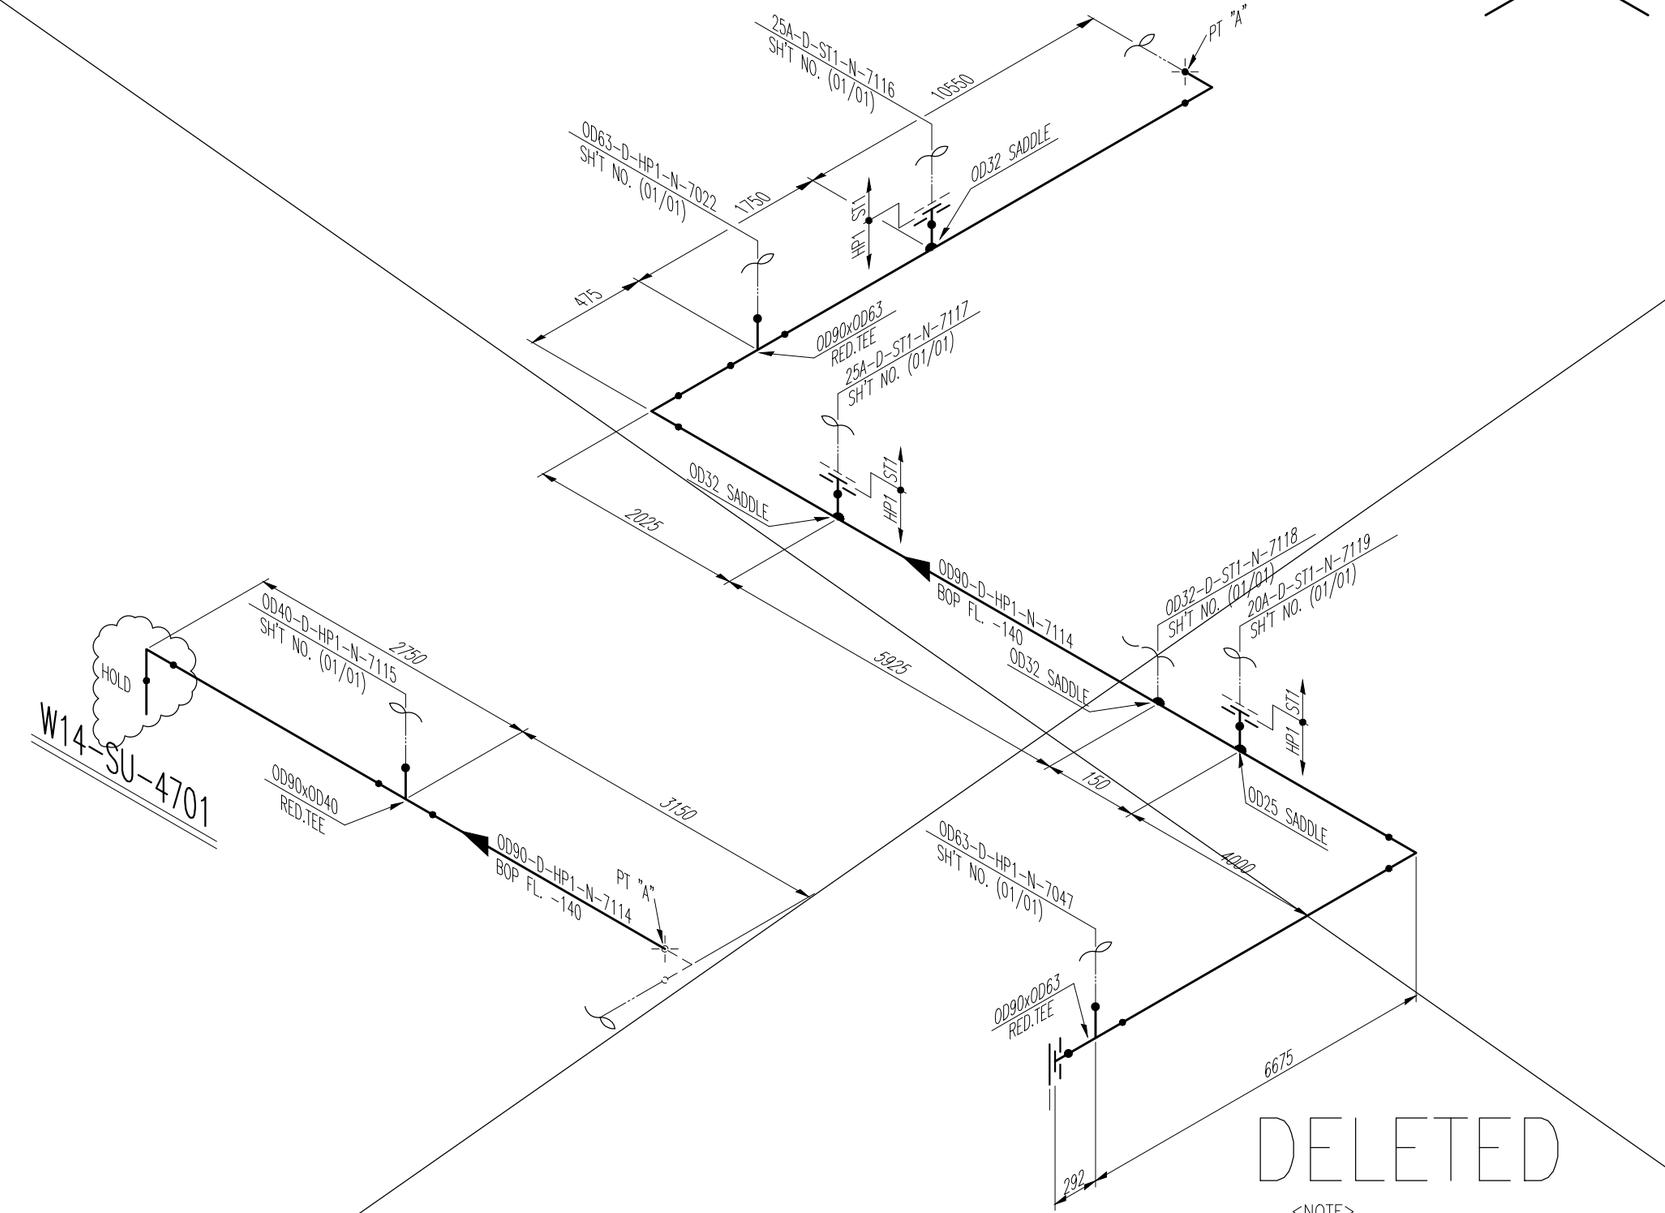



DELETED

<NOTE>
1. TRAY & ANGLE,CHANNEL SUPPORT가 적용되는 배관 ELEVATION은 현장 맞춤으로 한다.
2. (*) FIELD ADJUST

SK ecoplant

| ITEM | SIZE | Q'TY | DESCRIPTION |
|---|---|---|---|
| | | HP1 | |
| P | OD90 | 37.5M | PIPE, HDPE PE100, PE, BUTT FUSION, PN16/SDR11 |
| E90 | OD90 | 4EA | ELBOW 90 DEG, HDPE PE100, PE, BUTT FUSION, |
| | | | PN16/SDR11 |
| TR | OD90xOD40 | 1EA | TEE RED, HDPE PE100, PE, SOCKET FUSION, PN16/SDR11 |
| TR | OD90xOD63 | 1EA | TEE RED, HDPE PE100, PE, SOCKET FUSION, PN16/SDR11 |
| SD | OD90xOD25 | 1EA | SADDLE, HDPE PE100, PE, BRANCH-SOCKET FUSION, |
| | | | PN16/SDR11 |
| SD | OD90xOD32 | 3EA | SADDLE, HDPE PE100, PE, BRANCH-SOCKET FUSION, |
| | | | PN16/SDR11 |
| F | OD25 | 1EA | FLG LAP JOINT / STUB END SET, KS 10K, FF, |
| | | | LAP JOINT-STS304 / STUB END-HDPE PE100 |
| F | OD32 | 1EA | FLG LAP JOINT / STUB END SET, KS 10K, FF, |
| | | | LAP JOINT-STS304 / STUB END-HDPE PE100 |
| F | OD90 | 1EA | FLG LAP JOINT / STUB END SET, KS 10K, FF, |
| | | | LAP JOINT-STS304 / STUB END-HDPE PE100 |
| FB | OD90 | 1EA | FLG BLIND & LINER SET, KS 10K, FF, BLIND-STS304 |
| | | | / LINDER-HDPE PE100 (MIN 5.0MM TH'K) |
| G2 | OD90 | 1EA | GASKET, KS 10K, FF, PTFE+EPDM, BLIND, 3.0MM TH'K |
| B | OD90 | 1SET | MACHINE BOLT & NUTS :STS 304 / W WASHERS |

* PIPE : P/P1 * 90° ELBOW : E90 * 45° ELBOW : E45 * TEE : T * RED.TEE : TR * STUB-IN : STU * REINFORCING PAD : RP * CON.RED : RC * ECC.RED : RE * CON.SWAGE : RCS/RCS1 * ECC.SWAGE : RES/RES1 * NIPPLE : NP/NP1/NP2 * CAP : CAP/CAP1 * PLUG : PLG * FULL COUPLING : FC * HALF COUPLING : HF/HF1
* STUB-IN : STU * SOCKET(HDPE/PVC) : SC * SADDLE(HDPE) : SD * FLANGE : F/F1 * GASKET : G/G1/G2 * BOLT & NUT : B/B1 * BLIND FLANGE : FB/FB1 * GATE VA. : VG/VG1/VG2 * BALL VA. : VB/VBL0/VB1/VB1L0/VB2/VB2L0 * BUTTERFLY VA. : VF/VF4 * CHECK VA. : VC/VC1/VC2/VC3/VC4/VC5/VC6/VC7
* GLOBE VA. : VL/VL1/VL2 * DIAPHRAGM VA. : VD/VDL0 * DAMPER : VP * QUICK COUPLING : SQC * FLEXIBLE JOINT(STEEL) : FLXB * FLEXIBLE JOINT(RUBBER) : FLXR * FLEXIBLE JOINT(STEEL_PTFE LINED) : FLXL * FLEXIBLE HOSE : FLXH * STEAM TRAP : ST * SPRAY NOZZLE : SPN * EMERGENCY SHOWER : SSH
* STRAINER(Y-TYPE) : YSTR * STRAINER(T-TYPE) : TSTR * STRAINER(BUCKET-TYPE) : BSTR * ANCHOR PLATE : STOP * BIRD SCREEN : BS * ISOLATION KIT : IK * UNLOADING BOX : UB * AIR TRAP : AT * LOTO : LOTO * SIGHT GLASS : SG * PRESSURE GAUGE : PG * SHILED : SH * SPECIAL BOLT & NUT : BL/BL1

CLIENT SK hynix

| INSULATION | CODE | N | CONDITION | PRESS. (kg/cm2g) | TEMP. (°C) |
|---|---|---|---|---|---|
| | THICK. | – | DESIGN | 6.4 | 60 |
| | | | OPERATING | 4 | AMB |
| | | | | | |
| | | | | | |

AREA W14
UNIT R1FA
REF. PLAN DWG. CJ-M15W14-PI-A30-010018-A
REF. P & ID CJ-M15W14-PR-A20-000511

| REV. NO. | DATE | DESCRIPTION | BY | CHK | APP'D |
|---|---|---|---|---|---|
| 0 | 25.01.24 | APPROVED FOR CONSTRUCTION | 황래중 | 안남후 | 박동영 |

CONTRACTOR SK ecoplant
PROJECT NAME M15X Ph4 Project
COMMODITY D
JOB NO. 22330D
LINE NO. 0D90-D-HP1-N-7114
SH'T NO. 01 / 01
REV. 0

경고 : 본 도면은 SK HYNIX의 기업비밀 자료로서, 어떠한 경우에도 목적 외 사용, 복제, 제3자에게 공개, 누설 및 유출할 수 없으며, 회사는 유포자의 불법 사용으로 피해가 발생할 경우 유포자에게 민/형사상 책임을 요구할 수 있음.