

ISOMETRIC DRAWING LIST


PROJECT NO.: 22330D

PROJECT TITLE : M15X Ph4 Project


PFC-PRE(W)-501

NO	UNIT	LINE NUMBER	SHEET NUMBER	PKG NO	P&ID NO	REMARK
1	1FA	OD110-PFC-PRE(W)-HP1-N-9901-01	1 OF 1	501	CJ-M15W14-PR-A20-000601	
2	2FA	OD110-PFC-PRE(W)-HP1-N-9901-01	1 OF 2	501	CJ-M15W14-PR-A20-000601	
3	2FA	OD110-PFC-PRE(W)-HP1-N-9901-02	2 OF 2	501	CJ-M15W14-PR-A20-000601	
4	3FA	OD110-PFC-PRE(W)-HP1-N-9901-01	1 OF 1	501	CJ-M15W14-PR-A20-000601	


PFC-PRE(W)-501

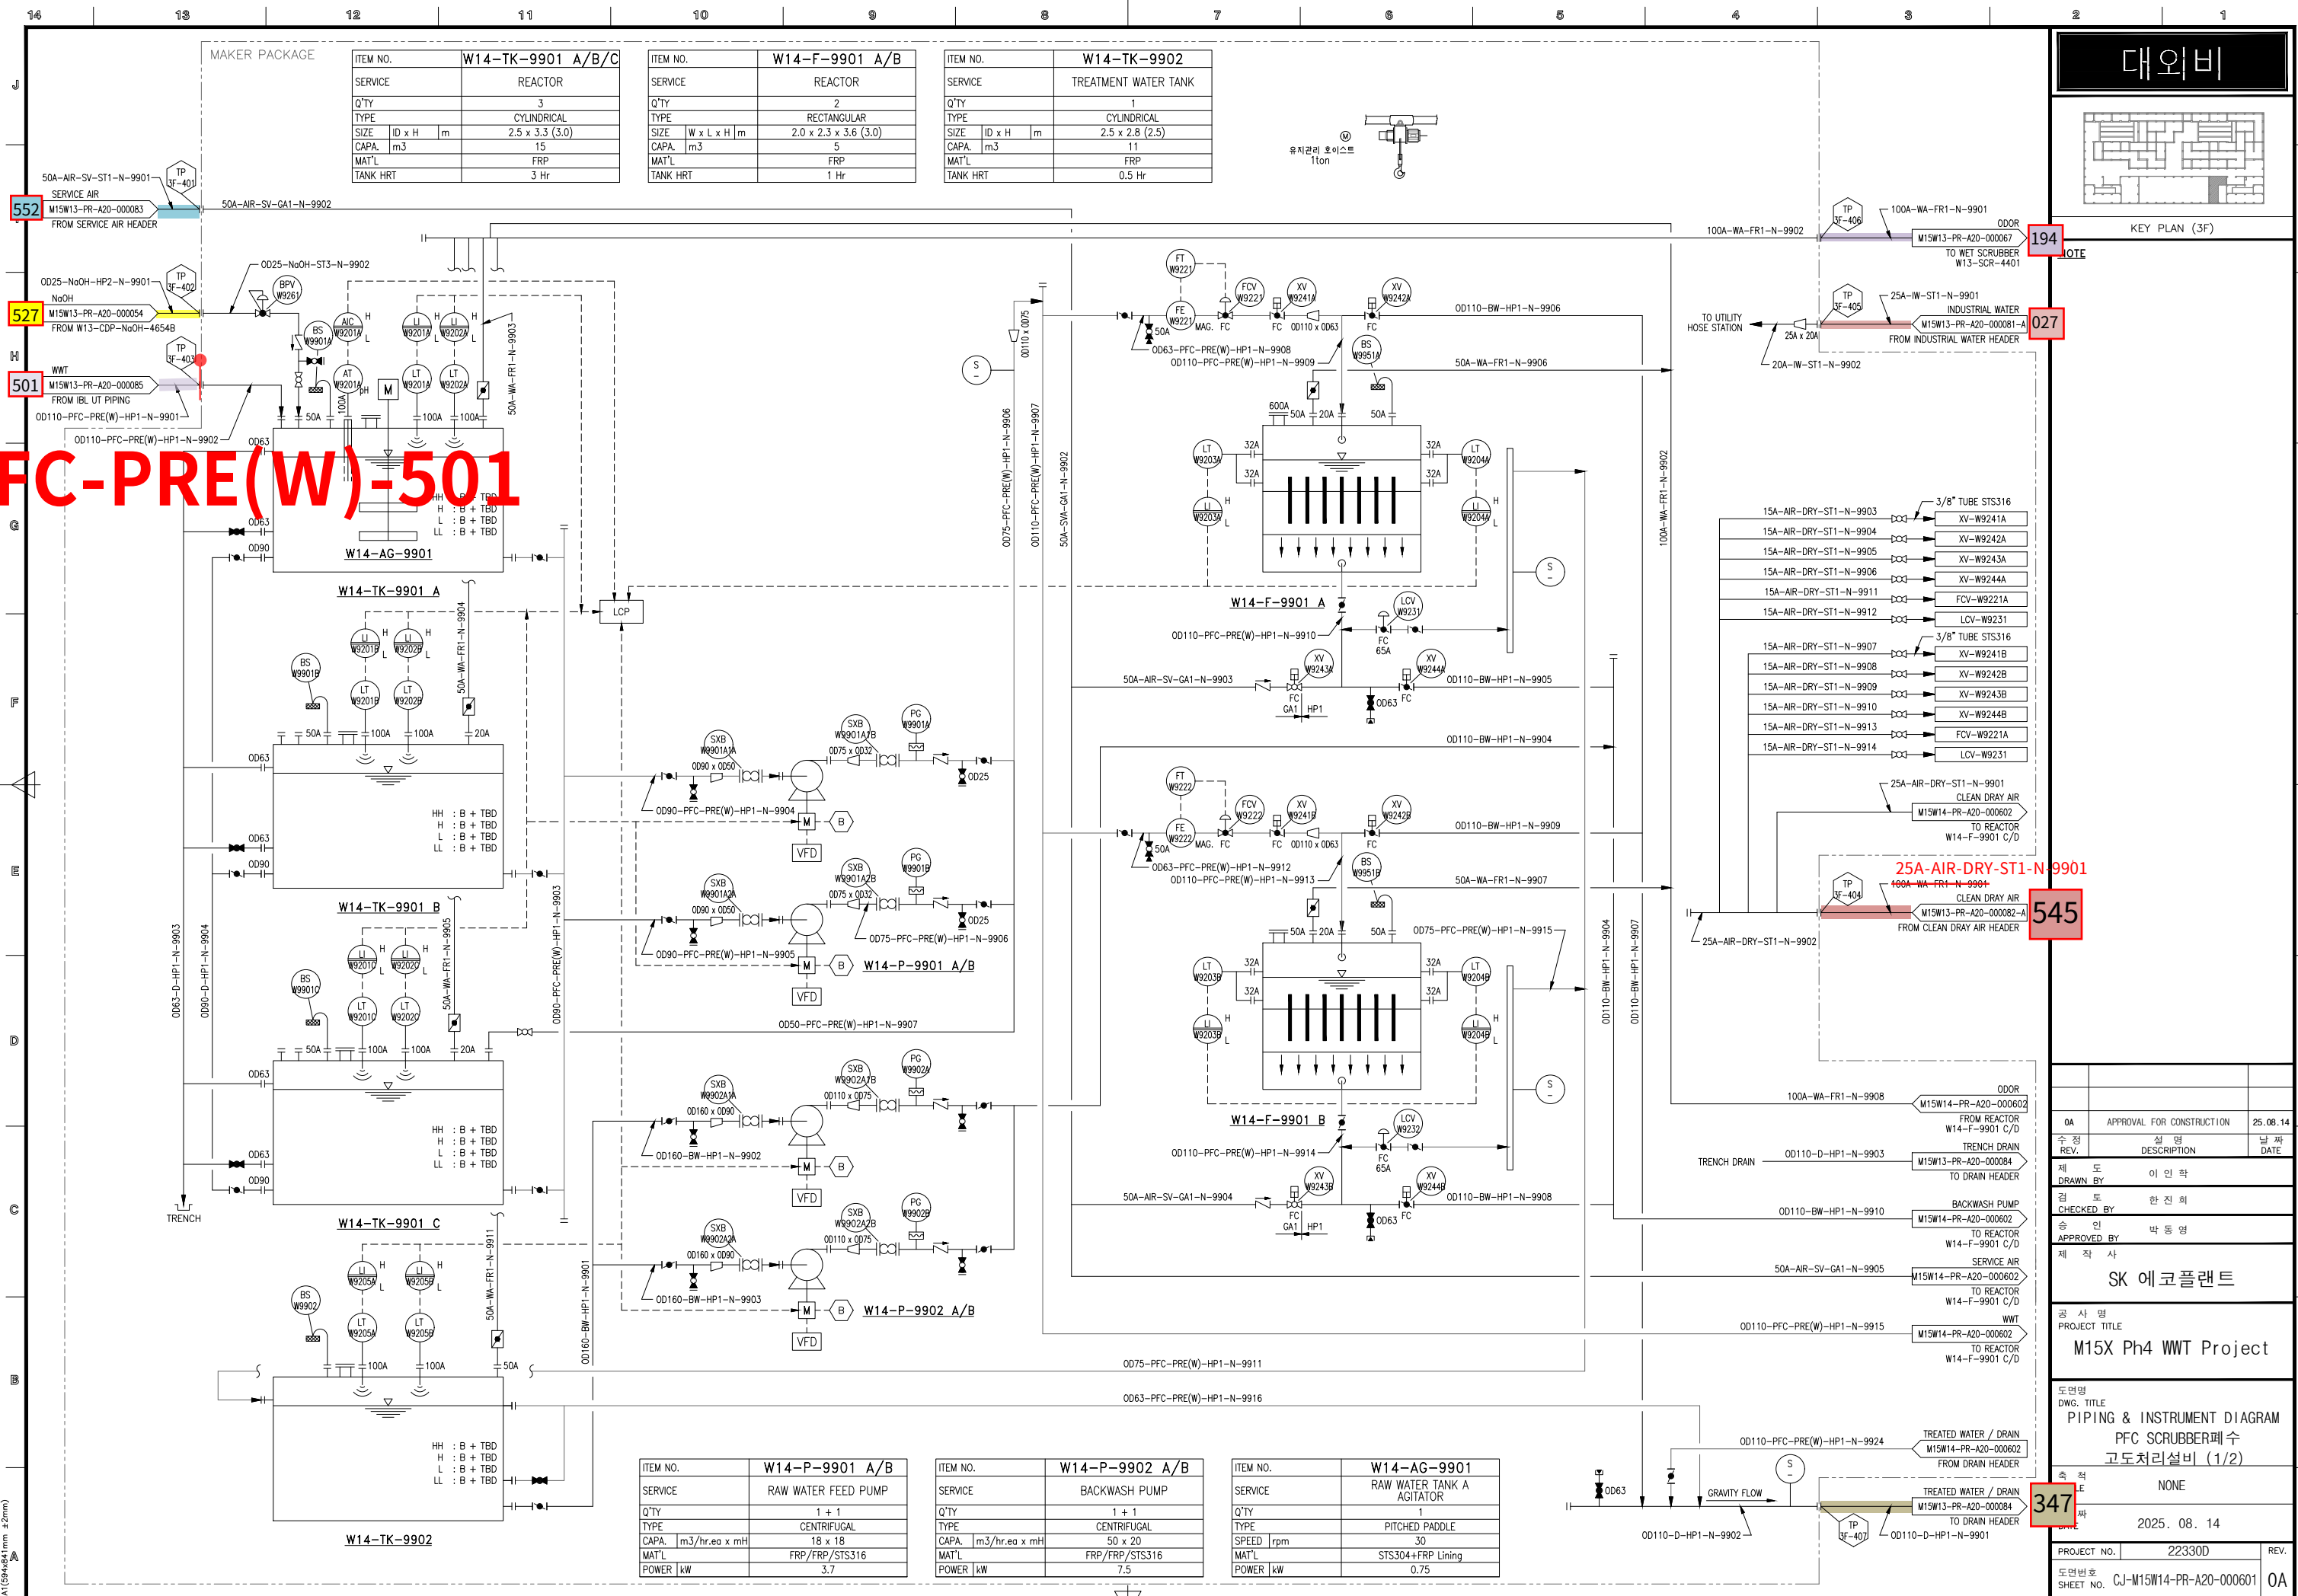

OVERALL INTERFACE SCHEME

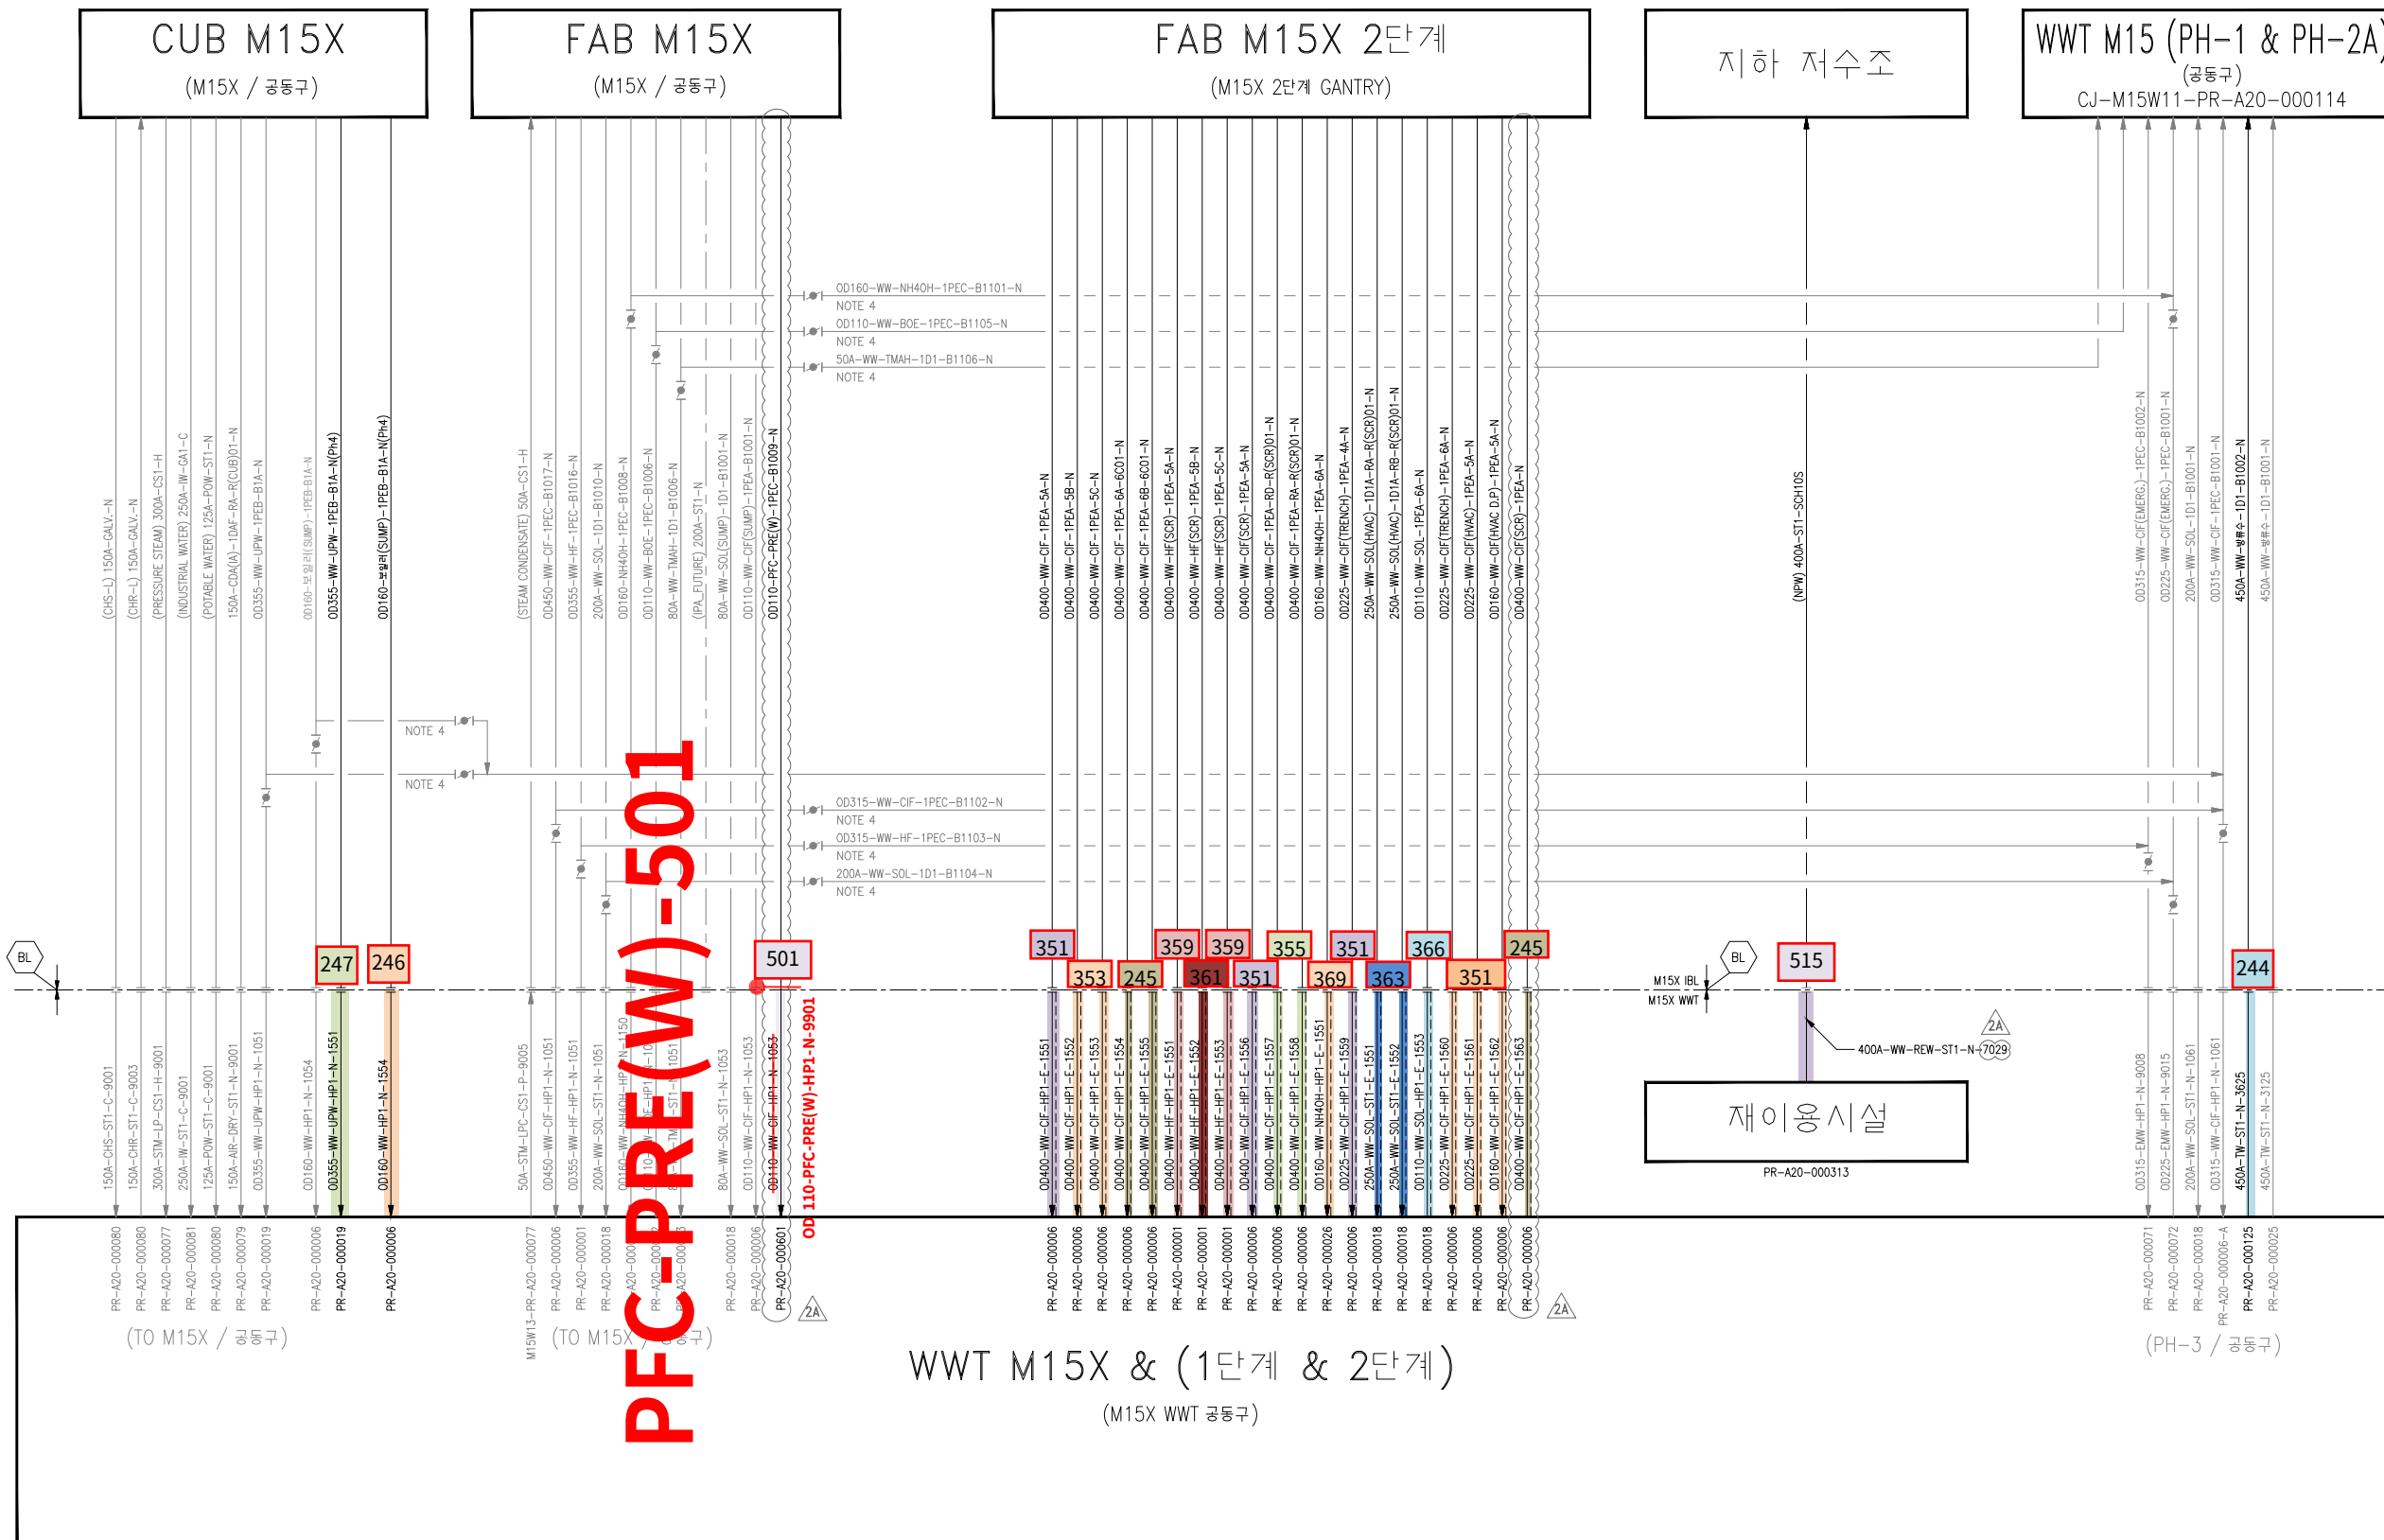

대외비

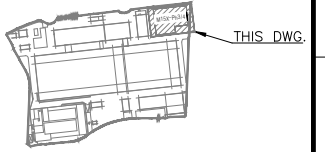

KEY PLAN

NOTE

1. PH-3 펌수는 WWTs에서 PUMPING 하여 공동구로 이송됨.
2. PH-4 펌수는 FAB에서 GRAVITY로 GANTRY를 통해 이송됨.
3. DELETED.
4. 초기 펌수 BACK-UP 용 보관.

LEGEND

_____ : PH-3 버전

_____ : PH-4 버전

2A	REVISED AFC	25.08.14
2	REVISED AFC	25.01.17
1	REVISED AFC	24.10.31
수정 REV.	설명 DESCRIPTION	날짜 DATE

제 도 이 인 학

검 토 하 지 회

승 인 바 도 여

제 작 사

SK 에코플랜트

공 사 명

M15X Ph4 WWT Project

PROJECT NO.	22330D
-------------	--------

2	REVISED AFC	24.06.21
1	REVISED AFC	23.02.28
0	APPROVAL FOR CONSTRUCTION	22.09.23
수정 REV.	설 명 DESCRIPTION	날 짜 DATE

제 도 한 진 회

검 토 시 무 요

스 인 바 드 어

APPROVED BY _____

SK 에코플랜트

공 사 명

M15X Ph3 WWT Project

두여면

OVERALL SCHEME

측 척
SCALE NONE


날 짜 2024. 06. 21
DATE

PROJECT NO.	22330D
-------------	--------

도면번호 C-I-M15W13-PB-A20-000

--	--


A

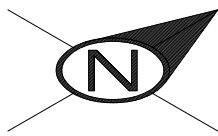

CONTRACTOR 		PROJECT NAME M15X Ph3 Project	
COMMODITY PFC-PRE(W)		JOB NO. 22330D	
LINE NO. OD110-PFC-PRE(W)-HP1-N-9901		SH'T NO. 01 / 01	REV. 0

INSULATION	CODE	N	CONDITION	PRESS. (kg/cm2g)	TEMP. (°C)	AREA W14						
	THICK.	—	DESIGN	5	60	UNIT 1FA						
			OPERATING	3.5	AMB	REF. PLAN DWG. CJ-M15W14-PI-A30-010016-A	0	25.03.31	APPROVED FOR CONSTRUCTION	황래중	안남후	박동영
					REF. P & ID CJ-M15W14-PR-A20-000601							
							REV. NO.	DATE	DESCRIPTION	BY	CHK	APP

PFC SCR SYSTEM 관련 LINE 추가

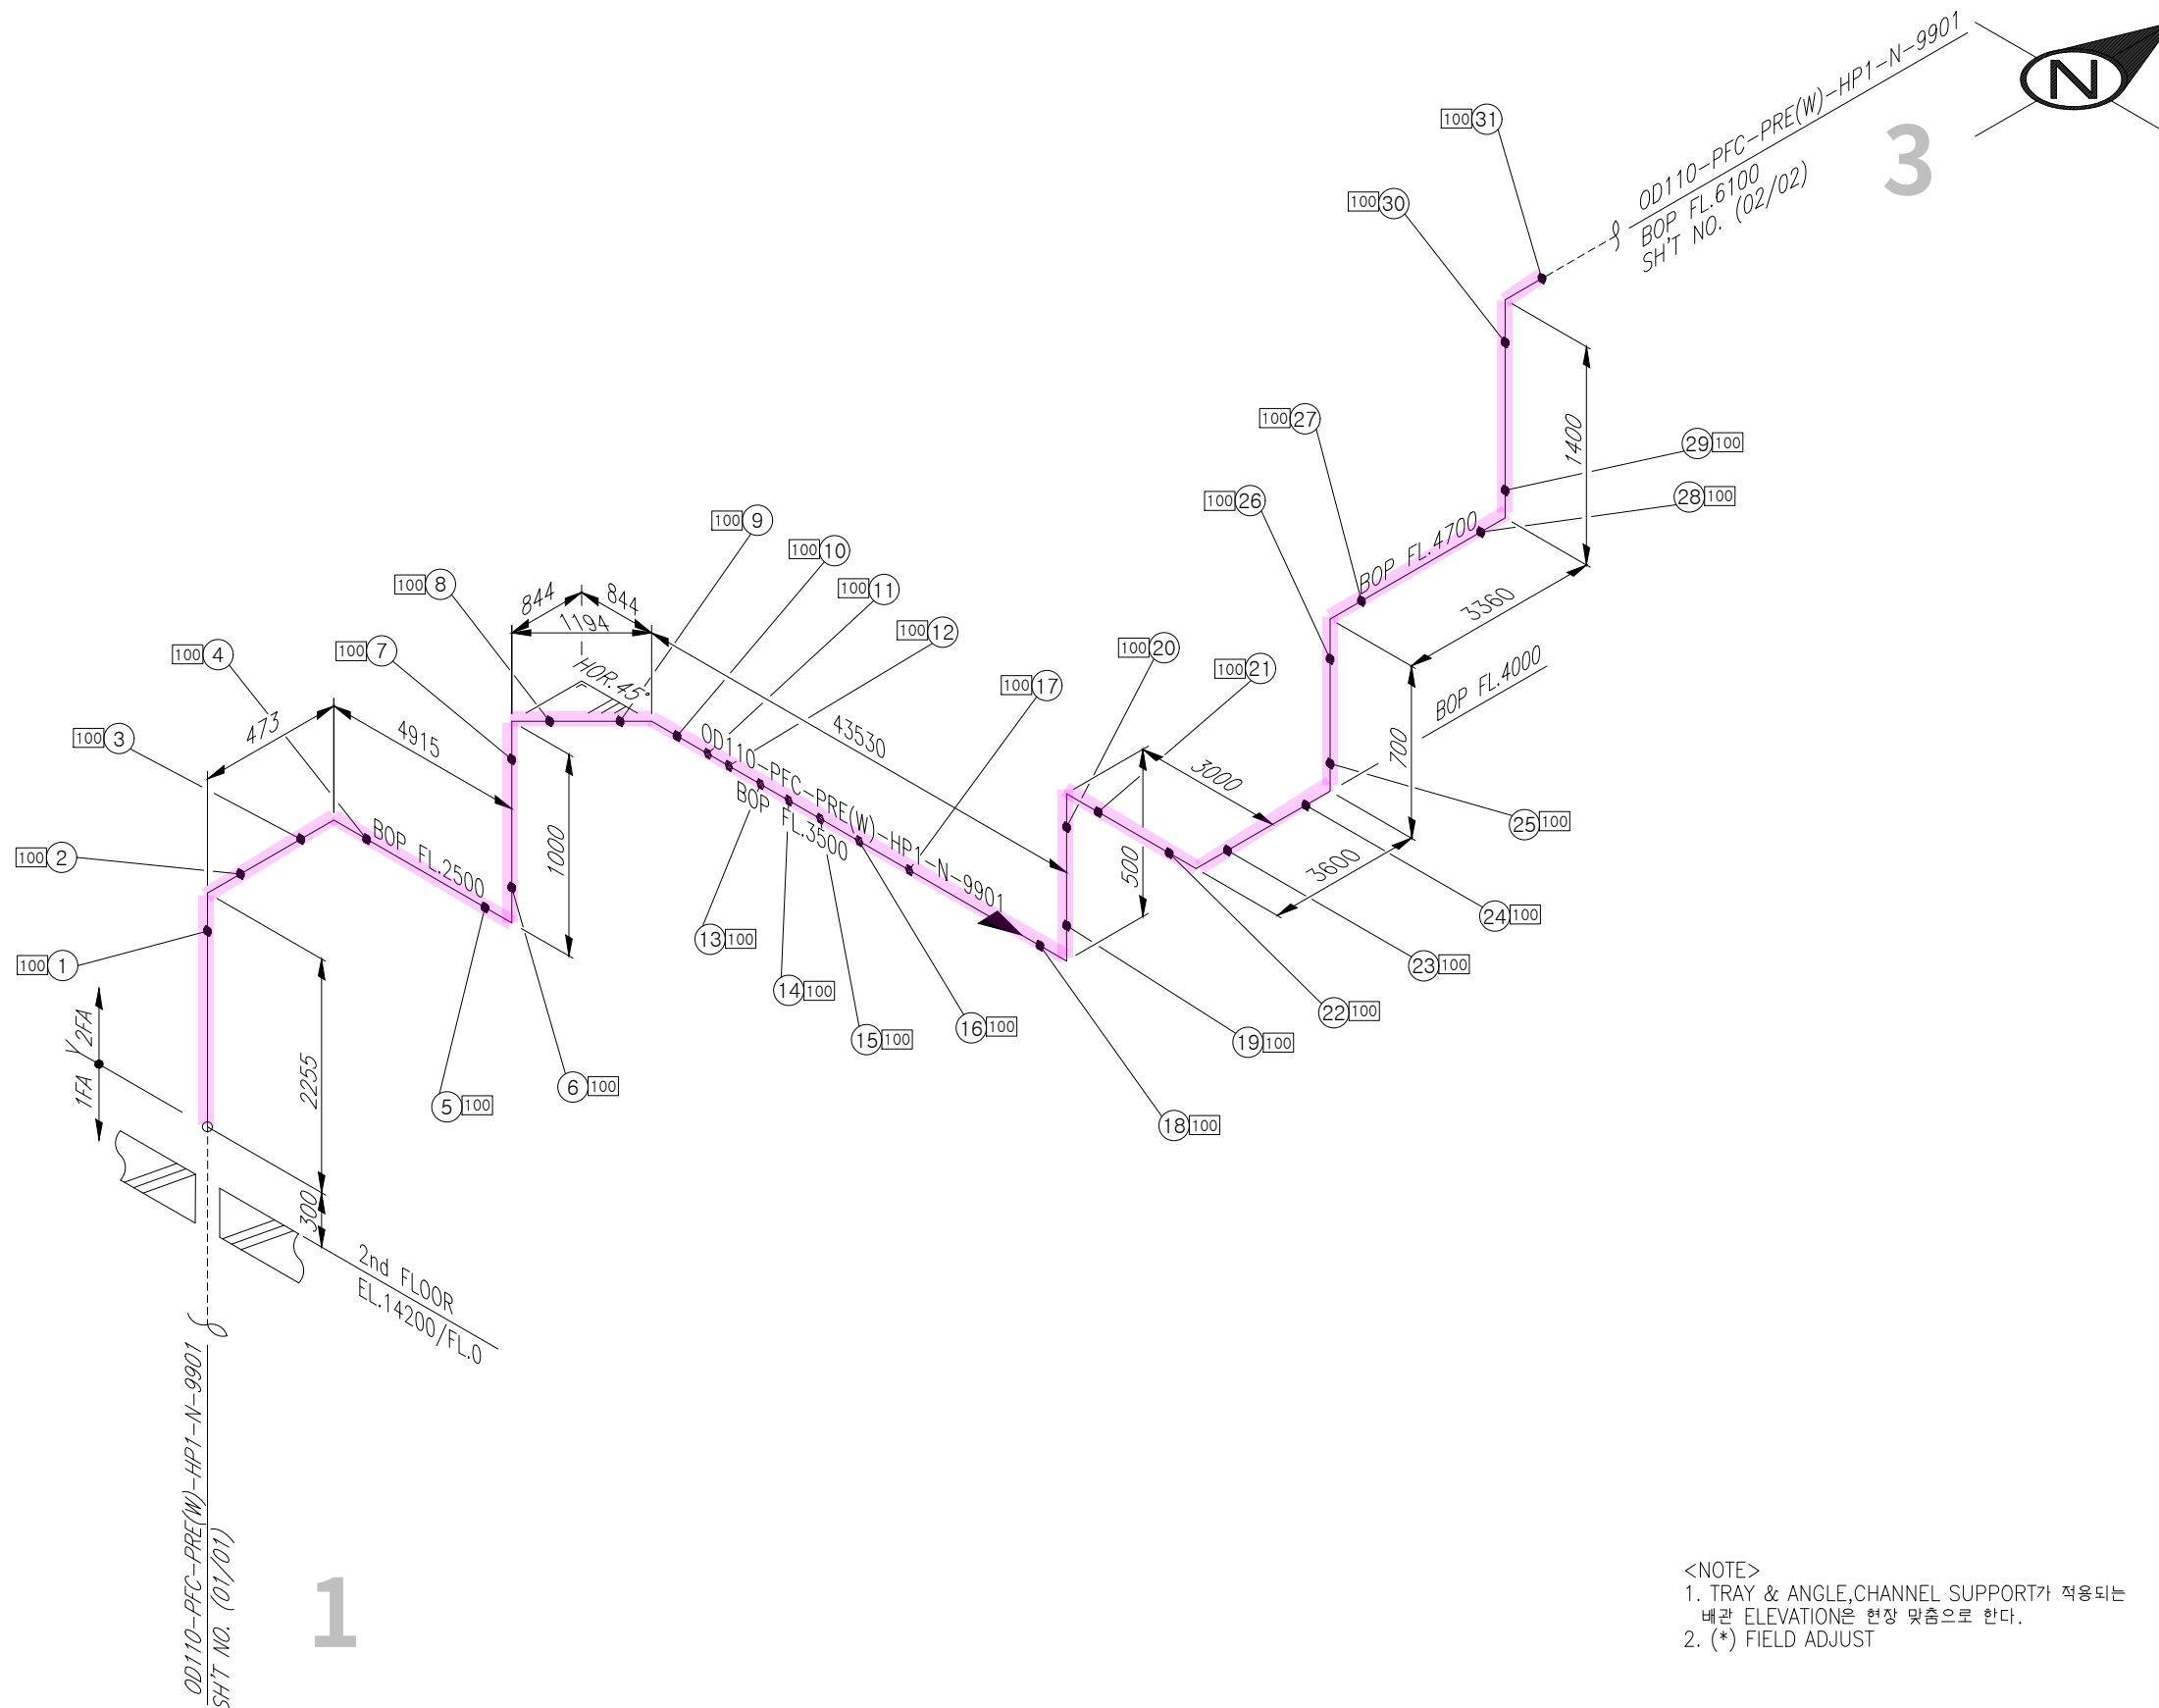


<NOTE>
1. TRAY & ANGLE, CHANNEL SUPPORT가 적용되는
배관 ELEVATION은 현장 맞춤으로 한다.
2. (*) FIELD ADJUST

[illegible]

INSULATION	CODE	N	CONDITION	PRESS. (kg/cm2g)	TEMP. (°C)	AREA	W14							CONTRACTOR	PROJECT NAME		
	THICK.	-	DESIGN	5	60	UNIT	2FA								M15X Ph3 Project		
			OPERATING	3.5	AMB	REF. PLAN DWG.									COMMODITY	PFC-PRE(W)	JOB NO.
							CJ-M15W14-PI-A30-020006-A									22330D	
						REF. P & ID								LINE NO.	0D110-PFC-PRE(W)-HP1-N-9901	SH'T NO.	REV.
						CJ-M15W14-PR-A20-000601										01 / 02	0
									25.03.31	APPROVED FOR CONSTRUCTION	황래중	안남후	박동영				
								REV. NO.	DATE	DESCRIPTION	BY	CHK	APP'D				

경고 : 본 도면은 SK HYNIX의 기밀비밀 자료로서, 어떠한 경우에도 목적 외 사용, 복제, 제3자에게 공개, 누설 및 유출할 수 없으며, 회사는 유포자의 불법 사용으로 피해가 발생할 경우 유포자에게 민/형사상 책임을 요구할 수 있음.

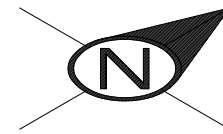

1. (*) FIELD ADJUST

OD110-PFC-PRE(W)-HP1-N-9901
SH'T NO. (01/01)

3rd FLOOR
EL.2720

4005

PT "

경고 : 본 도면은 SK HYNIX의 기밀비밀 자료로서, 어떠한 경우에도 목적 외 사용, 복제, 제3자에게 공개, 누설 및 유출할 수 없으며, 회사는 유포자의 불법 사용으로 피해가 발생할 경우 유포자에게 민/형사상 책임을 요구할 수 있음