

DRAWING LIST FOR TEST PACKAGE


PROJECT NO.: 22328D

PROJECT TITLE : M15X Ph4 Project


WW-REW-515

No	PKG No	UNIT	LINE NUMBER			P&ID		REMARK
			ISO DRAWING No	SHEET	REV	P&ID No	REV	
1	515	1FA	400A-WW-REW-ST1-C-7029-01	1 OF 1	0	CJ-M15W13-PR-A20-000085	2	
						CJ-M15W14-PR-A20-000313	1A	

OVERALL INTERFACE SCHEME

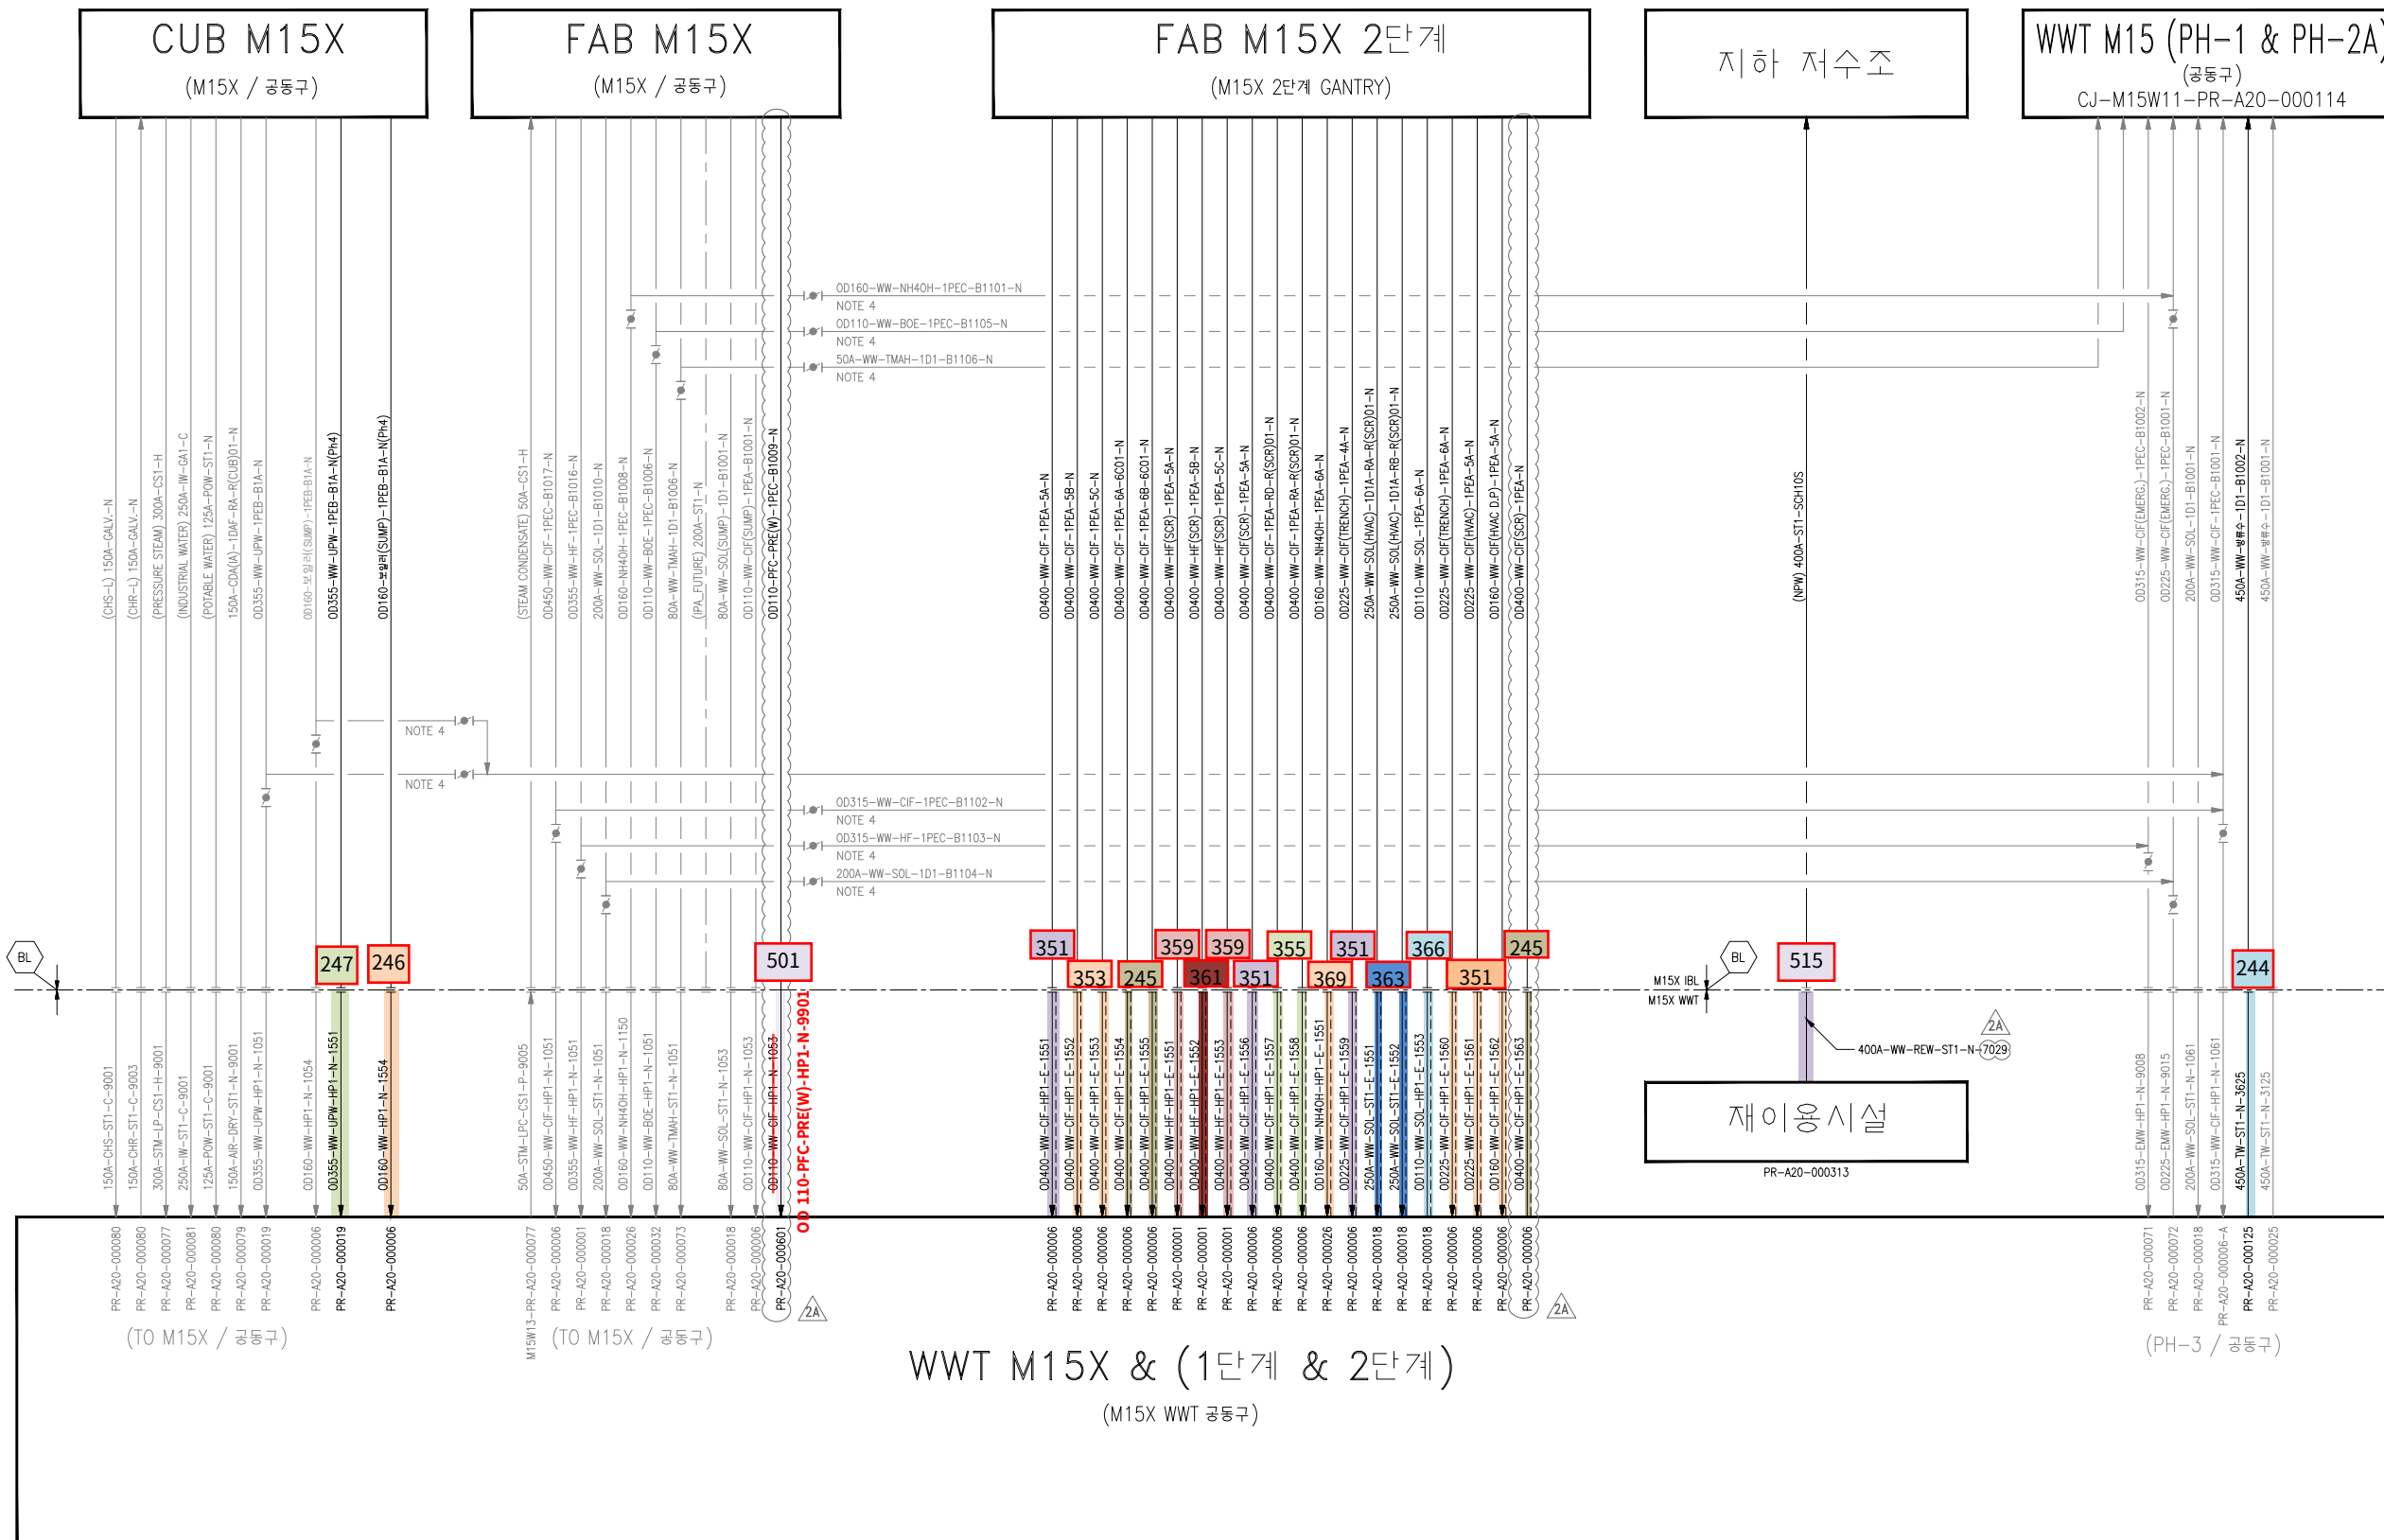

대오비

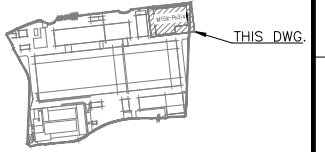

KEY PLAN

NOTE

1. PH-3 펌수는 WWTs에서 PUMPING 하여 공동구로 이송됨.
2. PH-4 펌수는 FAB에서 GRAVITY로 GANTRY를 통해 이송됨.
3. DELETED.
4. 초기 펌수 BACK-UP 용 보관.

LEGEND

- _____ : PH-3 보관
_____ : PH-4 보관

2A	REVISED AFC	25.08.14
2	REVISED AFC	25.01.17
1	REVISED AFC	24.10.31
수정 REV.	설명 DESCRIPTION	날짜 DATE

제 도 이 인 학

검 토 한 진 회

순	의	표	비	요
---	---	---	---	---

제 작 사

SK 에코플랜트

공 사 명

M15X Ph4 WWT Project

PROJECT NO.	22330D
-------------	--------

2	REVISED AFC	24.06.21
1	REVISED AFC	23.02.28
0	APPROVAL FOR CONSTRUCTION	22.09.23
수정 REV.	설 명 DESCRIPTION	날 짜 DATE

제 도 한 진 회

검 토 심 문 용

승 인 바 도 예

APPROVED BY _____
제 자 사

SK 에코플랜트

공 사 명

M15X Ph3 WWT Project

7. 7월 1일

DWG. TITLE

OVERALL SCHEME

축척 SCALE NONE

낙 짜

DATE 2024. 06. 21

PROJECT NO.	22330D
-------------	--------

도면번호
SHEET NO. CJ-M15W13-PR-A20-000085

--	--



CLIENT 

당고 : 「특」 도면은 SK HYNIX의 기밀비밀 자료로서, 어떠한 경우에도 목적 외 사용, 복제, 제3자에게 공개, 누설 및 유출할 수 없으며, 회사내 유무자의 무단 사용으로 피해가 발생할 경우 유무자에게 민/형사상 책임을 요구할 수 있음