

ISOMETRIC DRAWING LIST


PROJECT NO.: 22330D

PROJECT TITLE : M15X Ph4 Project

APOL-516

NO	UNIT	LINE NUMBER	SHEET NUMBER		P&ID NO	REMARK
1	3FA	65A-APOL-ST3-N-6526-01	1 OF 1	516	A20-000148	


MAKER PACKAGE	
ITEM NO.	W14-PD-4603 A
SERVICE	A-POLYMER AUTO DISSOLVING UNIT
Q'TY	1
SIZE	W x L x H m
CAPA	kg/hr
MAT'L	STS304
POWER	kw

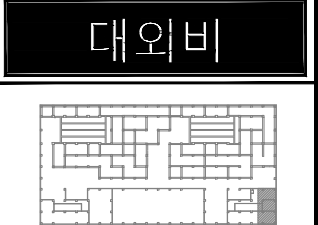


KEY PLAN (3F)

- 1. 약품종류에 따라 LINE 색상을 구분하여야 한다.
- 2. 약품용해장치 CURB 및 PUMP AREA에서 발생되는 누출액의 TRENCH로 흡수되어, DRAIN HEADER로 배출한다.
- 3. 약품 투입 PLATFORM, HANDRAIL 설치 할 것.
- 4. AGITATOR MAT'L 표기 : SHAFT/BLADE
- 5. 시 CLOSE 되는 내관에는 LOTO 설치.
- 6. INTERNAL PSV SET PRESSURE : 0.65 Mpag

539

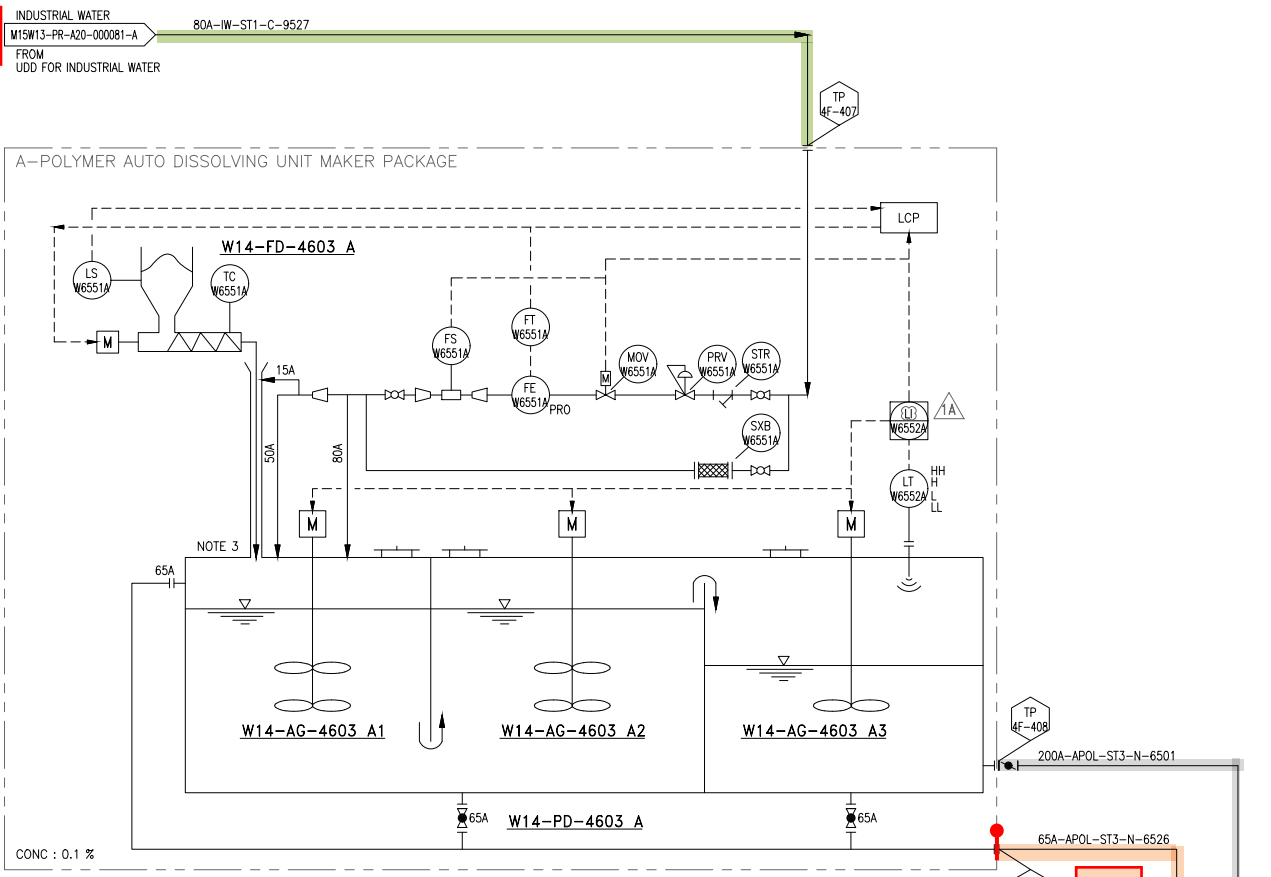


APOL-516

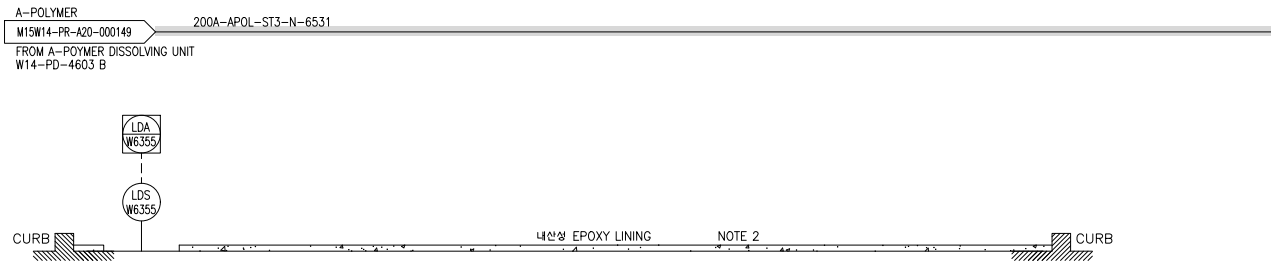

A-POLYMER AUTO DISSOLVING UNIT MAKER PACKAGE : DESIGN BY SUPPLIER	
ITEM NO.	W14-FD-4603 A
SERVICE	A-POLYMER FEEDER
Q'TY	1
TYPE	SCREW FEEDER
CAPA	kg/hr
MAT'L	STS304
POWER	kw

ITEM NO.	W14-AG-4603 A1/A2/A3
SERVICE	A-POLYMER AGITATOR
Q'TY	3
TYPE	PROPELLER
CAPA	kg/hr
MAT'L	STS304L/STS304L
POWER	kw

ITEM NO.	W14-CDP-APOL-4625 A/B/C/D
SERVICE	A-POLYMER FEED PUMP
Q'TY	3 + 1
TYPE	ROTARY LOBE (VVVF)
CAPA	m3/hr.ea x MPa
MAT'L	(NBR/GC250/SCM440)
POWER	kw

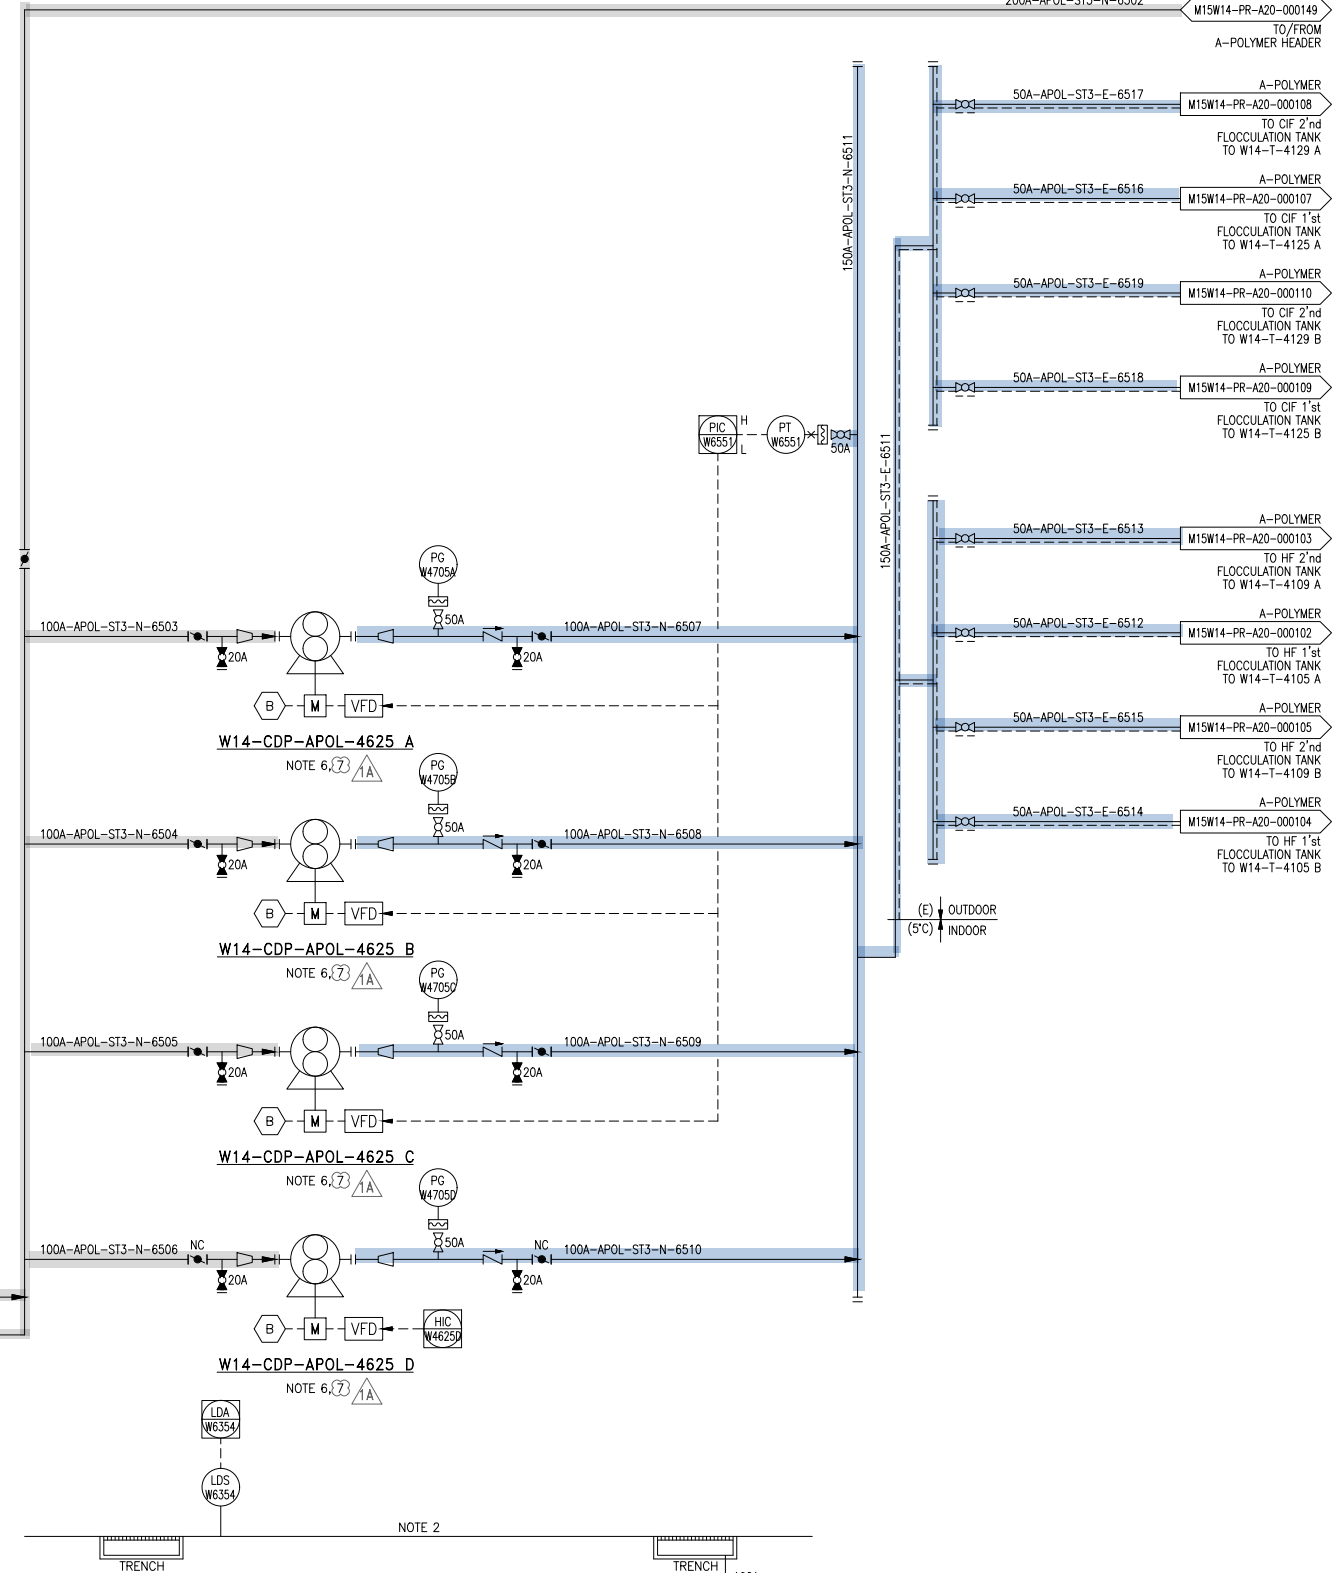

515
514
514
514
514
514
514
514
514
514
514

1A	REVISED AFC	25.08.14
1	REVISED AFC	25.01.17
0	APPROVAL FOR CONSTRUCTION	24.09.30

수정	실명	날짜
REV.	DESCRIPTION	DATE

제	도	이	인	학
DRAWN BY				

검	토	한	진	회
CHECKED BY				

승	인	박	동	영
APPROVED BY				

제	작	사

공	사	명
PROJECT TITLE		

도	면	명
DWG. TITLE		

속	척
SCALE	NONE

날	짜	DATE
		2025. 08. 14

PROJECT NO.	22330D	REV.	A
도면번호			

SHEET NO.	CJ-M15W14-PR-A20-000148	1A
-----------	-------------------------	----




CLIENT  1

CONTRACTOR 		PROJECT NAME M15X Ph4 Project	
COMMODITY APOL		JOB NO. 22330D	
LINE NO. 65A-APOL-ST3-N-6549		SH'T NO. 01 / 01	REV. 0



* PIPE : P/P1	* 90° ELBOW : E90	* 45° ELBOW : E45	* TEE : T	* RED.TEE : TR	* STUB-IN : STU	* REINFORCING PAD : RP	* CON.RED : RC	* ECC.RED : RE	* CON.SWAGE : RCS/RCS1	* ECC.SWAGE : RES/RES1	* NIPPLE : NP/NP1/NP2	* CAP : CAP/CAP1	* PLUG : PLG	* FULL COUPLING : FC	* HALF COUPLING : HF/HF1
* STUB-IN : STU	* SOCKET(HDPE/PVC) : SC	* SADDLE(HDPE) : SD	* FLANGE : F/F1	* GASKET : G/G1/G2	* BOLT & NUT : B/B1	* BLIND FLANGE : FB/FB1	* GATE VA. : VG/VG1/VG2	* BALL VA. : VB/VBLO/VB1/VB1LO/VB2/VB2LO	* BUTTERFLY VA. : VF/VF4	* CHECK VA. : VC/VC1/VC2/VC3/VC4/VC5/VC6/VC7					
* GLOBE VA. : VL/VL1/VL2	* DIAPHRAGM VA. : VD/VDLO	* DAMPER : VP	* QUICK COUPLING : SQC	* FLEXIBLE JOINT(STEEL) : FLXB	* FLEXIBLE JOINT(RUBBER) : FLXR	* FLEXIBLE JOINT(STEEL PTFE LINED) : FLXL	* FLEXIBLE HOSE : FLXH	* STEAM TRAP : ST	* SPRAY NOZZLE : SPN	* EMERGENCY SHOWER : SSH					
* STRAINER(Y-TYPE) : YSTR	* STRAINER(T-TYPE) : TSTR	* STRAINER(BUCKET-TYPE) : BSTR	* ANCHOR PLATE : STOP	* BIRD SCREEN : BS	* ISOLATION KIT : IK	* UNLOADING BOX : UB	* AIR TRAP : AT	* LOTO : LOTO	* SIGHT GLASS : SG	* PRESSURE GAUGE : PG	* SHILED : SH	* SPECIAL BOLT & NUT : BL/BL1			

 INSULATION	CODE	N	CONDITION	PRESS. (kg/cm2g)	TEMP. (°C)	AREA W14						CONTRACTOR	PROJECT NAME		
	THICK.	—	DESIGN	1.0	60	UNIT 3FA							M15X Ph4 Project		
			OPERATING	ATM	AMB	REF. PLAN DWG. CJ-M15W14-PI-A30-030008-A							COMMODITY	JOB NO.	
						REF. P & ID CJ-M15W14-PR-A20-000149		25.01.24	APPROVED FOR CONSTRUCTION	황래중	안남후	박동영	22330D		
							REV. NO.	DATE	DESCRIPTION	BY	CHK	APP'D		LINE NO.	SH'T NO.
													65A-APOL-ST3-N-6549	01 / 01	0