

DRAWING LIST FOR TEST PACKAGE


PROJECT NO.: 22328D

PROJECT TITLE : M15X Ph2 Project

CPOL-519


No	PKG No	UNIT	LINE NUMBER			P&ID		REMARK
			ISO DRAWING No	SHEET	REV	P&ID No	REV	
1	519	3FA	65A-CPOL-ST3-N-6513-01	1 OF 1	0	CJ-M15W14-PR-A20-000150	1A	

ITEM NO.	W14-PD-4604
SERVICE	C-POLYMER AUTO DISSOLVING UNIT
Q'TY	1
SIZE	W x L x H m
CAPA.	kg/hr
MAT'L	STS304
POWER	2.65
MAKER PACKAGE	

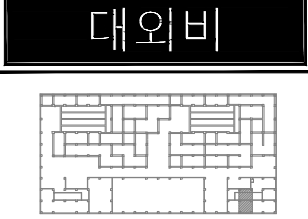


- NOTE
- 1.약품종류에 따라 LINE 역상을 구분하여야 한다.
 2. POLYMER 용해장치 CURB 및 PUMP AREA에서 발생되는 DRAIN은 인근의 TRENCH로 흡수되어, DRAIN HEADER로 이송된다.
 - 3.상부 PLATFORM, HANDRAIL 설치 할 것.
 4. AGITATOR MAT'L 표기 : SHAFT/BLADE
 - 5.론전 시 CLOSE 되는 내관에는 LOTO 설치.
 6. INTERNAL PSV 설치 할 것.
 7. INTERNAL PSV SET PRESSURE : 0.65 Mpag

539

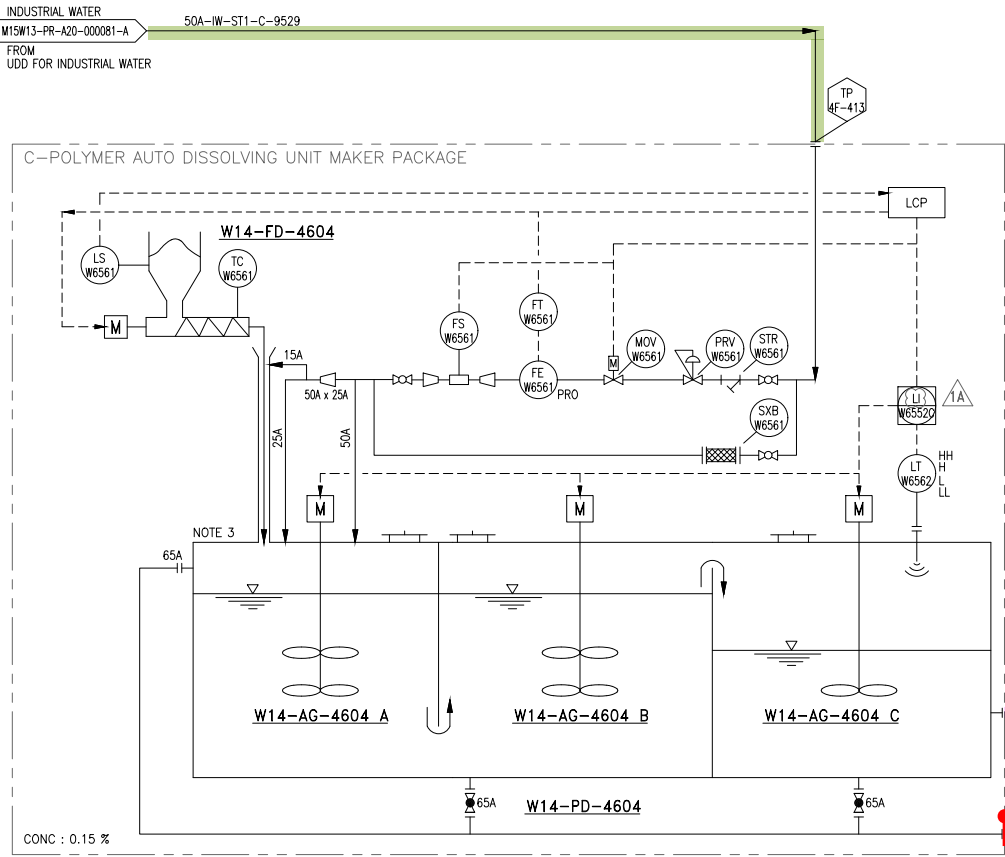

518

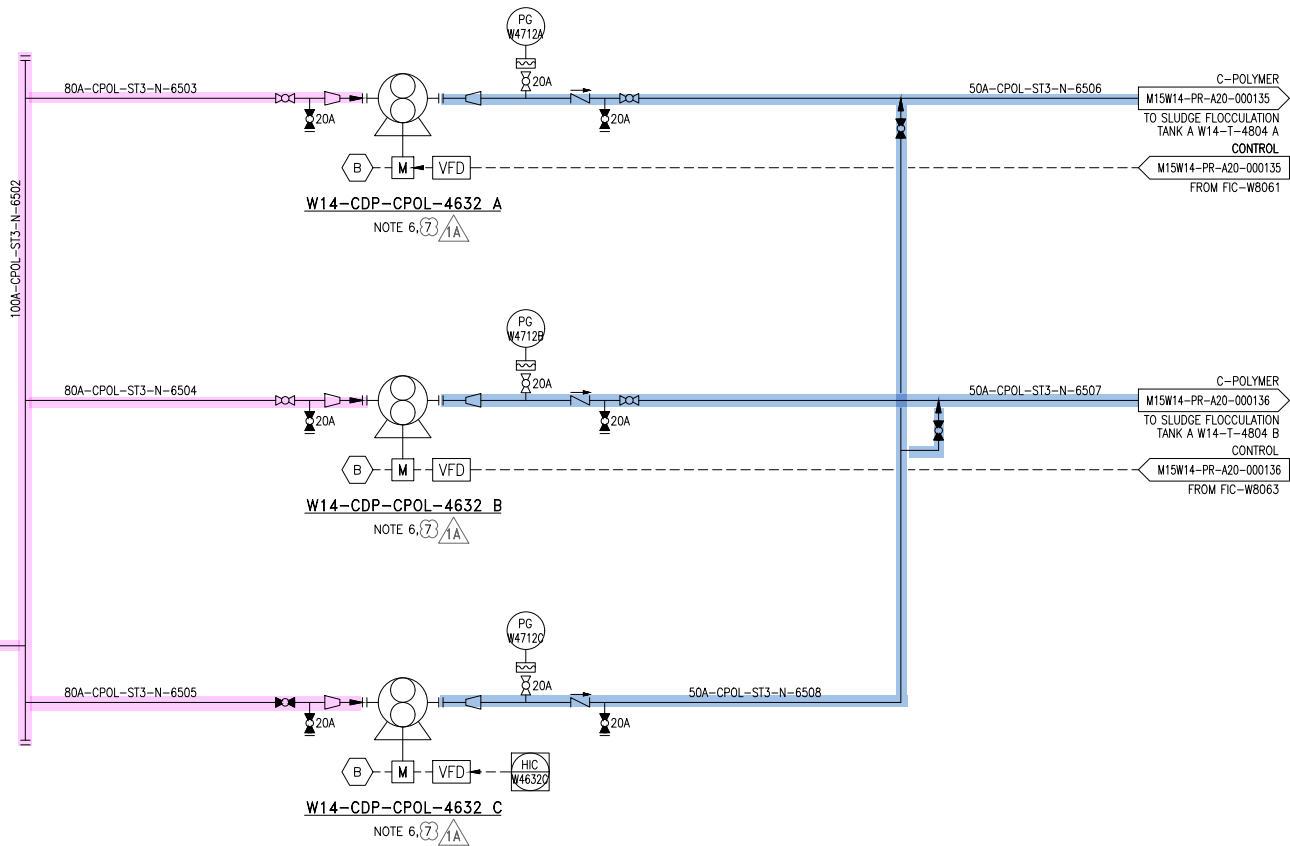

444

CPOL-519

519

C-POLYMER AUTO DISSOLVING UNIT MAKER PACKAGE : DESIGN BY SUPPLIER			
ITEM NO.	W14-FD-4604	ITEM NO.	W14-AG-4604 A/B/C
SERVICE	C-POLYMER FEEDER	SERVICE	C-POLYMER AGITATOR
Q'TY	1	Q'TY	3
TYPE	SCREW FEEDER	TYPE	PROPELLER
CAPA.	kg/hr	SPEED	rpm
MAT'L	STS304	MAT'L	STS304/STS304
POWER	kw	POWER	kw

ITEM NO.	W14-CDP-CPOL-4632 A/B/C
SERVICE	C-POLYMER FEED PUMP
Q'TY	2 + 1
TYPE	ROTARY LOBE (VWF)
CAPA.	m3/hr.ea x MPa
MAT'L	(NBR/GC250/SCM440)
POWER	kw

1A	REVISED AFC	25.08.14
1	REVISED AFC	25.01.17
0	APPROVAL FOR CONSTRUCTION	24.09.30
수정 REV.	실명 DESCRIPTION	날짜 DATE

제 도 이 인 학
DRAWN BY
검 토 한 진 회
CHECKED BY
승 인 박 동 명
APPROVED BY

제 작 사 SK 에코플랜트

공 사 명 PROJECT TITLE
M15X Ph4 WWT Project


도면명 DWG. TITLE
PIPING & INSTRUMENT DIAGRAM
C-POLYMER AUTO DISSOLVING UNIT & FEED PUMP

속 척 SCALE NONE
날 짜 DATE 2025. 08. 14

PROJECT NO. 22330D
도면번호 SHEET NO. CJ-M15W14-PR-A20-000150
REV. 1A



ITEM	SIZE	Q'TY	DESCRIPTION
		ST3	
P	65A	2.1M	PIPE, STS 304TP, ERW, BE - SCH 10S
E90	65A	2EA	ELBOW 90 DEG LR, STS304, ERW, BE - SCH 10S
F	65A	1EA	FLG SO, KS 10K, RF, STS304
G	65A	1EA	GASKET, KS 10K, RF, PTFE+EPDM, 3.0MM TH'K
B	65A	1SET	MACHINE BOLT & NUTS :STS 304 / W WASHERS

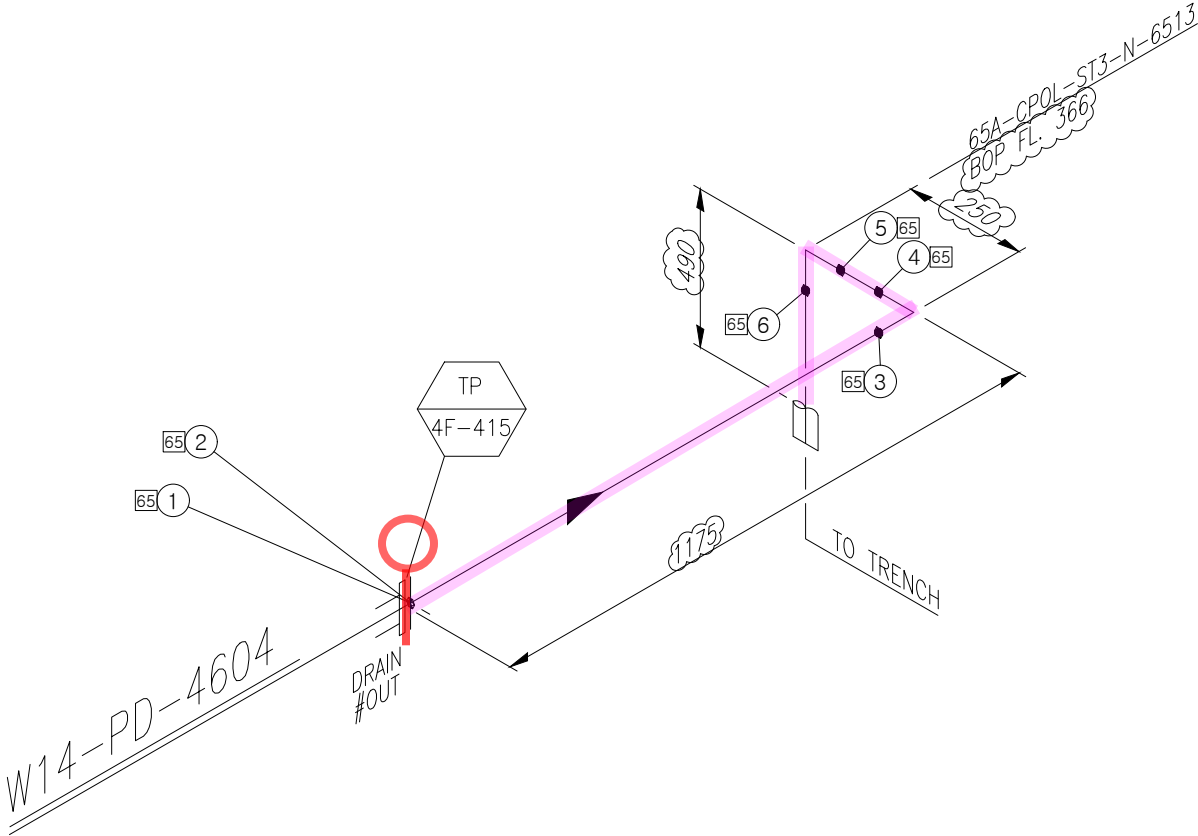

<NOTE>
1. (*) FIELD ADJUST

* PIPE : P/P1	* 90° ELBOW : E90	* 45° ELBOW : E45	* TEE : T	* RED.TEE : TR	* STUB-IN : STU	* REINFORCING PAD : RP	* CON.RED : RC	* ECC.RED : RE	* CON.SWAGE : RCS/RCS1	* ECC.SWAGE : RES/RES1	* NIPPLE : NP/NP1/NP2	* CAP : CAP/CAP1	* PLUG : PLG	* FULL COUPLING : FC	* HALF COUPLING : HF/HF1
* STUB-IN : STU	* SOCKET(HDPE/PVC) : SC	* SADDLE(HDPE) : SD	* FLANGE : F/F1	* GASKET : G/G1/G2	* BOLT & NUT : B/B1	* BLIND FLANGE : FB/FB1	* GATE VA. : VG/VG1/VG2	* BALL VA. : VB/VB1/VB2/VB2LO	* BUTTERFLY VA. : VF/VF4	* CHECK VA. : VC/VC1/VC2/VC3/VC4/VC5/VC6/VC7					
* GLOBE VA. : VL/VL1/VL2	* DIAPHRAGM VA. : VD/VDLO	* DAMPER : VP	* QUICK COUPLING : SQC	* FLEXIBLE JOINT(STEEL) : FLXB	* FLEXIBLE JOINT(RUBBER) : FLXR	* FLEXIBLE JOINT(STEEL PTFE LINED) : FLXL	* FLEXIBLE HOSE : FLXH	* STEAM TRAP : ST	* SPRAY NOZZLE : SPN	* EMERGENCY SHOWER : SSH					
* STRAINER(Y-TYPE) : YSTR	* STRAINER(T-TYPE) : TSTR	* STRAINER(BUCKET-TYPE) : BSTR	* ANCHOR PLATE : STOP	* BIRD SCREEN : BS	* ISOLATION KIT : IK	* UNLOADING BOX : UB	* AIR TRAP : AT	* LOTO : LOTO	* SIGHT GLASS : SG	* PRESSURE GAUGE : PG	* SHILED : SH	* SPECIAL BOLT & NUT : BL/BL1			

CLIENT		1	
			
CONTRACTOR		PROJECT NAME	
		M15X Ph4 Project	
COMMODITY		JOB NO.	
CPOL		22330D	
LINE NO.		SH'T NO.	REV.
65A-CPOL-ST3-N-6513		01 / 01	0