

DRAWING LIST FOR TEST PACKAGE

PROJECT NO.: 22328D


PROJECT TITLE : M15X Ph2 Project

GLU-520

No	PKG No	UNIT	LINE NUMBER			P&ID		REMARK
			ISO DRAWING No	SHEET	REV	P&ID No	REV	
1	520	4FA	40A-GLU-ST3-N-6508-01	1 OF 1	0	CJ-M15W14-PR-A20-000153	2A	
2	520	4FA	40A-GLU-ST3-N-6509-01	1 OF 1	0	CJ-M15W14-PR-A20-000153	2A	
3	520	4FA	40A-GLU-ST3-N-6510-01	1 OF 1	0	CJ-M15W14-PR-A20-000153	2A	
4	520	4FA	40A-GLU-ST3-N-6511-01	1 OF 1	0	CJ-M15W14-PR-A20-000153	2A	
5	520	4FA	40A-GLU-ST3-N-6512-01	1 OF 1	0	CJ-M15W14-PR-A20-000153	2A	
6	520	4FA	40A-GLU-ST3-N-6513-01	1 OF 1	0	CJ-M15W14-PR-A20-000153	2A	
7	520	4FA	50A-GLU-ST3-N-6505-01	1 OF 1	0	CJ-M15W14-PR-A20-000153	2A	
8	520	4FA	50A-GLU-ST3-N-6506-01	1 OF 1	0	CJ-M15W14-PR-A20-000153	2A	
9	520	4FA	50A-GLU-ST3-N-6507-01	1 OF 1	0	CJ-M15W14-PR-A20-000153	2A	

ITEM NO.	W14-T-GLU-4606 A/B		
SERVICE	GLUCOSE STORAGE TANK		
Q'TY	2		
TYPE	VERTICAL & CYLINDRICAL		
SIZE	ID x H	3.6 x 4.5 (EH/4.2)	
CAPA.	m3	46 (EH/43)	
MAT'L		STS304	


대외비

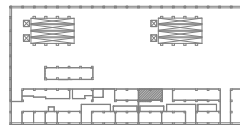

KEY PLAN (4F)

NOTE

- DIAPHRAGM PUMP
MAT'L 표기 : HEAD/DIAPHRAGM/CHECK BALL
약품종류에 따라 LINE 색상을 구분하여야 한다.
- CHEMICAL UNLOADING STATION에서 LEVEL을 볼 수 있도록 한다.
- CHEMICAL STORAGE TANK CURB 및 PUMP AREA에서 발생되는 DRAIN은 인근의 TRENCH로 접속되어, DRAIN HEADER로 이송된다.
- TANK의 역면 레벨 개이치는 VENDOR에서 공급한다.
- INTERLOCK NO. I-4617
(W14-CDP-GLU-4641A~C, 4642 A~C AUTO STOP)
: REMOTE STATUS에서 W14-T-GLU-4606 A/B LEVEL (LI-W6064 A/B) LOW LOW STOP.
- INTERLOCK NO. I-4659
(W13-CTP-GLU-4675 AUTO STOP)
: REMOTE STATUS에서 W14-T-GLU-4606 A/B LEVEL (LI-W6063 A/B) HIGH HIGH STOP.
- PUMP VENDOR 공급.
- 운전 시 CLOSE 되는 배관에는 LOTO 설치.
- STRAINER : Y TYPE (6~8 MESH).
- FIC-W2253, W2263 등 선택운전.
- OPERATING CAPACITY : 13 LPM
OPERATING PRESSURE : 0.25 MPa

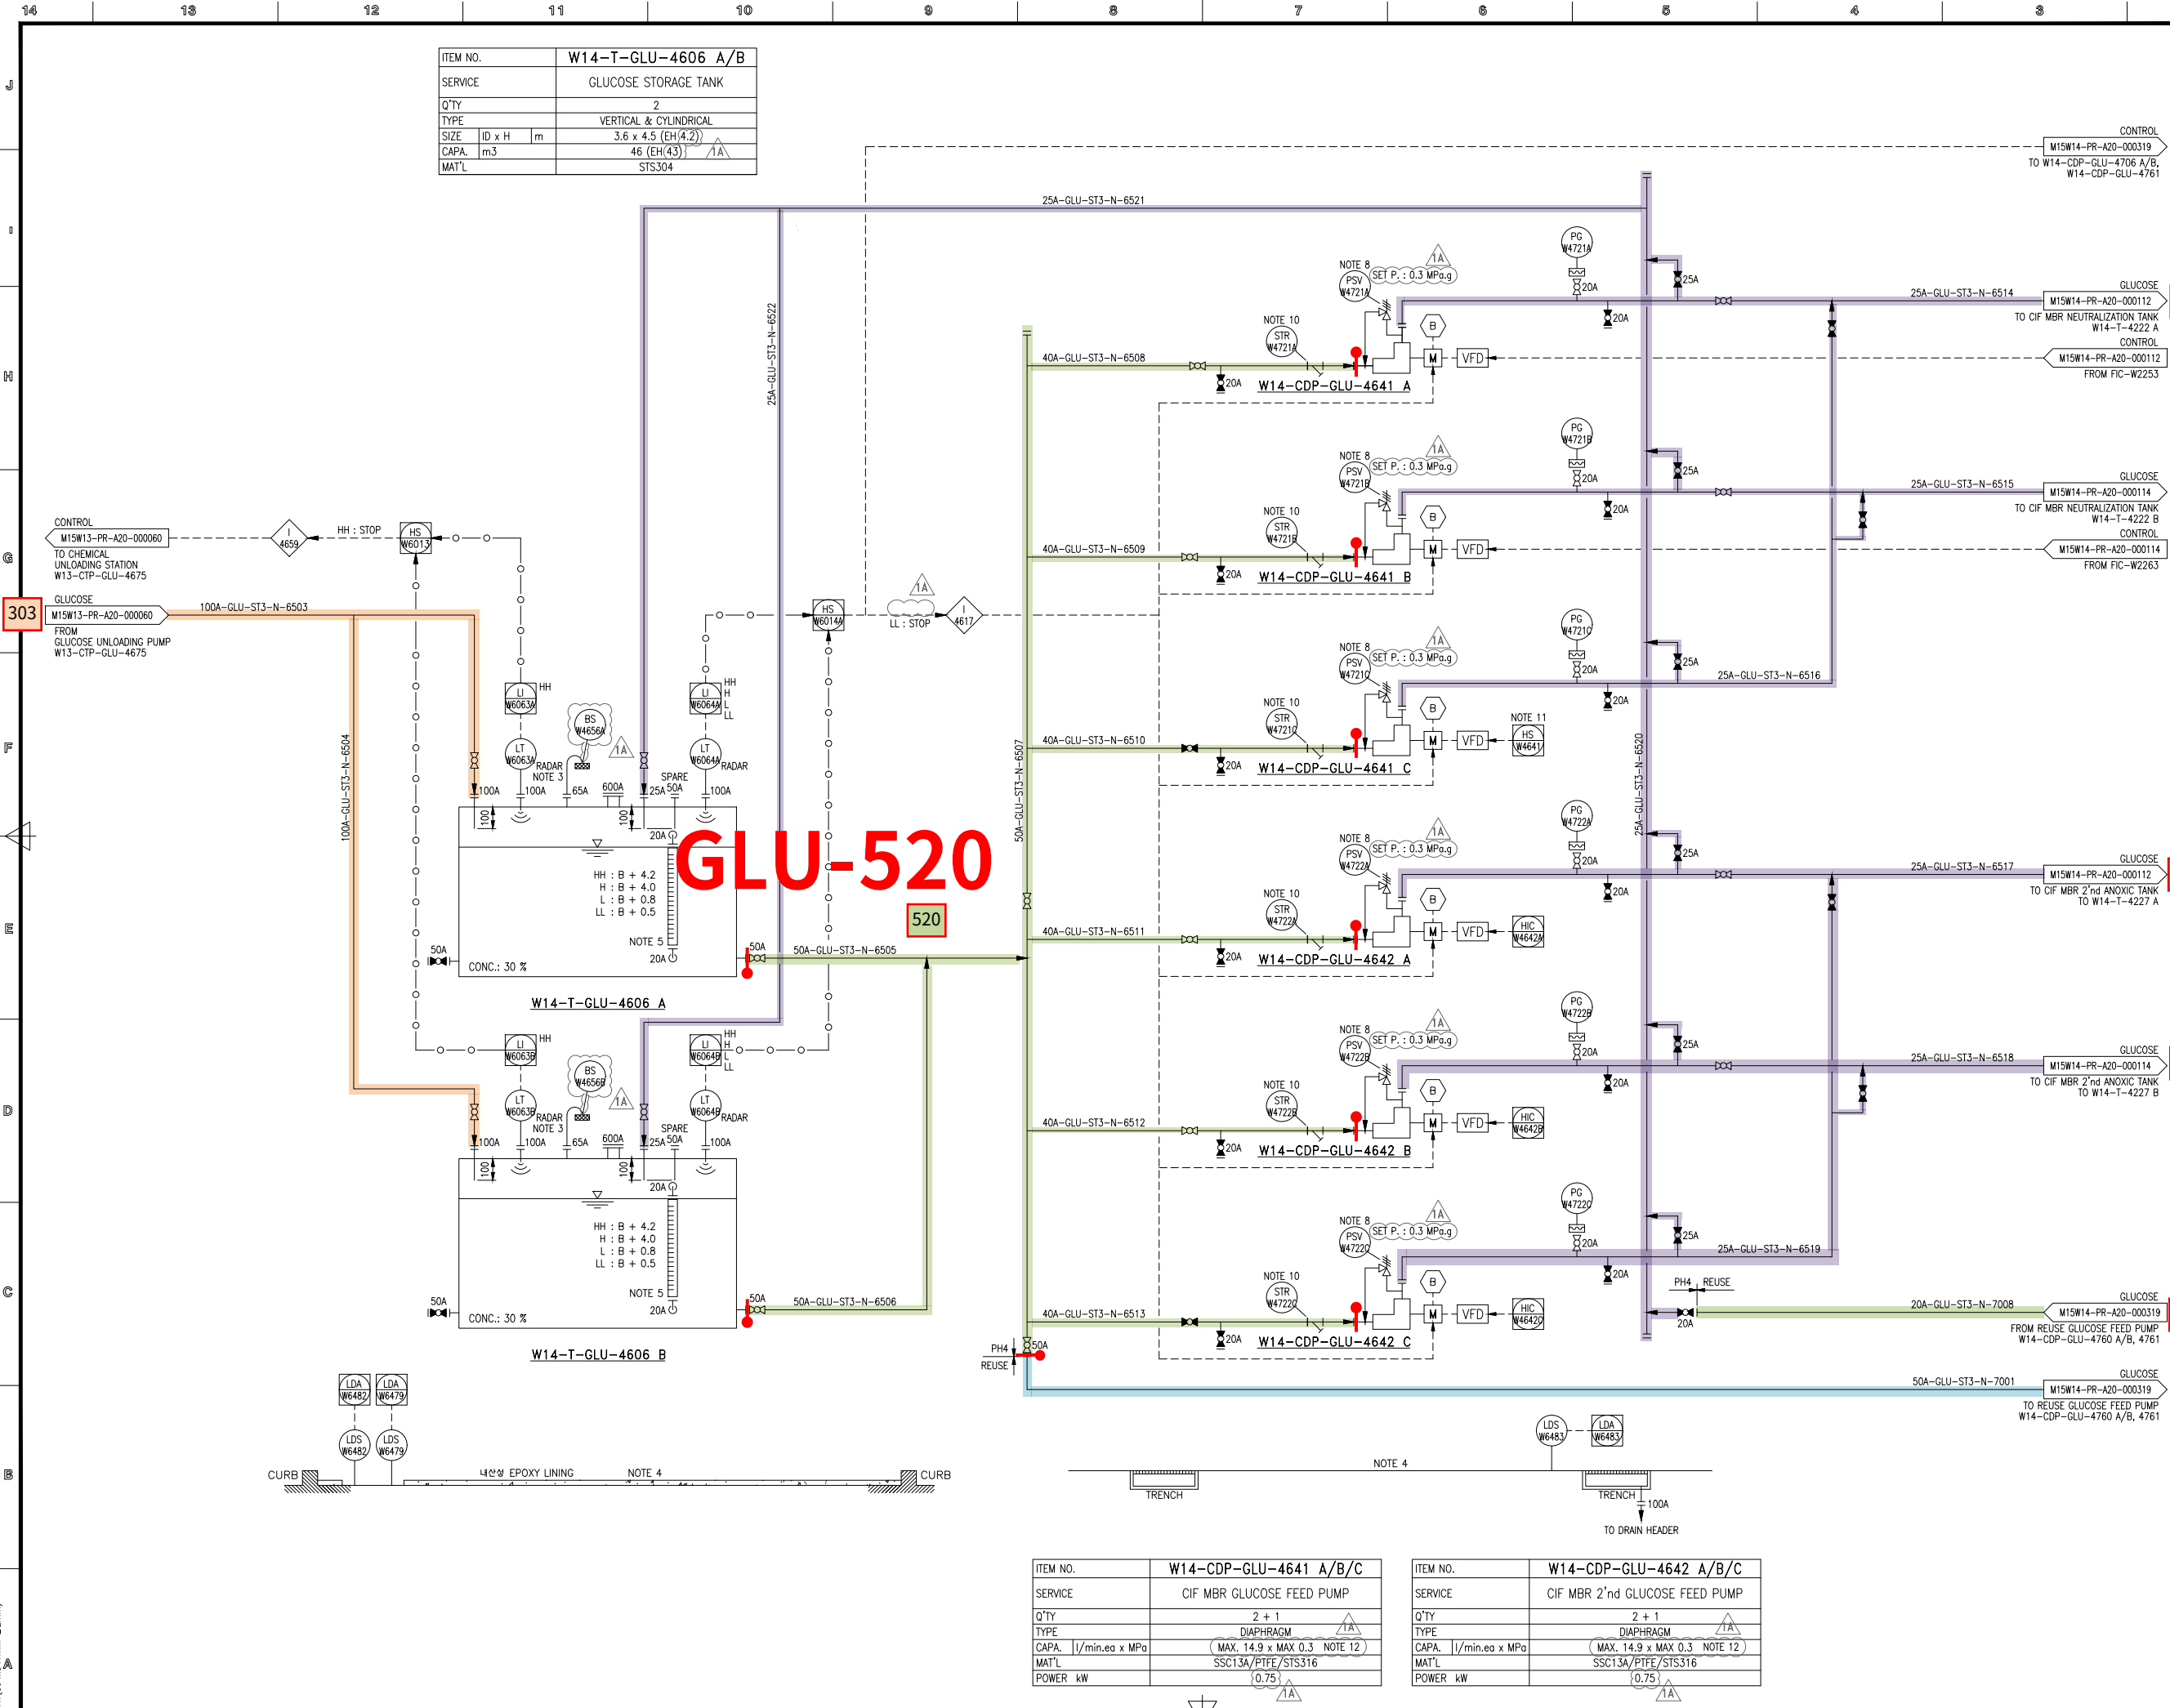

ITEM NO.	W14-CDP-GLU-4641 A/B/C		
SERVICE	CIF MBR GLUCOSE FEED PUMP		
Q'TY	2 + 1		
TYPE	DIAPHRAGM		
CAPA.	l/min.ea x MPa	MAX. 14.9 x MAX 0.3 NOTE 12	
MAT'L		SSC13A/PTFE/STS316	
POWER kW		(0.75)	

ITEM NO.	W14-CDP-GLU-4642 A/B/C		
SERVICE	CIF MBR 2'nd GLUCOSE FEED PUMP		
Q'TY	2 + 1		
TYPE	DIAPHRAGM		
CAPA.	l/min.ea x MPa	MAX. 14.9 x MAX 0.3 NOTE 12	
MAT'L		SSC13A/PTFE/STS316	
POWER kW		(0.75)	

2A	REVISED AFC	25.08.14
2	REVISED AFC	25.01.17
1	REVISED AFC	24.10.31
수정 REV.	실명 DESCRIPTION	날짜 DATE

제 DRAWN BY	이인학
검 CHECKED BY	한진희
인 PROVED BY	박동명
제 작 사	

SK 에코플랜트

사명
PROJECT TITLE
M15X Ph4 WWT Project

도면명
DWG. TITLE
PIPING & INSTRUMENT DIAGRAM
GLUCOSE STORAGE TANK
& FEED PUMP

속
SCALE
NONE

날
DATE
2025. 08. 14

PROJECT NO.	22330D	REV.	A
도면번호 SHEET NO.	CJ-M15W14-PR-A20-000153	2A	


[illegible]


<NOTE>
1. (*) FIELD ADJUST

* PIPE : P/P1	* 90° ELBOW : E90	* 45° ELBOW : E45	* TEE : T	* RED.TEE : TR	* STUB-IN : STU	* REINFORCING PAD : RP	* CON.RED : RC	* ECC.RED : RE	* CON.SWAGE : RCS/RCS1	* ECC.SWAGE : RES/RES1	* NIPPLE : NP/NP1/NP2	* CAP : CAP/CAP1	* PLUG : PLG	* FULL COUPLING : FC	* HALF COUPLING : HF/HF1
* STUB-IN : STU	* SOCKET(HDPE/PVC) : SC	* SADDLE(HDPE) : SD	* FLANGE : F/F1	* GASKET : G/G1/G2	* BOLT & NUT : B/B1	* BLIND FLANGE : FB/FB1	* GATE VA. : VG/VG1/VG2	* BALL VA. : VB/VBLO/VB1/VB1LO/VB2/VB2LO	* BUTTERFLY VA. : VF/VF4	* CHECK VA. : VC/VC1/VC2/VC3/VC4/VC5/VC6/VC7					
* GLOBE VA. : VL/VL1/VL2	* DIAPHRAGM VA. : VD/VDLO	* DAMPER : VP	* QUICK COUPLING : SQC	* FLEXIBLE JOINT(STEEL) : FLXB	* FLEXIBLE JOINT(RUBBER) : FLXR	* FLEXIBLE JOINT(STEEL PTFE LINED) : FLXL	* FLEXIBLE HOSE : FLXH	* STEAM TRAP : ST	* SPRAY NOZZLE : SPN	* EMERGENCY SHOWER : SSH					
* STRAINER(Y-TYPE) : YSTR	* STRAINER(T-TYPE) : TSTR	* STRAINER(BUCKET-TYPE) : BSTR	* ANCHOR PLATE : STOP	* BIRD SCREEN : BS	* ISOLATION KIT : IK	* UNLOADING BOX : UB	* AIR TRAP : AT	* LOTO : LOTO	* SIGHT GLASS : SG	* PRESSURE GAUGE : PG	* SHILED : SH	* SPECIAL BOLT & NUT : BL/BL1			


INSULATION	CODE	N	CONDITION	PRESS. (kg/cm2g)	TEMP. (°C)	AREA	W14							CONTRACTOR	PROJECT NAME		
	THICK.	—	DESIGN	1	60	UNIT	4FA								M15X Ph4 Project		
			OPERATING	ATM	AMB	REF. PLAN DWG.	CJ-M15W14-PI-A30-040012-A							COMMODITY	GLU	JOB NO.	
						REF. P & ID	CJ-M15W14-PR-A20-000153		25.01.24	APPROVED FOR CONSTRUCTION	황래중	안남후	박동영	LINE NO.	50A-GLU-ST3-N-6505	SH'T NO. 01 / 01	REV. 0
								REV. NO.	DATE	DESCRIPTION	BY	CHK	APP'D				

경고: 본 문서는 SK HYNIX의 기밀비밀 자료로서, 어떠한 경우에도 무단 사용, 복제, 제3자에게 공개, 누설, 변조, 유통, 기타 무단 사용, 또는 기타 행위를 금지합니다. 무단 사용, 또는 기타 행위를 한 자에 대해서는 법적 조치를 취할 수 있습니다. 본 문서는 SK HYNIX의 기밀비밀 자료로서, 어떠한 경우에도 무단 사용, 복제, 제3자에게 공개, 누설, 변조, 유통, 기타 무단 사용, 또는 기타 행위를 금지합니다. 무단 사용, 또는 기타 행위를 한 자에 대해서는 법적 조치를 취할 수 있습니다.

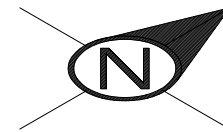

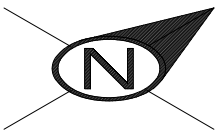

ITEM	SIZE	Q'TY	DESCRIPTION
ST3			
P	50A	3.4M	PIPE, STS 304TP, ERW, BE - SCH 10S
T	50A	1EA	TEE EQUAL, STS304, ERW, BE - SCH 10S
TR	50Ax40A	6EA	TEE RED, STSF304, SW - SCH 10S
VB	50A	2EA	BALL VALVE, KS 10K, RF FLG'D, BODY-SSC13 /
			TRIM-ST304 / SEAT-PTFE, FB, LEVER
F	50A	4EA	FLG SO, KS 10K, RF, STS304
FB	50A	1EA	FLG BLIND, KS 10K, RF, STS304
G	50A	4EA	GASKET, KS 10K, RF, PTFE+EPDM, 3.0MM TH'K
B	50A	4SET	MACHINE BOLT & NUTS :STS 304 / W WASHERS

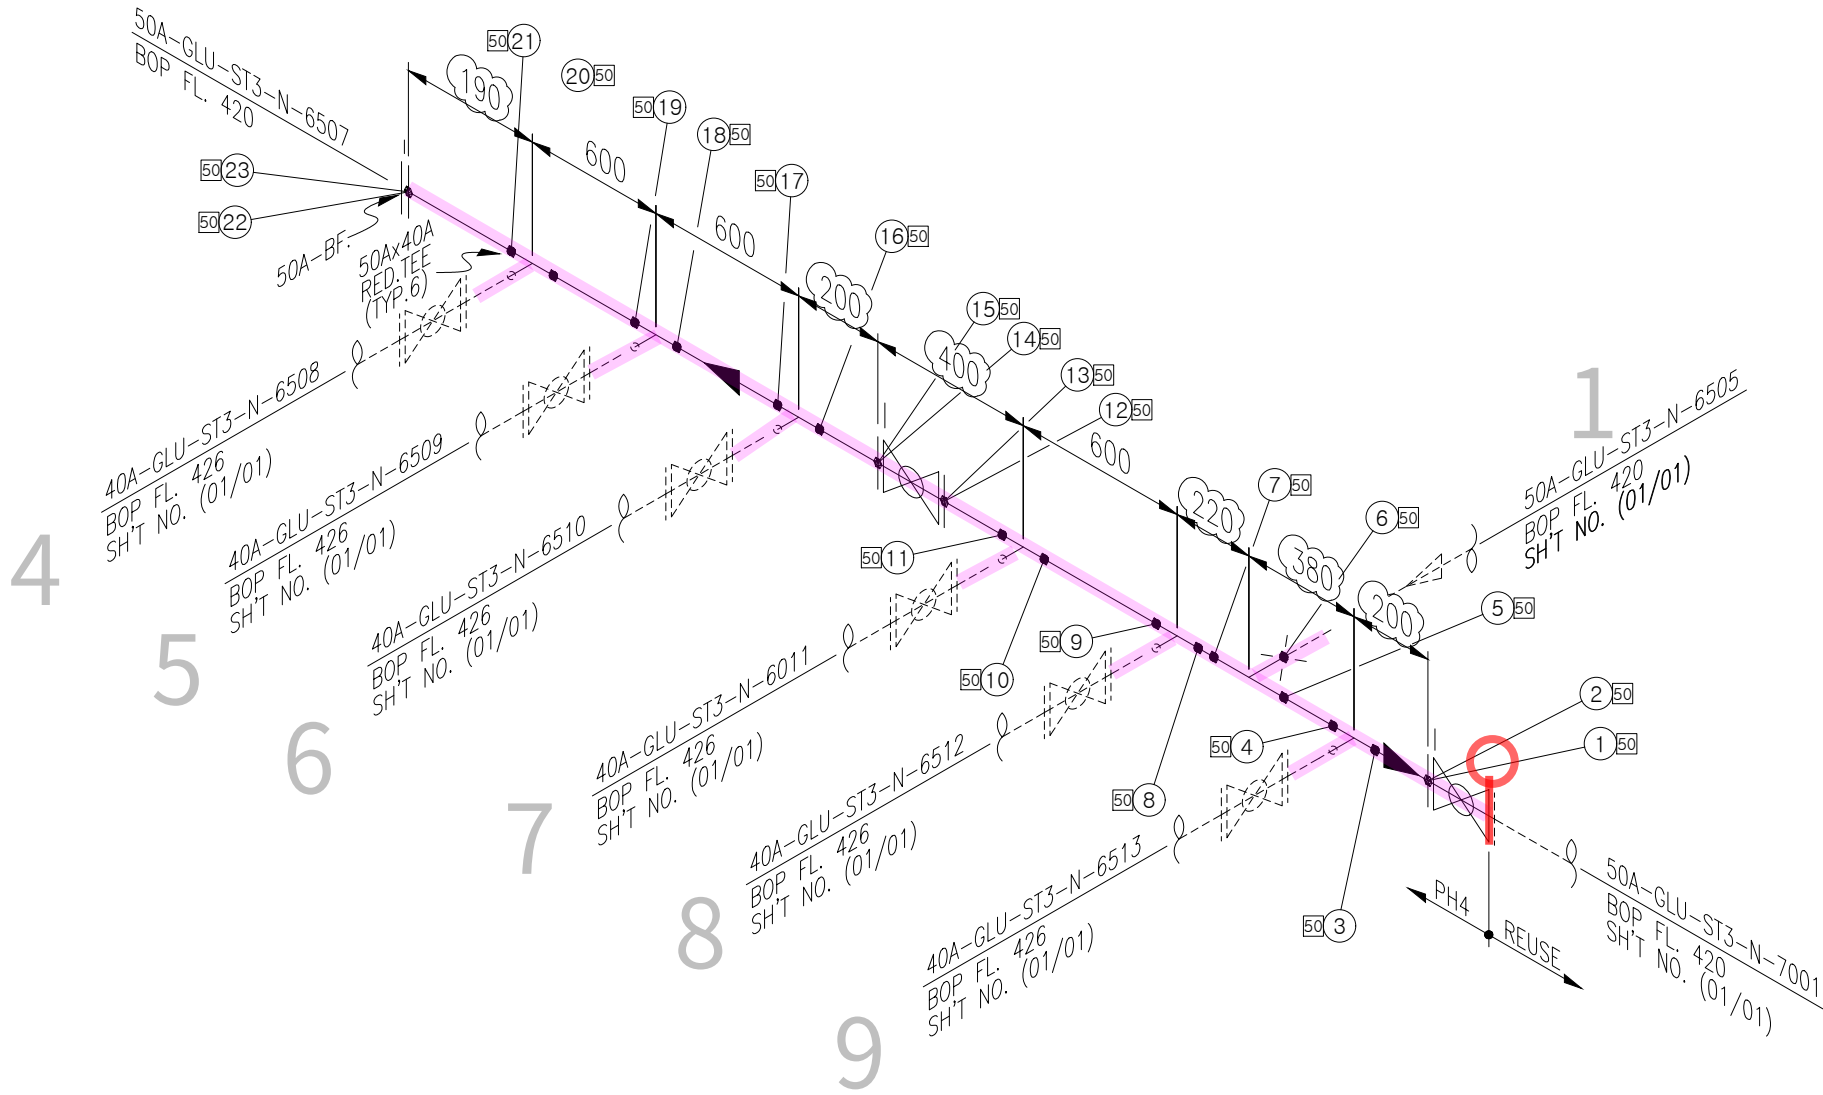

<NOTE>
1. (*) FIELD ADJUST

* PIPE : P/P1 * 90° ELBOW : E90 * 45° ELBOW : E45 * TEE : T * RED.TEE : TR * STUB-IN : STU * REINFORCING PAD : RP * CON.RED : RC * ECC.RED : RE * CON.SWAGE : RCS/RCS1 * ECC.SWAGE : RES/RES1 * NIPPLE : NP/NP1/NP2 * CAP : CAP/CAP1 * PLUG : PLG * FULL COUPLING : FC * HALF COUPLING : HF/HF1
* STUB-IN : STU * SOCKET(HDPE/PVC) : SC * SADDLE(HDPE) : SD * FLANGE : F/F1 * GASKET : G/G1/G2 * BOLT & NUT : B/B1 * BLIND FLANGE : FB/FB1 * GATE VA. : VG/VG1/VG2 * BALL VA. : VB/VBLO/VB1/VB1LO/VB2/VB2LO * BUTTERFLY VA. : VF/VF4 * CHECK VA. : VC/VC1/VC2/VC3/VC4/VC5/VC6/VC7
* GLOBE VA. : VL/VL1/VL2 * DIAPHRAGM VA. : VD/VDLO * DAMPER : VP * QUICK COUPLING : SQC * FLEXIBLE JOINT(STEEL) : FLXB * FLEXIBLE JOINT(RUBBER) : FLXR * FLEXIBLE JOINT(STEEL PTFE LINED) : FLXL * FLEXIBLE HOSE : FLXH * STEAM TRAP : ST * SPRAY NOZZLE : SPN * EMERGENCY SHOWER : SSH
* STRAINER(Y-TYPE) : YSTR * STRAINER(T-TYPE) : TSTR * STRAINER(BUCKET-TYPE) : BSTR * ANCHOR PLATE : STOP * BIRD SCREEN : BS * ISOLATION KIT : IK * UNLOADING BOX : UB * AIR TRAP : AT * LOTO : LOTO * SIGHT GLASS : SG * PRESSURE GAUGE : PG * SHILED : SH * SPECIAL BOLT & NUT : BL/BL1

CLIENT



3

CONTRACTOR



PROJECT NAME

M15X Ph4 Project

COMMODITY

GLU

JOB NO.

22330D

LINE NO.


50A-GLU-ST3-N-6507

SH'T NO.

REV.

01 / 01

0

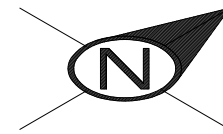


1. TRAY & ANGLE, CHANNEL SUPPORT가 적용되는 배관 ELEVATION은 현장 맞춤으로 한다.
2. (*) FIELD ADJUST

* PIPE : P/P1	* 90° ELBOW : E90	* 45° ELBOW : E45	* TEE : T	* RED.TEE : TR	* STUB-IN : STU	* REINFORCING PAD : RP	* CON.RED : RC	* ECC.RED : RE	* CON.SWAGE : RCS/RCS1	* ECC.SWAGE : RES/RES1	* NIPPLE : NP/NP1/NP2	* CAP : CAP/CAP1	* PLUG : PLG	* FULL COUPLING : FC	* HALF COUPLING : HF/HF1
* STUB-IN : STU	* SOCKET(HDPE/PVC) : SC	* SADDLE(HDPE) : SD	* FLANGE : F/F1	* GASKET : G/G1/G2	* BOLT & NUT : B/B1	* BLIND FLANGE : FB/FB1	* GATE VA. : VG/VG1/VG2	* BALL VA. : VB/VBLO/VB1/VB1LO/VB2/VB2LO	* BUTTERFLY VA. : VF/VF4	* CHECK VA. : VC/VC1/VC2/VC3/VC4/VC5/VC6/VC7					
* GLOBE VA. : VL/VL1/VL2	* DIAPHRAGM VA. : VD/VDLO	* DAMPER : VP	* QUICK COUPLING : SQC	* FLEXIBLE JOINT(STEEL) : FLXB	* FLEXIBLE JOINT(RUBBER) : FLXR	* FLEXIBLE JOINT(STEEL PTFE LINED) : FLXL	* FLEXIBLE HOSE : FLXH	* STEAM TRAP : ST	* SPRAY NOZZLE : SPN	* EMERGENCY SHOWER : SSH					
* STRAINER(Y-TYPE) : YSTR	* STRAINER(T-TYPE) : TSTR	* STRAINER(BUCKET-TYPE) : BSTR	* ANCHOR PLATE : STOP	* BIRD SCREEN : BS	* ISOLATION KIT : IK	* UNLOADING BOX : UB	* AIR TRAP : AT	* LOTO : LOTO	* SIGHT GLASS : SG	* PRESSURE GAUGE : PG	* SHILED : SH	* SPECIAL BOLT & NUT : BL/BL1			

INSULATION	CODE	N	CONDITION	PRESS. (kg/cm2g)	TEMP. (°C)	AREA W14						CONTRACTOR	PROJECT NAME		
	THICK.	-	DESIGN	1	60	UNIT 4FA							M15X Ph4 Project		
			OPERATING	ATM	AMB	REF. PLAN DWG. CJ-M15W14-PI-A30-040012-A						COMMODITY	JOB NO.		
						REF. P & ID CJ-M15W14-PR-A20-000153		25.01.24	APPROVED FOR CONSTRUCTION	황래중	안남후	박동영	22330D		
							REV. NO.	DATE	DESCRIPTION	BY	CHK	APP'D	LINE NO.	SH'T NO.	REV.
													40A-GLU-ST3-N-6510	01 / 01	0

경고 : 본 도면은 SK HYNIX의 기밀비밀 자료로서, 어떠한 경우에도 목적 외 사용, 복제, 제3자에게 공개, 누설 및 유출할 수 없으며, 회사는 유포자의 불법 사용으로 피해가 발생할 경우 유포자에게 민/형사상 책임을 요구할 수 있음

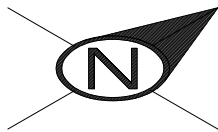

1. TRAY & ANGLE, CHANNEL SUPPORT가 적용되는 배관 ELEVATION은 현장 맞춤으로 한다.
2. (*) FIELD ADJUST

CLIENT

9

CONTRACTOR

PROJECT NAME
M15X Ph4 Project

COMMODITY

GU

LINE NO.

40A-GLU-ST3-N-6513

SH'T NO.

01 / 01	C
---------	---