

DRAWING LIST FOR TEST PACKAGE

GLU-522


PROJECT NO.: 22328D

PROJECT TITLE : M15X Ph2 Project

No	PKG No	UNIT	LINE NUMBER			P&ID		REMARK
			ISO DRAWING No	SHEET	REV	P&ID No	REV	
1	522	4FA	20A-GLU-ST3-N-7002-01	1 OF 1	0	CJ-M15W14-PR-A20-000319	1A	
2	522	4FA	20A-GLU-ST3-N-7003-01	1 OF 1	0	CJ-M15W14-PR-A20-000319	1A	
3	522	4FA	20A-GLU-ST3-N-7004-01	1 OF 1	0	CJ-M15W14-PR-A20-000319	1A	
4	522	4FA	50A-GLU-ST3-N-7001-01	1 OF 1	0	CJ-M15W14-PR-A20-000153	1A	

ITEM NO.	W14-T-GLU-4606 A/B	
SERVICE	GLUCOSE STORAGE TANK	
Q'TY	2	
TYPE	VERTICAL & CYLINDRICAL	
SIZE	ID x H	3.6 x 4.5 (EH(4.2))
CAPA.	m3	46 (EH(43))
MAT'L		STS304

대외비

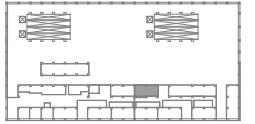

KEY PLAN (4F)

- NOTE
- 521

DIAPHRAGM PUMP
MAT'L 표기 : HEAD/DIAPHRAGM/CHECK BALL
약품종류에 따라 LINE 색상을 구분하여야 한다.
3. CHEMICAL UNLOADING STATION에서 LEVEL을 볼 수 있도록 한다.
4. CHEMICAL STORAGE TANK CURB 및 PUMP AREA에서 발생되는 DRAIN은 인근의 TRENCH로 접속되어, DRAIN HEADER로 이송된다.
5. TANK의 역면 레벨 게이지는 VENDOR에서 공급한다.
6. INTERLOCK NO. I-4617
(W14-CDP-GLU-4641A~C, 4642 A~C AUTO STOP)
: REMOTE STATUS에서 W14-T-GLU-4606 A/B LEVEL (LI-W6064 A/B) LOW LOW STOP.
- 521
- INTERLOCK NO. I-4659
(W13-CTP-GLU-4675 AUTO STOP)
: REMOTE STATUS에서 W14-T-GLU-4606 A/B LEVEL (LI-W6063 A/B) HIGH HIGH STOP.
8. PUMP VENDOR 공급.
9. 운전 시 CLOSE 되는 배관에는 LOTO 설치.
10. STRAINER : Y TYPE (6~8 MESH).
11. FIC-W2253, W2263 등 선택운전.
12. OPERATING CAPACITY : 13 LPM
OPERATING PRESSURE : 0.25 MPa

2A	REVISED AFC	25.08.14
2	REVISED AFC	25.01.17
1	REVISED AFC	24.10.31
수정 REV.	설명 DESCRIPTION	날짜 DATE
제 DRAWN BY	이인학	
검 CHECKED BY	한진희	
인 PROVED BY	박동명	
제 작 사		

SK 에코플랜트

사명
PROJECT TITLE

M15X Ph4 WWT Project

도면명
DWG. TITLE

PIPING & INSTRUMENT DIAGRAM
GLUCOSE STORAGE TANK
& FEED PUMP

속
척

SCALE

NONE

날
짜

DATE

2025. 08. 14

PROJECT NO.

22330D

REV.

A

도면번호
SHEET NO.

CJ-M15W14-PR-A20-000153

2A

GLU-522


ITEM NO.	W14-CDP-GLU-4641 A/B/C
SERVICE	CIF MBR GLUCOSE FEED PUMP
Q'TY	2 + 1
TYPE	DIAPHRAGM
CAPA.	1/min.ea x MPa MAX. 14.9 x MAX 0.3 NOTE 12
MAT'L	SSC13A/PTFE/STS316
POWER kW	(0.75)

ITEM NO.	W14-CDP-GLU-4642 A/B/C
SERVICE	CIF MBR 2'nd GLUCOSE FEED PUMP
Q'TY	2 + 1
TYPE	DIAPHRAGM
CAPA.	1/min.ea x MPa MAX. 14.9 x MAX 0.3 NOTE 12
MAT'L	SSC13A/PTFE/STS316
POWER kW	(0.75)





ITEM	SIZE	Q'TY	DESCRIPTION
ST3			
P	20A	0.8M	PIPE, STS 304TP, ERW, PE – SCH 10S
T	20A	1EA	TEE, STSF304, SW – SCH 10S
VB	20A	2EA	BALL VALVE, KS 10K, RF FLC'D, BODY–STSF304 /
F	20A	6EA	FRGMSGJES040K, SET STSF304 FB, LEVER
FB	20A	1EA	FLG BLIND, KS 10K, RF, STSF304
G	20A	7EA	GASKET, KS 10K, RF, PTFE+EPDM, 3.0MM TH'K
B	20A	7SET	MACHINE BOLT & NUTS :STS 304 / W WASHERS
YSTR	20A	1EA	Y–STRAINER
RES	20Ax15A	1EA	SWAGE ECC, STSF304, PBE – SCH 10S

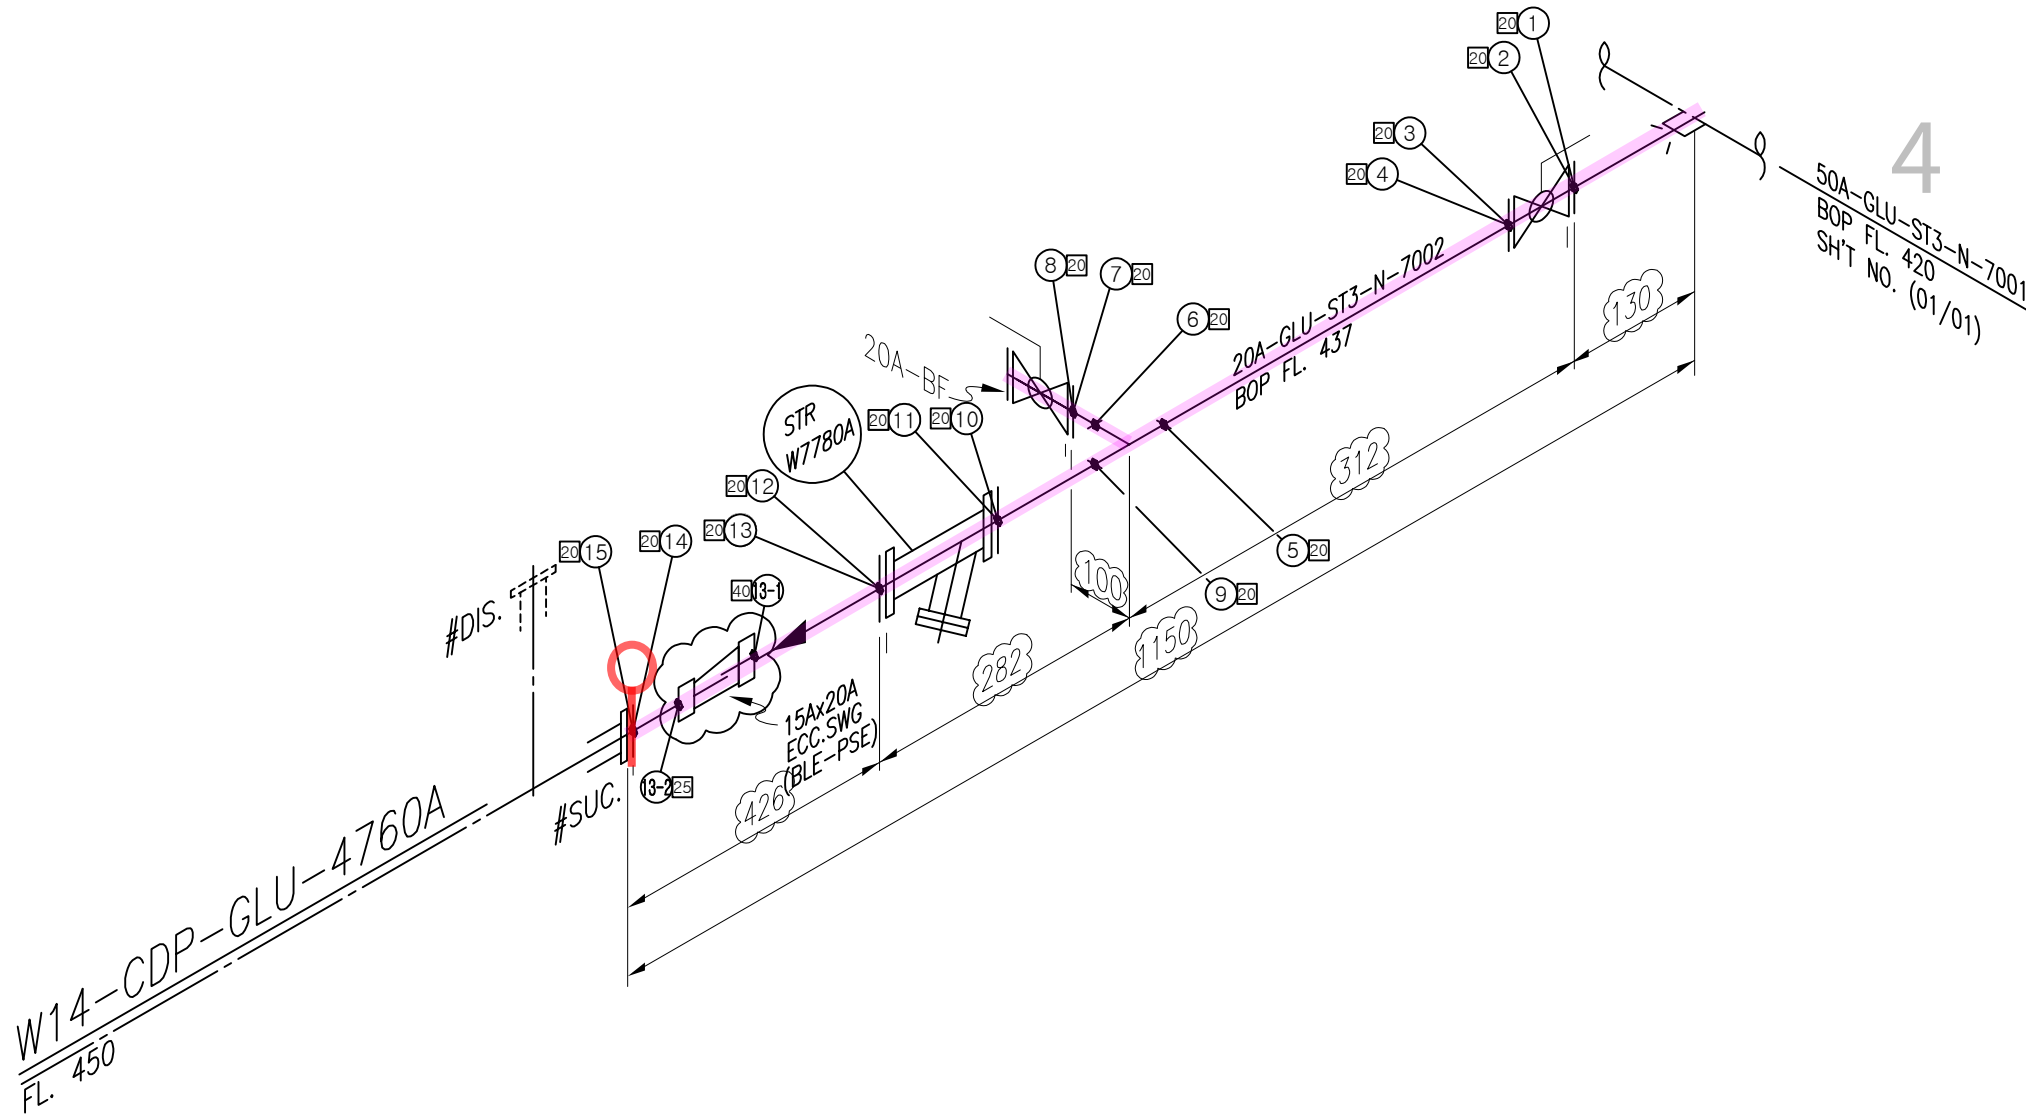



<NOTE>
1. (*) FIELD ADJUST

* PIPE : P/P1	* 90° ELBOW : E90	* 45° ELBOW : E45	* TEE : T	* RED.TEE : TR	* STUB-IN : STU	* REINFORCING PAD : RP	* CON.RED : RC	* ECC.RED : RE	* CON.SWAGE : RCS/RCS1	* ECC.SWAGE : RES/RES1	* NIPPLE : NP/NP1/NP2	* CAP : CAP/CAP1	* PLUG : PLG	* FULL COUPLING : FC	* HALF COUPLING : HF/HF1
* STUB-IN : STU	* SOCKET(HDPE/PVC) : SC	* SADDLE(HDPE) : SD	* FLANGE : F/F1	* GASKET : G/G1/G2	* BOLT & NUT : B/B1	* BLIND FLANGE : FB/FB1	* GATE VA. : VG/VG1/VG2	* BALL VA. : VB/VB1/VB2/VB2L0	* BUTTERFLY VA. : VF/VF4	* CHECK VA. : VC/VC1/VC2/VC3/VC4/VC5/VC6/VC7					
* GLOBE VA. : VL/VL1/VL2	* DIAPHRAGM VA. : VD/VDL0	* DAMPER : VP	* QUICK COUPLING : SQC	* FLEXIBLE JOINT(STEEL) : FLXB	* FLEXIBLE JOINT(RUBBER) : FLXR	* FLEXIBLE JOINT(STEEL PTFE LINED) : FLXL	* FLEXIBLE HOSE : FLXH	* STEAM TRAP : ST	* SPRAY NOZZLE : SPN	* EMERGENCY SHOWER : SSH					
* STRAINER(Y-TYPE) : YSTR	* STRAINER(T-TYPE) : TSTR	* STRAINER(BUCKET-TYPE) : BSTR	* ANCHOR PLATE : STOP	* BIRD SCREEN : BS	* ISOLATION KIT : IK	* UNLOADING BOX : UB	* AIR TRAP : AT	* LOTO : LOTO	* SIGHT GLASS : SG	* PRESSURE GAUGE : PG	* SHILED : SH	* SPECIAL BOLT & NUT : BL/BL1			

INSULATION	CODE	N	CONDITION	PRESS. (kg/cm2g)	TEMP. (°C)	AREA	W14							CONTRACTOR	PROJECT NAME	
	THICK.	—	DESIGN	1	60	UNIT	4FA								M15X Ph4 Project	
			OPERATING	ATM	AMB	REF. PLAN DWG.								COMMODITY	JOB NO.	
						CJ-M15W14-PI-A30-040012-A			25.01.24	APPROVED FOR CONSTRUCTION	황래중	안남후	박동영		22330D	
						REF. P & ID		REV. NO.	DATE	DESCRIPTION	BY	CHK	APP'D	LINE NO.	SH'T NO.	REV.
						CJ-M15W14-PR-A20-000319								20A-GLU-ST3-N-7002	01 / 01	0

경고 : 본 도면은 SK HYNIX의 기밀비밀 자료로서, 어떠한 경우에도 목적 외 사용, 복제, 제3자에게 공개, 누설 및 유출할 수 없으며, 회사는 유도자의 불법 사용으로 피해가 발생할 경우 유도자에게 민/형사상 책임을 요구할 수 있음.

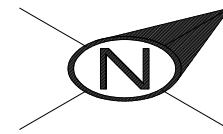

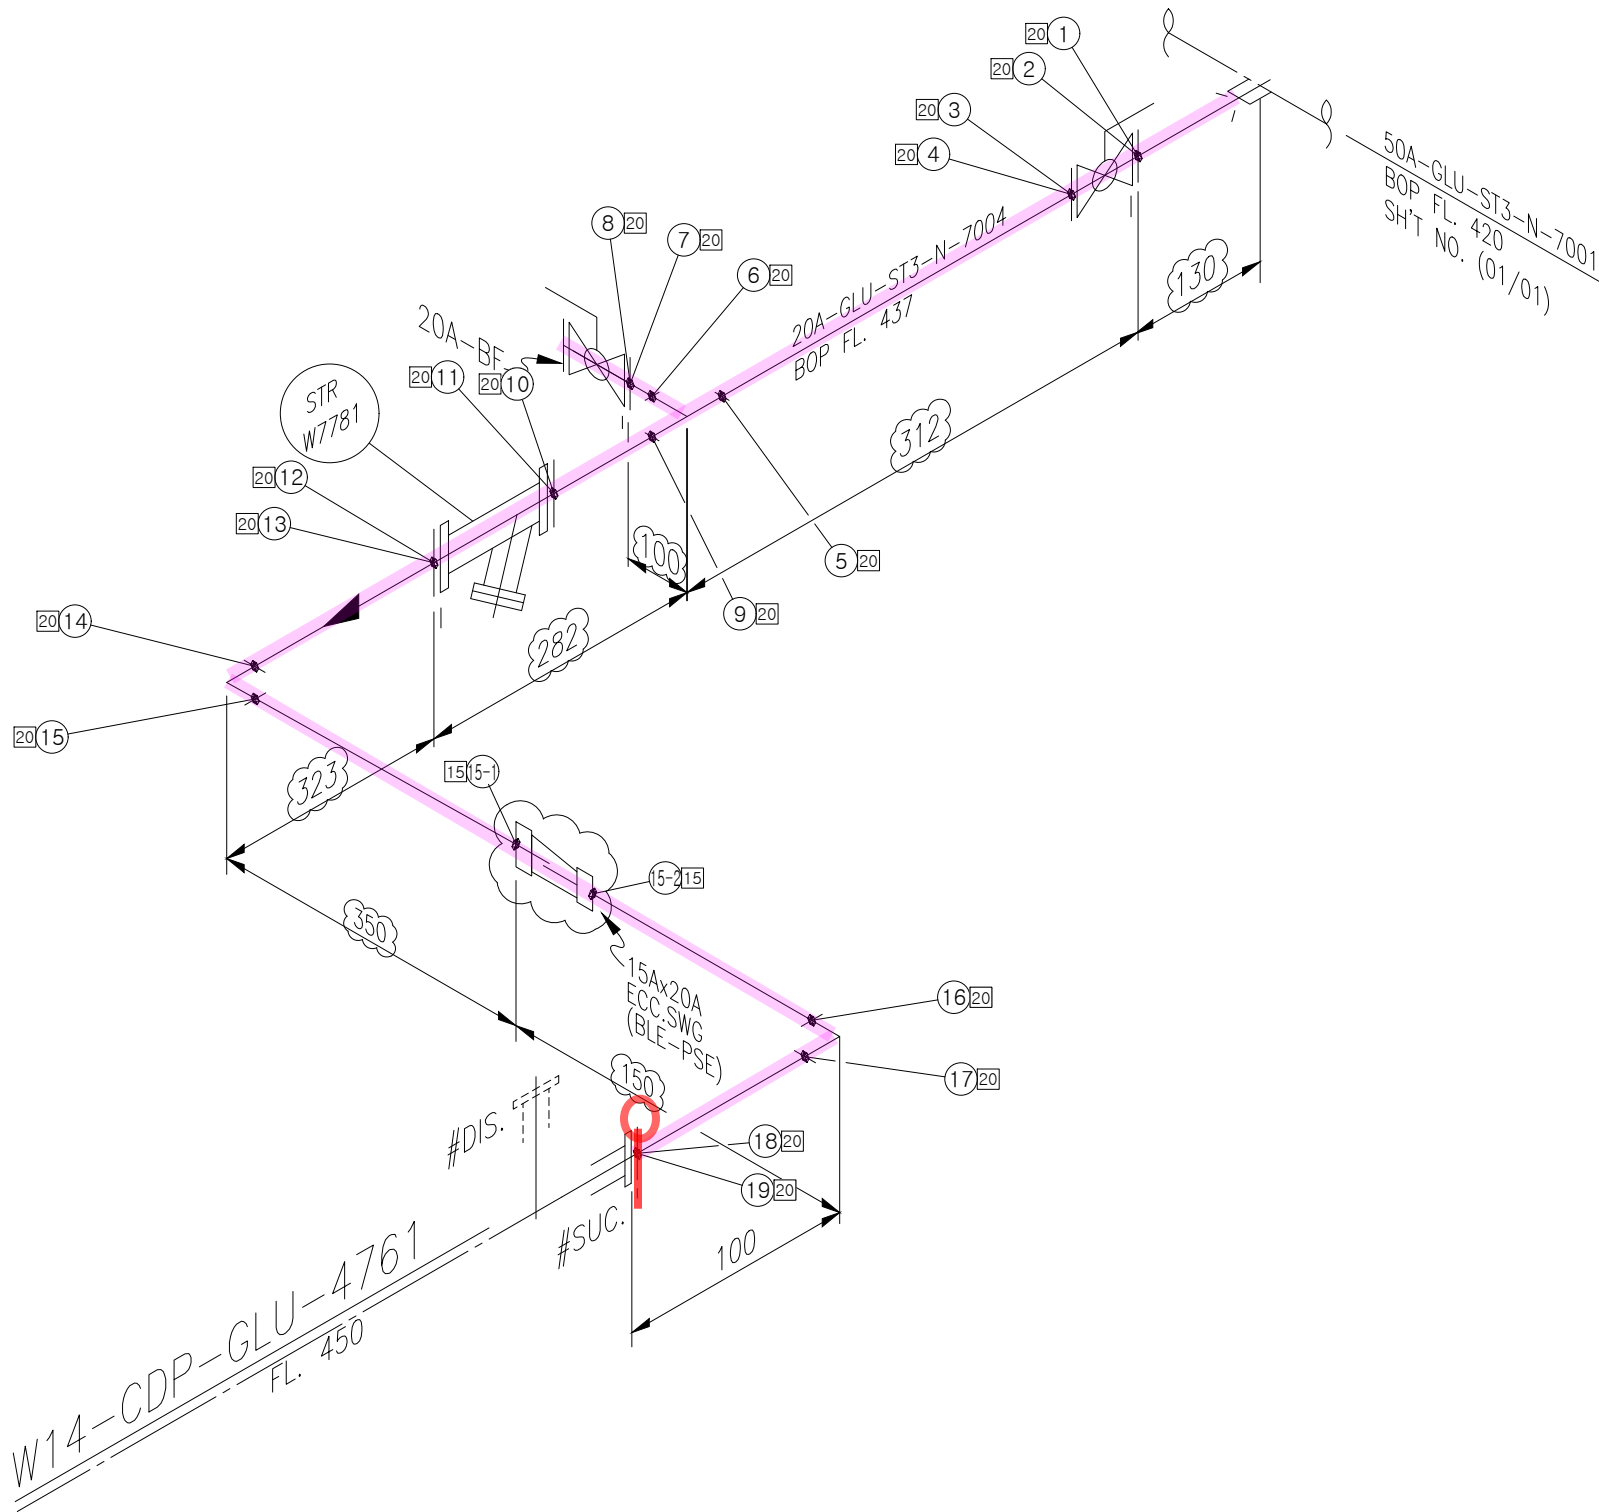

4

<NOTE>
1. (*) FIELD ADJUST



ITEM	SIZE	Q'TY	DESCRIPTION
ST3			
P	20A	1.3M	PIPE, STS 304TP, ERW, PE - SCH 10S
E90	20A	2EA	90ELBOW, STSF304, SW - SCH 10S
T	20A	1EA	TEE, STSF304, SW - SCH 10S
VB	20A	2EA	BALL VALVE, KS 10K, RF FLG'D, BODY-STSF304 /
F	20A	6EA	FLANGE, STSF304, RF, 150#
FB	20A	1EA	FLG BLIND, KS 10K, RF, STS304
G	20A	7EA	GASKET, KS 10K, RF, PTFE+EPDM, 3.0MM TH'K
B	20A	7SET	MACHINE BOLT & NUTS :STS 304 / W WASHERS
YSTR	20A	1EA	Y-STRAINER
RES	20Ax15A	1EA	SWAGE ECC, STSF304, PBE - SCH 10S

CLIENT



3

CONTRACTOR	PROJECT NAME
SK ecoplant	M15X Ph4 Project
COMMODITY	JOB NO.
GLU	22330D
LINE NO.	SH'T NO. REV.
20A-GLU-ST3-N-7004	01 / 01 0

* PIPE : P/P1 * 90° ELBOW : E90 * 45° ELBOW : E45 * TEE : T * RED.TEE : TR * STUB-IN : STU * REINFORCING PAD : RP * CON.RED : RC * ECC.RED : RE * CON.SWAGE : RCS/RCS1 * ECC.SWAGE : RES/RES1 * NIPPLE : NP/NP1/NP2 * CAP : CAP/CAP1 * PLUG : PLG * FULL COUPLING : FC * HALF COUPLING : HF/HF1
* STUB-IN : STU * SOCKET(HDPE/PVC) : SC * SADDLE(HDPE) : SD * FLANGE : F/F1 * GASKET : G/G1/G2 * BOLT & NUT : B/B1 * BLIND FLANGE : FB/FB1 * GATE VA. : VG/VG1/VG2 * BALL VA. : VB/VBLO/VB1/VB1LO/VB2/VB2LO * BUTTERFLY VA. : VF/VF4 * CHECK VA. : VC/VC1/VC2/VC3/VC4/VC5/VC6/VC7
* GLOBE VA. : VL/VL1/VL2 * DIAPHRAGM VA. : VD/VDLO * DAMPER : VP * QUICK COUPLING : SQC * FLEXIBLE JOINT(STEEL) : FLXB * FLEXIBLE JOINT(RUBBER) : FLXR * FLEXIBLE JOINT(STEEL PTFE LINED) : FLXL * FLEXIBLE HOSE : FLXH * STEAM TRAP : ST * SPRAY NOZZLE : SPN * EMERGENCY SHOWER : SSH
* STRAINER(Y-TYPE) : YSTR * STRAINER(T-TYPE) : TSTR * STRAINER(BUCKET-TYPE) : BSTR * ANCHOR PLATE : STOP * BIRD SCREEN : BS * ISOLATION KIT : IK * UNLOADING BOX : UB * AIR TRAP : AT * LOTO : LOTO * SIGHT GLASS : SG * PRESSURE GAUGE : PG * SHILED : SH * SPECIAL BOLT & NUT : BL/BL1

INSULATION	CODE	N	CONDITION	PRESS. (kg/cm2g)	TEMP. (°C)	AREA	W14							CONTRACTOR	PROJECT NAME
	THICK.	—	DESIGN	1	60	UNIT	4FA								M15X Ph4 Project
			OPERATING	ATM	AMB	REF. PLAN DWG.								COMMODITY	JOB NO.
						CJ-M15W14-PI-A30-040012-A			25.01.24	APPROVED FOR CONSTRUCTION	황래중	안남후	박동영		22330D
						REF. P & ID		REV. NO.	DATE	DESCRIPTION	BY	CHK	APP'D	LINE NO.	SH'T NO.
						CJ-M15W14-PR-A20-000319								20A-GLU-ST3-N-7004	01 / 01
															REV. 0

