


DRAWING LIST FOR TEST PACKAGE

PROJECT NO.: 22328D

PROJECT TITLE : M15X Ph2 Project

NaOH-527

No	PKG No	UNIT	LINE NUMBER			P&ID		REMARK
			ISO DRAWING No	SHEET	REV	P&ID No	REV	
1	527	3FA	OD25-NaOH-HP2-N-9901-01	1 OF 1	0	CJ-M15W13-PR-A20-000054, 601	2/0A	
2	527	4FA	OD25-NaOH-HP2-N-9901-01	1 OF 1	0	CJ-M15W13-PR-A20-000054, 601	2/0A	

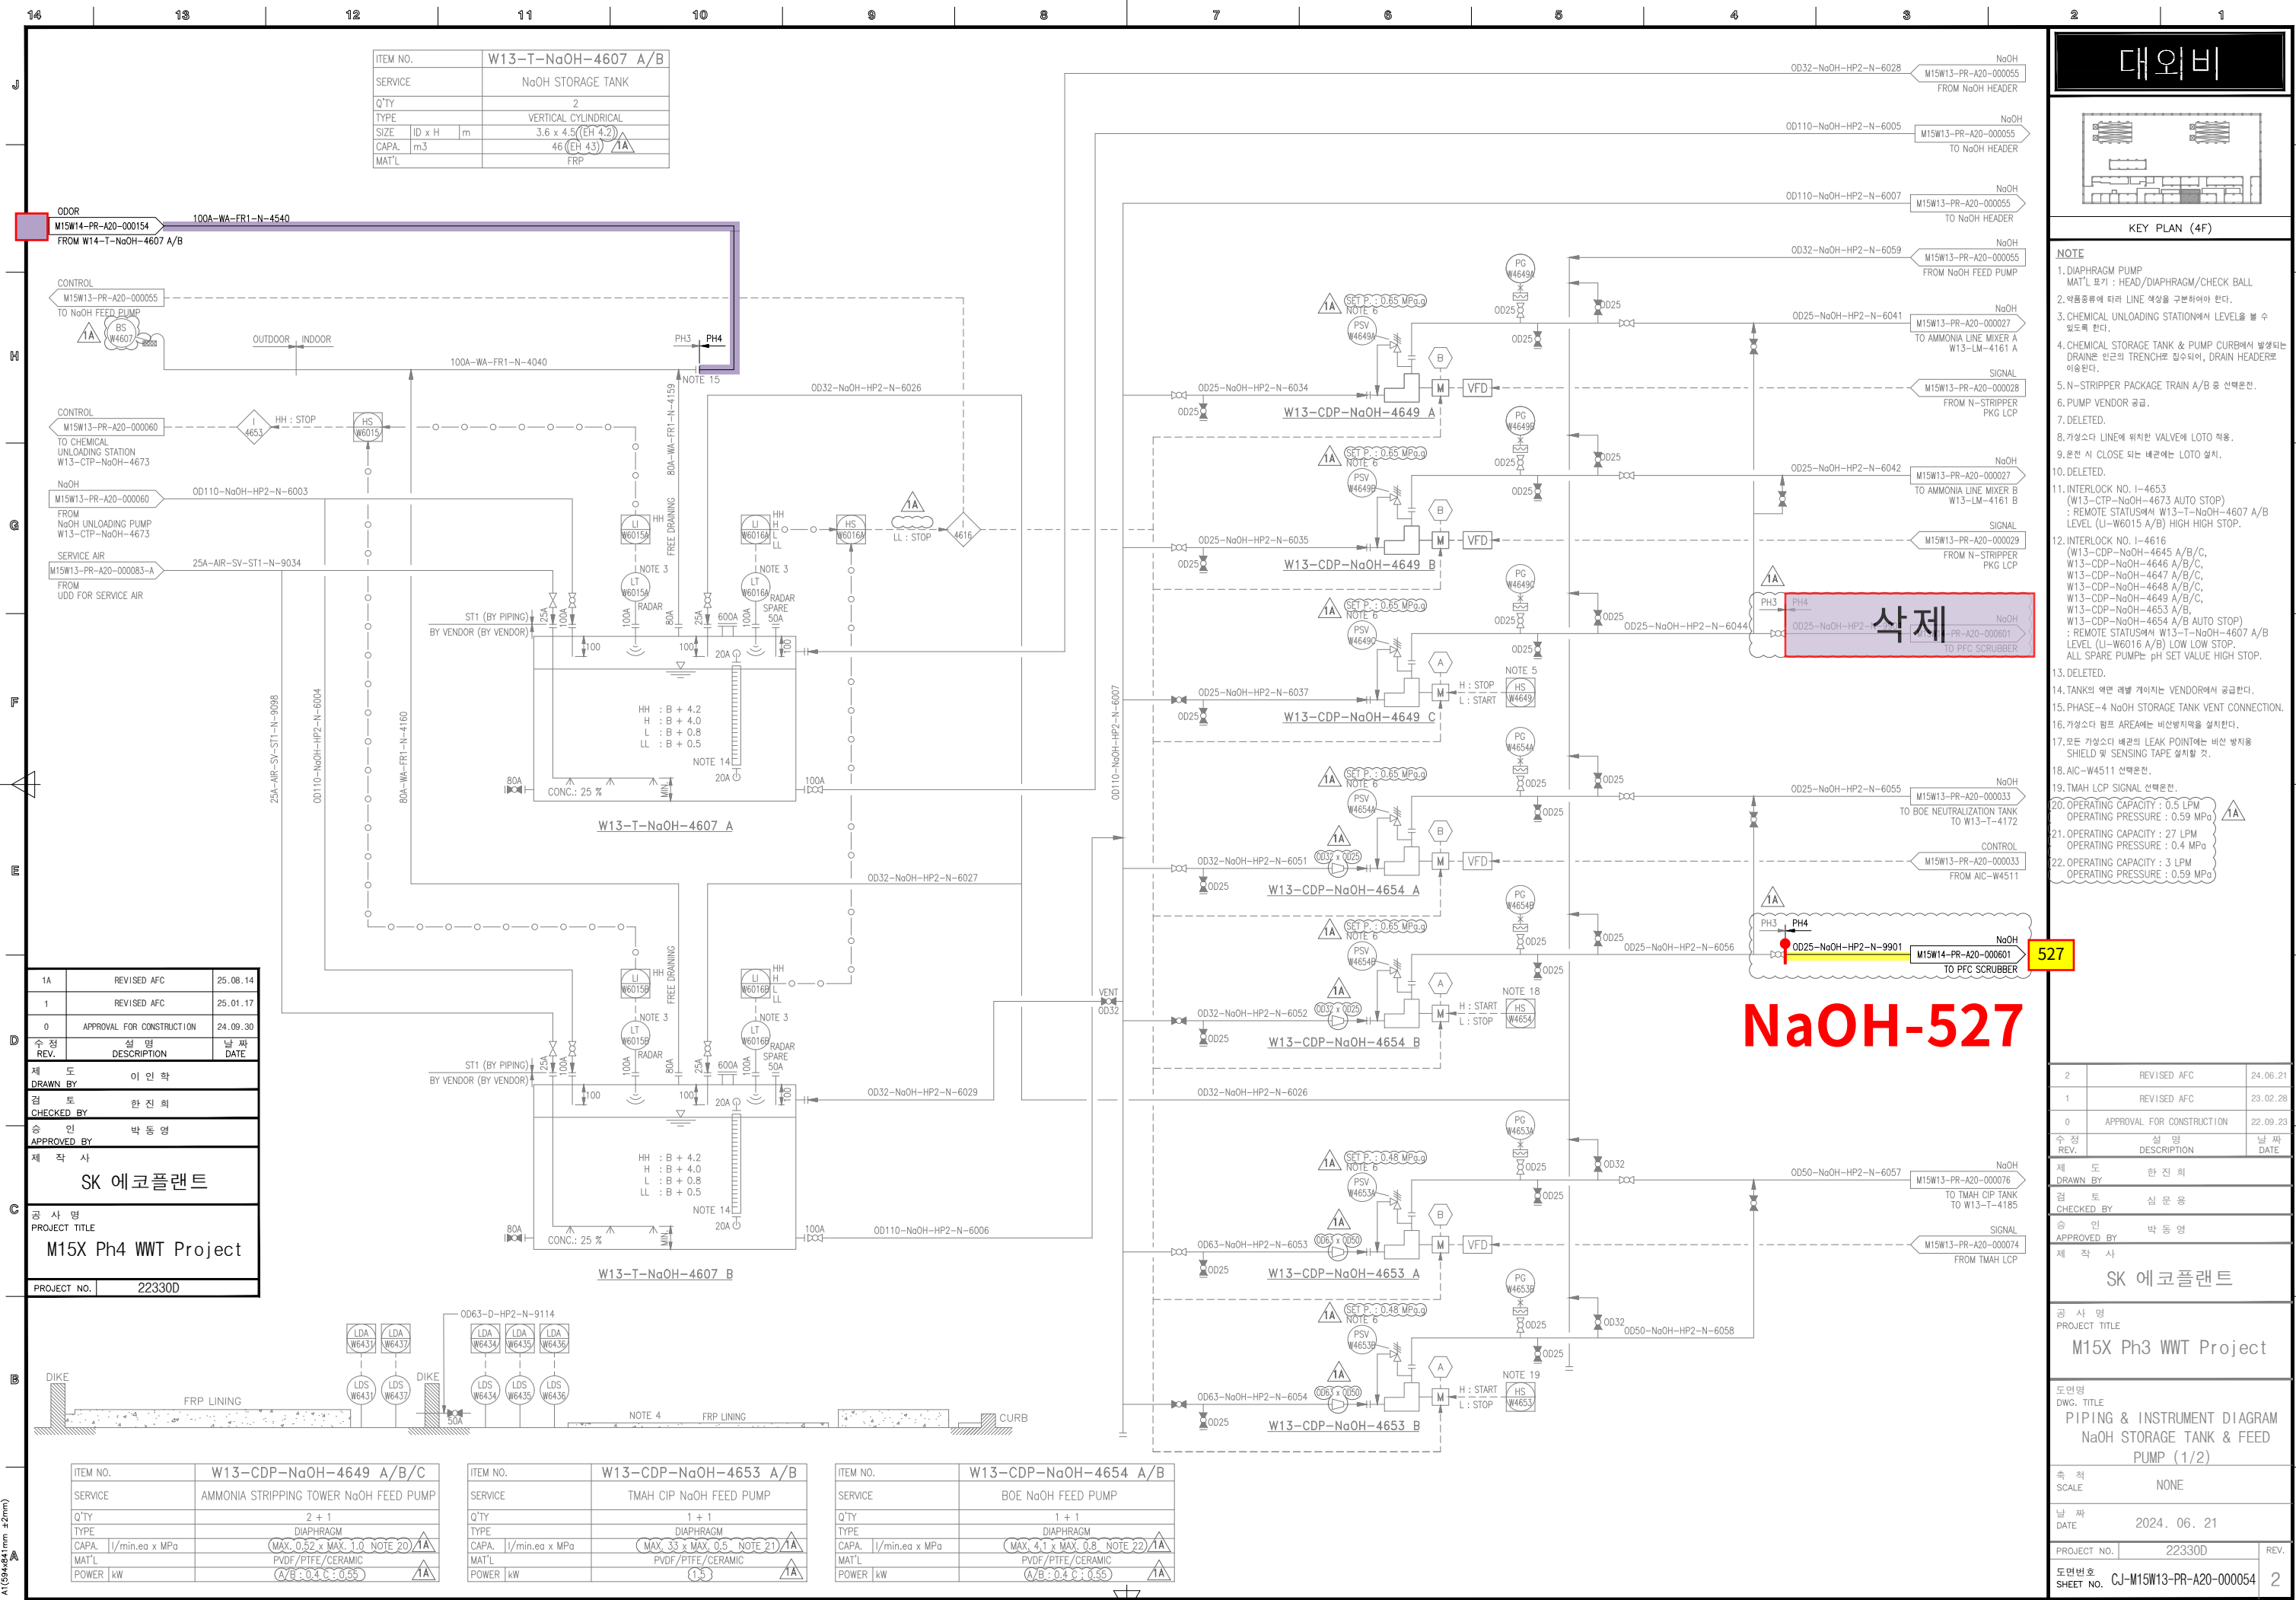

대외비

KEY PLAN (4F)

NOTE

1. DIAPHRAGM PUMP
MAT'L 표기 : HEAD/DIAPHRAGM/CHECK BALL

2.약품공류에 따라 LINE 색상을 구분하여야 한다.

3. CHEMICAL UNLOADING STATION에서 LEVEL을 볼 수 있도록 한다.

4. CHEMICAL STORAGE TANK & PUMP CURB에서 발생하는 DRAIN을 인근의 TRENCH로 침수되어, DRAIN HEADER로 이송된다.

5. N-STRIPPER PACKAGE TRAIN A/B 용 선택호전.

6. PUMP VENDOR 공급.

7. DELETED.

8. 가성스다 LINE에 위치한 VALVE에 LOTO 적용.

9. 운전 시 CLOSE 되는 배관에는 LOTO 설치.

10. DELETED.

11. INTERLOCK NO. I-4653
(W13-CTP-NaOH-4673 AUTO STOP)
: REMOTE STATUS에서 W13-T-NaOH-4607 A/B LEVEL (U-W6015 A/B) HIGH HIGH STOP.

12. INTERLOCK NO. I-4616
(W13-CDP-NaOH-4645 A/B/C,
W13-CDP-NaOH-4646 A/B/C,
W13-CDP-NaOH-4647 A/B/C,
W13-CDP-NaOH-4648 A/B/C,
W13-CDP-NaOH-4649 A/B/C,
W13-CDP-NaOH-4653 A/B,
W13-CDP-NaOH-4654 A/B AUTO STOP)
: REMOTE STATUS에서 W13-T-NaOH-4607 A/B LEVEL (U-W6015 A/B) LOW LOW STOP.
ALL SPARE PUMP는 pH SET VALUE HIGH STOP.

13. DELETED.

14. TANK의 액면 레벨 개지지는 VENDOR에서 공급한다.

15. PHASE-4 NaOH STORAGE TANK VENT CONNECTION.

16. 가성스다 펌프 AREA에는 비산방지막을 설치한다.

17. 모든 가성스다 배관의 LEAK POINT에는 비산 방지용 SHIELD 및 SENSING TAPE 설치할 것.

18. AIC-W4511 선택호전.

19. TMAH LCP SIGNAL 선택호전.

20. OPERATING CAPACITY : 0.5 LPM
OPERATING PRESSURE : 0.59 MPa

21. OPERATING CAPACITY : 27 LPM
OPERATING PRESSURE : 0.4 MPa

22. OPERATING CAPACITY : 3 LPM
OPERATING PRESSURE : 0.59 MPa

2

REVISED AFC

24.06.21

1

REVISED AFC

23.02.28

0

APPROVAL FOR CONSTRUCTION

22.09.23

수정 REV.

실명 DESCRIPTION

날짜 DATE

제 도

이 인 학

검 토

한 진 희

승 인

박 동 영

제 작 사

SK 에코플랜트

공 사 명

PROJECT TITLE

M15X Ph3 WWT Project

PROJECT NO.

22330D

2

REVISED AFC

24.06.21

1

REVISED AFC

23.02.28

0

APPROVAL FOR CONSTRUCTION

22.09.23

수정 REV.

실명 DESCRIPTION

날짜 DATE

제 도

한 진 희

검 토

심 문 용

승 인

박 동 영

제 작 사

SK 에코플랜트

공 사 명

PROJECT TITLE

M15X Ph3 WWT Project

도면명

DWG. TITLE

PIPING & INSTRUMENT DIAGRAM

NaOH STORAGE TANK & FEED PUMP (1/2)

측 척

SCALE

NONE

날 짜

DATE

2024. 06. 21

PROJECT NO.

22330D

REV.


A

도면번호

SHEET NO.

CJ-M15W13-PR-A20-000054

2

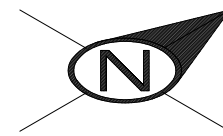

<NOTE>
1. (*) FIELD ADJUST

CONTRACTOR		PROJECT NAME	
		M15X Ph4 Project	
COMMODITY		JOB NO.	
NaOH		22330D	
LINE NO.	OD25-NaOH-HP2-N-9901	SH'T NO.	REV.
		01 / 01	0

경고 : 본 도면은 SK HYNIX의 기밀정보 자료로서, 어떠한 경우에도 목적 외 사용, 복제, 제3자에게 공개, 누설 등 유출할 수 없으며, 회사는 유출자의 불법 사용으로 피해가 발생할 경우 유출자에게 민/형사상 책임을 요구할 수 있음.

