


DRAWING LIST FOR TEST PACKAGE

AIR-DRY-544

PROJECT NO.: 22328D

PROJECT TITLE : M15X Ph2 Project

No	PKG No	UNIT	LINE NUMBER			P&ID		REMARK
			ISO DRAWING No	SHEET	REV	P&ID No	REV	
1	544	4FA	50A-AIR-DRY-ST1-N-9529-01	1 OF 1	0	CJ-M15W14-PR-A20-000113	2A	
2	544	4FA	80A-AIR-DRY-ST1-N-9510-01	1 OF 1	0	CJ-M15W13-PR-A20-000082-A	2	

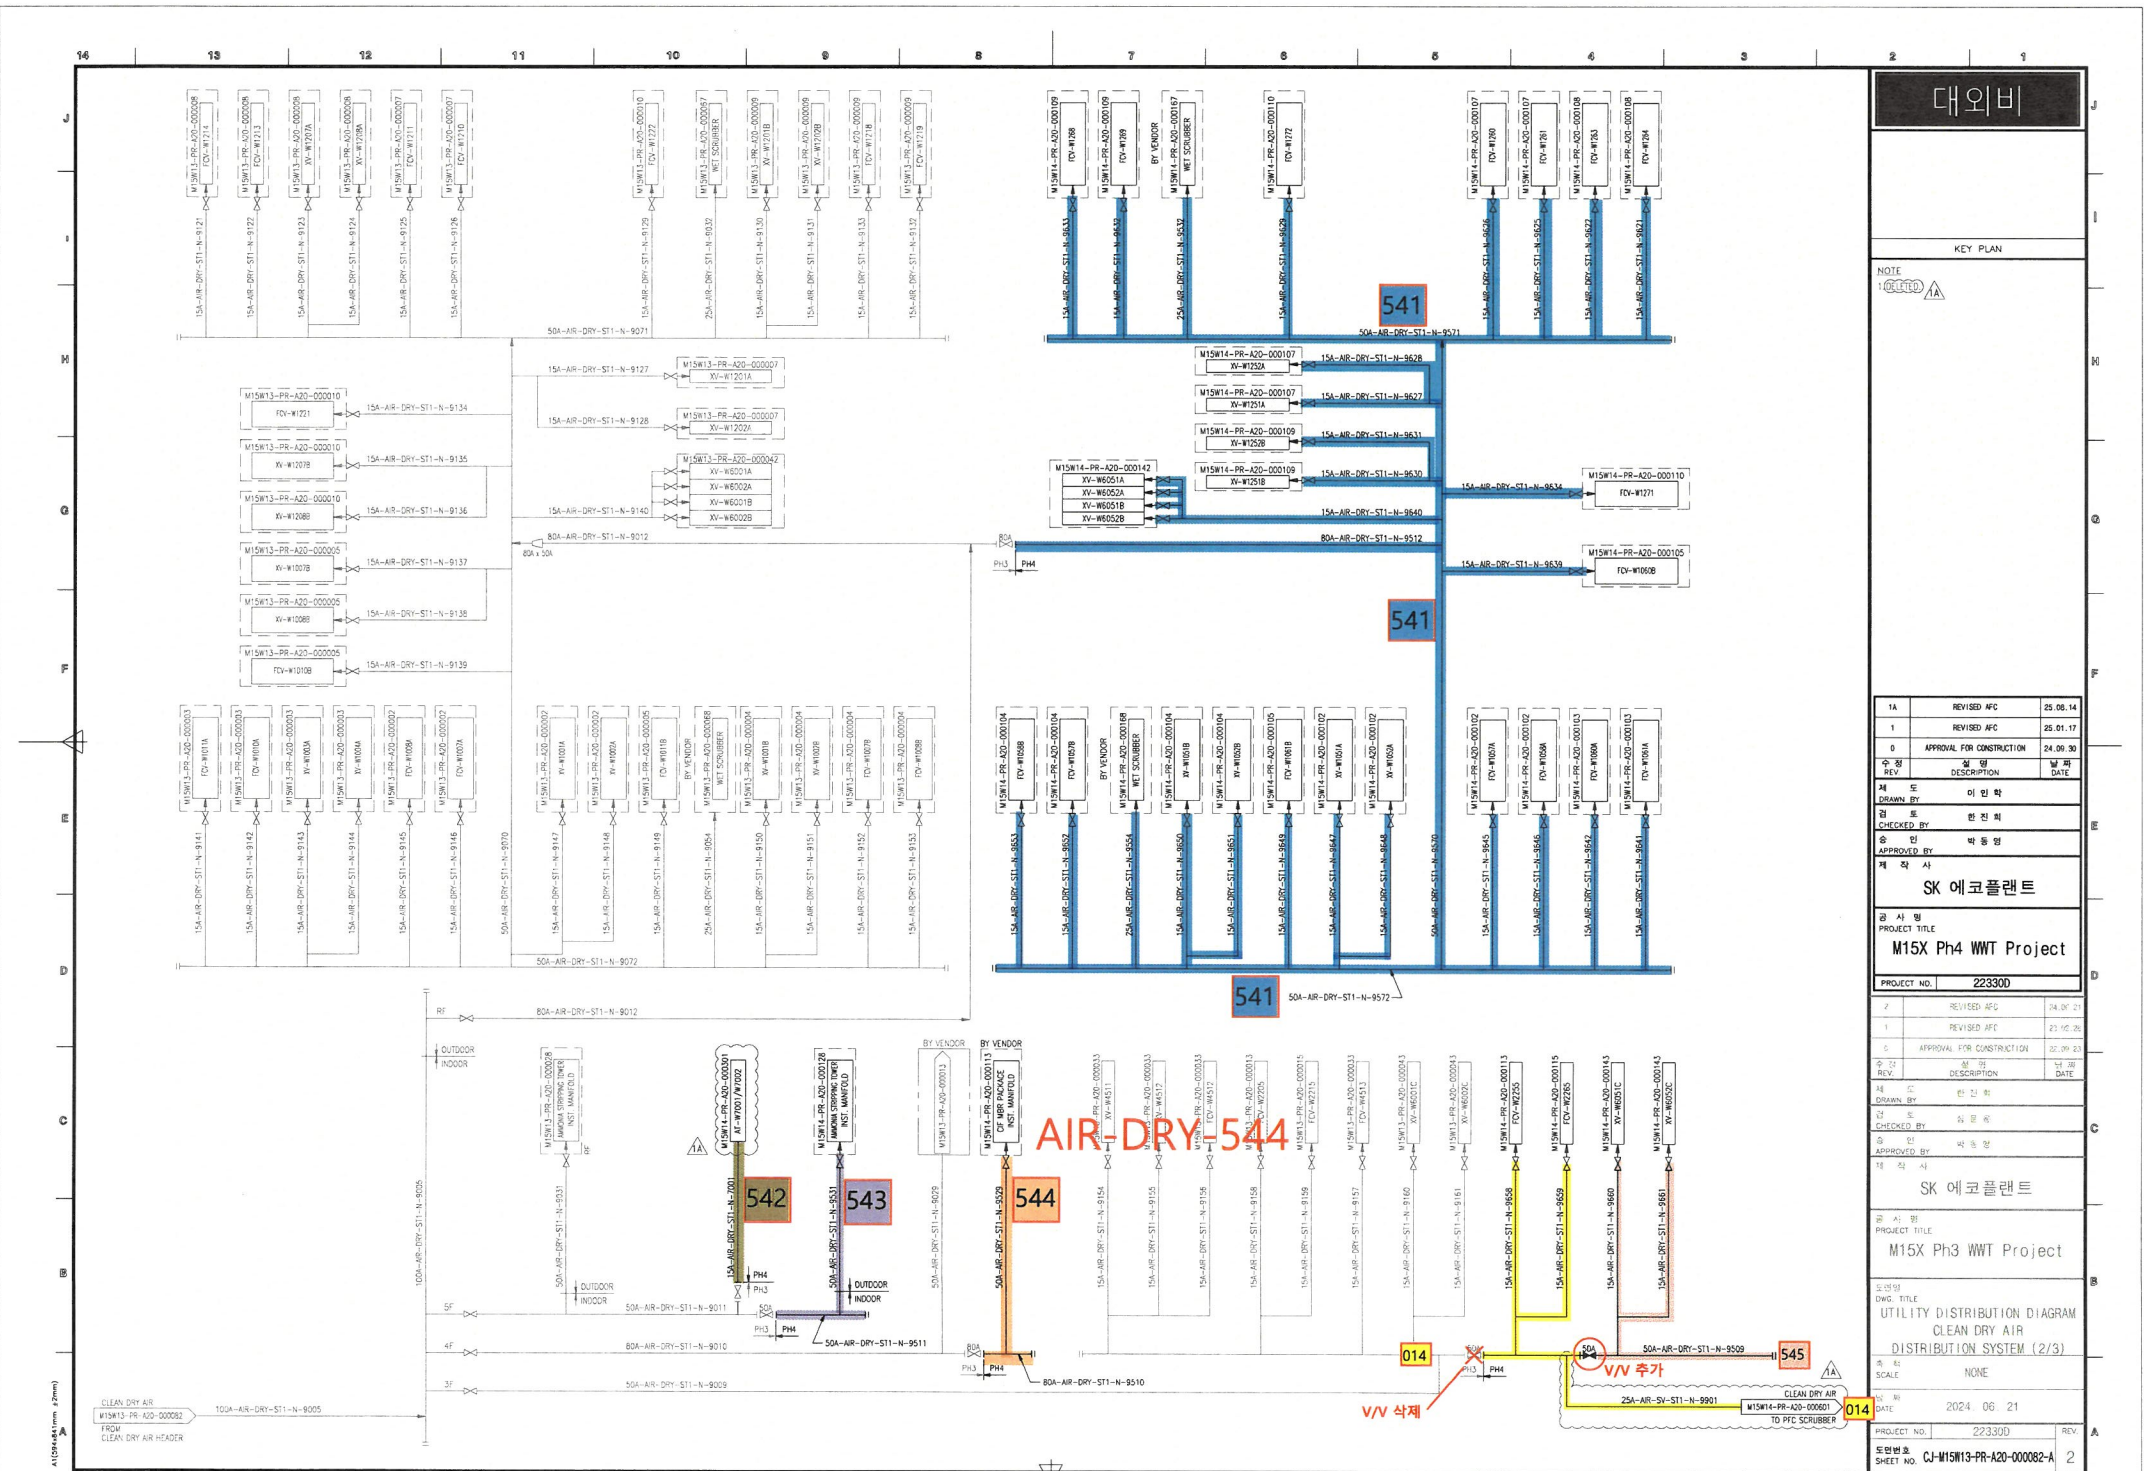

대외비

KEY PLAN

NOTE

REV	DESCRIPTION	DATE
1A	REVISED W/C	25.08.14
1	REVISED W/C	25.01.17
0	APPROVAL FOR CONSTRUCTION	24.08.30

수정	설명	날짜
도면	이민학	
검토	한진희	
확인	박동영	
작성		

SK 에코플랜트

M15X Ph4 WWT Project

PROJECT NO. 223300

2	REVISED W/C	24.09.21
1	REVISED W/C	23.05.26
0	APPROVAL FOR CONSTRUCTION	22.09.23

수정	설명	날짜
도면	한진희	
검토	조명숙	
확인	박동영	
작성		

SK 에코플랜트

M15X Ph3 WWT Project

UTILITY DISTRIBUTION DIAGRAM
CLEAN DRY AIR
DISTRIBUTION SYSTEM (2/3)

SCALE NONE

DATE 2024. 06. 21

PROJECT NO. 223300


도면번호 CJ-M15W13-PR-A20-000082-A

REV 2




INSULATION	CODE	N	CONDITION	PRESS. (kg/cm ² g)	TEMP (°C)	AREA	W14							CONTRACTOR	PROJECT NAME
	THICK.	-	DESIGN	10	60	UNIT	4FA								M15X Ph4 Project
			OPERATING	7.5	AMB	REF. PLAN DWG.								COMMODITY	JOB NO.
						CJ-M15W14-PI-A30-040002-C								AIR-DRY	22330D
						REF. P & ID								LINE NO.	SH'T NO.
						CJ-M15W13-PR-A20-000082-A								50A-AIR-DRY-ST1-N-9529	01 / 01
						REV. NO.	DATE	DESCRIPTION	BY	CHK	APP'D				REV.
							25.01.24	APPROVED FOR CONSTRUCTION	황재훈	안남후	박동영				0

경고 : 본 도면은 SK HYNIX의 기업비밀 자료로서, 어떠한 경우에도 목적 외 사용, 복제, 제3자에게 공개, 누설 및 유출할 수 없으며, 회사는 유도자의 불법 사용으로 피해가 발생할 경우 유도자에게 민/형사상 책임을 요구할 수 있음

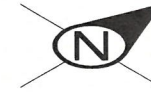

ITEM	SIZE	Q'TY	DESCRIPTION
ST1			
P	80A	73.0M	PIPE, STS 304TP, ERW, BE - SCH 10S
E90	80A	2EA	ELBOW 90 DEG LR, STS304, ERW, BE - SCH 10S
STU	80Ax50A	1EA	STUB-IN BRANCH
F	80A	2EA	FLG SD, KS 10K, RF, STS304
FB	80A	1EA	FLG BLIND, KS 10K, RF, STS304
G	80A	2EA	GASKET, KS 10K, RF, PTFE+EPDM, 3.0MM TH'K
B	80A	2SET	MACHINE BOLT & NUTS :STS 304 / W WASHERS

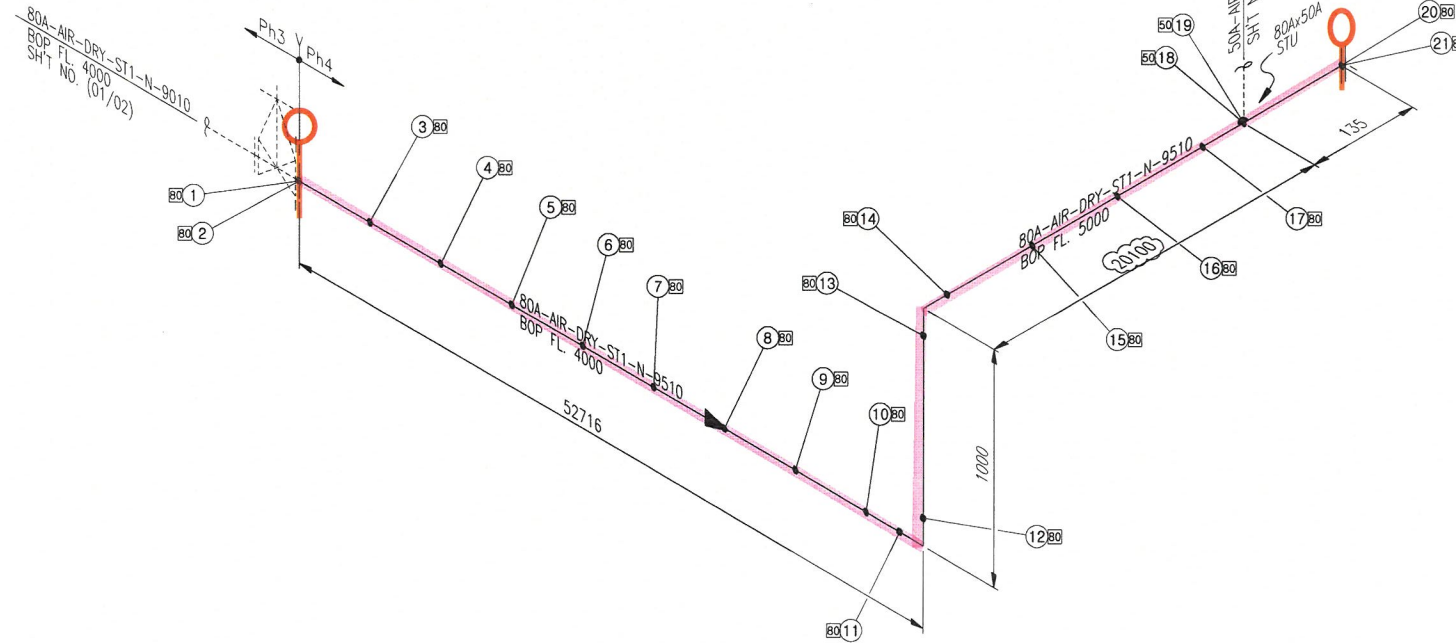

* PIPE : P/P1 * 90° ELBOW : E90 * 45° ELBOW : E45 * TEE : T * RED TEE : TR * STUB-IN : STU * REINFORCING PAD : RP * CON.RED : RC * ECC.RED : RE * CON.SWAGE : RCS/RCS1 * ECC.SWAGE : RES/RES1 * NIPPLE : NP/NP1/NP2 * CAP : CAP/CAP1 * PLUG : PLG * FULL COUPLING : FC * HALF COUPLING : HF/HF1
* STUB-IN : STU * SOCKET(HDPE/PVC) : SC * SADDLE(HDPE) : SD * FLANGE : F/F1 * GASKET : G/G1/G2 * BOLT & NUT : B/B1 * BLIND FLANGE : FB/FB1 * GATE VA. : VG/VG1/VG2 * BALL VA. : VB/VB1/VB2/VB2LO * BUTTERFLY VA. : VF/VF1 * CHECK VA. : VC/VC1/VC2/VC3/VC4/VC5/VC6/VC7
* GLOBE VA. : VL/VL1/VL2 * DIAPHRAGM VA. : VD/VDLO * DAMPER : VP * QUICK COUPLING : SQC * FLEXIBLE JOINT(STEEL) : FLXB * FLEXIBLE JOINT(RUBBER) : FLXR * FLEXIBLE JOINT(STEEL PIPE LINED) : FLXL * FLEXIBLE HOSE : FLXH * STEAM TRAP : ST * SPRAY NOZZLE : SPN * EMERGENCY SHOWER : SSH
* STRAINER(Y-TYPE) : YSTR * STRAINER(T-TYPE) : TSTR * STRAINER(BUCKET-TYPE) : BSTR * ANCHOR PLATE : STOP * BIRD SCREEN : BS * ISOLATION KIT : IK * UNLOADING BOX : UB * AIR TRAP : AT * LOTID : LOTID * SIGHT GLASS : SG * PRESSURE GAUGE : PG * SHIELD : SH * SPECIAL BOLT & NUT : BL/BL1

INSULATION	CODE	N	CONDITION	PRESS. (kg/cm2g)	TEMP. (°C)	AREA	W14				
	THICK.	-	DESIGN	10	60	UNIT	4FA				
			OPERATING	7.5	AMB	REF. PLAN DWG.					
						CJ-M15W14-PI-A30-040008-A					
						REF. P & ID					
						CJ-M15W13-PR-A20-000082-A					

CLIENT		SK hynix 2	
CONTRACTOR		SK ecoplant	
COMMODITY		AIR-DRY	
LINE NO.		80A-AIR-DRY-ST1-N-9510	
PROJECT NAME		M15X Ph4 Project	
JOB NO.		22330D	
SH'T NO.		01 / 01	
REV.		0	

경고 : 본 도면은 SK HYNIX의 기밀비밀 자료로서, 어떠한 경우에도 목적 외 사용, 복제, 제3자에게 공개, 누설 및 유출할 수 없으며, 회사는 유표자의 불법 사용으로 피해가 발생할 경우 유표자에게 민/형사상 책임을 요구할 수 있음.

PUNCH LIST

Project No : 22330D

Package No :

Project Title : M15X Ph3 Project

Date :

S/N	Drawing No	Description	Category A B C	Punch Clear Status			
				작성자		확인자	
				Name	Sign	Name	Sign
1							
2							
Remarks

A : Before Hydro Test

B : Before M/C

C : Before Commissioning