



DRAWING LIST FOR TEST PACKAGE

PROJECT NO.: 22328D

PROJECT TITLE : M15X Ph2 Project

CAOH2-547

No	PKG No	UNIT	LINE NUMBER			P&ID		REMARK
			ISO DRAWING No	SHEET	REV	P&ID No	REV	
1	547	RFA	80A-CAOH2-ST3-E-6559-01	1 OF 1	1	CJ-M15W14-PR-A20-000142	1A	
2	547	RFA	OD90-CAOH2-PV2-E-6583-01	1 OF 1	1	CJ-M15W14-PR-A20-000104	1A	

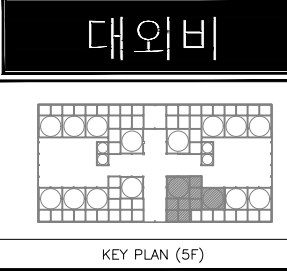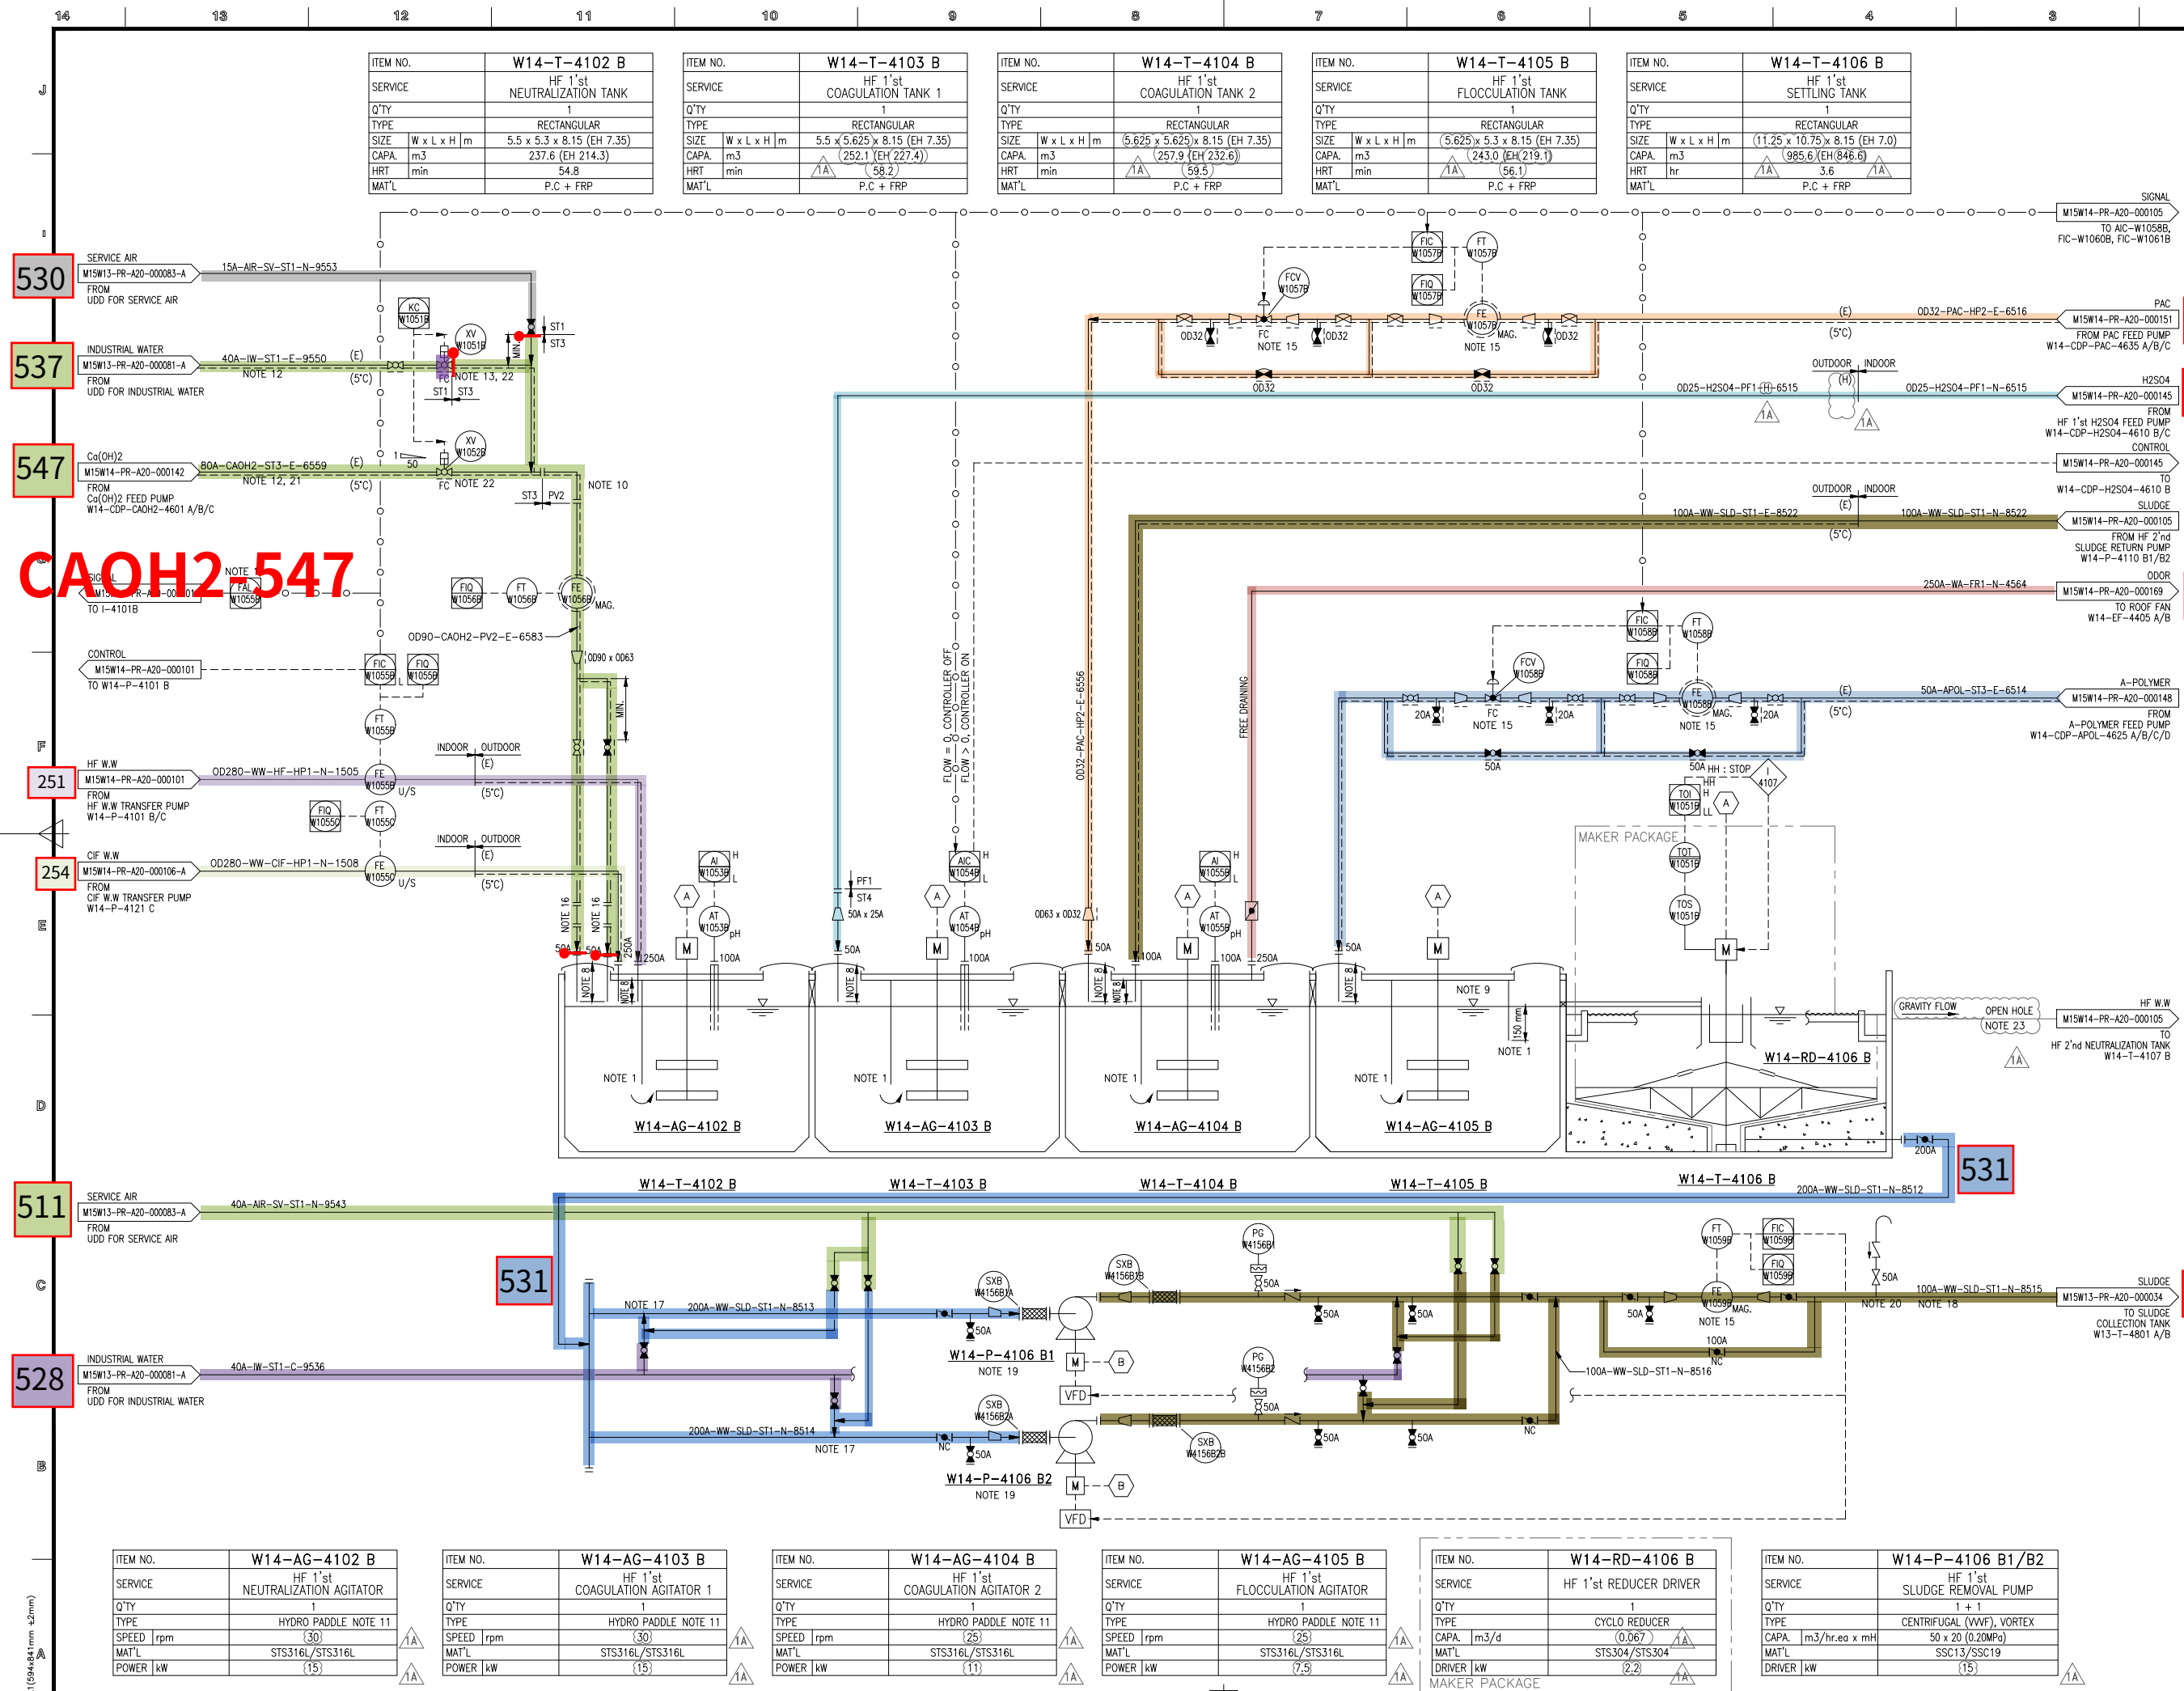


- NOTE**
1. Baffle 제형 : FRP
Baffle 상부에 0.02 m2 이상 AIR HOLE 설치.
 2. NK와 HWL 이하로 연결되는 모든 배관은 BLOCK 밸브 1일 것.
 3. 3.2m 이상 높은 곳에 설치된 밸브는 CHAIN VALVE 또는 PLATFORM 구성할 것.
 4. INHOLE : 2개 이상 설치한다.
INHOLE COVER : FRP
시 CLOSE 되는 배관에는 LOTO 설치.
 5. CENTRIFUGAL PUMP.
MAT'L 표기 : CASING / IMPELLER
 6. AGITATOR MAT'L 표기 : SHAFT/BLADE
 7. TANK 내 유입시, 육안 확인이 가능하고, 비산이 되지 않도록 최소 길이로 변경 할 것.
B 으로부터 100mm 떨어질 것
 8. FRP LINING TANK의 SLEEVE는 504 + FRP LINING 적용.
 9. 10. Co(OH)2 배관의 ELBOW 부분은 FLANGE 설치할 것
 11. 주용 VENDOR에서 결정한다.
 12. 라인은 상부에서 시공 시 유입하드록 설치한다.
 13. W1051B OPEN (12시간마다 15초) 일 경우 : W1052B CLOSE
 14. W14-P-4101 B가 RUN 후 30초 후부터 동작한다.
 15. INSTRUMENT VENDOR 선정 후 CONTROL SCHEME 및 CONTROL VALVE INLET/OUTLET NOZZLE SIZE 확정
 16. 구간 투명 PVC 적용. (주입 여부 확인용)
 17. SHING 용 WATER / AIR 배관은 45도 서선으로 연결할 것.

1A	REVISED AFC	25.08.14
1	REVISED AFC	25.01.17
0	APPROVAL FOR CONSTRUCTION	24.09.30
수정	실명	날짜
REV.	DESCRIPTION	DATE

제 도	이 인 학
DRAWN BY	
토	한 진 희
DESIGNED BY	
인	박 동 영
CHECKED BY	

SK 에코플랜트		
공 사 명		
PROJECT TITLE		
M15X Ph4 WWT Project		
도면명		
DWG. TITLE		
PIPING & INSTRUMENT DIAGRAM		
HF 1st COAGULATION & SETTLING TANK B (2/2)		
속 측	SCALE	
	NONE	
날 짜	DATE	
	2025. 08. 14	
PROJECT NO.	22330D	REV.
도면번호	CJ-M15W14-PR-A20-000104	1A

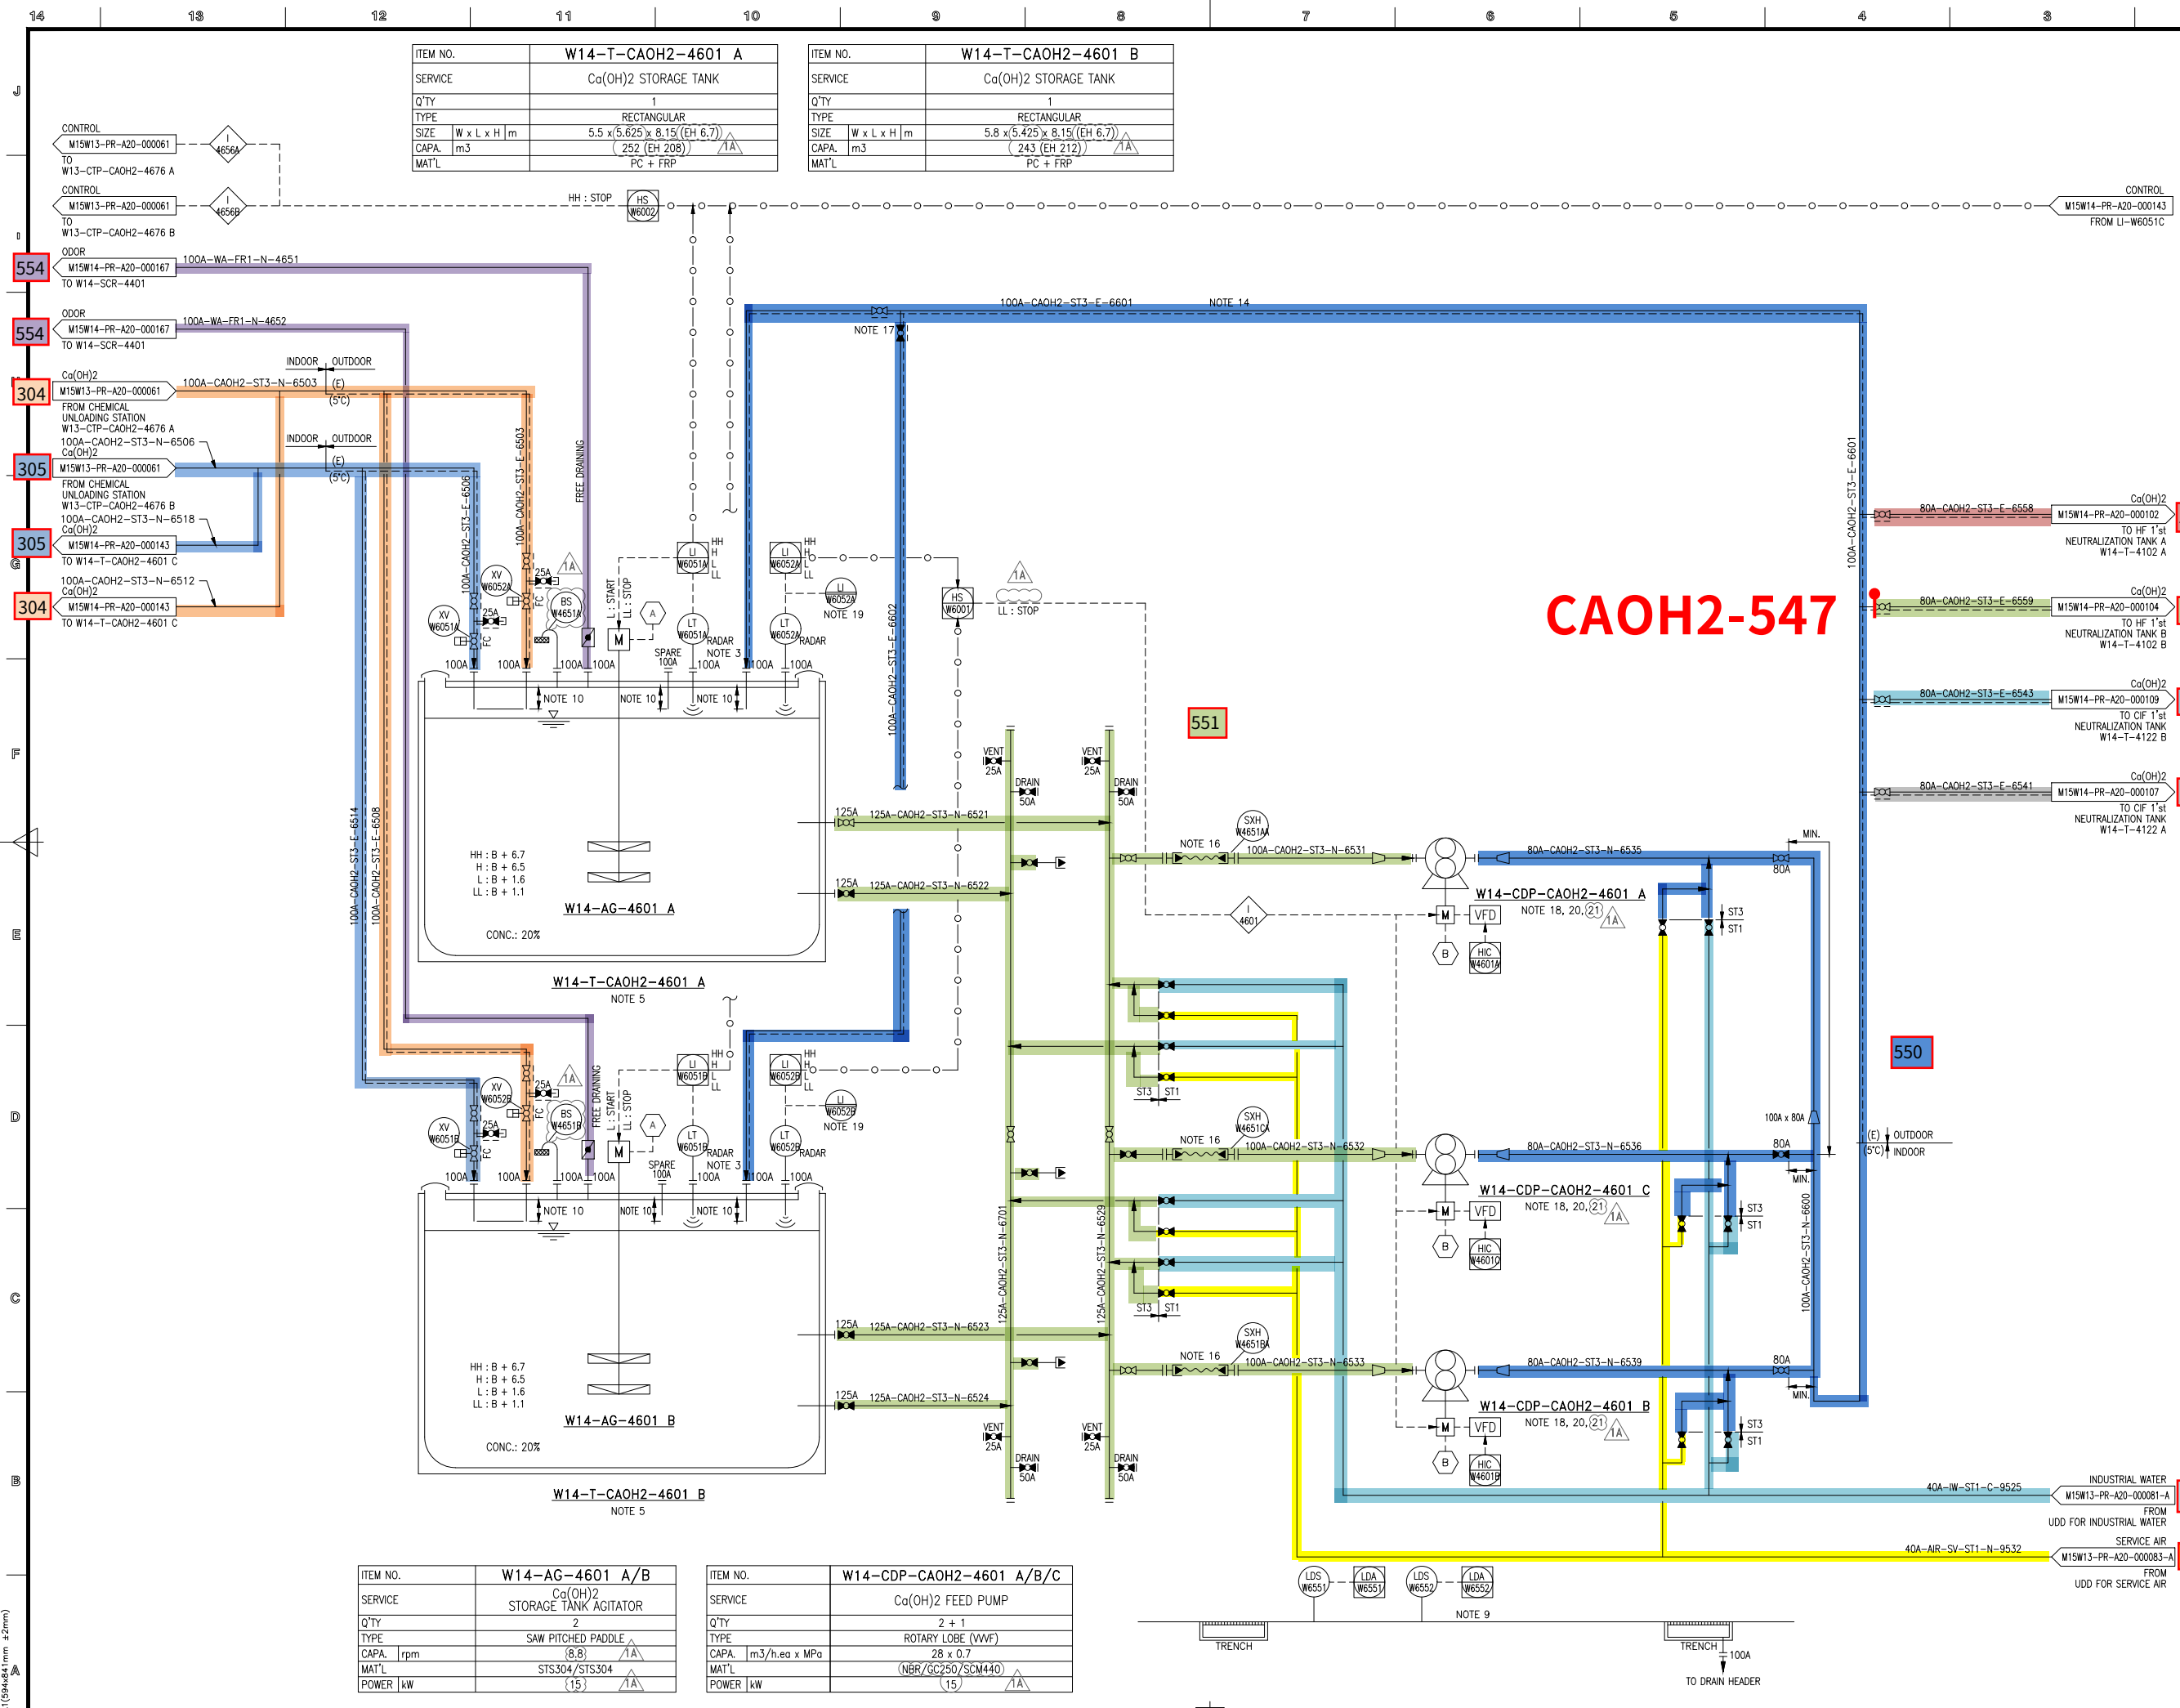

대외비

KEY PLAN (5F)

NOTE

- CaOH2 배관의 ELBOW 부분은 FLANGE 설치할 것.
- 2m 이상 높은 곳에 설치된 밸브는 CHAIN VALVE 또는 PLATFORM 구성할 것.
- CHEMICAL UNLOADING STATION에서 LEVEL을 볼 수 있도록 한다.
- P&ID에 표기된 모든 ELECTRIC POWER는 VENDOR PRINT 참조 후 작성할 것.
- 5층에 설치할 것.
- 약품종류에 따라 LINE 색상을 구분하여야 한다.
- 훈련 시 CLOSE 되는 배관에는 LOTO 설치.
- AGITATOR MAT'L 표기 : SHAFT/BLADE
- CHEMICAL STORAGE TANK CURB 및 PUMP AREA에서 발생되는 DRAIN은 인근의 TRENCH로 집수되어, DRAIN HEADER로 이송된다.
- TANK 내 유량, 폭안 확인이 가능하고, 비산되지 않도록 최소 길이로 반영할 것 (SLAB로부터 100mm 떨어진 것).
- MANHOLE : 2개 이상 설치한다.
- INTERLOCK NO. 1-4601 (W14-CDP-CAOH2-4601 A/B/C AUTO STOP) : REMOTE STATUS#M W14-T-CAOH2-4601 A/B LEVEL (LI-W6052A/B) LOW LOW STOP.
- INTERLOCK NO. 1-4656A/B (W13-CTP-CAOH2-4676 A/B AUTO STOP) : REMOTE STATUS#M W14-T-CAOH2-4601 A/B/C LEVEL (LI-W6051A/B/C) HIGH HIGH STOP.
- RINGMAN LINE SCHEMATIC

SCHEMATIC DRAWING

- 내부 FRP LINING TANK의 SLEEVE는 SUS304 + FRP LINING 적용.
- 7개 VENDOR LOOSE PART 공급.
- 훈련용 Ca(OH)2 TANK A/B RETURN VALVE 2ea 중 1ea는 반드시 OPEN 되어있어야 한다.
- INTERNAL PSV 설치 할 것.
- 5층 소액취 주입포트 인근에 TANK LEVEL 확인 가능하도록 LOCAL PANEL 설치.
- 소액취 주입 포트 AREA에는 비산 방지막을 설치한다.
- INTERNAL PSV SET PRESSURE : 0.8 Mpa(g)

REV.	DESCRIPTION	DATE
1A	REVISED AFC	25.08.14
1	REVISED AFC	25.01.17
0	APPROVAL FOR CONSTRUCTION	24.09.30

수정
REV.

설 명
DESCRIPTION

날 짜
DATE

제 도
DRAWN BY

이 인 학

검 토
CHECKED BY

한 진 희

승 인
APPROVED BY

박 동 영

제 작 사

SK 에코플랜트

공 사 명
PROJECT TITLE

M15X Ph4 WWT Project

면 명
WG. TITLE

PIPING & INSTRUMENT DIAGRAM

속 측
SCALE

NONE

날 짜
DATE

2025. 08. 14

PROJECT NO.

22330D


도면번호
SHEET NO.

CJ-M15W14-PR-A20-000142

REV.

1A

C:\Users\WTOP\Desktop\WP&ID251013W[M15X Ph-4 for 인허가]CAD FILE_0910WCJ-M15W14-PR-A20-000142 R1 P&ID FOR Ca(OH)

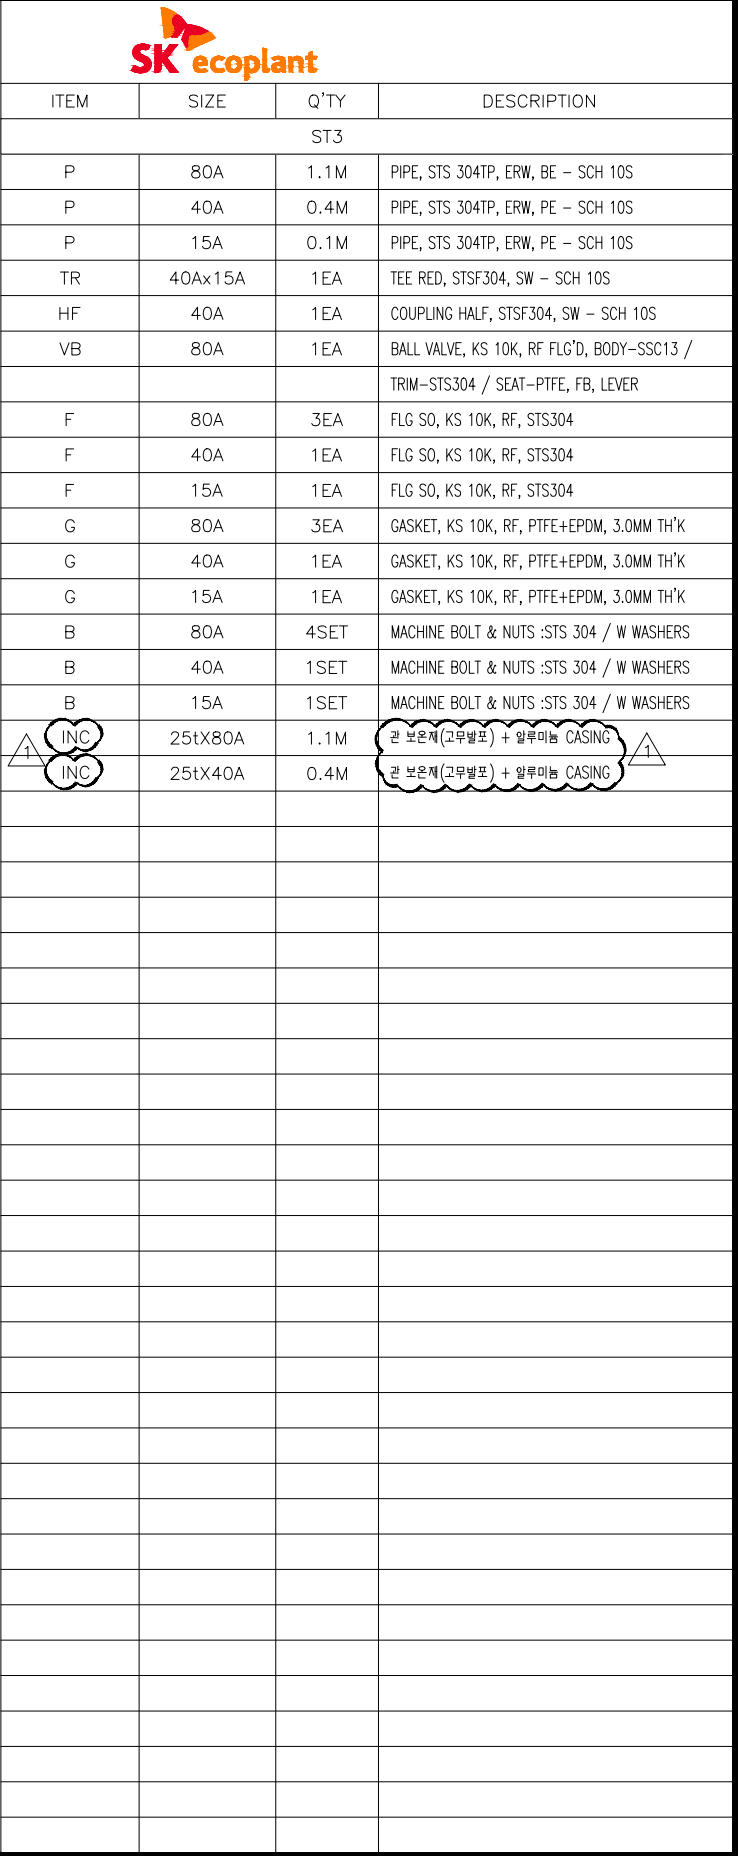

* HALF COUPLING : HF/HF1
 * EMERGENCY SHOWER : SSH
 * SPECIAL BOLT & NUT : BL/BL1

* PIPE : P/P1 * 90° ELBOW : E90 * 45° ELBOW : E45 * TEE : T * RED.TEE : TR * STUB-IN : STU * REINFORCING PAD : RP * CON.RED : RC * ECC.RED : RE * CON.SWAGE : RCS/RCS1 * ECC.SWAGE : RES/RES1 * NIPPLE : NP/NP1/NP2 * CAP : CAP/CAP1 * PLUG : PLG * FULL COUPLING : FC * HALF COUPLING : HF/HF1 * STUB-IN : STU * SOCKET(HDPE/PVC) : SC * SADDLE(HDPE) : SD * FLANGE : F/F1 * GASKET : G/G1/G2 * BOLT & NUT : B/B1 * BLIND FLANGE : FB/FB1 * GATE VA. : VG/VG1/VG2 * BALL VA. : VB/VBLO/VB1/VB1LO/VB2/VB2LO * BUTTERFLY VA. : VF/VF4 * CHECK VA. : VC/VC1/VC2/VC3/VC4/VC5/VC6/VC7 * GLOBE VA. : VL/VL1/VL2 * DIAPHRAGM VA. : VD/VDLO * DAMPER : VP * QUICK COUPLING : SQC * FLEXIBLE JOINT(STEEL) : FLXB * FLEXIBLE JOINT(RUBBER) : FLXR * FLEXIBLE JOINT(STEEL PTFE LINED) : FLXL * FLEXIBLE HOSE : FLXH * STEAM TRAP : ST * SPRAY NOZZLE : SPN * EMERGENCY SHOWER : SSH * STRAINER(Y-TYPE) : YSTR * STRAINER(T-TYPE) : TSTR * STRAINER(BUCKET-TYPE) : BSTR * ANCHOR PLATE : STOP * BIRD SCREEN : BS * ISOLATION KIT : IK * UNLOADING BOX : UB * AIR TRAP : AT * LOTO : LOTO * SIGHT GLASS : SG * PRESSURE GAUGE : PG * SHILED : SH * SPECIAL BOLT & NUT : BL/BL1									
--	--	--	--	--	--	--	--	--	--

INSULATION	CODE	E	CONDITION	PRESS. (kg/cm2g)	TEMP. (°C)	AREA	W14						
	THICK.	25	DESIGN	8	60	UNIT	RFA						
			OPERATING	7.2	AMB	REF. PLAN DWG.			25.03.31	REVISED AS MARKED	황래중	안남후	박동
						CJ-M15W14-PI-A30-R10009-B			25.01.24	APPROVED FOR CONSTRUCTION	황래중	안남후	박동
						REF. P & ID CJ-M15W14-PR-A20-000104		REV. NO.	DATE	DESCRIPTION	BY	CHK	APP

[illegible]

