


DRAWING LIST FOR TEST PACKAGE

PROJECT NO.: 22328D

PROJECT TITLE : M15X Ph2 Project

CAOH2-548

No	PKG No	UNIT	LINE NUMBER			P&ID		REMARK
			ISO DRAWING No	SHEET	REV	P&ID No	REV	
1	548	RFA	80A-CAOH2-ST3-E-6543-01	1 OF 1	1	CJ-M15W14-PR-A20-000142	1A	
2	548	RFA	OD90-CAOH2-PV2-E-6587-01	1 OF 1	1	CJ-M15W14-PR-A20-000109	1A	

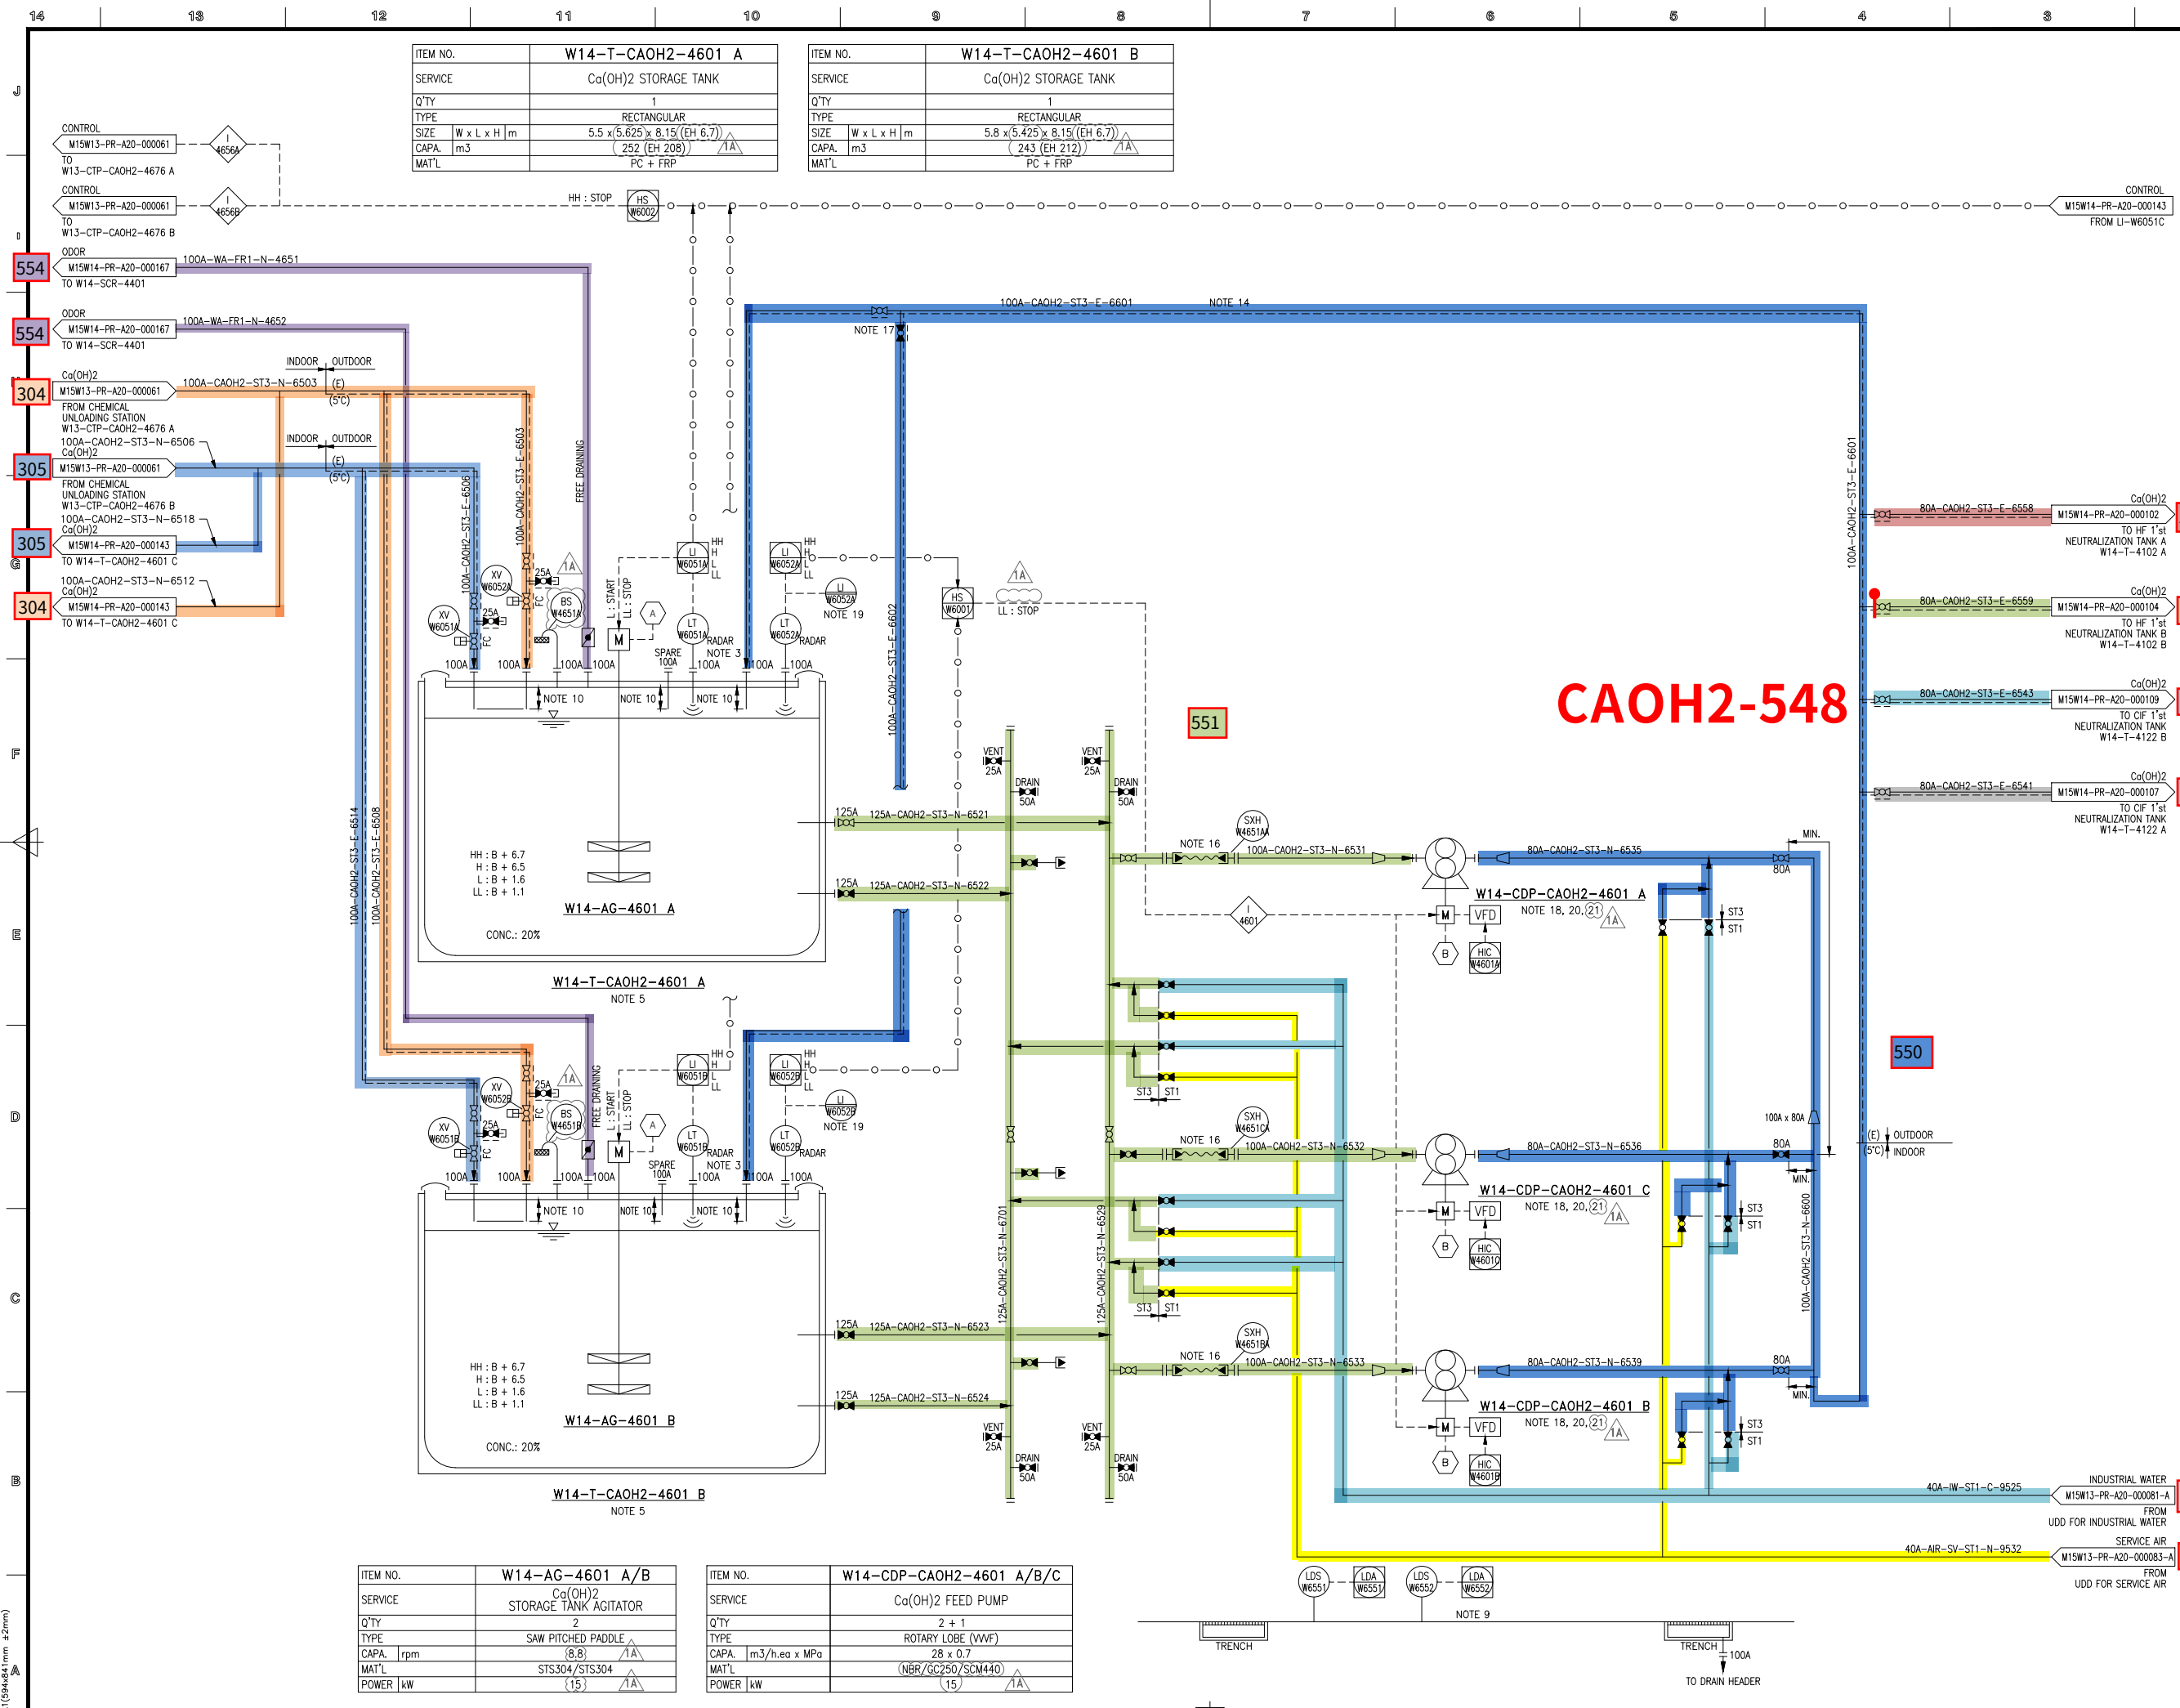

대외비

KEY PLAN (5F)

NOTE

- CaOH2 배관의 ELBOW 부분은 FLANGE 설치할 것.
- 2m 이상 높은 곳에 설치된 밸브는 CHAIN VALVE 또는 PLATFORM 구성할 것.
- CHEMICAL UNLOADING STATION에서 LEVEL을 볼 수 있도록 한다.
- P&ID에 표기된 모든 ELECTRIC POWER는 VENDOR PRINT 참조 후 작성함.
- 5층에 설치함.
- 약품종류에 따라 LINE 색상을 구분하여야 한다.
- 훈련 시 CLOSE 되는 배관에는 LOTO 설치.
- AGITATOR MAT'L 표기 : SHAFT/BLADE
- CHEMICAL STORAGE TANK CURB 및 PUMP AREA에서 발생되는 DRAIN은 인근의 TRENCH로 흡수되어, DRAIN HEADER로 이송된다.
- TANK 내 유량, 폭안 확인이 가능하고, 비산되지 않도록 최소 길이로 반영할 것 (SLAB로부터 100mm 떨어진 것).
- MANHOLE : 2개 이상 설치한다.
- INTERLOCK NO. 1-4601 (W14-CDP-CAOH2-4601 A/B/C AUTO STOP) REMOTE STATUS#M W14-T-CAOH2-4601 A/B LEVEL (LI-W6052A/B) LOW LOW STOP.
- INTERLOCK NO. 1-4656A/B (W13-CTP-CAOH2-4676 A/B AUTO STOP) REMOTE STATUS#M W14-T-CAOH2-4601 A/B/C LEVEL (LI-W6051A/B/C) HIGH HIGH STOP.
- RINGMAN LINE SCHEMATIC

SCHEMATIC DRAWING

- 내부 FRP LINING TANK의 SLEEVE는 SUS304 + FRP LINING 적용.
- 7개 VENDOR LOOSE PART 공급.
- 훈련용 Ca(OH)2 TANK A/B RETURN VALVE 2ea 중 1ea는 반드시 OPEN 되어있어야 한다.
- INTERNAL PSV 설치 할 것.
- 5층 소액취 주입포트 인근에 TANK LEVEL 확인 가능하도록 LOCAL PANEL 설치.
- 소액취 주입 포트 AREA에는 비산 방지막을 설치한다.
- INTERNAL PSV SET PRESSURE : 0.8 Mpa(g)

REV.	DESCRIPTION	DATE
1A	REVISED AFC	25.08.14
1	REVISED AFC	25.01.17
0	APPROVAL FOR CONSTRUCTION	24.09.30

수정

REV.

설명

DESCRIPTION

날짜

DATE

제 도

DRAWN BY

이 인 학

검 토

CHECKED BY

한 진 희

승 인

APPROVED BY

박 동 영

제 작 사

SK 에코플랜트

공 사 명

PROJECT TITLE

M15X Ph4 WWT Project

면명

WG. TITLE

PIPING & INSTRUMENT DIAGRAM

속 측

SCALE

NONE

날 짜

DATE

2025. 08. 14

PROJECT NO.

22330D

REV.


A

도면번호

SHEET NO.

CJ-M15W14-PR-A20-000142


1A

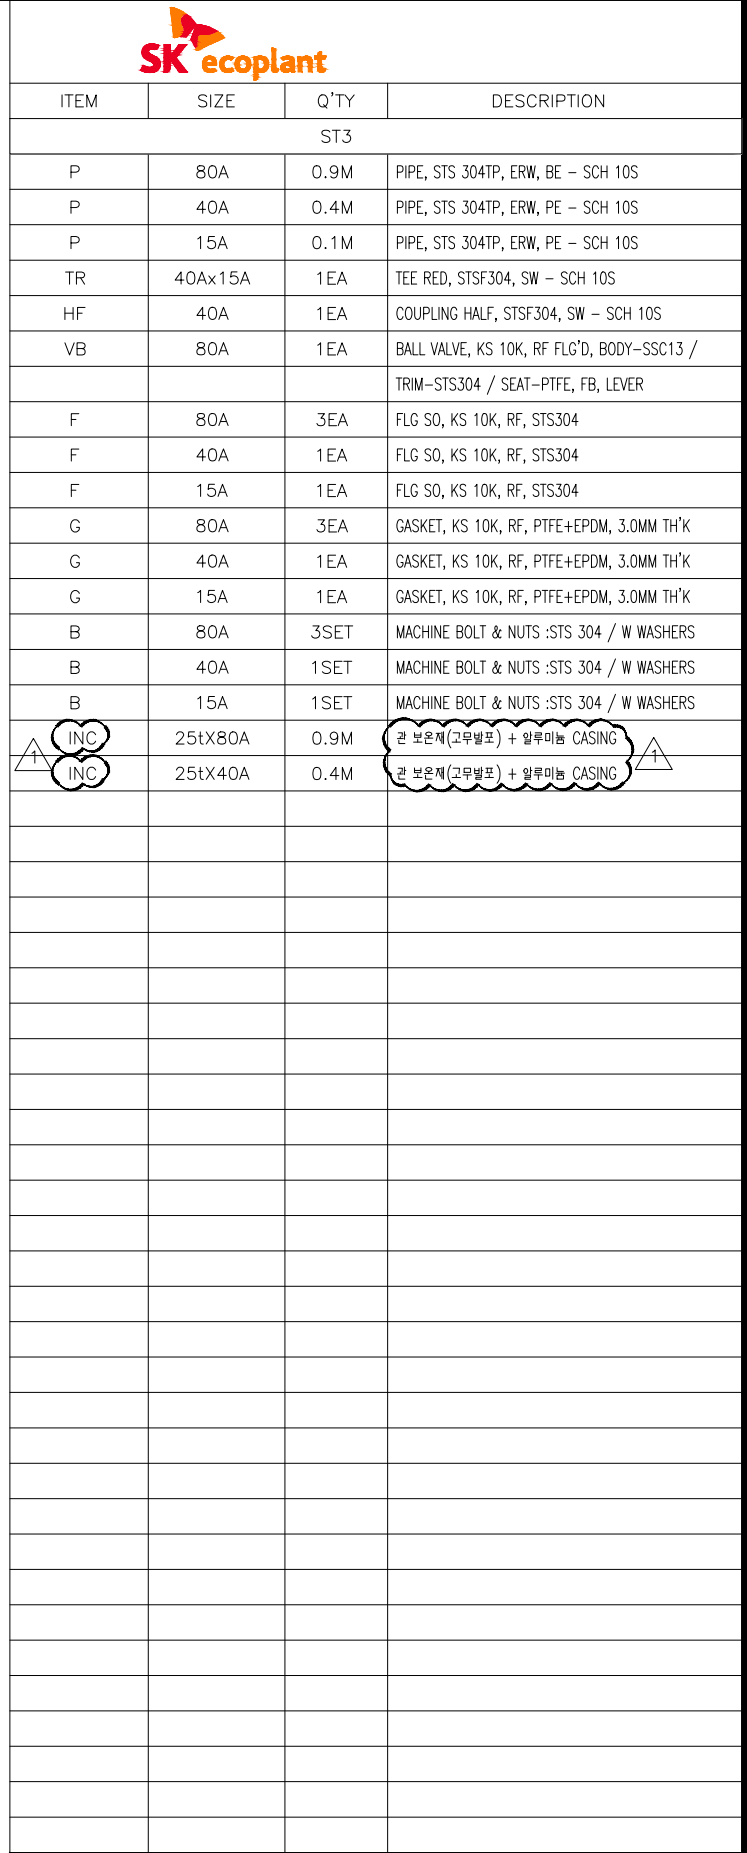

1. (*) FIELD ADJUST

CLIENT  1

경고 : 피고인 SK HYNIX의 기밀비밀 자료로서, 어떠한 경우에도 목적 외 사용, 복제, 제3자에게 공개, 누설 또는 기타 방법으로 유출할 수 없으며, 회사 내부자의 사생활이나 영업 비밀에 관한 정보 등 법령상 기업에 대한 기밀사항으로서 유출 시 피해가 발생할 경우 영업자에게 민/형사상 책임을 요구할 수 있음

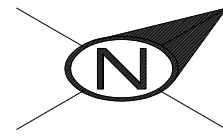

1. (*) FIELD ADJUST

CLIENT  2

경고 : 본 도면은 SK HYNIX의 기밀비밀 자료로서, 어떠한 경우에도 목적 외 사용, 복제, 제3자에게 공개, 누설 및 유출할 수 없으며, 회사는 유포자의 불법 사용으로 피해가 발생할 경우 유포자에게 민/형사상 책임을 요구할 수 있음.