


DRAWING LIST FOR TEST PACKAGE

PROJECT NO.: 22328D

PROJECT TITLE : M15X Ph2 Project

CAOH2-549

No	PKG No	UNIT	LINE NUMBER			P&ID		REMARK
			ISO DRAWING No	SHEET	REV	P&ID No	REV	
1	549	RFA	80A-CAOH2-ST3-E-6541-01	1 OF 1	1	CJ-M15W14-PR-A20-000142	1A	
2	549	RFA	OD90-CAOH2-PV2-E-6585-01	1 OF 1	1	CJ-M15W14-PR-A20-000107	1A	

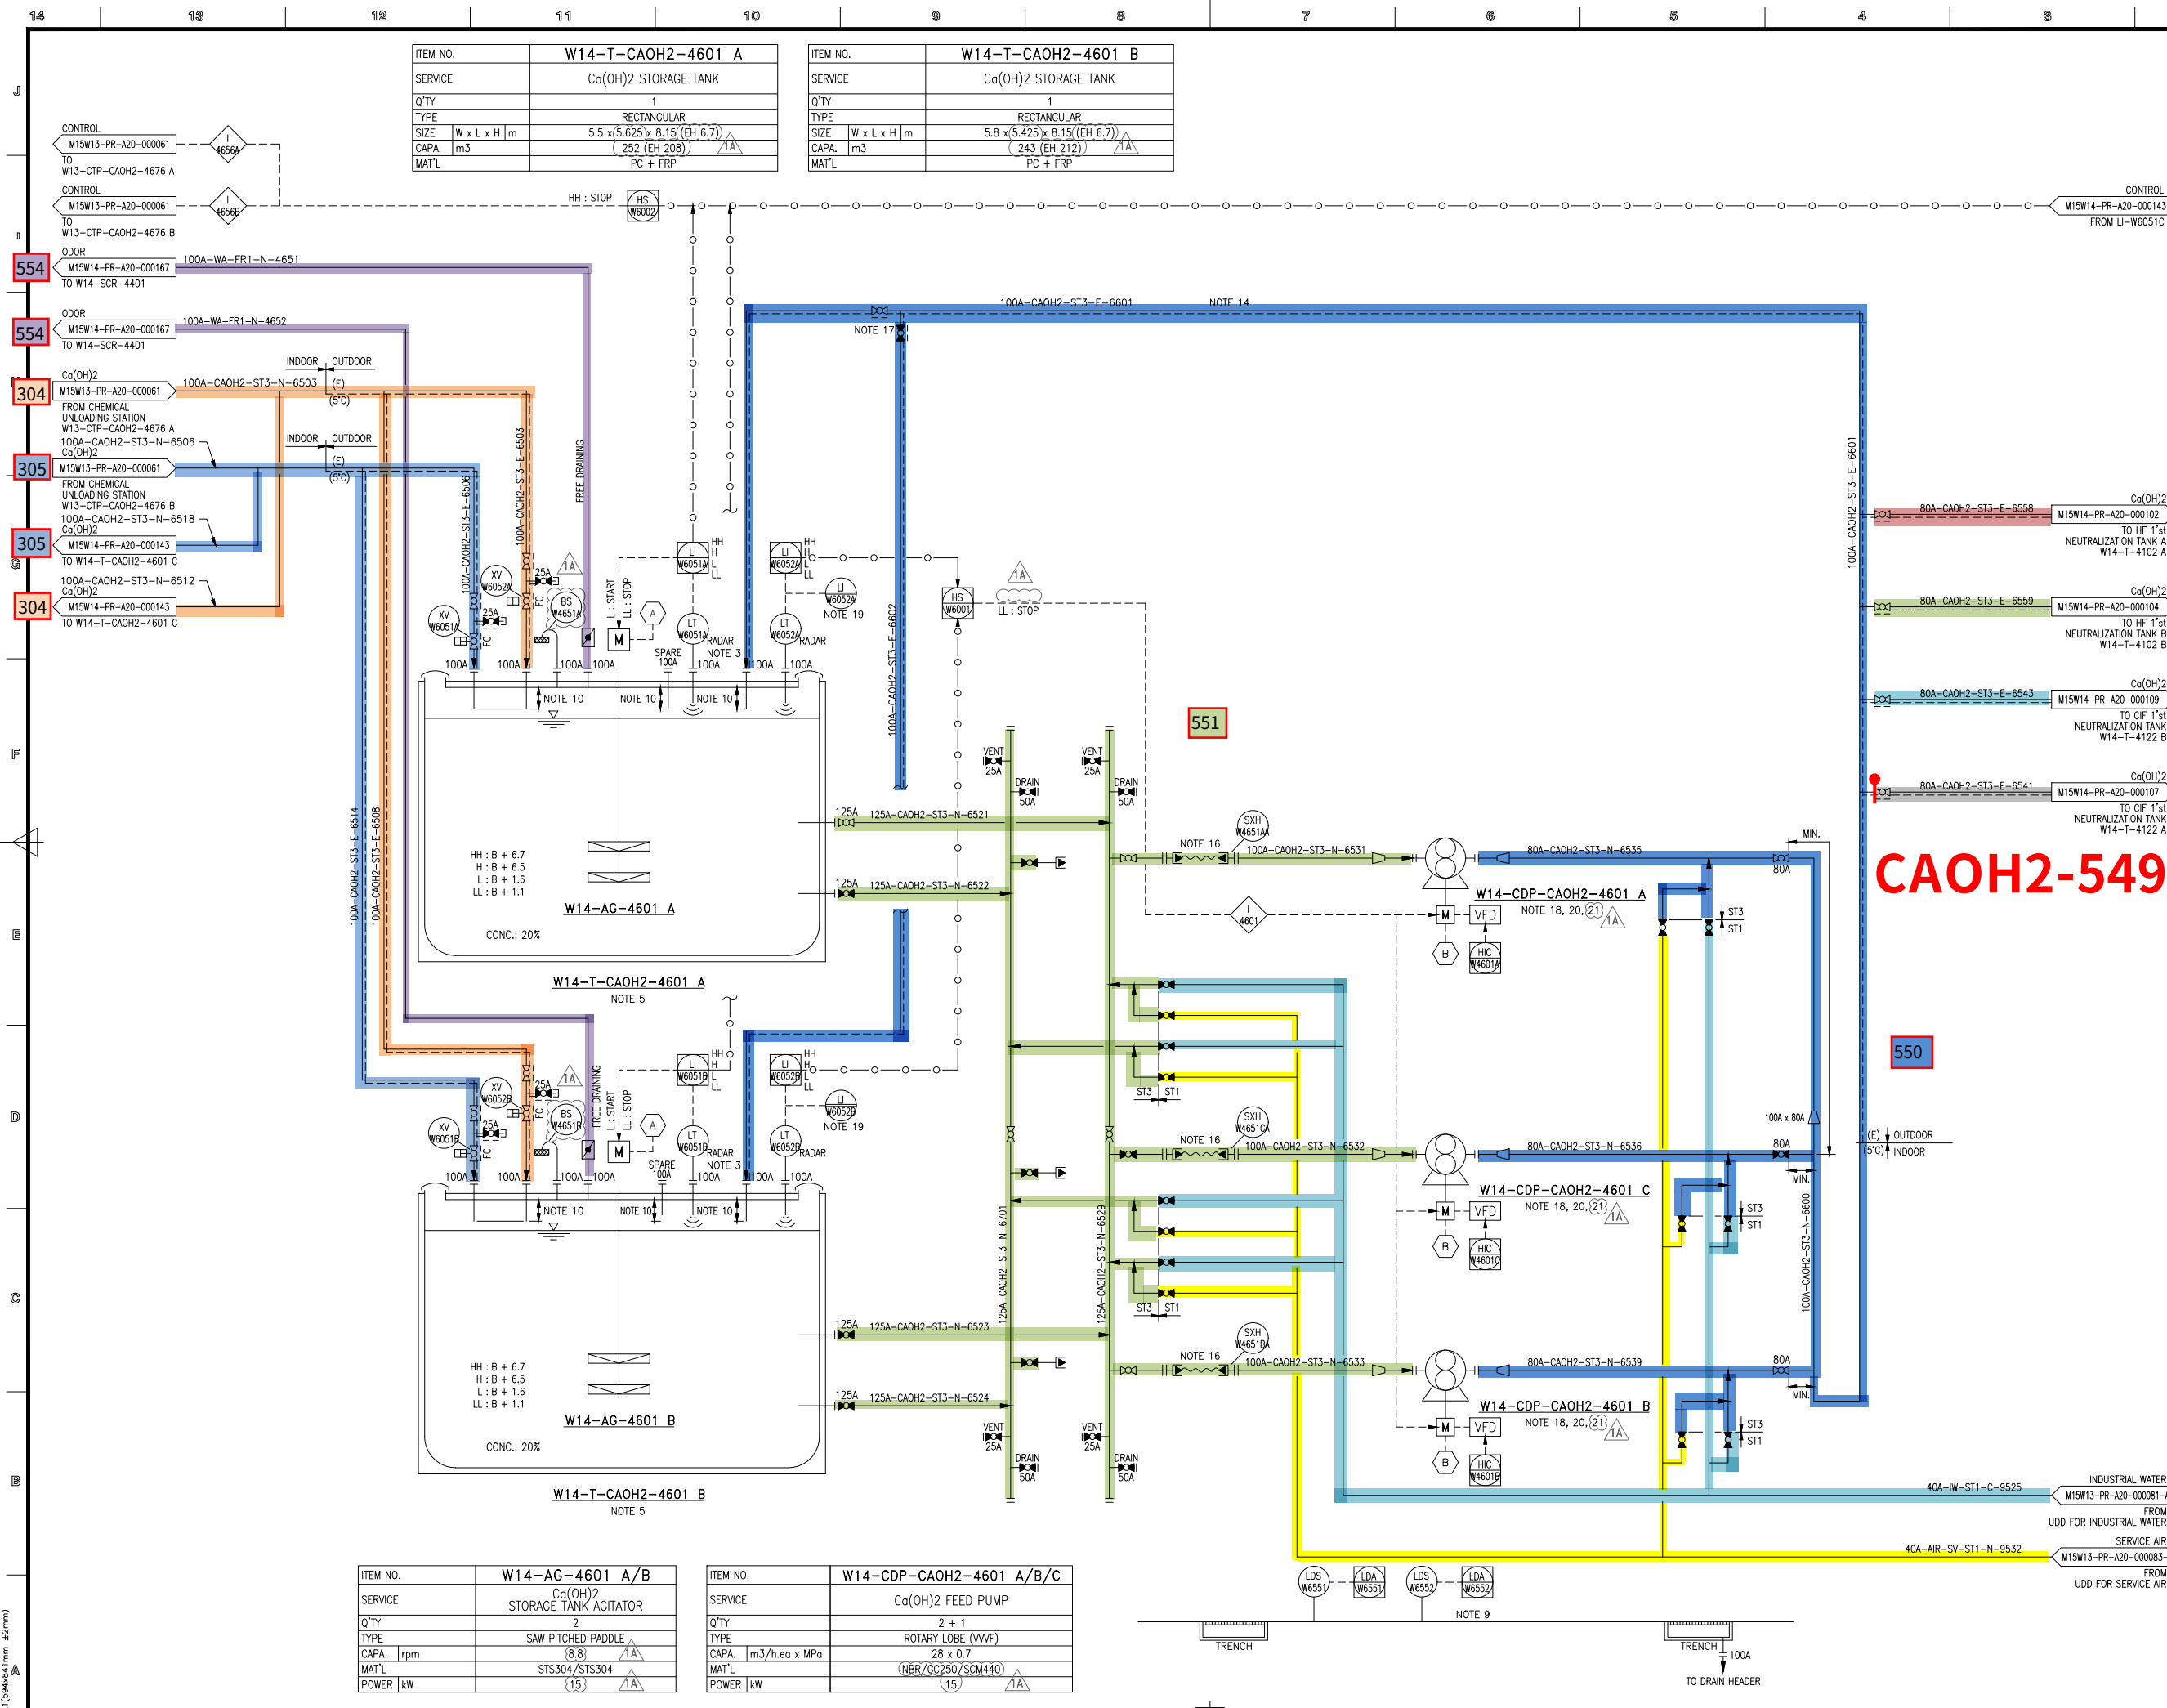

대외비

KEY PLAN (5F)

NOTE

1. CaOH2 배관의 ELBOW 부분은 FLANGE 설치할 것.

2. 2m 이상 높은 곳에 설치된 밸브는 CHAIN VALVE 또는 PLATFORM 구성할 것.

3. CHEMICAL UNLOADING STATION에서 LEVEL을 볼 수 있도록 한다.

4. P&ID에 표기된 모든 ELECTRIC POWER는 VENDOR PRINT 참조 후 작성할 것.

5. 5층에 설치할 것.

6. 약품종류에 따라 LINE 색상을 구분하여야 한다.

7. 운전 시 CLOSE 되는 배관에는 LOTO 설치.

8. AGITATOR MAT'L 표기 : SHAFT/BLADE

9. CHEMICAL STORAGE TANK CURB 및 PUMP AREA에서 발생되는 DRAIN은 인근의 TRENCH로 집수되어, DRAIN HEADER로 이송된다.

11. MANHOLE : 2개 이상 설치한다.

12. INTERLOCK NO. 1-4601 (W14-CDP-CAOH2-4601 A/B/C AUTO STOP) : REMOTE STATUS#M W14-T-CAOH2-4601 A/B LEVEL (LI-W6052A/B) LOW LOW STOP.

13. INTERLOCK NO. 1-4656A/B (W13-CTP-CAOH2-4676 A/B AUTO STOP) : REMOTE STATUS#M W14-T-CAOH2-4601 A/B/C LEVEL (LI-W6051A/B/C) HIGH HIGH STOP.

14. RINGMAN LINE SCHEMATIC

SCHEMATIC DRAWING

15. 내부 FRP LINING TANK의 SLEEVE는 SUS304 + FRP LINING 적용.

16. 기계적 VENDOR LOOSE PART 공급.

17. 운전중 Ca(OH)2 TANK A/B RETURN VALVE 2ea 중 1ea는 반드시 OPEN 되어있어야 한다.

18. INTERNAL PSV 설치 할 것.

19. 5층 소액의 주입펌프 인근에 TANK LEVEL 확인 가능하도록 LOCAL PANEL 설치.

20. 소액의 주입 펌프 AREA에는 비산 방지막을 설치한다.

21. INTERNAL PSV SET PRESSURE : 0.8 Mpa(g)

REV.	DESCRIPTION	DATE
1A	REVISED AFC	25.08.14
1	REVISED AFC	25.01.17
0	APPROVAL FOR CONSTRUCTION	24.09.30

수정

REV.

설명

DESCRIPTION

날짜

DATE

제 도

DRAWN BY

이 인 학

검 토

CHECKED BY

한 진 희

승 인

APPROVED BY

박 동 영

제 작 사

SK 에코플랜트

공 사 명

PROJECT TITLE

M15X Ph4 WWT Project

WG. TITLE

PIPING & INSTRUMENT DIAGRAM

Ca(OH)2 STORAGE TANK & FEED PUMP (1/2)

속 측

SCALE

NONE

날 짜

DATE

2025. 08. 14

PROJECT NO.

22330D

REV.

A

도면번호

SHEET NO.

CJ-M15W14-PR-A20-000142

1A


[illegible]

1

* PIPE : P/P1	* 90° ELBOW : E90	* 45° ELBOW : E45	* TEE : T	* RED.TEE : TR	* STUB-IN : STU	* REINFORCING PAD : RP	* CON.RED : RC	* ECC.RED : RE	* CON.SWAGE : RCS/RCS1	* ECC.SWAGE : RES/RES1	* NIPPLE : NP/NP1/NP2	* CAP : CAP/CAP1	* PLUG : PLG	* FULL COUPLING : FC	* HALF COUPLING : HF/HF1
* STUB-IN : STU	* SOCKET(HDPE/PVC) : SC	* SADDLE(HDPE) : SD	* FLANGE : F/F1	* GASKET : G/G1/G2	* BOLT & NUT : B/B1	* BLIND FLANGE : FB/FB1	* GATE VA. : VG/VG1/VG2	* BALL VA. : VB/VBLO/VB1/VB1LO/VB2/VB2LO	* BUTTERFLY VA. : VF/VF4	* CHECK VA. : VC/VC1/VC2/VC3/VC4/VC5/VC6/VC7					
* GLOBE VA. : VL/VL1/VL2	* DIAPHRAGM VA. : VD/VDLO	* DAMPER : VP	* QUICK COUPLING : SQC	* FLEXIBLE JOINT(STEEL) : FLXB	* FLEXIBLE JOINT(RUBBER) : FLXR	* FLEXIBLE JOINT(STEEL PTFE LINED) : FLXL	* FLEXIBLE HOSE : FLXH	* STEAM TRAP : ST	* SPRAY NOZZLE : SPN	* EMERGENCY SHOWER : SSH					
* STRAINER(Y-TYPE) : YSTR	* STRAINER(T-TYPE) : TSTR	* STRAINER(BUCKET-TYPE) : BSTR	* ANCHOR PLATE : STOP	* BIRD SCREEN : BS	* ISOLATION KIT : IK	* UNLOADING BOX : UB	* AIR TRAP : AT	* LOTO : LOTO	* SIGHT GLASS : SG	* PRESSURE GAUGE : PG	* SHILED : SH	* SPECIAL BOLT & NUT : BL/BL1			

INSULATION	CODE	E	CONDITION	PRESS. (kg/cm2g)	TEMP. (°C)	AREA W14							CONTRACTOR 	PROJECT NAME		
	THICK.	25	DESIGN	8	60	UNIT RFA								M15X Ph4 Project		
			OPERATING	7.2	AMB	REF. PLAN DWG. CJ-M15W14-PI-A30-R10002-B		25.03.31	REVISED AS MARKED	황래중	안남후	박동영	COMMODITY	CAOH2	JOB NO.	
						REF. P & ID CJ-M15W14-PR-A20-000107		25.01.24	APPROVED FOR CONSTRUCTION	황래중	안남후	박동영			22330D	
						REV. NO.	DATE	DESCRIPTION	BY	CHK	APP'D	LINE NO.	80A-CAOH2-ST3-E-6541	SH'T NO. 01 / 01	REV. 1	

경고 : 본 도면은 SK HYNIX의 기밀비밀 자료로서, 어떠한 경우에도 목적 외 사용, 복제, 제3자에게 공개, 누설 및 유출할 수 없으며, 회사는 유도자의 불법 사용으로 피해가 발생할 경우 유도자에게 민/형사상 책임을 요구할 수 있음

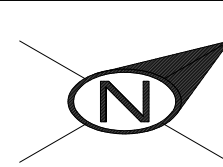

CLIENT		 2	
CONTRACTOR 		PROJECT NAME	
		M15X Ph4 Project	
영	COMMODITY	JOB NO.	
	CAOH2	22330D	
영	LINE NO.	SH'T NO.	REV.
D	0D90-CAOH2-PV2-E-6585	01 / 01	1

정답: ① SK HYNIX의 기업비밀 자료로서, 어떠한 경우에도 제3자에게 공개, 누설 및 유출할 수 없으며, 회사나 유도자의 내부 사정으로 피해가 발생할 경우 유도자에게 민/형사상 책임을 요구할 수 있음