


DRAWING LIST FOR TEST PACKAGE

CAOH2-550

PROJECT NO.: 22328D

PROJECT TITLE : M15X Ph2 Project

No	PKG No	UNIT	LINE NUMBER			P&ID		REMARK
			ISO DRAWING No	SHEET	REV	P&ID No	REV	
1	550	5FA	80A-CAOH2-ST3-N-6535-01	1 OF 1	0	CJ-M15W14-PR-A20-000142	1A	
2	550	5FA	80A-CAOH2-ST3-N-6536-01	1 OF 1	0	CJ-M15W14-PR-A20-000142	1A	
3	550	5FA	80A-CAOH2-ST3-N-6539-01	1 OF 1	0	CJ-M15W14-PR-A20-000142	1A	
4	550	5FA	100A-CAOH2-ST3-N-6600-01	1 OF 1	0	CJ-M15W14-PR-A20-000142	1A	
5	550	5FA	100A-CAOH2-ST3-N-6601-01	1 OF 1	0	CJ-M15W14-PR-A20-000142	1A	
6	550	RFA	100A-CAOH2-ST3-E-6601-01	1 OF 3	1	CJ-M15W14-PR-A20-000142	1A	
7	550	RFA	100A-CAOH2-ST3-E-6601-02	2 OF 3	1	CJ-M15W14-PR-A20-000142	1A	
8	550	RFA	100A-CAOH2-ST3-E-6601-03	3 OF 3	1	CJ-M15W14-PR-A20-000142	1A	
9	550	RFA	100A-CAOH2-ST3-E-6602-01	1 OF 1	1	CJ-M15W14-PR-A20-000142	1A	
10	550	RFA	80A-CAOH2-ST3-E-6541-01	1 OF 1	0	CJ-M15W14-PR-A20-000142	1A	
11	550	RFA	80A-CAOH2-ST3-E-6543-01	1 OF 1	0	CJ-M15W14-PR-A20-000142	1A	
12	550	RFA	80A-CAOH2-ST3-E-6558-01	1 OF 1	0	CJ-M15W14-PR-A20-000142	1A	
13	550	RFA	80A-CAOH2-ST3-E-6559-01	1 OF 1	0	CJ-M15W14-PR-A20-000142	1A	

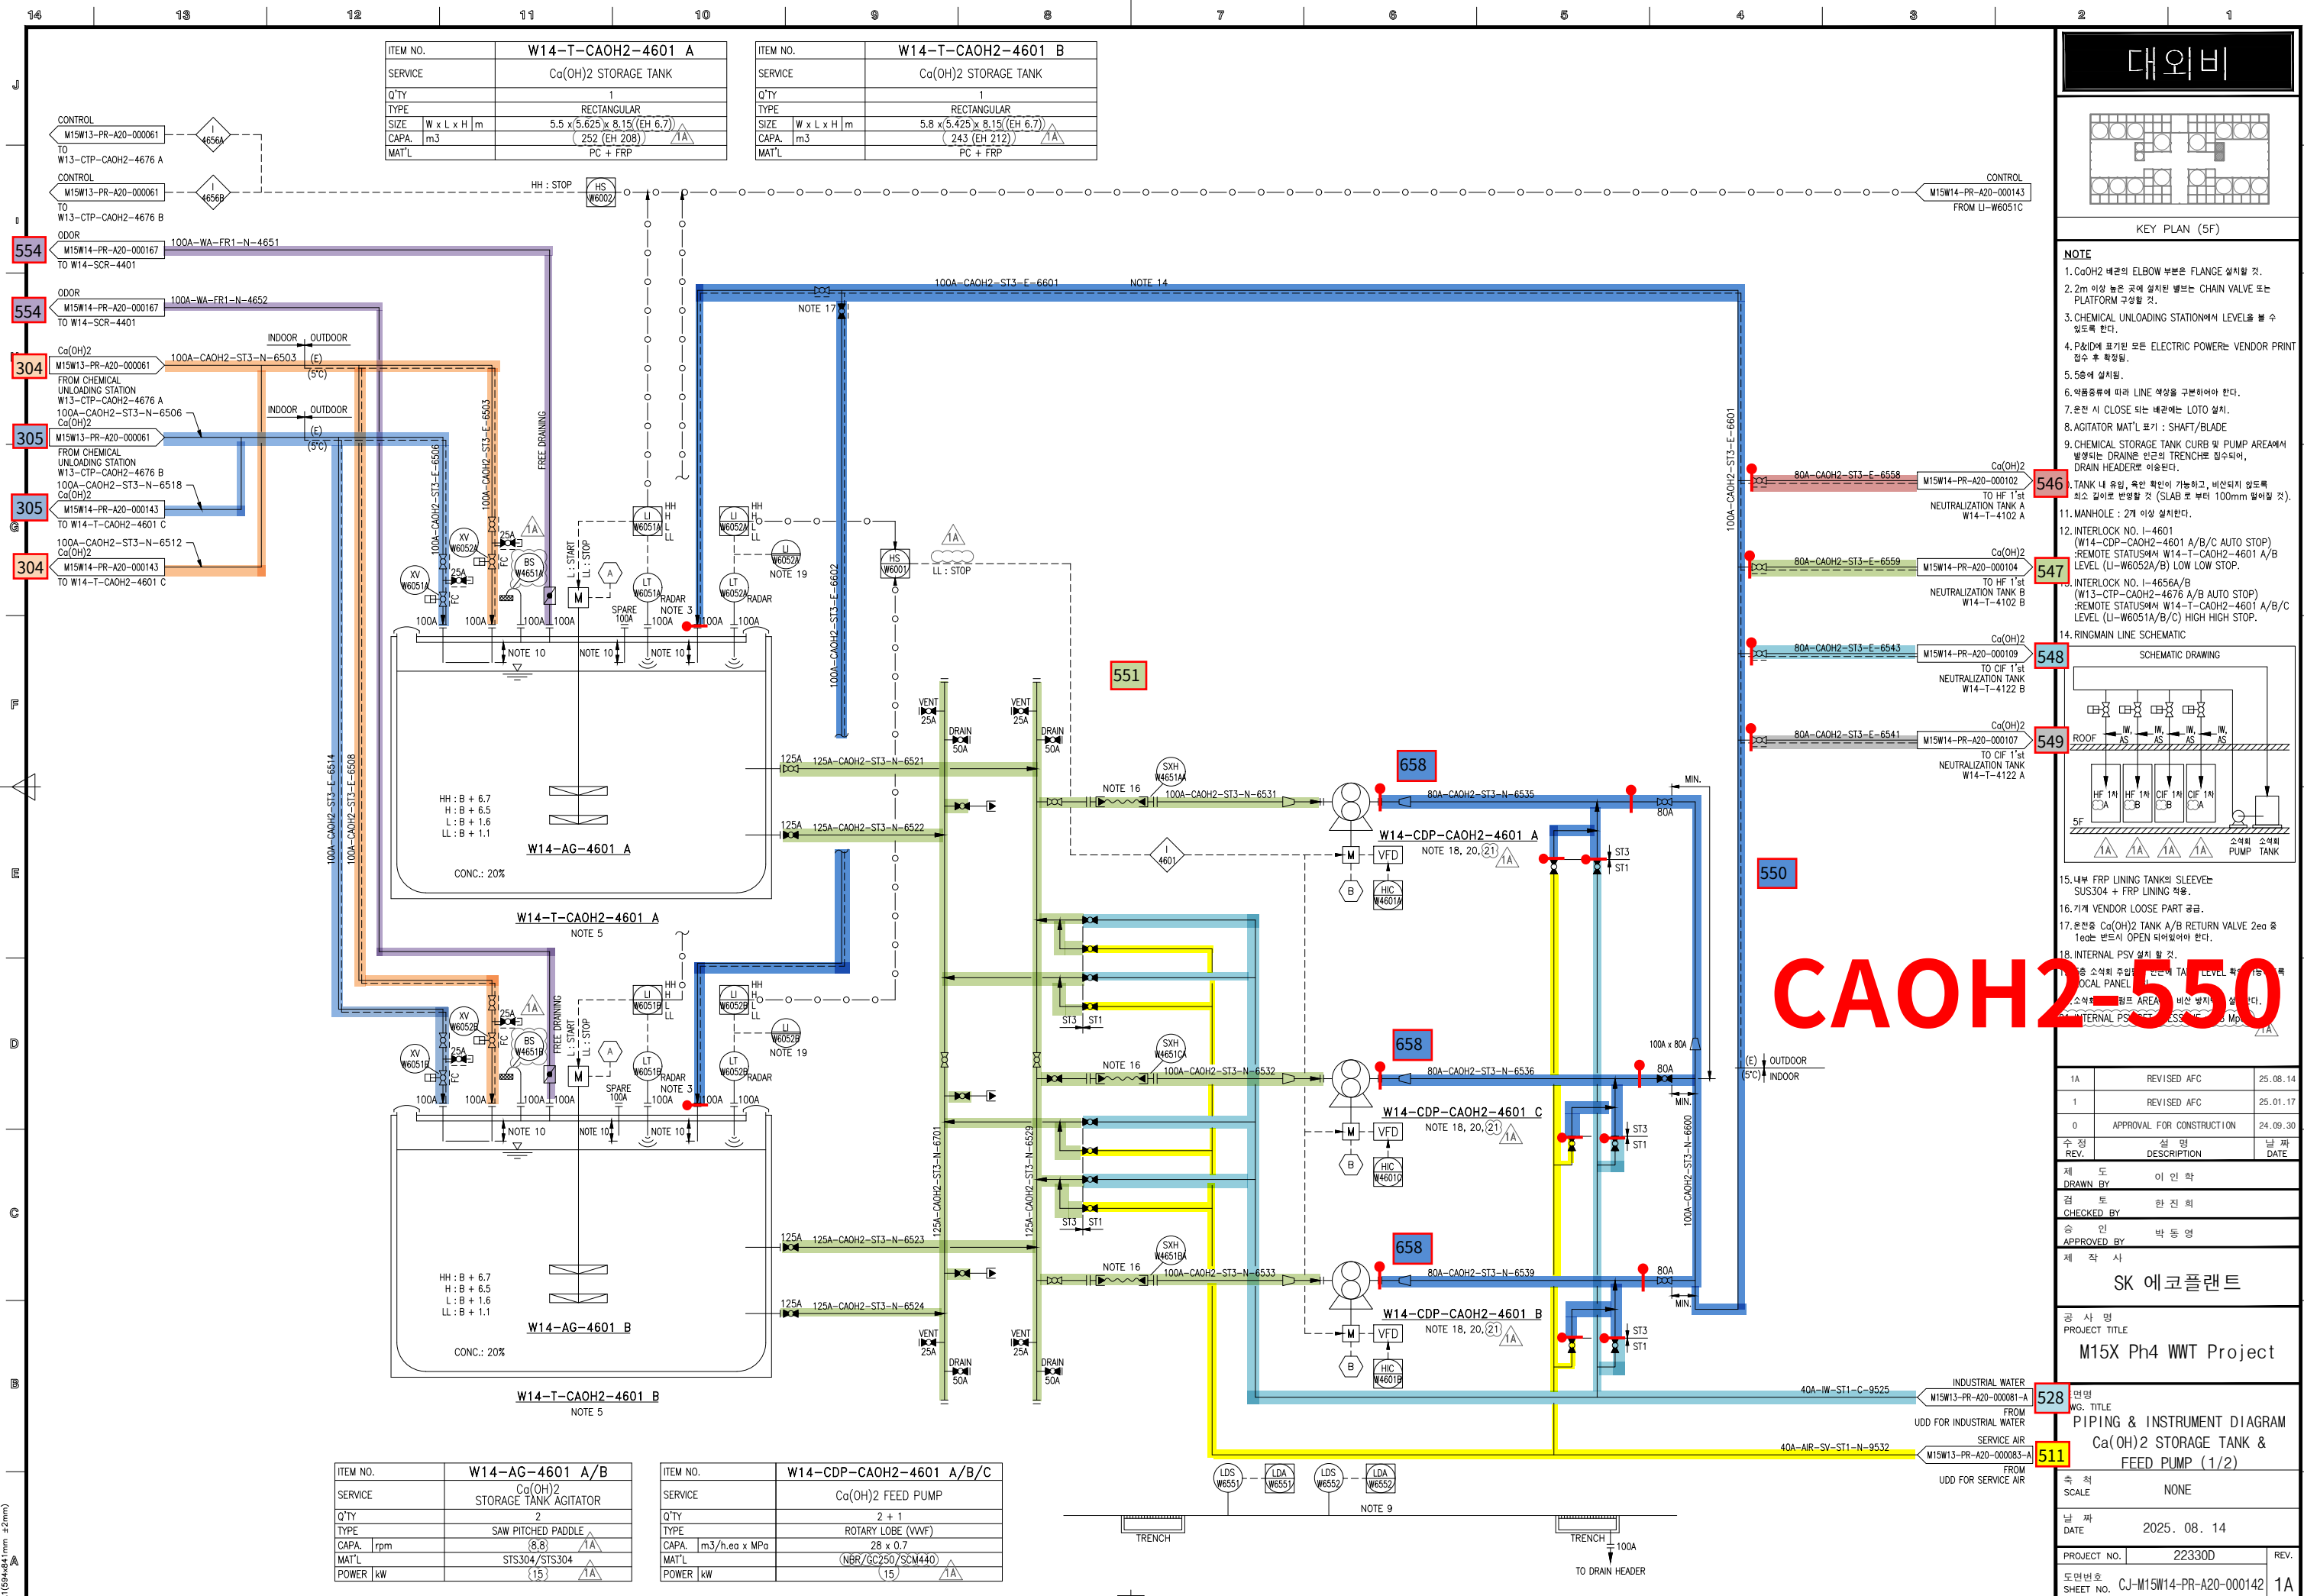

대외비

KEY PLAN (5F)

NOTE

- CaOH2 배관의 ELBOW 부분은 FLANGE 설치할 것.
- 2m 이상 높은 곳에 설치된 밸브는 CHAIN VALVE 또는 PLATFORM 구성할 것.
- CHEMICAL UNLOADING STATION에서 LEVEL을 볼 수 있도록 한다.
- P&ID에 표기된 모든 ELECTRIC POWER는 VENDOR PRINT 참조 후 작성할 것.
- 5층에 설치할 것.
- 약품종류에 따라 LINE 색상을 구분하여야 한다.
- 훈련 시 CLOSE 되는 배관에는 LOTO 설치.
- AGITATOR MAT'L 표기 : SHAFT/BLADE
- CHEMICAL STORAGE TANK CURB 및 PUMP AREA에서 발생되는 DRAIN은 인근의 TRENCH로 집수되어, DRAIN HEADER로 이송된다.
- TANK 내 유량, 폭안 확인이 가능하고, 비산되지 않도록 최소 길이로 반영할 것 (SLAB로부터 100mm 떨어진 것).
- MANHOLE : 2개 이상 설치한다.
- INTERLOCK NO. 1-4601 (W14-CDP-CAOH2-4601 A/B/C AUTO STOP) : REMOTE STATUS#M W14-T-CAOH2-4601 A/B LEVEL (LI-W6052A/B) LOW LOW STOP.
- INTERLOCK NO. 1-4656A/B (W13-CTP-CAOH2-4676 A/B AUTO STOP) : REMOTE STATUS#M W14-T-CAOH2-4601 A/B/C LEVEL (LI-W6051A/B/C) HIGH HIGH STOP.
- RINGMAN LINE SCHEMATIC

SCHEMATIC DRAWING

15. 내부 FRP LINING TANK의 SLEEVE는 SUS304 + FRP LINING 적용.

16. 기계 VENDOR LOOSE PART 공표.

17. 훈련용 Ca(OH)2 TANK A/B RETURN VALVE 2ea 중 1ea는 반드시 OPEN 되어있어야 한다.

18. INTERNAL PSV 설치 할 것.

19. 5층 소액의 주입에 따른 TANK LEVEL 확인 가능 LOCAL PANEL

20. 소액의 원료 AREA 비산 방지 설치 할 것.

21. INTERNAL PSV 설치 할 것.

1A	REVISED AFC	25.08.14
1	REVISED AFC	25.01.17
0	APPROVAL FOR CONSTRUCTION	24.09.30
수정	실명	날짜
REV.	DESCRIPTION	DATE

제 도 이 인 학

검 토 한 진 회

CHECKED BY

승 인 박 동 영

APPROVED BY

제 작 사

SK 에코플랜트

공 사 명

PROJECT TITLE

M15X Ph4 WWT Project

면명

WG. TITLE

PIPING & INSTRUMENT DIAGRAM

Ca(OH)2 STORAGE TANK & FEED PUMP (1/2)

속 측 NONE

SCALE

날 짜 2025. 08. 14

DATE


PROJECT NO. 22330D

도면번호

SHEET NO. CJ-M15W14-PR-A20-000142


REV. 1A

C:\Users\WTOP\Desktop\WP&ID251013W[M15X Ph-4 for 인허가]CAD FILE_0910WCJ-M15W14-PR-A20-000142 R1 P&ID FOR Ca(OH)

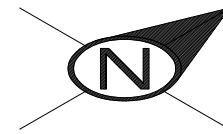


CLIENT  1

경고 : 본 도면은 SK HYNIX의 기업비밀 자료로서, 어떠한 경우에도 목적 외 사용, 복제, 제3자에게 공개, 누설 및 유출할 수 없으며, 회사는 유포자의 불법 사용으로 피해가 발생할 경우 유포자에게 민/형사상 책임을 요구할 수 있음

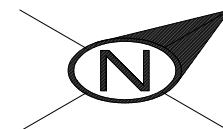[illegible]

CLIENT			
		2	
CONTRACTOR		PROJECT NAME	
		M15X Ph4 Project	
COMMODITY		JOB NO.	
CAOH2		22330D	
LINE NO.	80A-CAOH2-ST3-N-6536	SH'T NO.	REV.
		01 / 01	0

* PIPE : P/P1 * 90° ELBOW : E90 * 45° ELBOW : E45 * TEE : T * RED.TEE : TR * STUB-IN : STU * REINFORCING PAD : RP * CON.RED : RC * ECC.RED : RE * CON.SWAGE : RCS/RCS1 * ECC.SWAGE : RES/RES1 * NIPPLE : NP/NP1/NP2 * CAP : CAP/CAP1 * PLUG : PLG * FULL COUPLING : FC * HALF COUPLING : HF/HF1 * STUB-IN : STU * SOCKET(HDPE/PVC) : SC * SADDLE(HDPE) : SD * FLANGE : F/F1 * GASKET : G/G1/G2 * BOLT & NUT : B/B1 * BLIND FLANGE : FB/FB1 * GATE VA. : VG/VG1/VG2 * BALL VA. : VB/VBLO/VB1/VB1LO/VB2/VB2LO * BUTTERFLY VA. : VF/VF4 * CHECK VA. : VC/VC1/VC2/VC3/VC4/VC5/VC6/VC7 * GLOBE VA. : VL/VL1/VL2 * DIAPHRAGM VA. : VD/VDLO * DAMPER : VP * QUICK COUPLING : SQC * FLEXIBLE JOINT(STEEL) : FLXB * FLEXIBLE JOINT(RUBBER) : FLXR * FLEXIBLE JOINT(STEEL PTFE LINED) : FLXL * FLEXIBLE HOSE : FLXH * STEAM TRAP : ST * SPRAY NOZZLE : SPN * EMERGENCY SHOWER : SSH * STRAINER(Y-TYPE) : YSTR * STRAINER(T-TYPE) : TSTR * STRAINER(BUCKET-TYPE) : BSTR * ANCHOR PLATE : STOP * BIRD SCREEN : BS * ISOLATION KIT : IK * UNLOADING BOX : UB * AIR TRAP : AT * LOTO : LOTO * SIGHT GLASS : SG * PRESSURE GAUGE : PG * SHILED : SH * SPECIAL BOLT & NUT : BL/BL1												
INSULATION	CODE	N	CONDITION	PRESS. (kg/cm2g)	TEMP. (°C)	AREA W14						
	THICK.	—	DESIGN	8	60	UNIT 5FA						
			OPERATING	7.2	AMB	REF. PLAN DWG. CJ-M15W14-PI-A30-050005-A	0	25.01.24	APPROVED FOR CONSTRUCTION	황래중	안남후	박동
						REF. P & ID CJ-M15W14-PR-A20-000142						
							REV. NO.	DATE	DESCRIPTION	BY	CHK	APR

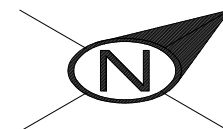[illegible]

CLIENT	 		3
CONTRACTOR	CAOH2	PROJECT NAME	M15X Ph4 Project
COMMODITY	22330D	JOB NO.	
LINE NO.	80A-CAOH2-ST3-N-6539	SH'T NO.	REV.
		01 / 01	0

* PIPE : P/P1 * 90° ELBOW : E90 * 45° ELBOW : E45 * TEE : T * RED.TEE : TR * STUB-IN : STU * REINFORCING PAD : RP * CON.RED : RC * ECC.RED : RE * CON.SWAGE : RCS/RCS1 * ECC.SWAGE : RES/RES1 * NIPPLE : NP/NP1/NP2 * CAP : CAP/CAP1 * PLUG : PLG * FULL COUPLING : FC * HALF COUPLING : HF/HF1 * STUB-IN : STU * SOCKET(HDPE/PVC) : SC * SADDLE(HDPE) : SD * FLANGE : F/F1 * GASKET : G/G1/G2 * BOLT & NUT : B/B1 * BLIND FLANGE : FB/FB1 * GATE VA. : VG/VG1/VG2 * BALL VA. : VB/VBLO/VB1/VB1LO/VB2/VB2LO * BUTTERFLY VA. : VF/VF4 * CHECK VA. : VC/VC1/VC2/VC3/VC4/VC5/VC6/VC7 * GLOBE VA. : VL/VL1/VL2 * DIAPHRAGM VA. : VD/VDLO * DAMPER : VP * QUICK COUPLING : SQC * FLEXIBLE JOINT(STEEL) : FLXB * FLEXIBLE JOINT(RUBBER) : FLXR * FLEXIBLE JOINT(STEEL PTFE LINED) : FLXL * FLEXIBLE HOSE : FLXH * STEAM TRAP : ST * SPRAY NOZZLE : SPN * EMERGENCY SHOWER : SSH * STRAINER(Y-TYPE) : YSTR * STRAINER(T-TYPE) : TSTR * STRAINER(BUCKET-TYPE) : BSTR * ANCHOR PLATE : STOP * BIRD SCREEN : BS * ISOLATION KIT : IK * UNLOADING BOX : UB * AIR TRAP : AT * LOTO : LOTO * SIGHT GLASS : SG * PRESSURE GAUGE : PG * SHILED : SH * SPECIAL BOLT & NUT : BL/BL1												
INSULATION	CODE	N	CONDITION	PRESS. (kg/cm2g)	TEMP. (°C)	AREA W14						
	THICK.	-	DESIGN	8	60	UNIT 5FA						
			OPERATING	7.2	AMB	REF. PLAN DWG. CJ-M15W14-PI-A30-050005-A		25.01.24	APPROVED FOR CONSTRUCTION	황래중	안남후	박동
						REF. P & ID CJ-M15W14-PR-A20-000142						
						REV. NO.	DATE	DESCRIPTION	BY	CHK	APP	


[illegible]

4


* PIPE : P/P1	* 90° ELBOW : E90	* 45° ELBOW : E45	* TEE : T	* RED.TEE : TR	* STUB-IN : STU	* REINFORCING PAD : RP	* CON.RED : RC	* ECC.RED : RE	* CON.SWAGE : RCS/RCS1	* ECC.SWAGE : RES/RES1	* NIPPLE : NP/NP1/NP2	* CAP : CAP/CAP1	* PLUG : PLG	* FULL COUPLING : FC	* HALF COUPLING : HF/HF1
* STUB-IN : STU	* SOCKET(HDPE/PVC) : SC	* SADDLE(HDPE) : SD	* FLANGE : F/F1	* GASKET : G/G1/G2	* BOLT & NUT : B/B1	* BLIND FLANGE : FB/FB1	* GATE VA. : VG/VG1/VG2	* BALL VA. : VB/VBLO/VB1/VB1O/VB2/VB2LO	* BUTTERFLY VA. : VF/VF4	* CHECK VA. : VC/VC1/VC2/VC3/VC4/VC5/VC6/VC7					
* GLOBE VA. : VL/VL1/VL2	* DIAPHRAGM VA. : VD/VDLO	* DAMPER : VP	* QUICK COUPLING : SQC	* FLEXIBLE JOINT(STEEL) : FLXB	* FLEXIBLE JOINT(RUBBER) : FLXR	* FLEXIBLE JOINT(STEEL PTFE LINED) : FLXL	* FLEXIBLE HOSE : FLXH	* STEAM TRAP : ST	* SPRAY NOZZLE : SPN	* EMERGENCY SHOWER : SSH					
* STRAINER(Y-TYPE) : YSTR	* STRAINER(T-TYPE) : TSTR	* STRAINER(BUCKET-TYPE) : BSTR	* ANCHOR PLATE : STOP	* BIRD SCREEN : BS	* ISOLATION KIT : IK	* UNLOADING BOX : UB	* AIR TRAP : AT	* LOTO : LOTO	* SIGHT GLASS : SG	* PRESSURE GAUGE : PG	* SHILED : SH	* SPECIAL BOLT & NUT : BL/BL1			

INSULATION	CODE	N	CONDITION	PRESS. (kg/cm2g)	TEMP. (°C)	AREA W14								CONTRACTOR		PROJECT NAME	
	THICK.	-	DESIGN	12.5	60	UNIT 5FA										M15X Ph4 Project	
			OPERATING	10	6	REF. PLAN DWG. CJ-M15W14-PI-A30-050005-A		25.01.24	APPROVED FOR CONSTRUCTION	황래중	안남후	박동영	COMMODITY		JOB NO.		
					REF. P & ID CJ-M15W14-PR-A20-000142	CAOH2							22330D				
							REV. NO.	DATE	DESCRIPTION	BY	CHK	APP'D	LINE NO.	100A-CAOH2-ST3-N-6600		SH'T NO. 01 / 01	REV. 0

정 : SK HYNIX의 기밀정보를 자료로서, 어떠한 주위에 도록 전제 없이 사용, 복제, 제3자에게 공개, 누설 또는 기타 방법으로 유출한 경우 응모자에게 민/형사상 책임을 물을 수 있는지를 확인하고자 하는지 여부를 묻는 질문입니다.

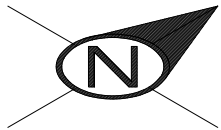

ITEM	SIZE	Q'TY	DESCRIPTION
ST3			
P	100A	21.3M	PIPE, STS 304TP, ERW, BE - SCH 10S
E90	100A	5EA	ELBOW 90 DEG LR, STS304, ERW, BE - SCH 10S
F	100A	19EA	FLG SO, KS 10K, RF, STS304
G	100A	9EA	GASKET, KS 10K, RF, PTFE+EPDM, 3.0MM TH'K
B	100A	9SET	MACHINE BOLT & NUTS :STS 304 / W WASHERS
SH	100A	4EA	SHIELD

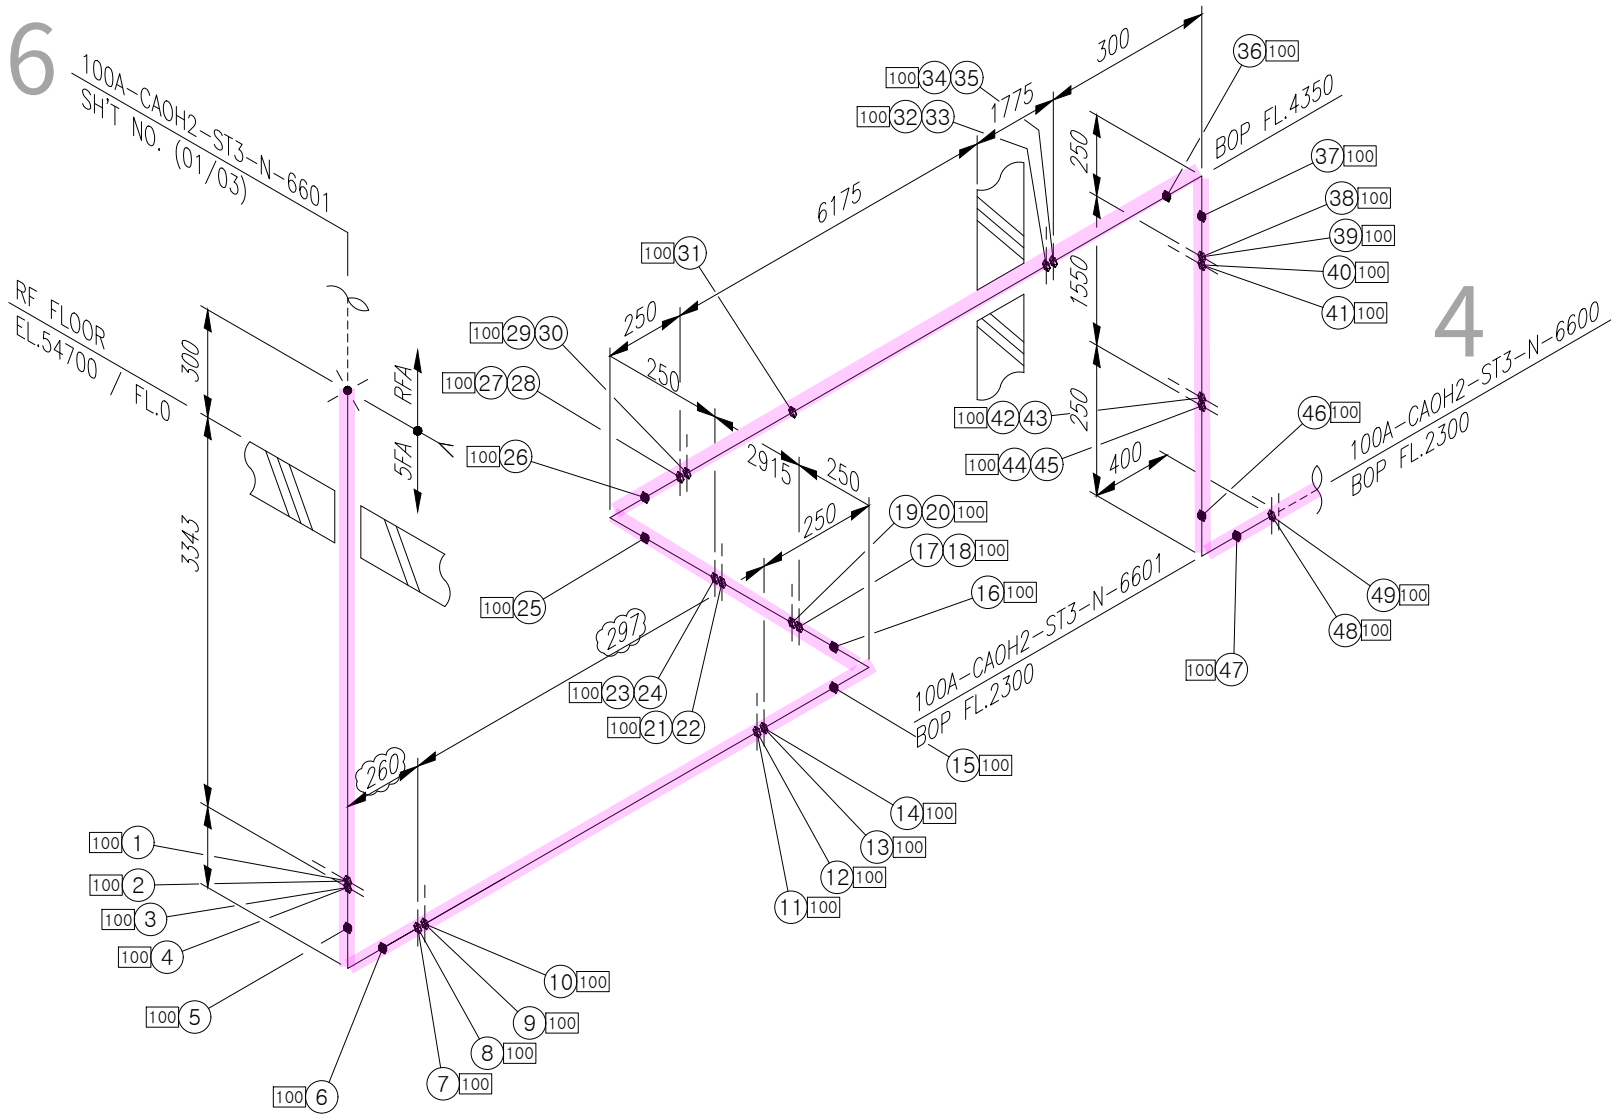

<NOTE>

1. (*) FIELD ADJUST

* PIPE : P/P1 * 90° ELBOW : E90 * 45° ELBOW : E45 * TEE : T * RED.TEE : TR * STUB-IN : STU * REINFORCING PAD : RP * CON.RED : RC * ECC.RED : RE * CON.SWAGE : RCS/RCS1 * ECC.SWAGE : RES/RES1 * NIPPLE : NP/NP1/NP2 * CAP : CAP/CAP1 * PLUG : PLG * FULL COUPLING : FC * HALF COUPLING : HF/HF1
* STUB-IN : STU * SOCKET(HDPE/PVC) : SC * SADDLE(HDPE) : SD * FLANGE : F/F1 * GASKET : G/G1/G2 * BOLT & NUT : B/B1 * BLIND FLANGE : FB/FB1 * GATE VA. : VG/VG1/VG2 * BALL VA. : VB/VBLO/VB1/VB1LO/VB2/VB2LO * BUTTERFLY VA. : VF/VF4 * CHECK VA. : VC/VC1/VC2/VC3/VC4/VC5/VC6/VC7
* GLOBE VA. : VL/VL1/VL2 * DIAPHRAGM VA. : VD/VDLO * DAMPER : VP * QUICK COUPLING : SQC * FLEXIBLE JOINT(STEEL) : FLXB * FLEXIBLE JOINT(RUBBER) : FLXR * FLEXIBLE JOINT(STEEL PTFE LINED) : FLXL * FLEXIBLE HOSE : FLXH * STEAM TRAP : ST * SPRAY NOZZLE : SPN * EMERGENCY SHOWER : SSH
* STRAINER(Y-TYPE) : YSTR * STRAINER(T-TYPE) : TSTR * STRAINER(BUCKET-TYPE) : BSTR * ANCHOR PLATE : STOP * BIRD SCREEN : BS * ISOLATION KIT : IK * UNLOADING BOX : UB * AIR TRAP : AT * LOTO : LOTO * SIGHT GLASS : SG * PRESSURE GAUGE : PG * SHILED : SH * SPECIAL BOLT & NUT : BL/BL1

CLIENT



5

CONTRACTOR



PROJECT NAME

M15X Ph4 Project

COMMODITY

CAOH2

JOB NO.

22330D

LINE NO.


100A-CAOH2-ST3-N-6601

SH'T NO.

01 / 01

REV.



0

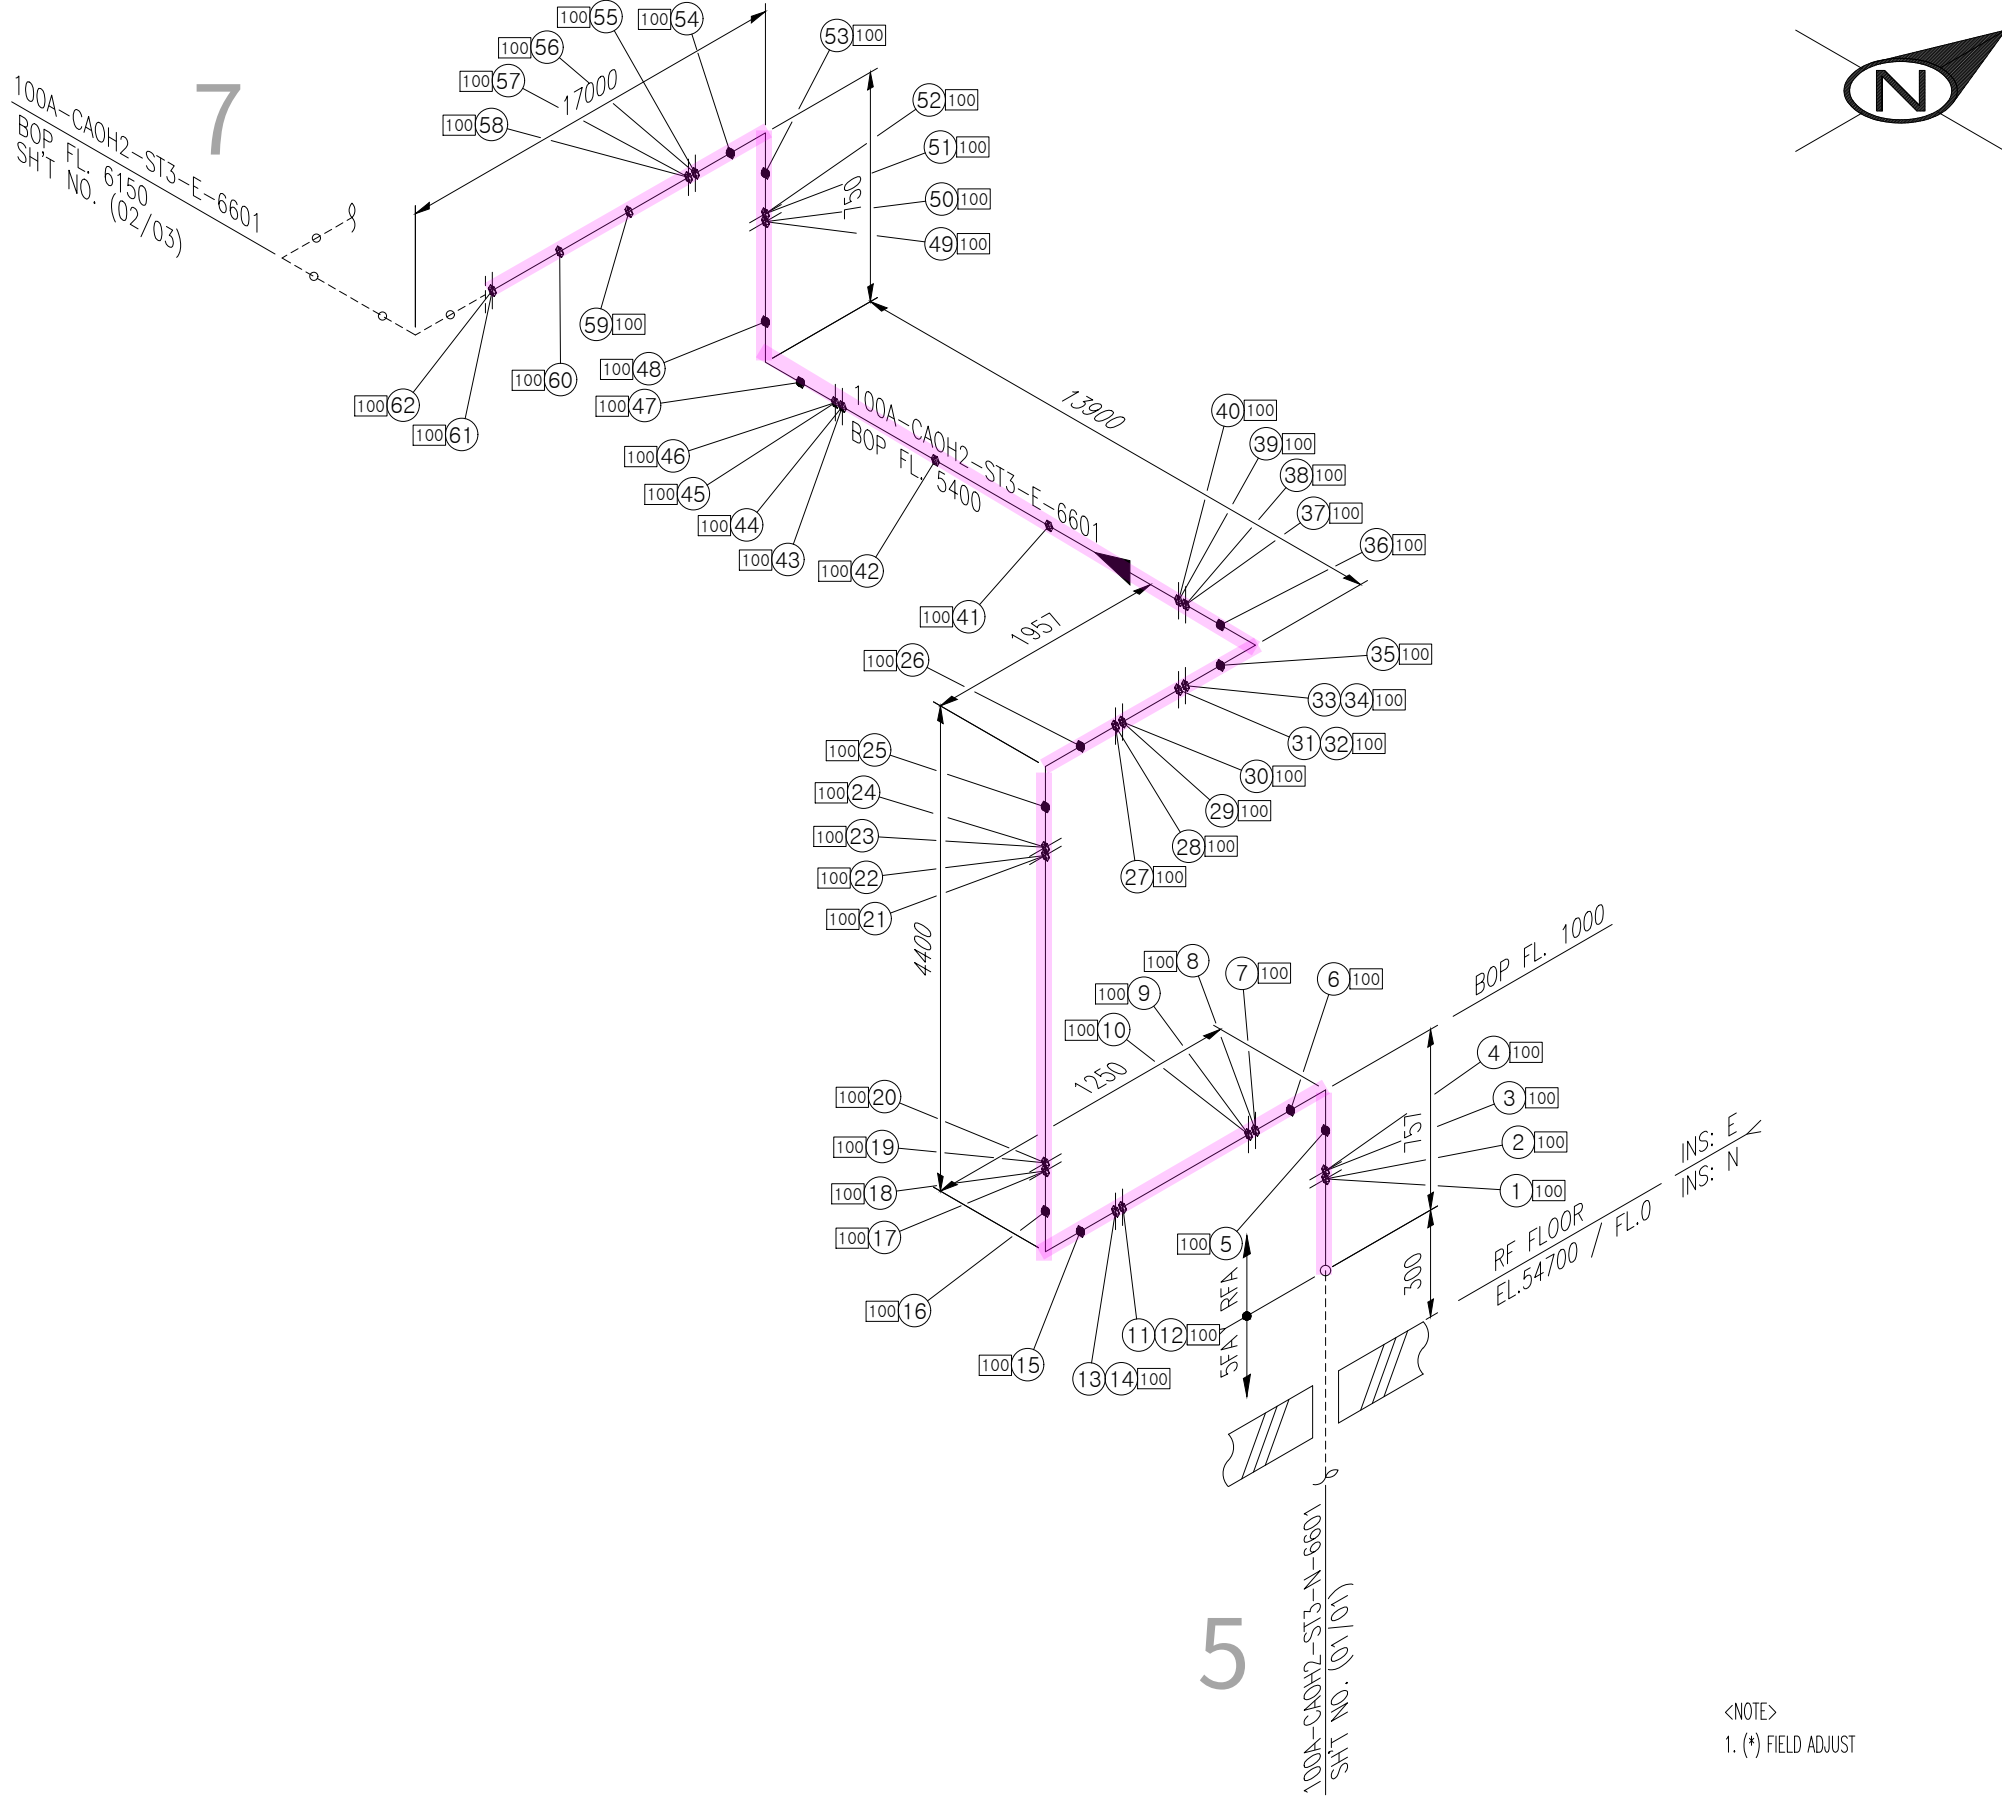

<NOTE>
1. (*) FIELD ADJUST

* PIPE : P/P1 * 90° ELBOW : E90 * 45° ELBOW : E45 * TEE : T * RED.TEE : TR * STUB-IN : STU * REINFORCING PAD : RP * CON.RED : RC * ECC.RED : RE * CON.SWAGE : RCS/RCS1 * ECC.SWAGE : RES/RES1 * NIPPLE : NP/NP1/NP2 * CAP : CAP/CAP1 * PLUG : PLG * FULL COUPLING : FC * HALF COUPLING : HF/HF1
* STUB-IN : STU * SOCKET(HDPE/PVC) : SC * SADDLE(HDPE) : SD * FLANGE : F/F1 * GASKET : G/G1/G2 * BOLT & NUT : B/B1 * BLIND FLANGE : FB/FB1 * GATE VA. : VG/VG1/VG2 * BALL VA. : VB/VBLO/VB1/VB1LO/VB2/VB2LO * BUTTERFLY VA. : VF/VF4 * CHECK VA. : VC/VC1/VC2/VC3/VC4/VC5/VC6/VC7
* GLOBE VA. : VL/VL1/VL2 * DIAPHRAGM VA. : VD/VDLO * DAMPER : VP * QUICK COUPLING : SQC * FLEXIBLE JOINT(STEEL) : FLXB * FLEXIBLE JOINT(RUBBER) : FLXR * FLEXIBLE JOINT(STEEL PTFE LINED) : FLXL * FLEXIBLE HOSE : FLXH * STEAM TRAP : ST * SPRAY NOZZLE : SPN * EMERGENCY SHOWER : SSH
* STRAINER(Y-TYPE) : YSTR * STRAINER(T-TYPE) : TSTR * STRAINER(BUCKET-TYPE) : BSTR * ANCHOR PLATE : STOP * BIRD SCREEN : BS * ISOLATION KIT : IK * UNLOADING BOX : UB * AIR TRAP : AT * LOTO : LOTO * SIGHT GLASS : SG * PRESSURE GAUGE : PG * SHILED : SH * SPECIAL BOLT & NUT : BL/BL1

INSULATION	CODE	E	CONDITION	PRESS. (kg/cm2g)	TEMP. (°C)	AREA	W14							CONTRACTOR 	PROJECT NAME		
	THICK.	25	DESIGN	12.5	60	UNIT	RFA								M15X Ph4 Project		
			OPERATING	10	6	REF. PLAN DWG. CJ-M15W14-PI-A30-R10008-A			25.03.31	REVISED AS MARKED	황래중	안남후	박동영	COMMODITY	CAOH2	JOB NO.	
						REF. P & ID CJ-M15W14-PR-A20-000142			25.01.24	APPROVED FOR CONSTRUCTION	황래중	안남후	박동영	LINE NO.	100A-CAOH2-ST3-E-6601	SH'T NO. 01 / 03	REV. 1
								REV. NO.	DATE	DESCRIPTION	BY	CHK	APP'D				

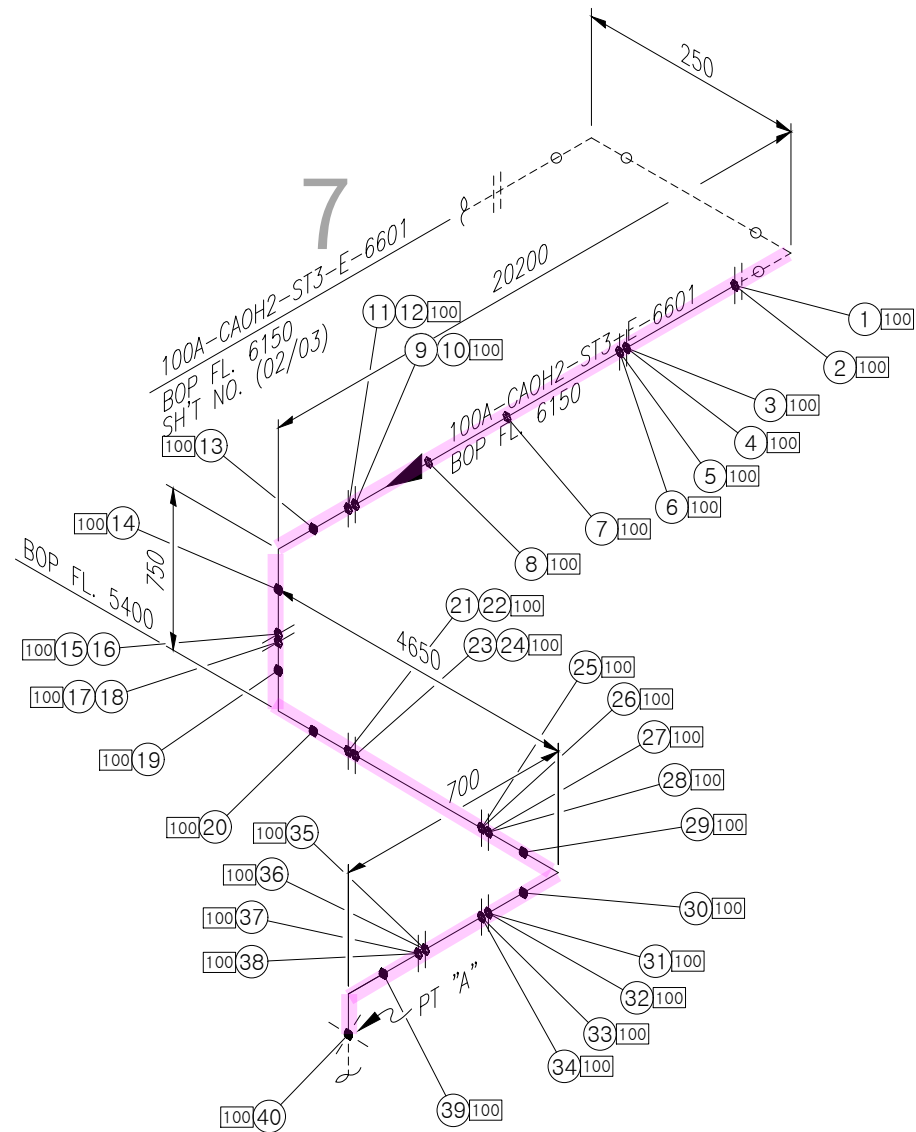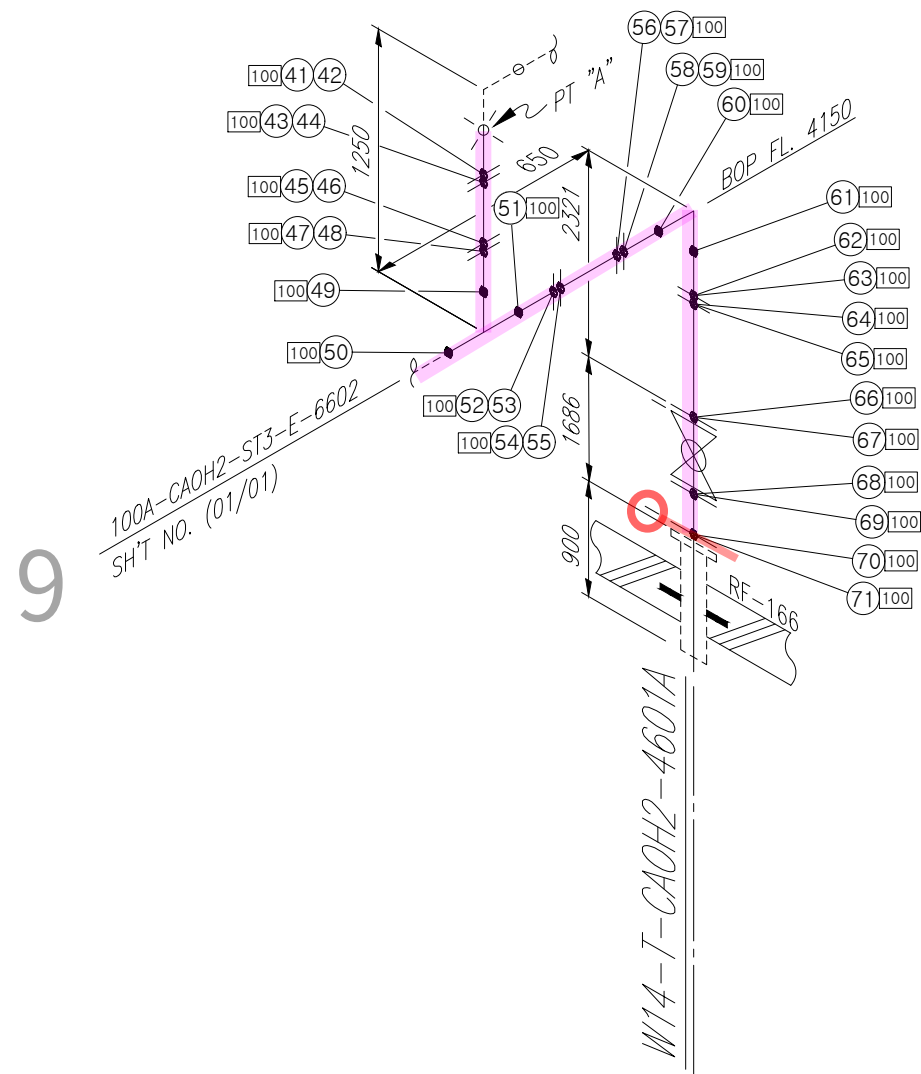

<NOTE>

1. (*) FIELD ADJUST

[illegible]

CLIENT		 		8	
CONTRACTOR				PROJECT NAME	
				M15X Ph4 Project	
COMMODITY		CA0H2		JOB NO.	
				22330D	
LINE NO.		100A-CA0H2-ST3-E-6601		SH'T NO.	REV.
				03 / 03	1

INSULATION	CODE	E	CONDITION	PRESS. (kg/cm2g)	TEMP. (°C)	AREA W14						
	THICK.	25	DESIGN	12.5	60	UNIT RFA						
			OPERATING	10	6	REF. PLAN DWG. CJ-M15W14-PI-A30-R10005-A		25.03.31	REVISED AS MARKED	황래중	안남후	박동영
						REF. P & ID		25.01.24	APPROVED FOR CONSTRUCTION	황래중	안남후	박동영
						CJ-M15W14-PR-A20-000142	REV. NO.	DATE	DESCRIPTION	BY	CHK	APP'D

[illegible]

<NOTE>

1. (*) FIELD ADJUST

CLIENT



9

* PIPE : P/P1	* 90° ELBOW : E90	* 45° ELBOW : E45	* TEE : T	* RED.TEE : TR	* STUB-IN : STU	* REINFORCING PAD : RP	* CON.RED : RC	* ECC.RED : RE	* CON.SWAGE : RCS/RCS1	* ECC.SWAGE : RES/RES1	* NIPPLE : NP/NP1/NP2	* CAP : CAP/CAP1	* PLUG : PLG	* FULL COUPLING : FC	* HALF COUPLING : HF/HF1
* STUB-IN : STU	* SOCKET(HDPE/PVC) : SC	* SADDLE(HDPE) : SD	* FLANGE : F/F1	* GASKET : G/G1/G2	* BOLT & NUT : B/B1	* BLIND FLANGE : FB/FB1	* GATE VA. : VG/VG1/VG2	* BALL VA. : VB/VB0/VB1/VB10/VB2/VB20	* BUTTERFLY VA. : VF/VF4	* CHECK VA. : VC/VC1/VC2/VC3/VC4/VC5/VC6/VC7					
* GLOBE VA. : VL/VL1/VL2	* DIAPHRAGM VA. : VD/VD0	* DAMPER : VP	* QUICK COUPLING : SQC	* FLEXIBLE JOINT(STEEL) : FLXB	* FLEXIBLE JOINT(RUBBER) : FLXR	* FLEXIBLE JOINT(STEEL PTFE LINED) : FLXL	* FLEXIBLE HOSE : FLXH	* STEAM TRAP : ST	* SPRAY NOZZLE : SPN	* EMERGENCY SHOWER : SSH					
* STRAINER(Y-TYPE) : YSTR	* STRAINER(T-TYPE) : TSTR	* STRAINER(BUCKET-TYPE) : BSTR	* ANCHOR PLATE : STOP	* BIRD SCREEN : BS	* ISOLATION KIT : IK	* UNLOADING BOX : UB	* AIR TRAP : AT	* LOTO : LOTO	* SIGHT GLASS : SG	* PRESSURE GAUGE : PG	* SHILED : SH	* SPECIAL BOLT & NUT : BL/BL1			

INSULATION	CODE	E	CONDITION	PRESS. (kg/cm2g)	TEMP. (°C)	AREA	W14							CONTRACTOR	PROJECT NAME		
	THICK.	25	DESIGN	12.5	60	UNIT	RFA								M15X Ph4 Project		
			OPERATING	10	6	REF. PLAN DWG. CJ-M15W14-PI-A30-R10005-A			25.03.31	REVISED AS MARKED	황래중	안남후	박동영	COMMODITY	CAOH2	JOB NO.	
						REF. P & ID CJ-M15W14-PR-A20-000142			25.01.24	APPROVED FOR CONSTRUCTION	황래중	안남후	박동영			22330D	
								REV. NO.	DATE	DESCRIPTION	BY	CHK	APP'D	LINE NO.	100A-CAOH2-ST3-E-6602	SH'T NO. 01 / 01	REV. 1

[illegible]

[illegible]


<NOTE>

1. (*) FIELD ADJUST

* PIPE : P/P1	* 90° ELBOW : E90	* 45° ELBOW : E45	* TEE : T	* RED.TEE : TR	* STUB-IN : STU	* REINFORCING PAD : RP	* CON.RED : RC	* ECC.RED : RE	* CON.SWAGE : RCS/RCS1	* ECC.SWAGE : RES/RES1	* NIPPLE : NP/NP1/NP2	* CAP : CAP/CAP1	* PLUG : PLG	* FULL COUPLING : FC	* HALF COUPLING : HF/HF1
* STUB-IN : STU	* SOCKET(HDPE/PVC) : SC	* SADDLE(HDPE) : SD	* FLANGE : F/F1	* GASKET : G/G1/G2	* BOLT & NUT : B/B1	* BLIND FLANGE : FB/FB1	* GATE VA. : VG/VG1/VG2	* BALL VA. : VB/VBLO/VB1/VB1LO/VB2/VB2LO	* BUTTERFLY VA. : VF/VF4	* CHECK VA. : VC/VC1/VC2/VC3/VC4/VC5/VC6/VC7					
* GLOBE VA. : VL/VL1/VL2	* DIAPHRAGM VA. : VD/VDLO	* DAMPER : VP	* QUICK COUPLING : SQC	* FLEXIBLE JOINT(STEEL) : FLXB	* FLEXIBLE JOINT(RUBBER) : FLXR	* FLEXIBLE JOINT(STEEL PTFE LINED) : FLXL	* FLEXIBLE HOSE : FLXH	* STEAM TRAP : ST	* SPRAY NOZZLE : SPN	* EMERGENCY SHOWER : SSH					
* STRAINER(Y-TYPE) : YSTR	* STRAINER(T-TYPE) : TSTR	* STRAINER(BUCKET-TYPE) : BSTR	* ANCHOR PLATE : STOP	* BIRD SCREEN : BS	* ISOLATION KIT : IK	* UNLOADING BOX : UB	* AIR TRAP : AT	* LOTO : LOTO	* SIGHT GLASS : SG	* PRESSURE GAUGE : PG	* SHILED : SH	* SPECIAL BOLT & NUT : BL/BL1			

[illegible]

경고 : 본 도면은 SK HYNIX의 기밀비밀 자료로서, 어떠한 경우에도 목적 외 사용, 복제, 제3자에게 공개, 누설 및 유출할 수 없으며, 회사는 유도자의 불법 사용으로 피해가 발생할 경우 유도자에게 민/형사상 책임을 요구할 수 있음

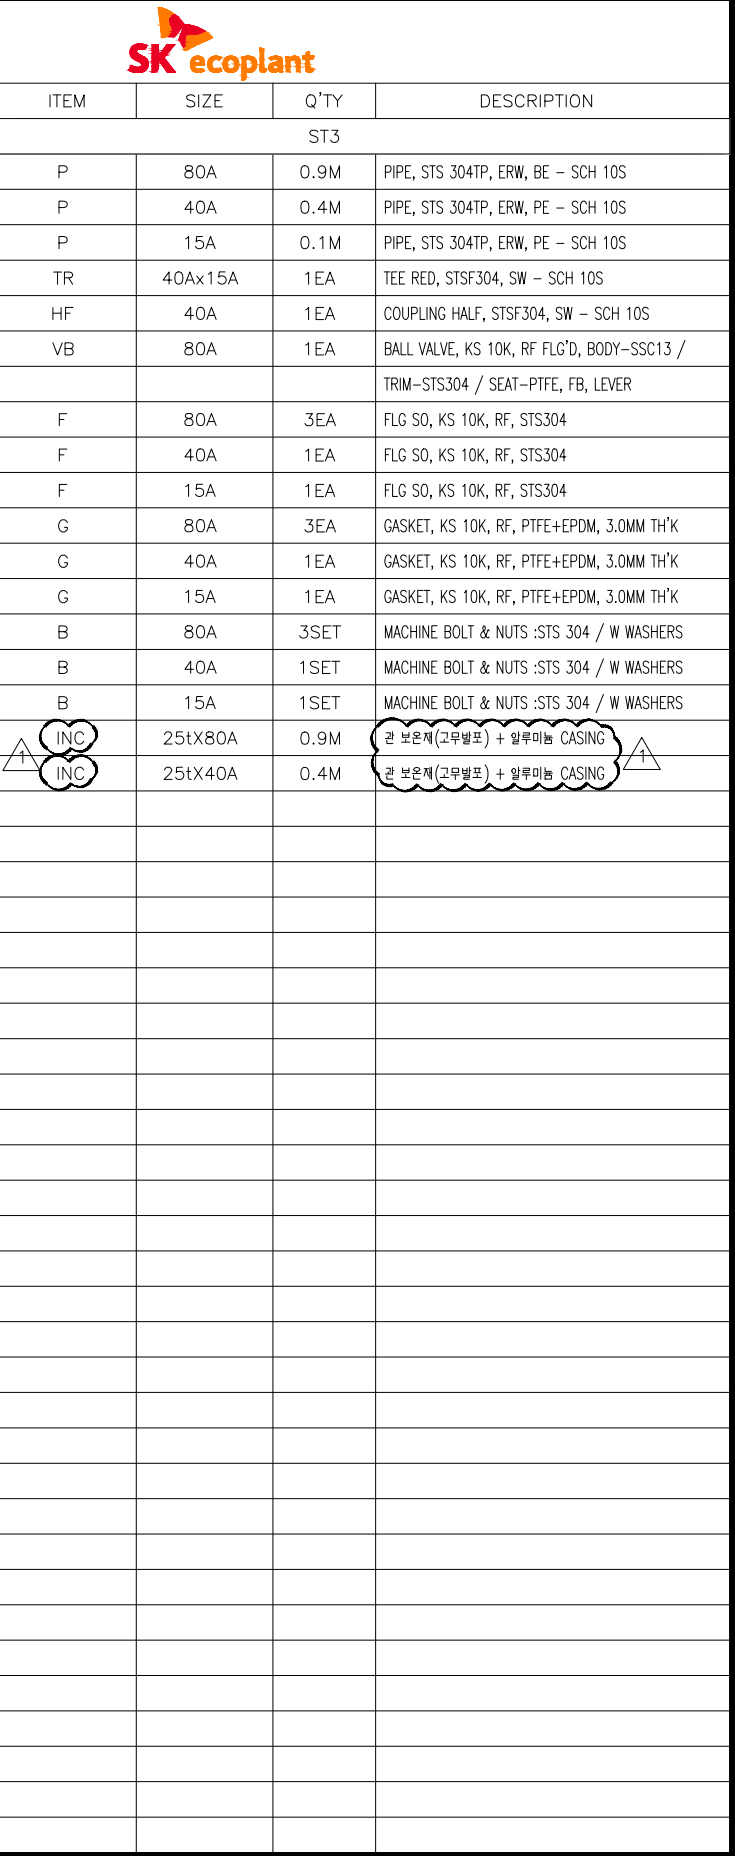

CLIENT		 	
CONTRACTOR 		PROJECT NAME M15X Ph4 Project	
COMMODITY CA0H2		JOB NO. 22330D	
LINE NO. 80A-CA0H2-ST3-E-6543		SH'T NO. 01 / 01	REV. 1

INSULATION	CODE	E	CONDITION	PRESS. (kg/cm2g)	TEMP. (°C)	AREA W14						
	THICK.	25	DESIGN	8	60	UNIT RFA						
			OPERATING	7.2	AMB	REF. PLAN DWG. CJ-M15W14-PI-A30-R10003-B		25.03.31	REVISED AS MARKED	황래중	안남후	박동영
						REF. P & ID CJ-M15W14-PR-A20-000109		25.01.24	APPROVED FOR CONSTRUCTION	황래중	안남후	박동영
							REV. NO.	DATE	DESCRIPTION	BY	CHK	APP'D

[illegible]

<NOTE>

1. (*) FIELD ADJUST


CLIENT



12

INSULATION	CODE	E	CONDITION	PRESS. (kg/cm2g)	TEMP. (°C)	AREA W14							CONTRACTOR	PROJECT NAME		
	THICK.	25	DESIGN	8	60	UNIT RFA								M15X Ph4 Project		
			OPERATING	7.2	AMB	REF. PLAN DWG. CJ-M15W14-PI-A30-R10008-B		25.03.31	REVISED AS MARKED	황래중	안남후	박동영	COMMODITY	CAOH2	JOB NO.	
						REF. P & ID CJ-M15W14-PR-A20-000102		25.01.24	APPROVED FOR CONSTRUCTION	황래중	안남후	박동영	LINE NO.	80A-CAOH2-ST3-E-6558	SH'T NO. 01 / 01	REV. 1
							REV. NO.	DATE	DESCRIPTION	BY	CHK	APP'D				

경고 : 본 도면은 SK HYNIX의 기밀비밀 자료로서, 어떠한 경우에도 목적 외 사용, 복제, 제3자에게 공개, 누설 및 유출할 수 없으며, 회사는 유도자의 불법 사용으로 피해가 발생할 경우 유도자에게 민/형사상 책임을 요구할 수 있음

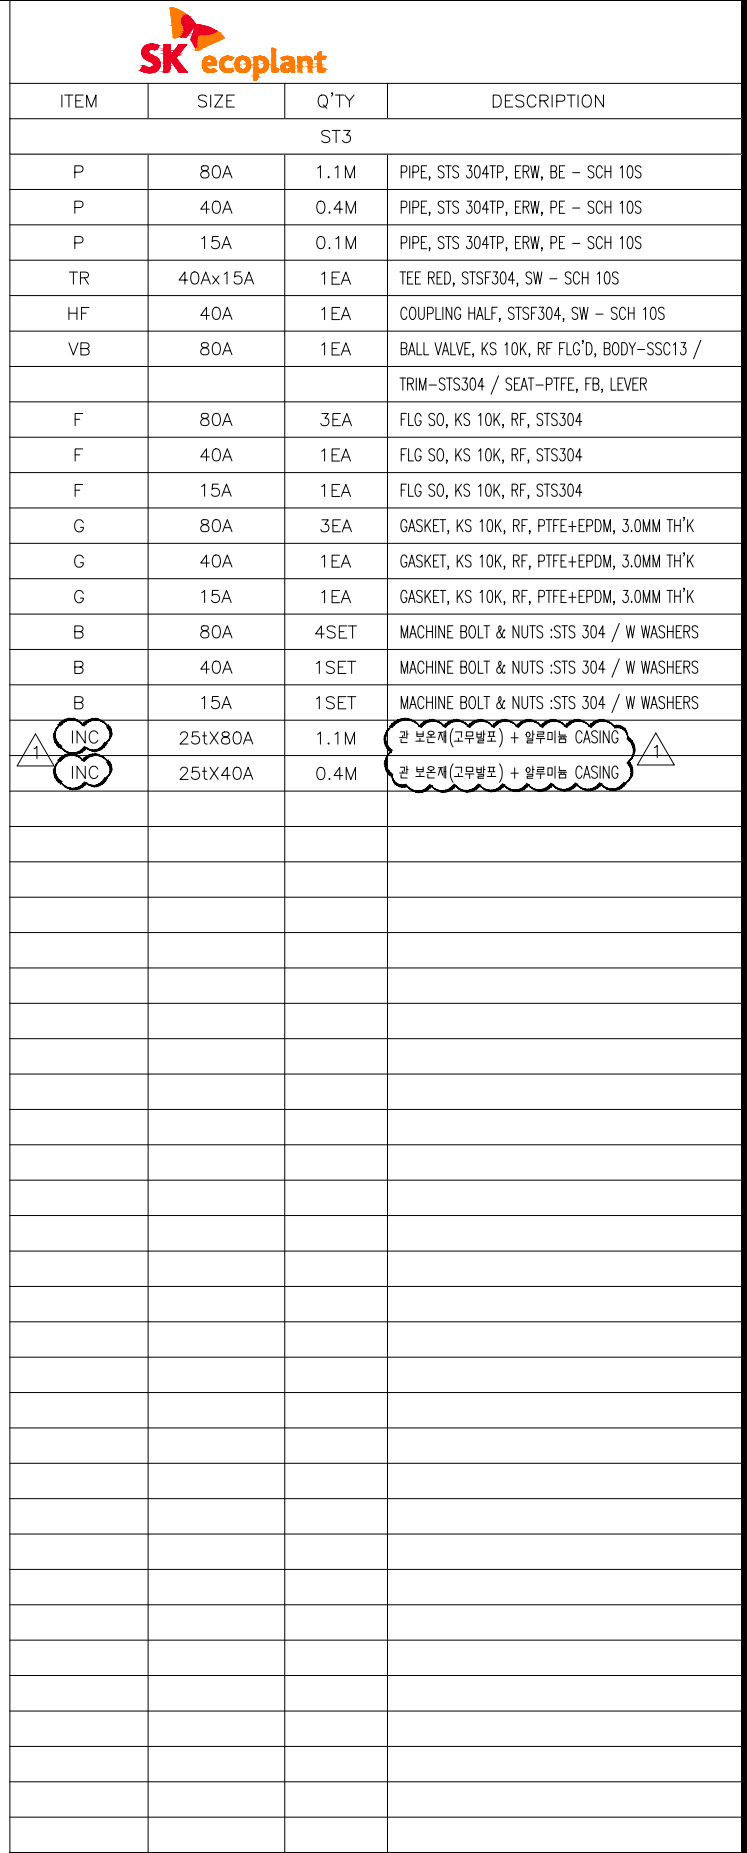

INSULATION	CODE	E	CONDITION	PRESS. (kg/cm2g)	TEMP. (°C)	AREA W14							CONTRACTOR	PROJECT NAME	
	THICK.	25	DESIGN	8	60	UNIT RFA								M15X Ph4 Project	
			OPERATING	7.2	AMB	REF. PLAN DWG. CJ-M15W14-PI-A30-R10009-B		25.03.31	REVISED AS MARKED	황래중	안남후	박동영	COMMODITY	CAOH2	JOB NO.
						REF. P & ID CJ-M15W14-PR-A20-000104		25.01.24	APPROVED FOR CONSTRUCTION	황래중	안남후	박동영	LINE NO.	80A-CAOH2-ST3-E-6559	SH'T NO.
							REV. NO.	DATE	DESCRIPTION	BY	CHK	APP'D			01 / 01