


WW-SLD-557

PROJECT TITLE : M15X Ph2 Project

[illegible]

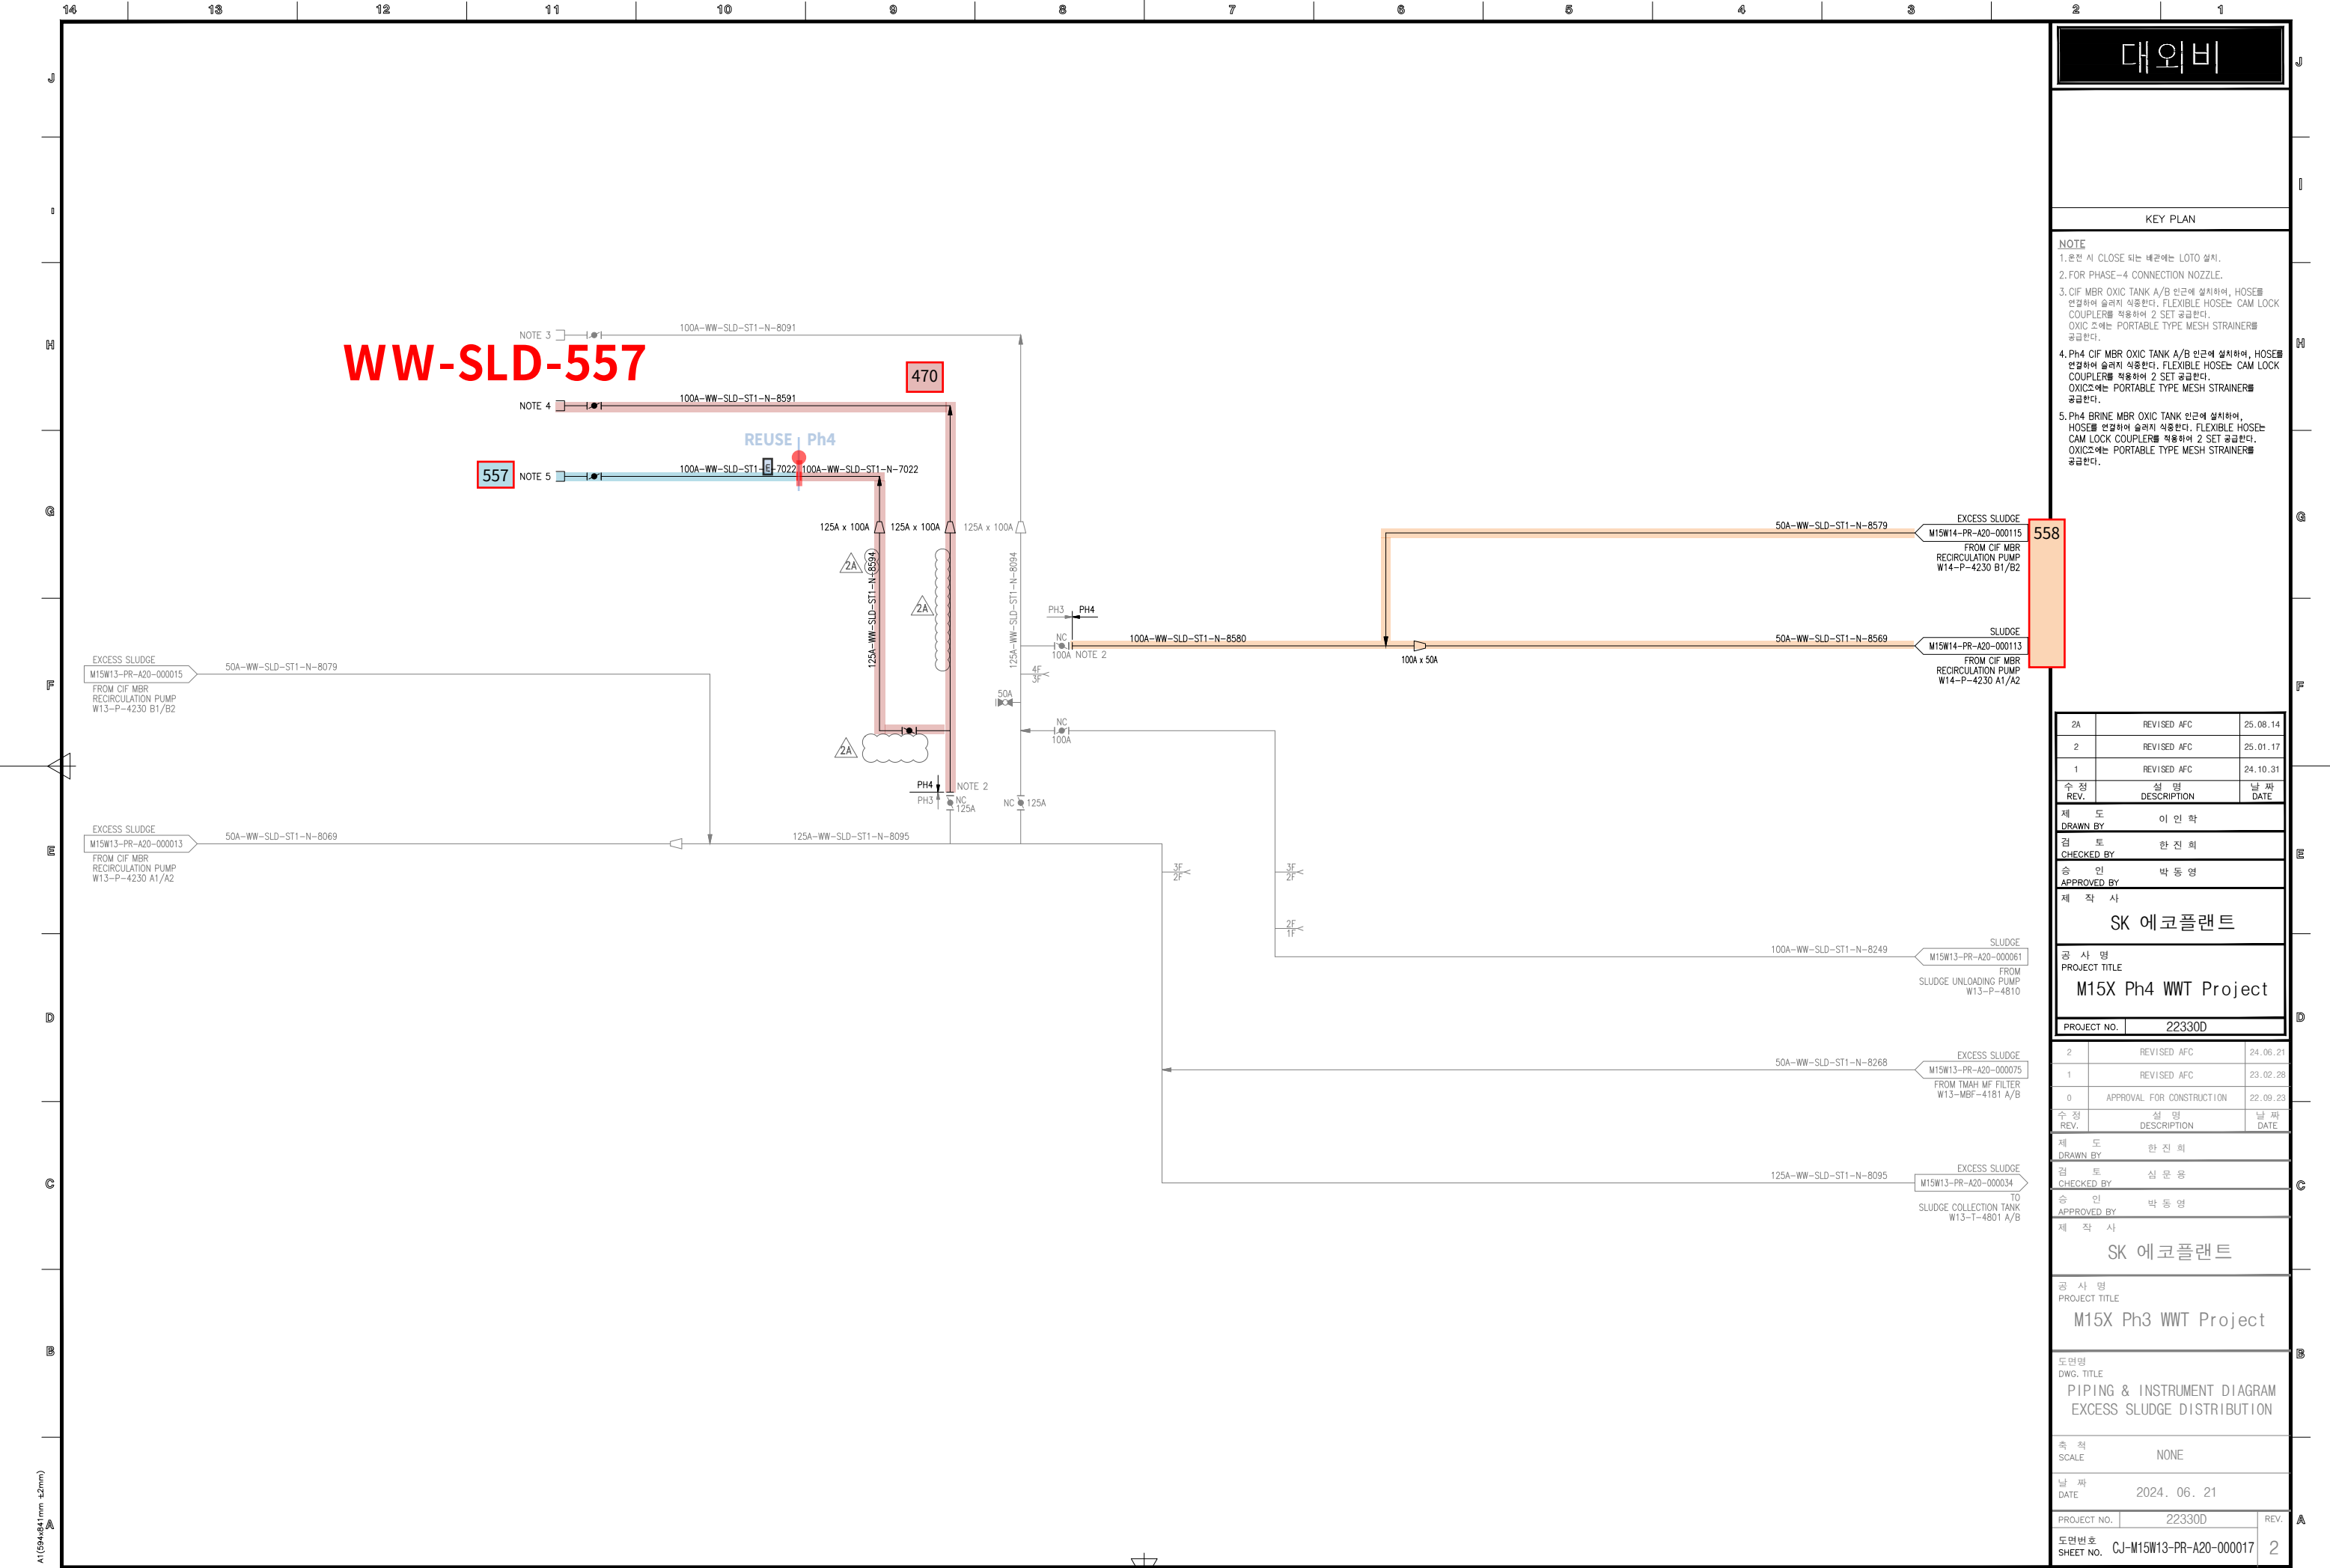

대외비

KEY PLAN

NOTE

1. 환전 시 CLOSE 되는 배관에는 LOTO 설치.

2. FOR PHASE-4 CONNECTION NOZZLE.

3. CIF MBR OXIC TANK A/B 인근에 설치하여, HOSE를 연결하여 슬러지 식중한다. FLEXIBLE HOSE는 CAM LOCK COUPLER를 적용하여 2 SET 공급한다. OXIC 조에는 PORTABLE TYPE MESH STRAINER를 공급한다.

4. Ph4 CIF MBR OXIC TANK A/B 인근에 설치하여, HOSE를 연결하여 슬러지 식중한다. FLEXIBLE HOSE는 CAM LOCK COUPLER를 적용하여 2 SET 공급한다. OXIC 조에는 PORTABLE TYPE MESH STRAINER를 공급한다.

5. Ph4 BRINE MBR OXIC TANK 인근에 설치하여, HOSE를 연결하여 슬러지 식중한다. FLEXIBLE HOSE는 CAM LOCK COUPLER를 적용하여 2 SET 공급한다. OXIC 조에는 PORTABLE TYPE MESH STRAINER를 공급한다.

2A	REVISED AFC	25.08.14
2	REVISED AFC	25.01.17
1	REVISED AFC	24.10.31
수정 REV.	설명 DESCRIPTION	날짜 DATE
제 도	이 인 학	
검 토	한 진 희	
승 인	박 동 영	
제 작 사	SK 에코플랜트	
공 사 명	PROJECT TITLE	
M15X Ph4 WWT Project		
PROJECT NO.	22330D	
2	REVISED AFC	24.06.21
1	REVISED AFC	23.02.28
0	APPROVAL FOR CONSTRUCTION	22.09.23
수정 REV.	설명 DESCRIPTION	날짜 DATE
제 도	한 진 희	
검 토	심 문 용	
승 인	박 동 영	
제 작 사	SK 에코플랜트	
공 사 명	PROJECT TITLE	
M15X Ph3 WWT Project		
도면명	DWG. TITLE	
PIPING & INSTRUMENT DIAGRAM EXCESS SLUDGE DISTRIBUTION		
측 척	SCALE	
NONE		
날 짜	DATE	
2024. 06. 21		
PROJECT NO.	22330D	REV.
도면번호	CJ-M15W13-PR-A20-000017	2

[illegible]

CLIENT		1	
			
CONTRACTOR		PROJECT NAME	
WW—SLD		M15X Ph4 Project	
COMMODITY		JOB NO.	
100A-WW-SLD-ST1-E-7022		22330D	
LINE NO.		SH'T NO.	REV.
		01 / 01	0