


DRAWING LIST FOR TEST PACKAGE

PROJECT NO.: 22328D

PROJECT TITLE : M15X Ph2 Project

WW-NH4OH-560

No	PKG No	UNIT	LINE NUMBER			P&ID		REMARK
			ISO DRAWING No	SHEET	REV	P&ID No	REV	
1	560	5FA	OD160-WW-NH4OH-HP1-N-1745-01	1 OF 1	0	CJ-M15W13-PR-A20-000031	2	
2	560	RFA	OD160-WW-NH4OH-HP1-E-1745-01	1 OF 1	1	CJ-M15W13-PR-A20-000031	2	

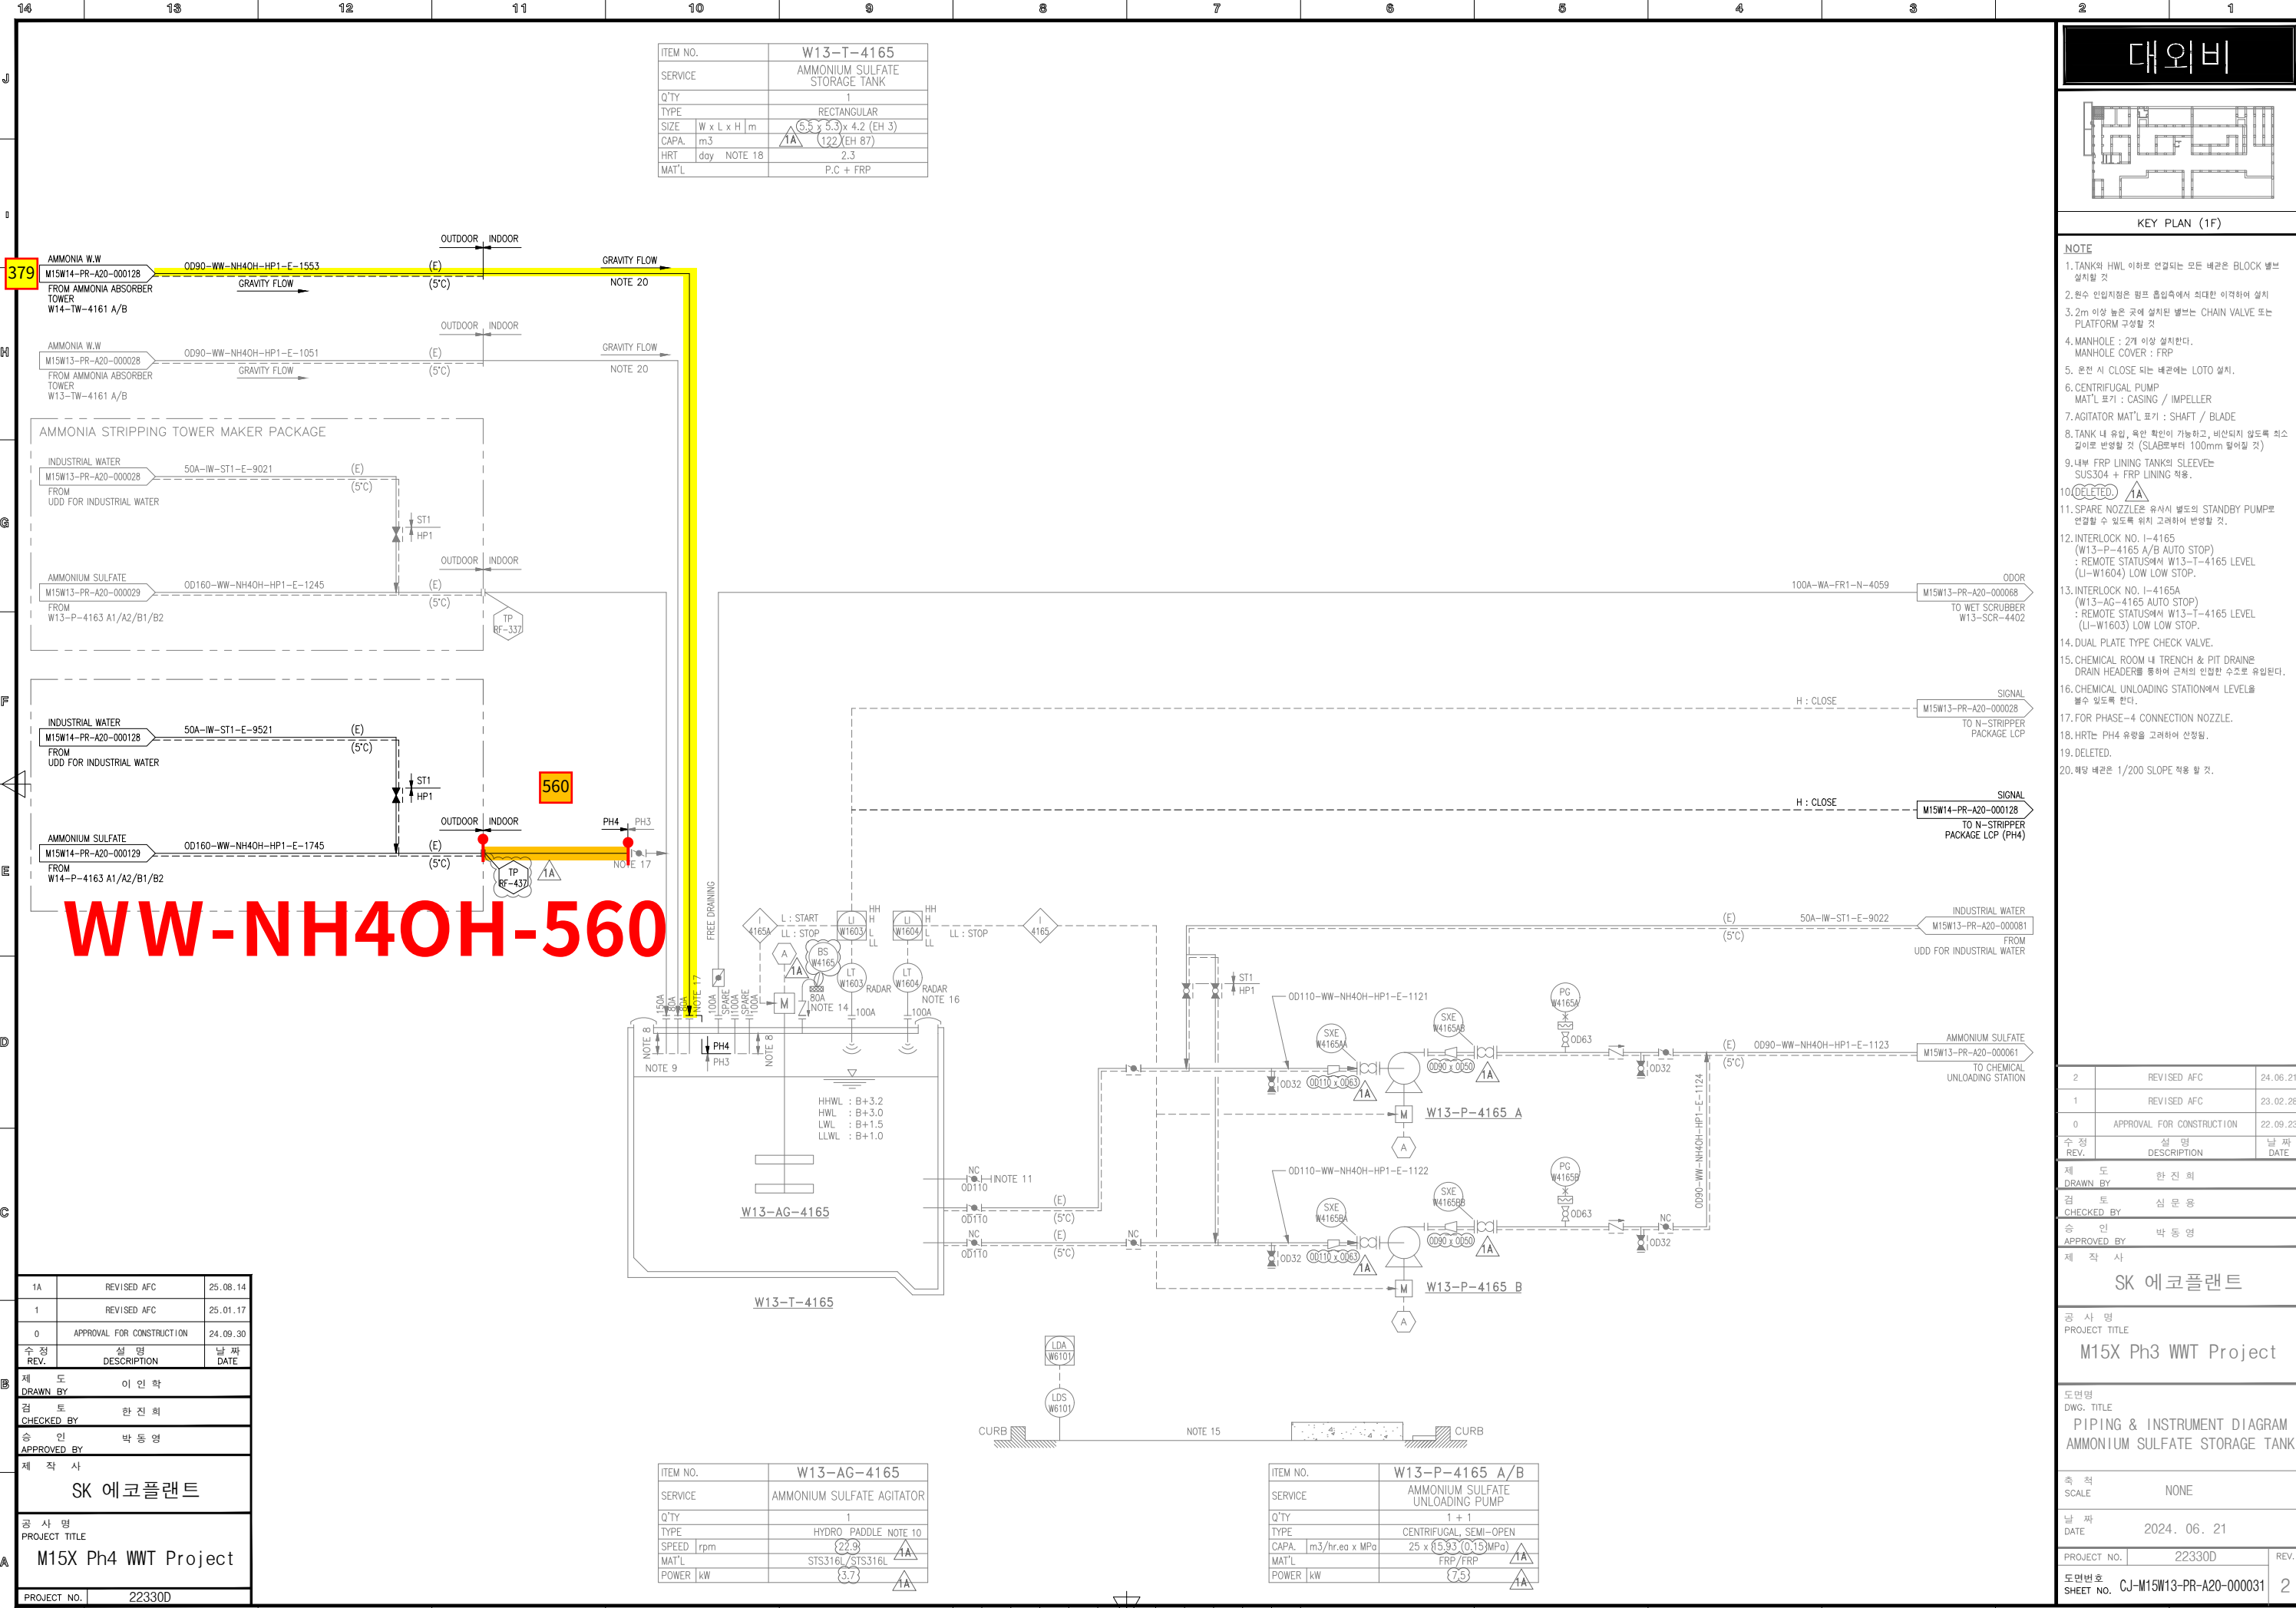

1A	REVISED AFC	25.08.14
1	REVISED AFC	25.01.17
0	APPROVAL FOR CONSTRUCTION	24.09.30
수정 REV.	설명 DESCRIPTION	날짜 DATE
제도 DRAWN BY	이인학	
검토 CHECKED BY	한진희	
승인 APPROVED BY	박동영	
제작사	SK 에코플랜트	
공사명 PROJECT TITLE	M15X Ph4 WWT Project	
PROJECT NO.	22330D	

ITEM NO.	W13-T-4165
SERVICE	AMMONIUM SULFATE STORAGE TANK
Q'TY	1
TYPE	RECTANGULAR
SIZE	W x L x H m (5.5 x 5.3 x 4.2 (EH 3))
CAPA	m3 (122 (EH 87))
HRT	day NOTE 18 2.3
MAT'L	P.C + FRP

ITEM NO.	W13-AG-4165
SERVICE	AMMONIUM SULFATE AGITATOR
Q'TY	1
TYPE	HYDRO PADDLE NOTE 10
SPEED	rpm (22.9)
MAT'L	STS316L/STS316L
POWER	kW (3.7)

ITEM NO.	W13-P-4165 A/B
SERVICE	AMMONIUM SULFATE UNLOADING PUMP
Q'TY	1 + 1
TYPE	CENTRIFUGAL, SEMI-OPEN
CAPA	m3/hr.ea x MPa 25 x (5.93 (0.13)MPa)
MAT'L	FRP/FRP
POWER	kW (7.5)

대외비

KEY PLAN (1F)

NOTE

1. TANK의 HWL 이하로 연결되는 모든 배관은 BLOCK 밸브 설치할 것

2. 환수 인입지점은 펌프 흡입측에서 최대한 이격하여 설치

3. 2m 이상 높은 곳에 설치된 밸브는 CHAIN VALVE 또는 PLATFORM 구성할 것

4. MANHOLE : 2개 이상 설치한다.
MANHOLE COVER : FRP

5. 온한 시 CLOSE 되는 배관에는 LOTO 설치.

6. CENTRIFUGAL PUMP
MAT'L 표기 : CASING / IMPELLER

7. AGITATOR MAT'L 표기 : SHAFT / BLADE

8. TANK 내 유입, 육안 확인이 가능하고, 비산되지 않도록 최소 길이로 반영할 것 (SLAB면부터 100mm 떨어질 것)

9. 내부 FRP LINING TANK의 SLEEVE는 SUS304 + FRP LINING 적용.

10. ~~DELETED~~ 1A

11. SPARE NOZZLE은 유제시 별도의 STANDBY PUMP로 연결할 수 있도록 위치 고려하여 반영할 것.

12. INTERLOCK NO. 1-4165 (W13-P-4165 A/B AUTO STOP) : REMOTE STATUS에서 W13-T-4165 LEVEL (LI-W1604) LOW LOW STOP.

13. INTERLOCK NO. 1-4165A (W13-AG-4165 AUTO STOP) : REMOTE STATUS에서 W13-T-4165 LEVEL (LI-W1603) LOW LOW STOP.

14. DUAL PLATE TYPE CHECK VALVE.

15. CHEMICAL ROOM 내 TRENCH & PIT DRAIN은 DRAIN HEADER를 통하여 근처의 인입관 수조로 유입된다.

16. CHEMICAL UNLOADING STATION에서 LEVEL을 불수 있도록 한다.

17. FOR PHASE-4 CONNECTION NOZZLE.


18. HRT는 PH4 유량을 고려하여 선정함.

19. DELETED.

20. 해당 배관은 1/200 SLOPE 적용 할 것.

2	REVISED AFC	24.06.21
1	REVISED AFC	23.02.28
0	APPROVAL FOR CONSTRUCTION	22.09.23
수정 REV.	설명 DESCRIPTION	날짜 DATE
제도 DRAWN BY	한진희	
검토 CHECKED BY	심문용	
승인 APPROVED BY	박동영	
제작사	SK 에코플랜트	
공사명 PROJECT TITLE	M15X Ph3 WWT Project	
도면명 DWG. TITLE	PIPING & INSTRUMENT DIAGRAM AMMONIUM SULFATE STORAGE TANK	
축척 SCALE	NONE	
날짜 DATE	2024. 06. 21	
PROJECT NO.	22330D	REV.
도면번호 SHEET NO.	CJ-M15W13-PR-A20-000031	2

C:\Users\WTOP\Desktop\W&ID\251013\W[M15X Ph-4 for 인허가]\CAD FILE_0910\WCJ-M15W13-PR-A20-000031 R1 P&ID FOR AMMO

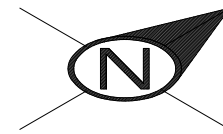

1. (*) FIELD ADJUST
2. TRAY & ANGLE, CHANNEL SUPPORT가 적용되는
배관 ELEVATION은 현장 맞춤으로 한다.

CLIENT



1

INSULATION	CODE	N	CONDITION	PRESS. (kg/cm2g)	TEMP. (°C)	AREA W14						
	THICK.	-	DESIGN	BY VENDOR	60	UNIT 5FA						
			OPERATING	BY VENDOR	BY VENDOR	REF. PLAN DWG. CJ-M15W14-PI-A30-050008-D						
						REF. P & ID CJ-M15W14-PR-A20-000129		25.01.24	APPROVED FOR CONSTRUCTION	황래중	안남후	박동영
							REV. NO.	DATE	DESCRIPTION	BY	CHK	APP'D



CLIENT



2

경고 : 본 문건은 SK HYNIX의 기밀비밀 자료로서, 어떠한 경우에도 무단으로 복제, 제3자에게 공개, 누설할 수 없습니다. 회사는 오폭자의 사용으로 인해 피해가 발생할 경우 오폭자에게 민/형사상 책임을 물을 것입니다.