


C6H8O7-562

PROJECT TITLE : M15X Ph2 Project[illegible]

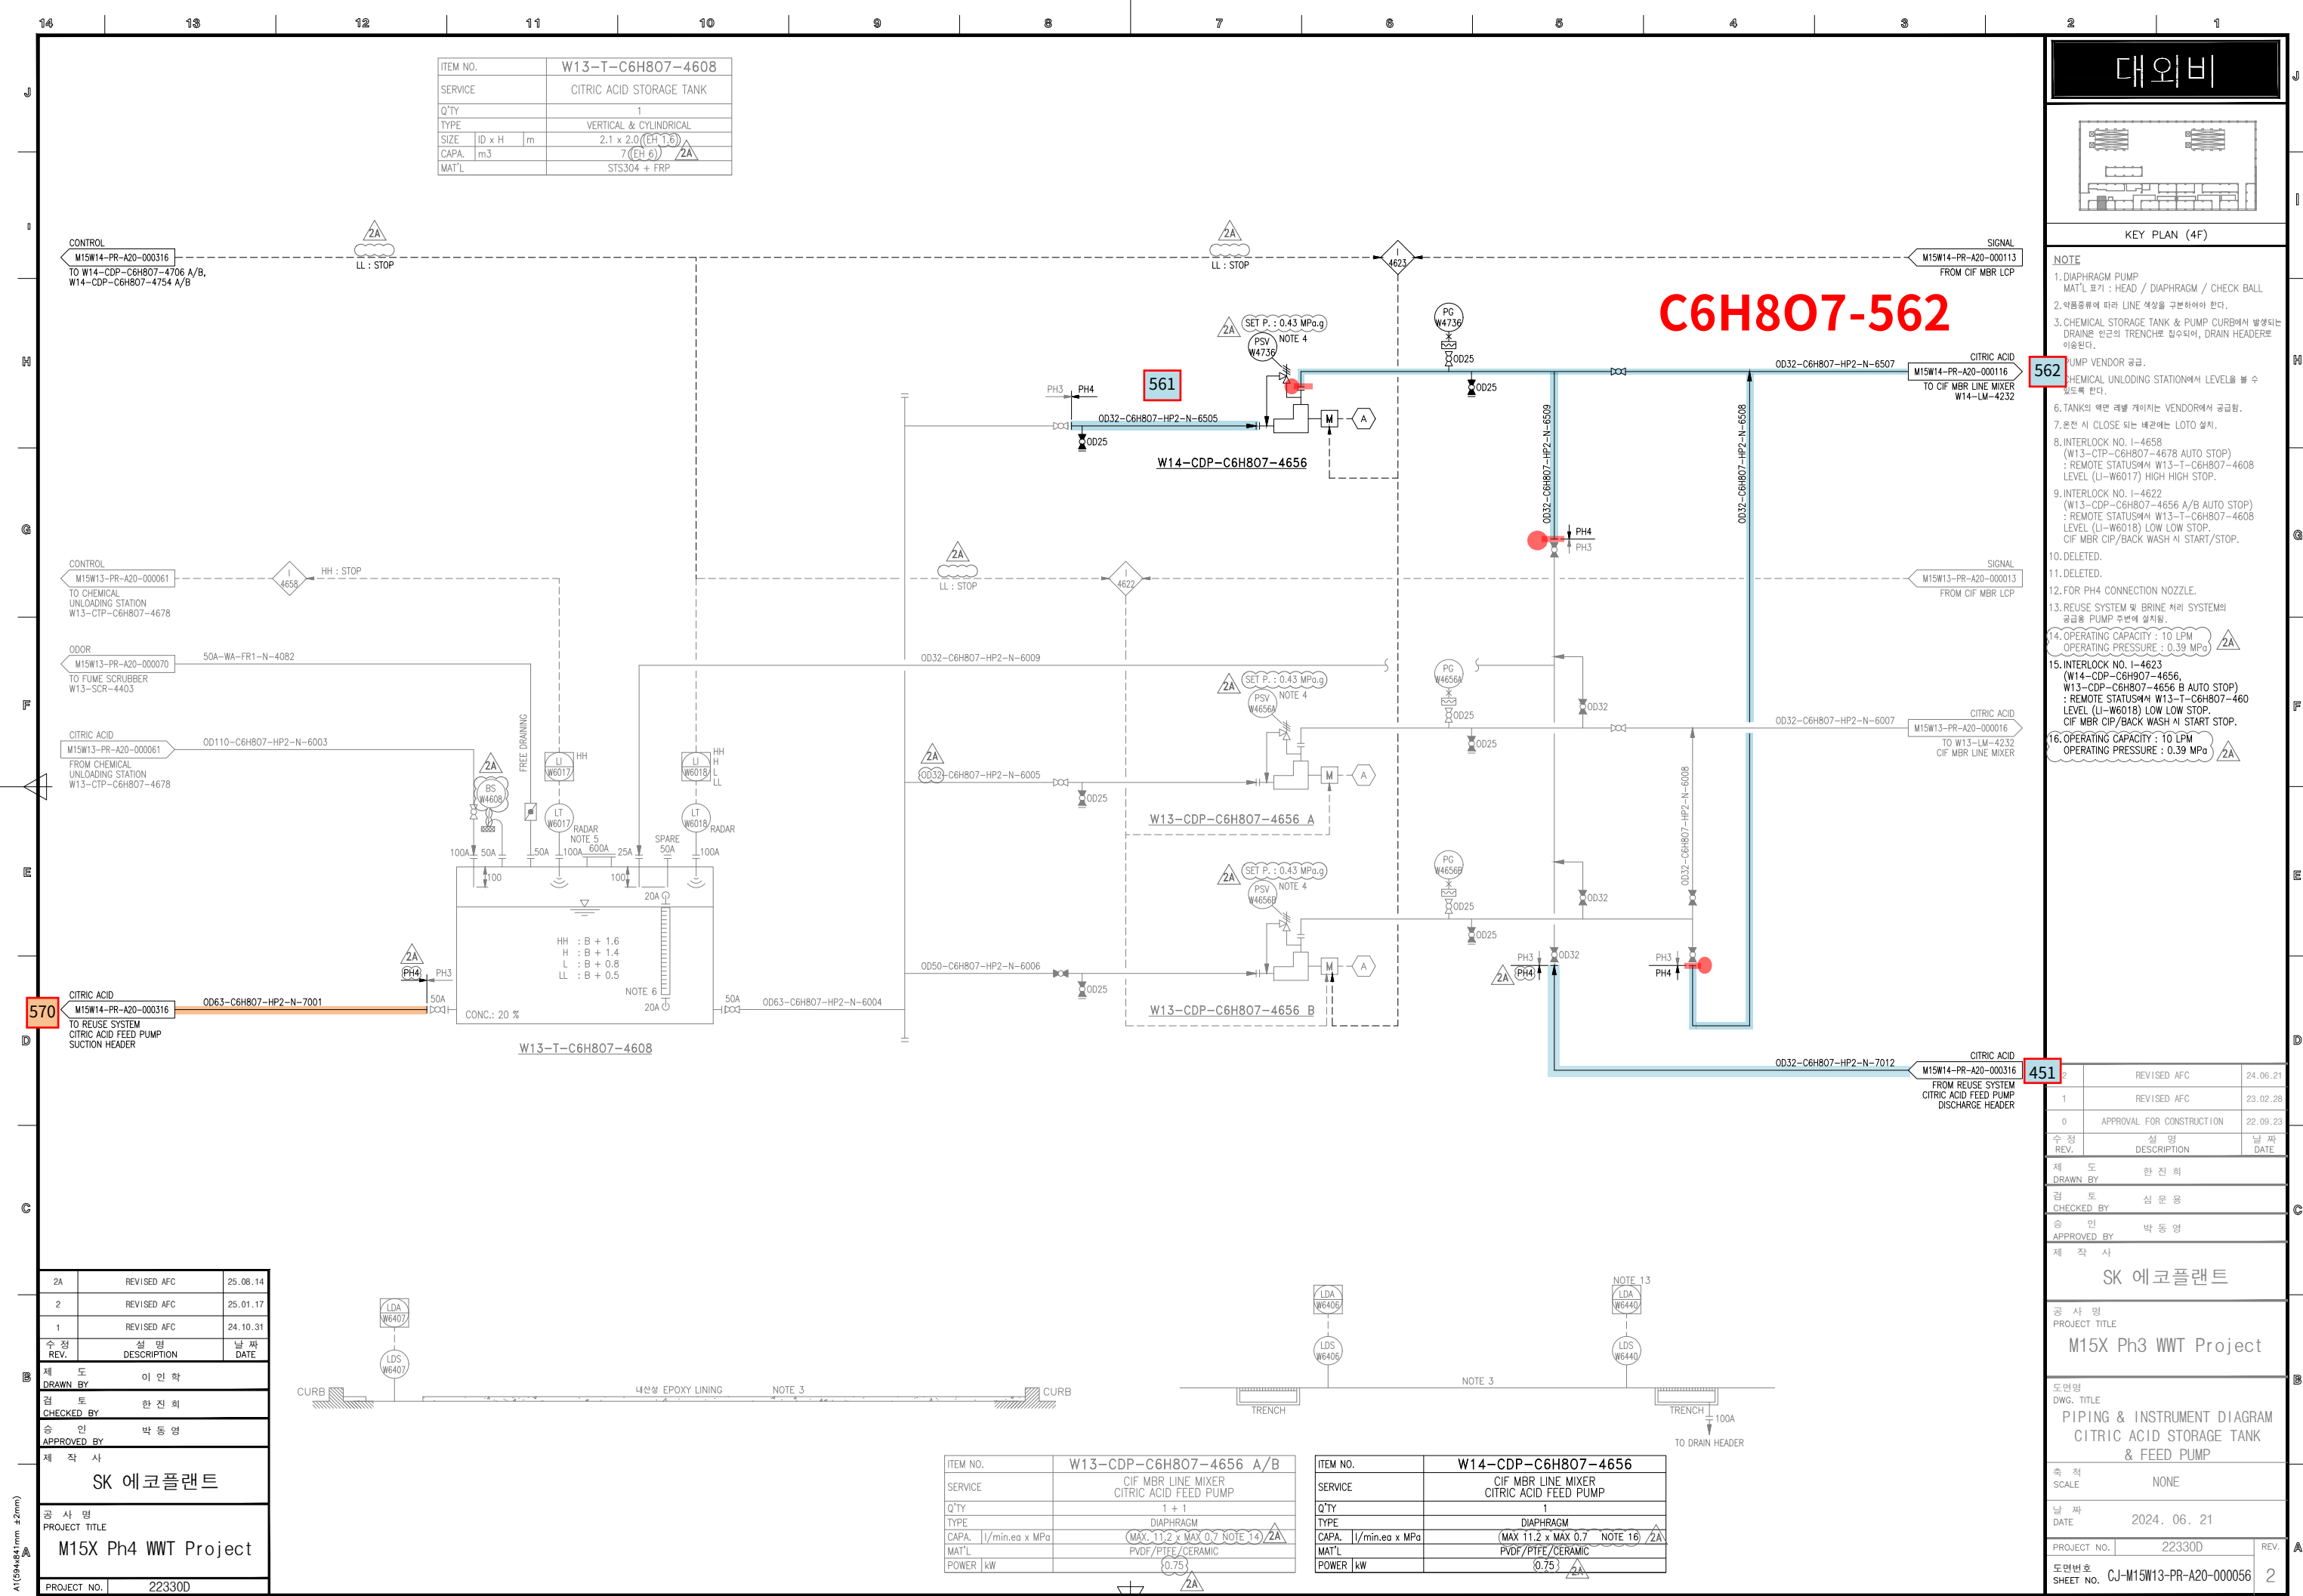

대외비


KEY PLAN (4F)


NOTE
1. DIAPHRAGM PUMP
MAT'L 표기 : HEAD / DIAPHRAGM / CHECK BALL
2. 역류종류에 따라 LINE 역상을 구분하여야 한다.
3. CHEMICAL STORAGE TANK & PUMP CURB에서 발생하는 DRAIN은 인근의 TRENCH로 흡수되어, DRAIN HEADER로 이용된다.
4. PUMP VENDOR 공표.
5. CHEMICAL UNLOADING STATION에서 LEVEL을 볼 수 있도록 한다.
6. TANK의 역면 레벨 개시지는 VENDOR에서 공급함.
7. 운전 시 CLOSE 되는 배관에는 LOTO 설치.
8. INTERLOCK NO. I-4658
(W13-CTP-C6H807-4678 AUTO STOP)
: REMOTE STATUS에서 W13-T-C6H807-4608 LEVEL (U-W6017) HIGH HIGH STOP.
9. INTERLOCK NO. I-4622
(W13-CDP-C6H807-4656 A/B AUTO STOP)
: REMOTE STATUS에서 W13-T-C6H807-4608 LEVEL (U-W6018) LOW LOW STOP.
CIF MBR CIP/BACK WASH 시 START/STOP.
10. DELETED.
11. DELETED.
12. FOR PH4 CONNECTION NOZZLE.
13. REUSE SYSTEM 및 BRINE 처리 SYSTEM의 공급을 PUMP 주변에 설치함.
14. OPERATING CAPACITY : 10 LPM
OPERATING PRESSURE : 0.39 MPa
15. INTERLOCK NO. I-4623
(W14-CDP-C6H807-4656, W13-CDP-C6H807-4656 B AUTO STOP)
: REMOTE STATUS에서 W13-T-C6H807-4608 LEVEL (U-W6018) LOW LOW STOP.
CIF MBR CIP/BACK WASH 시 START/STOP.
16. OPERATING CAPACITY : 10 LPM
OPERATING PRESSURE : 0.39 MPa


REVISED AFC	24.06.21	
1	REVISED AFC	23.02.28
0	APPROVAL FOR CONSTRUCTION	22.09.23
수정 REV.	실명 DESCRIPTION	날짜 DATE
제도	한진희	
검토 CHECKED BY	심문용	
승인 APPROVED BY	박동영	
제작사	SK 에코플랜트	
공사명 PROJECT TITLE	M15X Ph3 WWT Project	
도면명 DWG. TITLE	PIPING & INSTRUMENT DIAGRAM CITRIC ACID STORAGE TANK & FEED PUMP	
축척 SCALE	NONE	
날짜 DATE	2024. 06. 21	
PROJECT NO.	22330D	REV.
도면번호 SHEET NO.	CJ-M15W13-PR-A20-000056	2



ITEM NO.	W14-T-4233	
SERVICE	CIF MBR BACKWASH TANK	
Q'TY	1	
TYPE	RECTANGULAR	
SIZE	3 x 4 x 3.5 (EH3.2)	
CAPA.	42 (EH38.4)	
MAT'L	BY VENDOR	

ITEM NO.	W14-P-4232 A/B		
SERVICE	CIF MBR BACK WASHING PUMP		
Q'TY	1 + 1		
TYPE	CENTRIFUGAL(WWF)		
CAPA.	m ³ /hr x mH	{ 70.72 }	1A
MAT'L	STS304/STS304		
POWER	kW	{ 7.5 }	1A

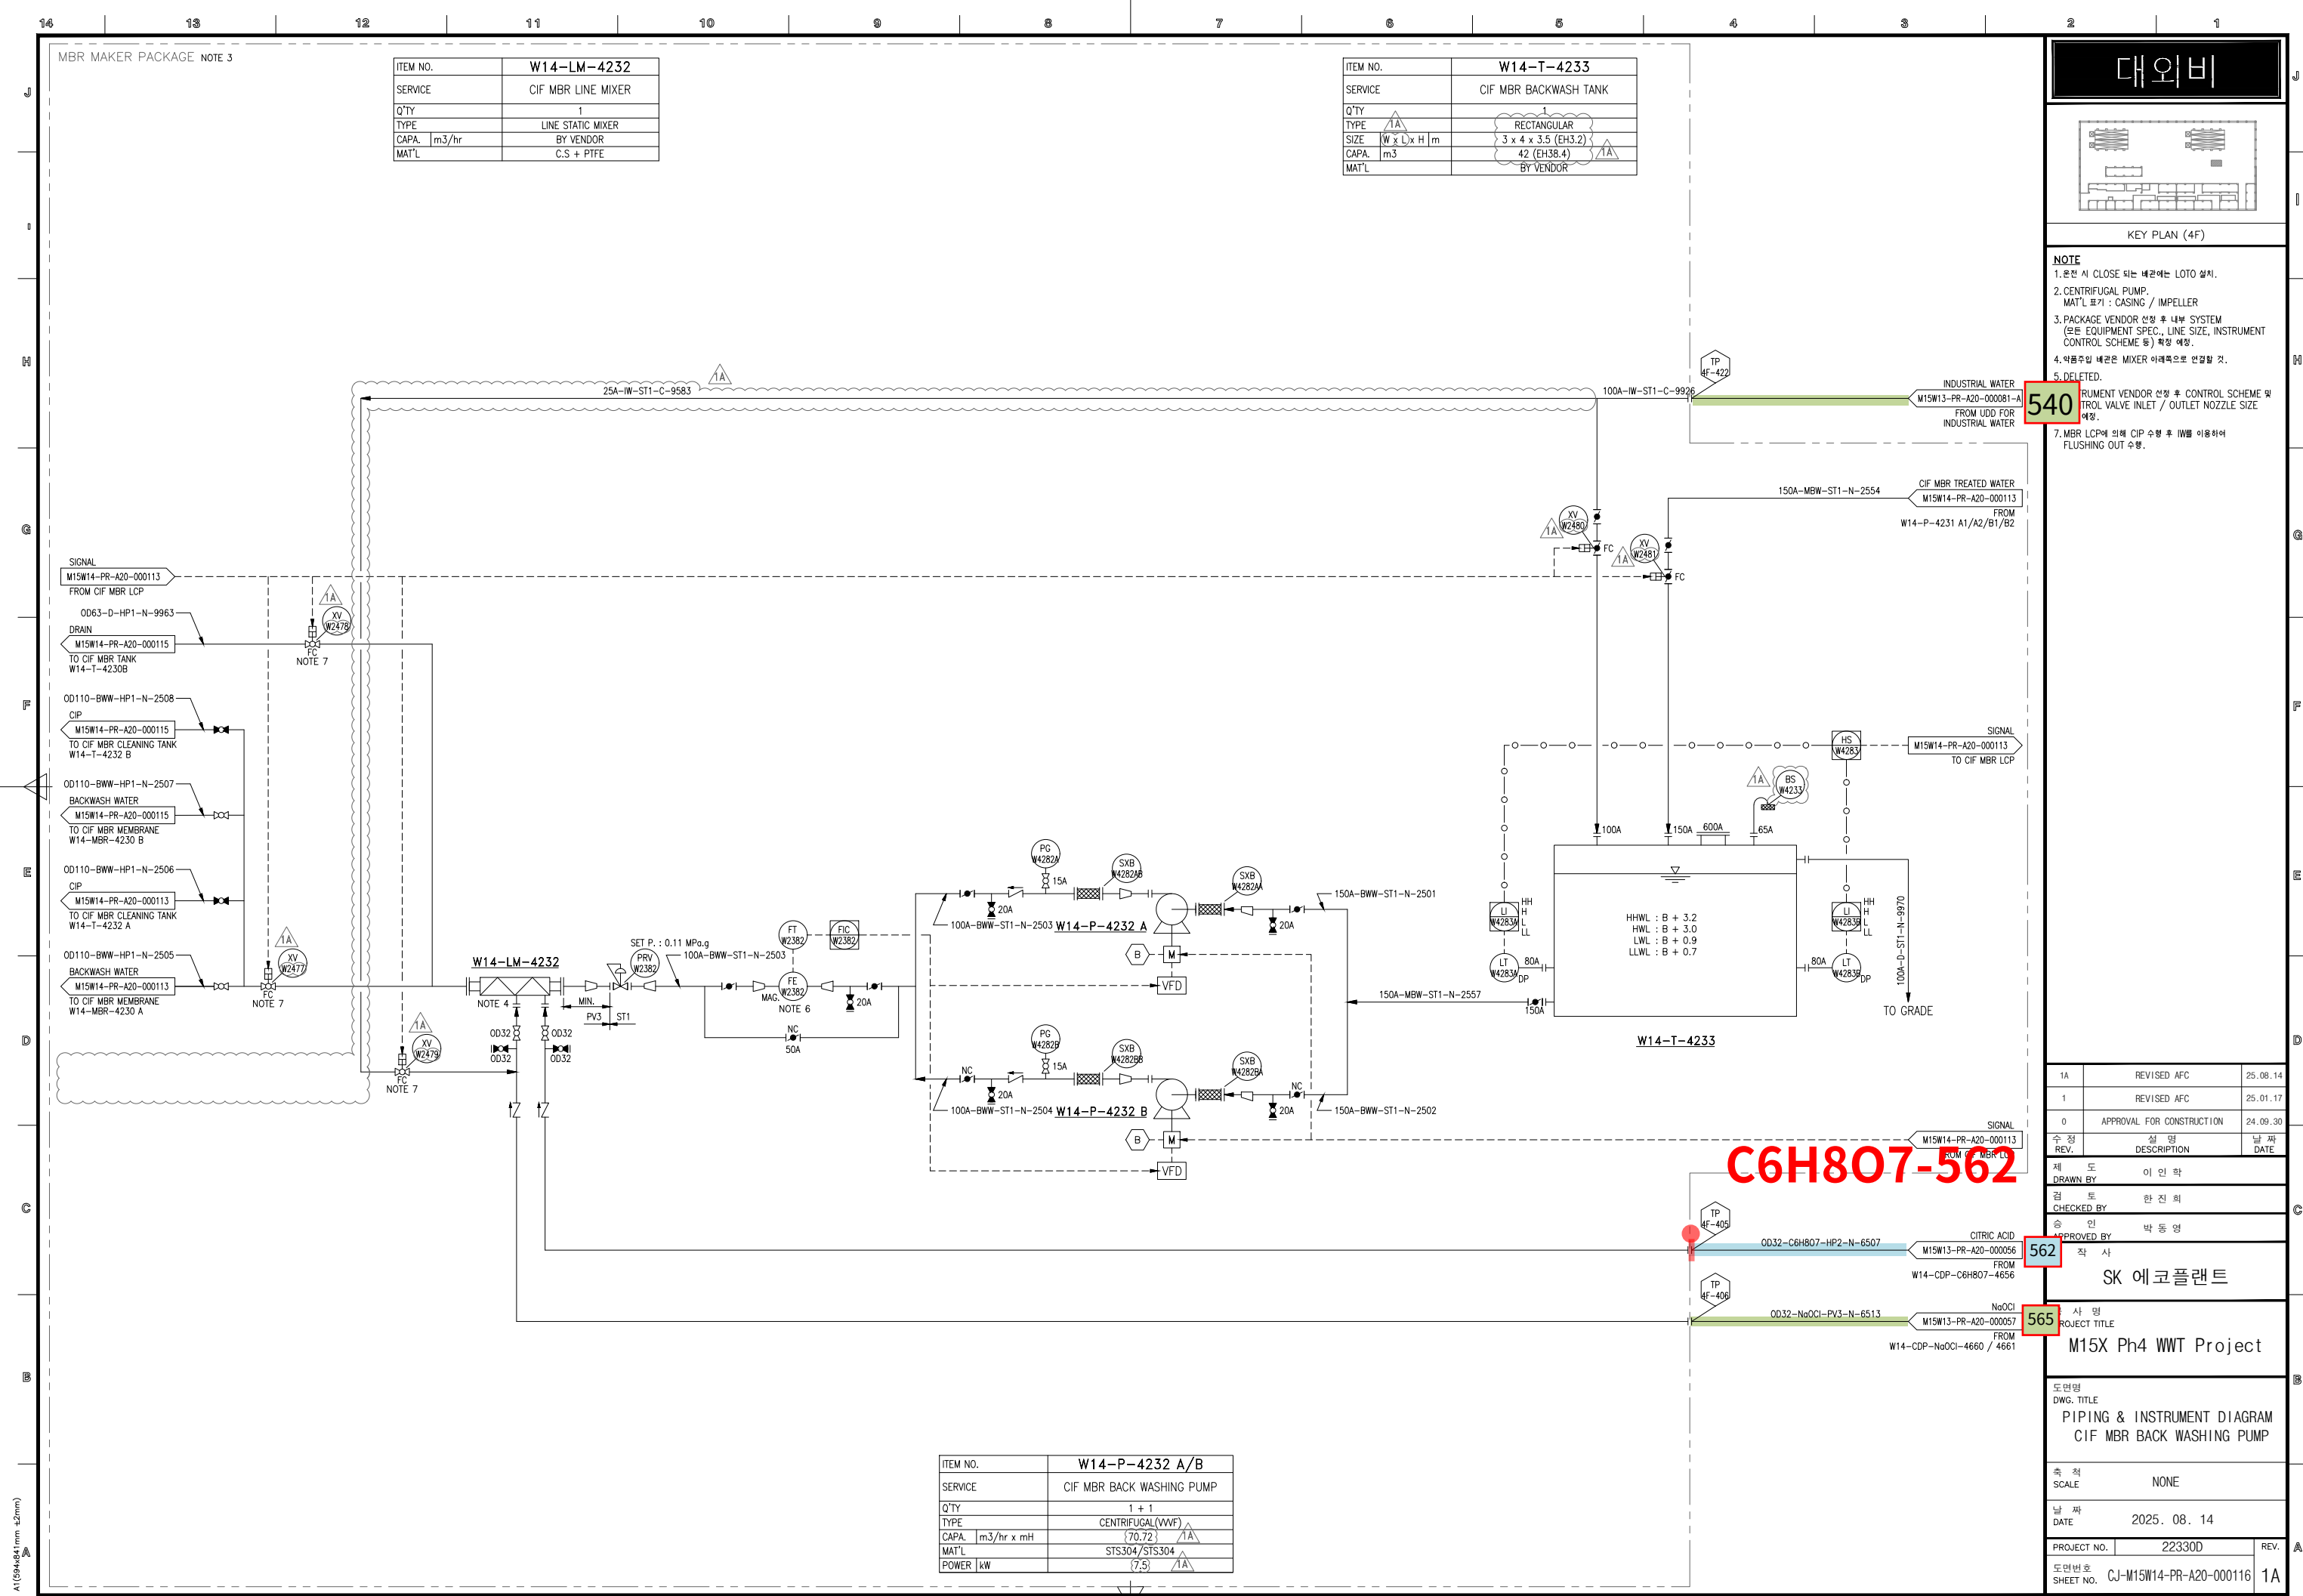

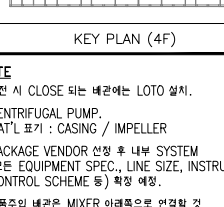대외비		
		
KEY PLAN (4F)		
NOTE 1. 운전 시 CLOSE 되는 배관에는 LOTO 설치. 2. CENTRIFUGAL PUMP. MAT'L 표기 : CASING / IMPELLER 3. PACKAGE VENDOR 선정 후 내부 SYSTEM (포트 EQUIPMENT SPEC., LINE SIZE, INSTRUMENT CONTROL SCHEME 등) 작성 예정. 4. 약품주입 배관은 MIXER 아래쪽으로 연결할 것. 5. DELETED.		
40	INSTRUMENT VENDOR 선정 후 CONTROL SCHEME 및 TROL VALVE INLET / OUTLET NOZZLE SIZE 예정. 7. MBR LCP에 의해 CIP 수행 후 IW를 이용하여 FLUSHING OUT 수행.	
1A	REVISED AFC	25.08.14
1	REVISED AFC	25.01.14
0	APPROVAL FOR CONSTRUCTION	24.09.30
수정 REV.	설 명 DESCRIPTION	날 짜 DATE
제 도 이 인 학 DRAWN BY		
검 토 한 진 회 CHECKED BY		
승 인 박 동 영 APPROVED BY		
62	작 사	
SK 에코플랜트		
55	사 명 PROJECT TITLE	
M15X Ph4 WWT Project		
도면명 DWG. TITLE		
PIPING & INSTRUMENT DIAGRAM CIF MBR BACK WASHING PUMP		
축 적 SCALE		
NONE		
날 짜 DATE		
2025. 08. 14		
PROJECT NO.	22330D	REV.
SHEET NO.	CJ-M15W14-PR-A20-000116	1A

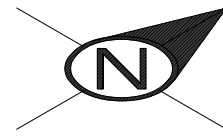

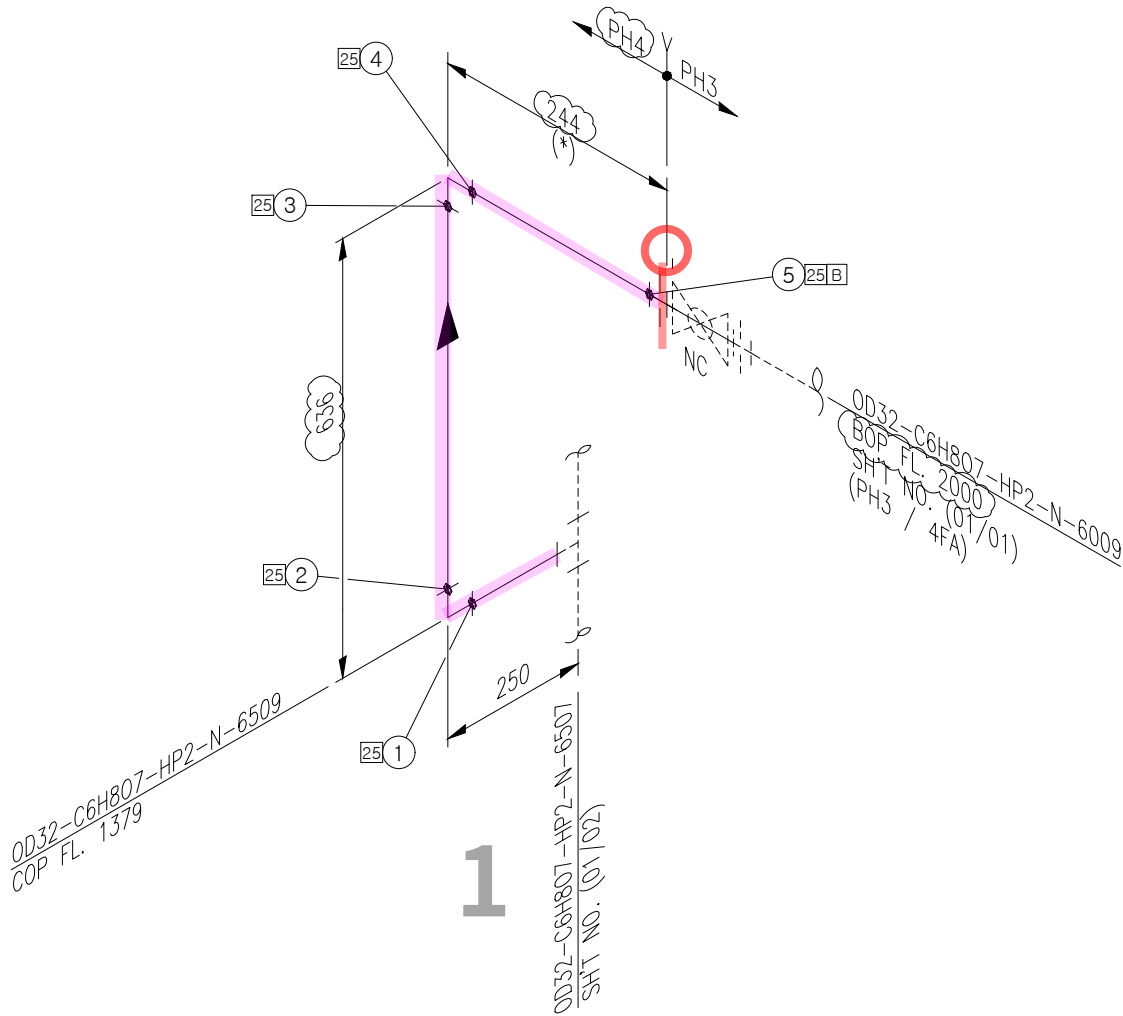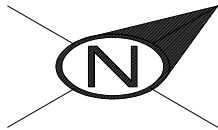

<NOTE>
1. TRAY & ANGLE,CHANNEL SUPPORT가 적용되는
배관 ELEVATION은 현장 맞춤으로 한다.
2. (*) FIELD ADJUST



ITEM	SIZE	Q'TY	DESCRIPTION
HP2			
P	OD32	1.1M	PIPE, HDPE PE100, PE, SOCKET FUSION, PN16/SDR11
E90	OD32	2EA	ELBOW 90 DEG, HDPE PE100, PE, SOCKET FUSION,
F	OD32	1EA	FLG LAP JOINT / STUB END SET, KS 10K, FF,
			LAP JOINT-ST304 / STUB END-HDPE PE100
G	OD32	1EA	GASKET, KS 10K, FF, PTFE+EPDM, 3.0MM TH'K
B	OD32	1SET	MACHINE BOLT & NUTS :STS 304 / W WASHERS
LOTO	OD32	1EA	LOTO

CLIENT



3

* PIPE : P/P1 * 90° ELBOW : E90 * 45° ELBOW : E45 * TEE : T * RED.TEE : TR * STUB-IN : STU * REINFORCING PAD : RP * CON.RED : RC * ECC.RED : RE * CON.SWAGE : RCS/RCS1 * ECC.SWAGE : RES/RES1 * NIPPLE : NP/NP1/NP2 * CAP : CAP/CAP1 * PLUG : PLG * FULL COUPLING : FC * HALF COUPLING : HF/HF1
* STUB-IN : STU * SOCKET(HDPE/PVC) : SC * SADDLE(HDPE) : SD * FLANGE : F/F1 * GASKET : G/G1/G2 * BOLT & NUT : B/B1 * BLIND FLANGE : FB/FB1 * GATE VA. : VG/VG1/VG2 * BALL VA. : VB/VBLO/VB1/VB1LO/VB2/VB2LO * BUTTERFLY VA. : VF/VF4 * CHECK VA. : VC/VC1/VC2/VC3/VC4/VC5/VC6/VC7
* GLOBE VA. : VL/VL1/VL2 * DIAPHRAGM VA. : VD/VDLO * DAMPER : VP * QUICK COUPLING : SQC * FLEXIBLE JOINT(STEEL) : FLXB * FLEXIBLE JOINT(RUBBER) : FLXR * FLEXIBLE JOINT(STEEL PTFE LINED) : FLXL * FLEXIBLE HOSE : FLXH * STEAM TRAP : ST * SPRAY NOZZLE : SPN * EMERGENCY SHOWER : SSH
* STRAINER(Y-TYPE) : YSTR * STRAINER(T-TYPE) : TSTR * STRAINER(BUCKET-TYPE) : BSTR * ANCHOR PLATE : STOP * BIRD SCREEN : BS * ISOLATION KIT : IK * UNLOADING BOX : UB * AIR TRAP : AT * LOTO : LOTO * SIGHT GLASS : SG * PRESSURE GAUGE : PG * SHILED : SH * SPECIAL BOLT & NUT : BL/BL1

INSULATION	CODE	N	CONDITION	PRESS. (kg/cm2g)	TEMP. (°C)	AREA	W14									CONTRACTOR	PROJECT NAME
	THICK.	-	DESIGN	1.0	60	UNIT	4FA										
			OPERATING	ATM	AMB	REF. PLAN DWG.			25.01.24	APPROVED FOR CONSTRUCTION	황래중	안남후	박동영				M15X Ph4 Project
						CJ-M15W14-PI-A30-040009-A											
						REF. P & ID		REV. NO.	DATE	DESCRIPTION	BY	CHK	APP'D			COMMODITY	JOB NO.
						CJ-M15W13-PR-A20-000056											
																C6H807	22330D
																LINE NO.	SH'T NO.
																OD32-C6H807-HP2-N-6509	01 / 01
																	REV.
																	0