

DRAWING LIST FOR TEST PACKAGE


PROJECT NO.: 22328D

PROJECT TITLE : M15X Ph2 Project

NaOCI-563


No	PKG No	UNIT	LINE NUMBER			P&ID		REMARK
			ISO DRAWING No	SHEET	REV	P&ID No	REV	
1	563	4FA	OD32-NaOCI-PV3-N-7027-01	1 OF 2	0	CJ-M15W14-PR-A20-000315	1A	
2	563	4FA	OD32-NaOCI-PV3-N-7027-02	2 OF 2	1	CJ-M15W13-PR-A20-000057	2	
3	563	4FA	OD32-NaOCI-PV3-N-7028-01	1 OF 1	0	CJ-M15W14-PR-A20-000315	1A	

NaOCI-563

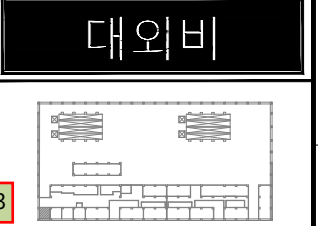

KEY PLAN (4F)

- NOTE**
1. 본선 시 CLOSE 되는 배관에는 LOTO 설치.
 2. DIAPHRAGM PUMP
MAT'L 표기 : HEAD / DIAPHRAGM / CHECK BALL
작동종류에 따라 LINE 역상을 구분하여야 한다.
 3. CHEMICAL ROOM 내 TRENCH & PIT DRAIN
DRAIN HEADER를 통하여 근처의 인접한 수조로 유입된다.
 4. PUMP VENDOR 공급.
 5. INTERLOCK NO. I-7021
(W14-CDP-NaOCI-4752 A/B,
W14-CDP-NaOCI-4753 A/B AUTO STOP)
: REMOTE STATUS에서 W13-T-NaOCI-4609
LEVEL (LI-W6020) LOW LOW STOP.
BRINE MBR CIP/BACK WASH 시 START/STOP.
 6. INTERLOCK NO. I-7022
(W14-CDP-NaOCI-4703 A/B,
W14-CDP-NaOCI-4704 A/B,
W14-CDP-NaOCI-4705 A/B AUTO STOP)
: REMOTE STATUS에서 W13-T-NaOCI-4609
LEVEL (LI-W6020) LOW LOW STOP.
 7. REUSE SYSTEM 및 BRINE 처리 SYSTEM의 공급용 PUMP
주변의 LEAK DETECTOR는 기 공급함.
(LDS-W6438/W6439)
 8. OPERATING CAPACITY : 5 LPM
OPERATING PRESSURE : 0.49 MPa
 9. OPERATING CAPACITY : 3 LPM
OPERATING PRESSURE : 0.29 MPa
 10. OPERATING CAPACITY : 8 LPM
OPERATING PRESSURE : 0.29 MPa
 11. OPERATING CAPACITY : 1 LPM
OPERATING PRESSURE : 0.29 MPa
 12. OPERATING CAPACITY : 10 LPM
OPERATING PRESSURE : 0.29 MPa

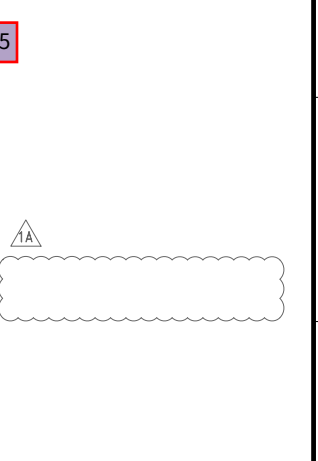

1A	REVISED AFC	25.08.14
1	REVISED AFC	25.01.17
0	APPROVAL FOR CONSTRUCTION	24.10.31
수정	REV.	실명
수정	REV.	DESCRIPTION
수정	REV.	날짜
수정	REV.	DATE

제 도	이 인 학
검 토	한 진 희
승 인	박 동 영
APPROVED BY	
제 작 사	

SK 에코플랜트


공 사 명
PROJECT TITLE
M15X Ph4 WWT Project

도면명
DWG. TITLE
PIPING & INSTRUMENT DIAGRAM
NaOCI FEED PUMP


속 척
SCALE
NONE

날 짜
DATE
2025. 08. 14


PROJECT NO. 22330D
SHEET NO. CJ-M15W14-PR-A20-000315
도면번호
1A

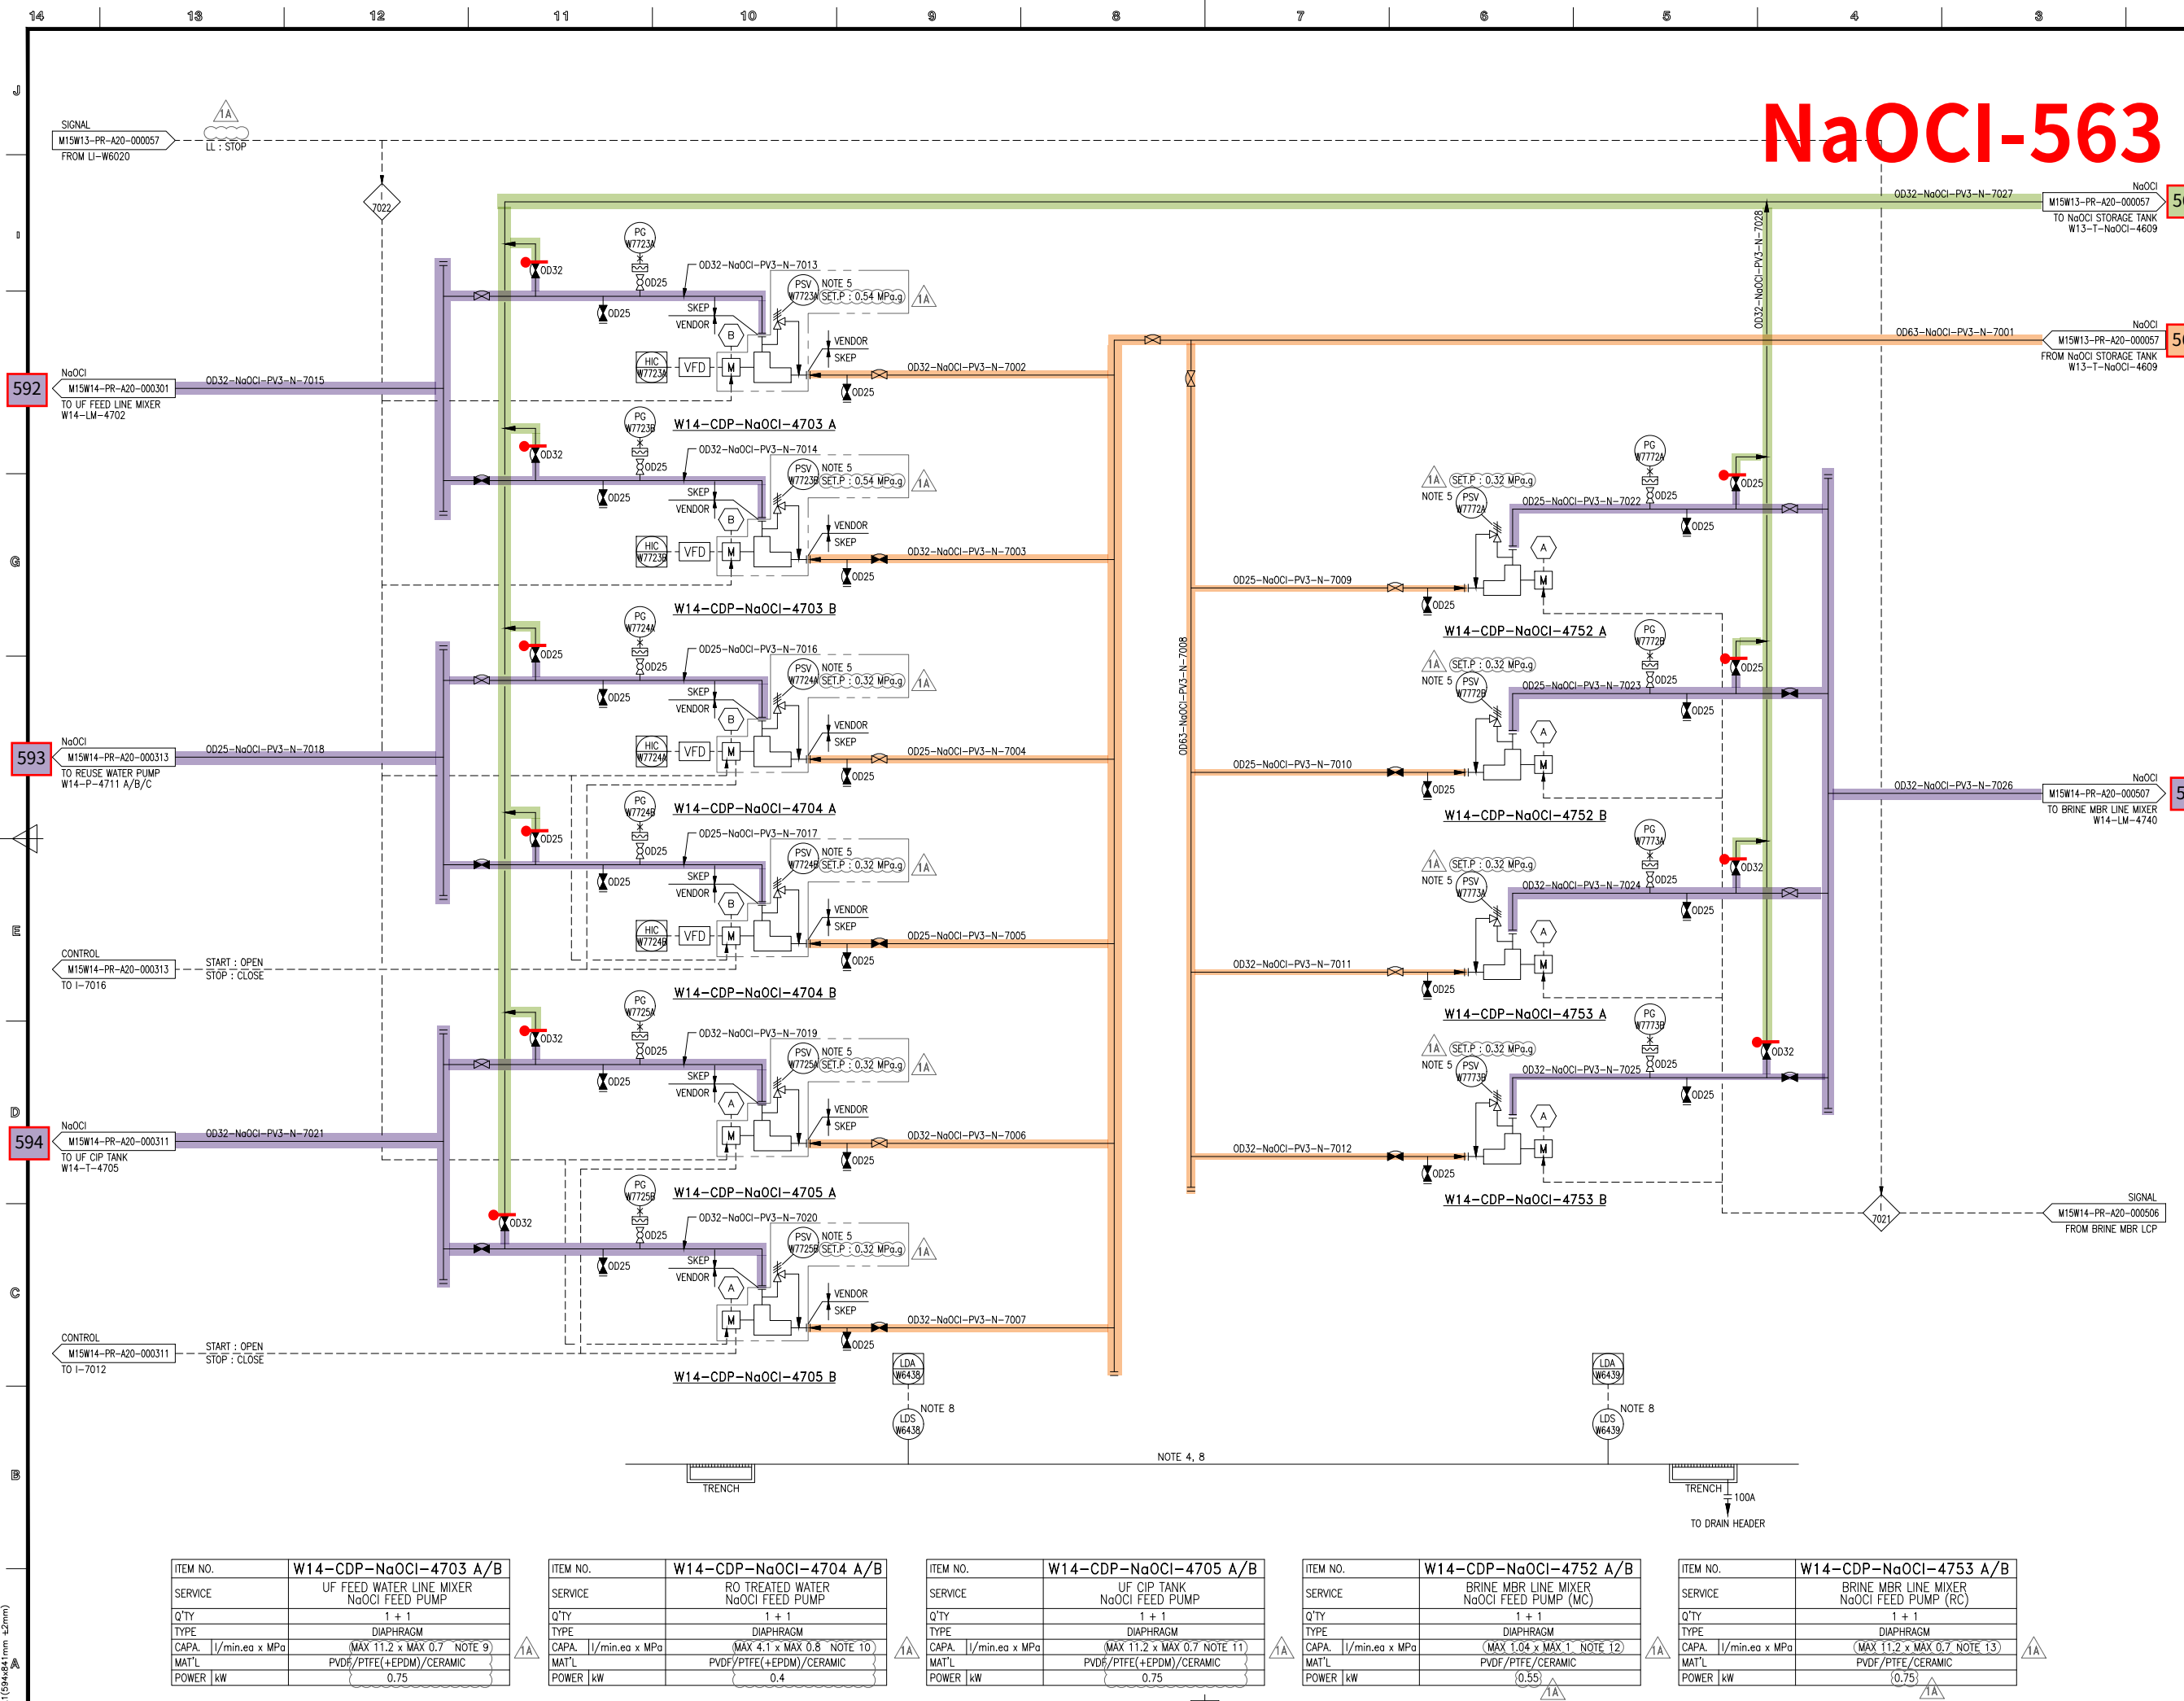

ITEM NO.	W14-CDP-NaOCI-4703 A/B	ITEM NO.	W14-CDP-NaOCI-4704 A/B	ITEM NO.	W14-CDP-NaOCI-4705 A/B	ITEM NO.	W14-CDP-NaOCI-4752 A/B	ITEM NO.	W14-CDP-NaOCI-4753 A/B
SERVICE	UF FEED WATER LINE MIXER NaOCI FEED PUMP	SERVICE	RO TREATED WATER NaOCI FEED PUMP	SERVICE	UF CIP TANK NaOCI FEED PUMP	SERVICE	BRINE MBR LINE MIXER NaOCI FEED PUMP (MC)	SERVICE	BRINE MBR LINE MIXER NaOCI FEED PUMP (RC)
Q'TY	1 + 1	Q'TY	1 + 1	Q'TY	1 + 1	Q'TY	1 + 1	Q'TY	1 + 1
TYPE	DIAPHRAGM	TYPE	DIAPHRAGM	TYPE	DIAPHRAGM	TYPE	DIAPHRAGM	TYPE	DIAPHRAGM
CAPA.	1/min.ea x MPa (MAX 11.2 x MAX 0.7 NOTE 9)	CAPA.	1/min.ea x MPa (MAX 4.1 x MAX 0.8 NOTE 10)	CAPA.	1/min.ea x MPa (MAX 11.2 x MAX 0.7 NOTE 11)	CAPA.	1/min.ea x MPa (MAX 1.04 x MAX 1. NOTE 12)	CAPA.	1/min.ea x MPa (MAX 11.2 x MAX 0.7 NOTE 13)
MAT'L	PVDF/PTFE(+EPDM)/CERAMIC	MAT'L	PVDF/PTFE(+EPDM)/CERAMIC	MAT'L	PVDF/PTFE(+EPDM)/CERAMIC	MAT'L	PVDF/PTFE/CERAMIC (0.55)	MAT'L	PVDF/PTFE/CERAMIC (0.75)
POWER kW	0.75	POWER kW	0.4	POWER kW	0.75	POWER kW		POWER kW	

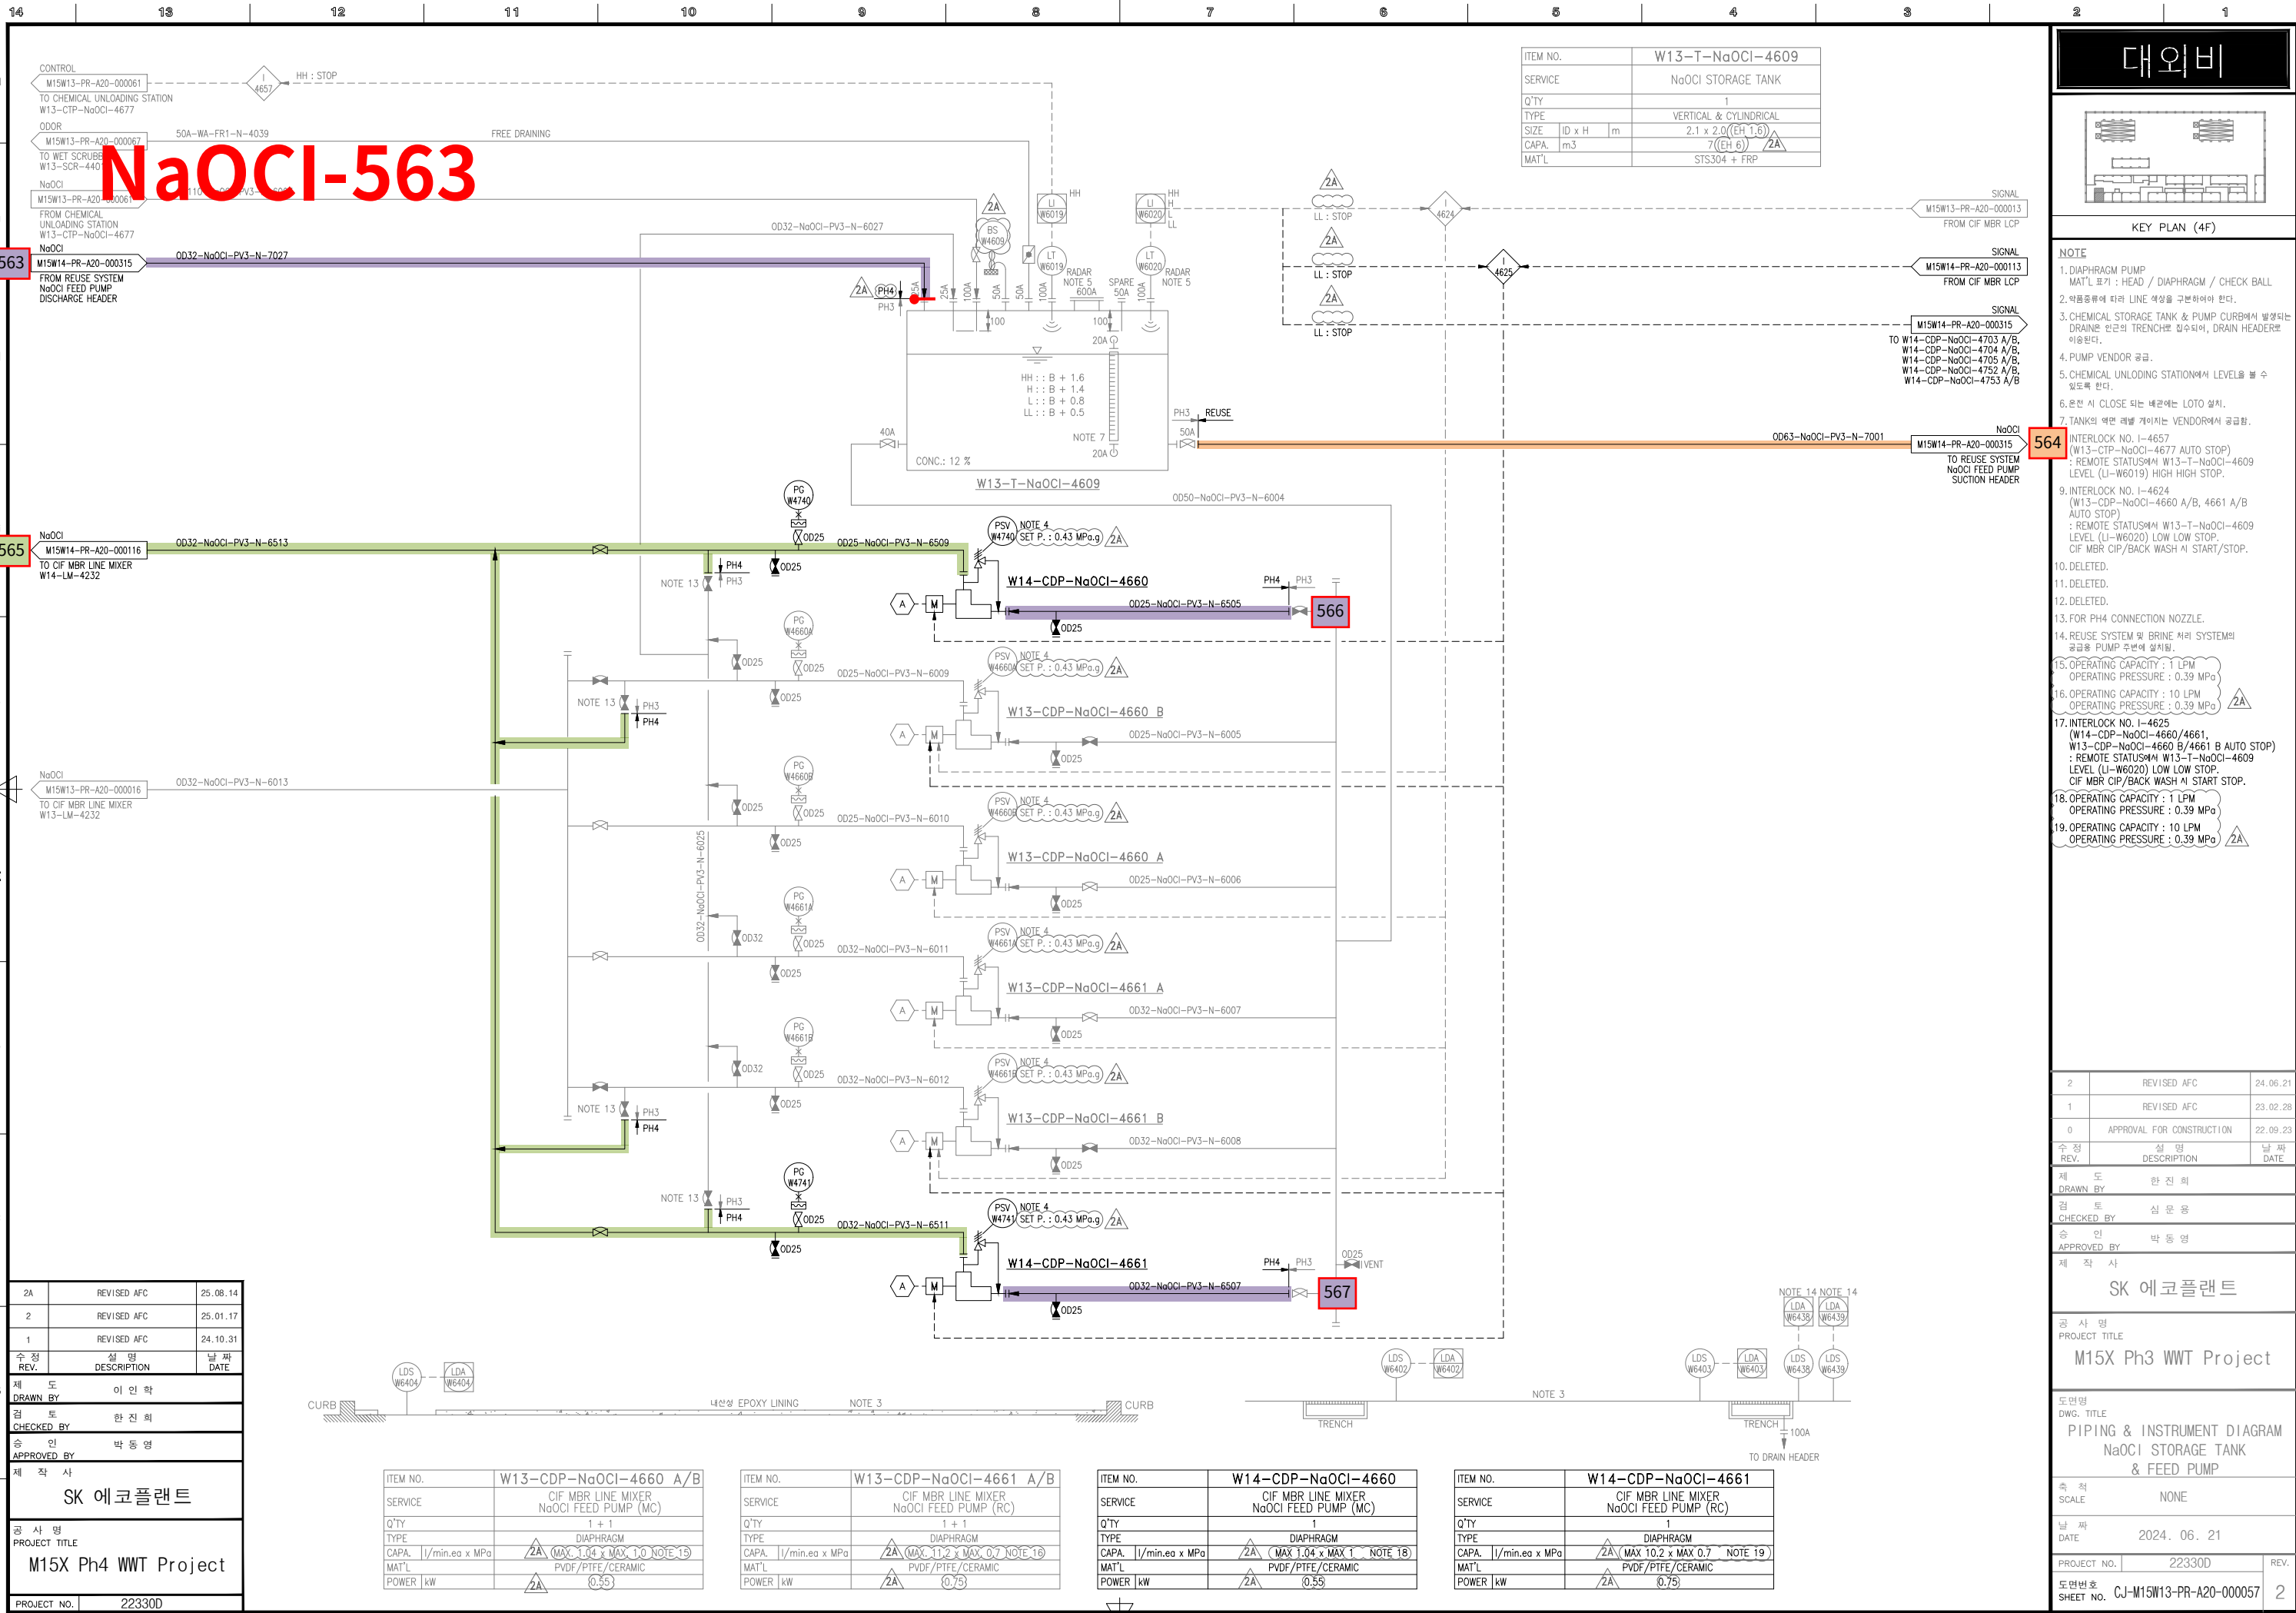

대외비

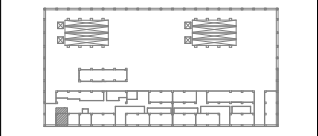

KEY PLAN (4F)

- NOTE
1. DIAPHRAGM PUMP
MAT'L 표기 : HEAD / DIAPHRAGM / CHECK BALL
 2. 약품종류에 따라 LINE 색상을 구분하여야 한다.
 3. CHEMICAL STORAGE TANK & PUMP CURB에서 발생하는 DRAIN에 인근의 TRENCH로 흡수되어, DRAIN HEADER로 이용된다.
 4. PUMP VENDOR 규격.
 5. CHEMICAL UNLOADING STATION에서 LEVEL을 볼 수 있도록 한다.
 6. 운전 시 CLOSE 되는 배관에는 LOTO 설치.
 7. TANK의 역면 레벨 게이지는 VENDOR에서 공급함.
 8. INTERLOCK NO. I-4657
(W13-CTP-NaOCI-4677 AUTO STOP)
: REMOTE STATUS에서 W13-T-NaOCI-4609 LEVEL (U-W6019) HIGH HIGH STOP.
 9. INTERLOCK NO. I-4624
(W13-CDP-NaOCI-4660 A/B, 4661 A/B AUTO STOP)
: REMOTE STATUS에서 W13-T-NaOCI-4609 LEVEL (U-W6020) LOW LOW STOP.
CIF MBR CIP/BACK WASH 시 START/STOP.
 10. DELETED.
 11. DELETED.
 12. DELETED.
 13. FOR PH4 CONNECTION NOZZLE.
 14. REUSE SYSTEM 및 BRINE 처리 SYSTEM의 공급용 PUMP 수단에 설치함.
 15. OPERATING CAPACITY : 1 LPM
OPERATING PRESSURE : 0.39 MPa
 16. OPERATING CAPACITY : 10 LPM
OPERATING PRESSURE : 0.39 MPa
 17. INTERLOCK NO. I-4625
(W14-CDP-NaOCI-4660/4661, W13-CDP-NaOCI-4660 B/4661 B AUTO STOP)
: REMOTE STATUS에서 W13-T-NaOCI-4609 LEVEL (U-W6020) LOW LOW STOP.
CIF MBR CIP/BACK WASH 시 START STOP.
 18. OPERATING CAPACITY : 1 LPM
OPERATING PRESSURE : 0.39 MPa
 19. OPERATING CAPACITY : 10 LPM
OPERATING PRESSURE : 0.39 MPa

2	REVISED AFC	24.06.21
1	REVISED AFC	23.02.28
0	APPROVAL FOR CONSTRUCTION	22.09.23

수정 REV.	설명 DESCRIPTION	날짜 DATE
제 도	이 인 회	
검 토	심 문 용	
승 인	박 동 영	

제 작 사

SK 에코플랜트

공 사 명
PROJECT TITLE
M15X Ph3 WWT Project

도면명
DWG. TITLE
PIPING & INSTRUMENT DIAGRAM
NaOCI STORAGE TANK
& FEED PUMP


속 척
SCALE
NONE

날 짜
DATE
2024. 06. 21

PROJECT NO. 22330D

REVISION SHEET NO. CJ-M15W13-PR-A20-000057

2

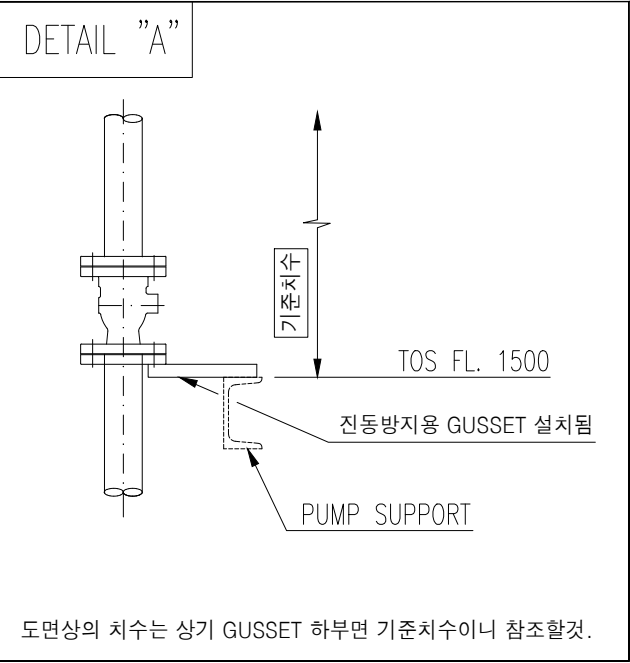[illegible]

<NOTE>
1. TRAY & ANGLE, CHANNEL SUPPORT가 적용되는
배관 ELEVATION은 현장 맞춤으로 한다.
2. (*) FIELD ADJUST

[illegible]

CLIENT		1	
			
CONTRACTOR		PROJECT NAME	
		M15X Ph4 Project	
COMMODITY		JOB NO.	
NaOCI		22330D	
LINE NO.		SH'T NO.	REV.
0D32-NaOCI-PV3-N-7027		01 / 02	0

* PIPE : P/P1 * 90° ELBOW : E90 * 45° ELBOW : E45 * TEE : T * RED.TEE : TR * STUB-IN : STU * REINFORCING PAD : RP * CON.RED : RC * ECC.RED : RE * CON.SWAGE : RCS/RCS1 * ECC.SWAGE : RES/RES1 * NIPPLE : NP/NP1/NP2 * CAP : CAP/CAP1 * PLUG : PLG * FULL COUPLING : FC * HALF COUPLING : HF/HF1 * STUB-IN : STU * SOCKET(HDPE/PVC) : SC * SADDLE(HDPE) : SD * FLANGE : F/F1 * GASKET : G/G1/G2 * BOLT & NUT : B/B1 * BLIND FLANGE : FB/FB1 * GATE VA. : VG/VG1/VG2 * BALL VA. : VB/VBLO/VB1/VB1LO/VB2/VB2LO * BUTTERFLY VA. : VF/VF4 * CHECK VA. : VC/VC1/VC2/VC3/VC4/VC5/VC6/VC7 * GLOBE VA. : VL/VL1/VL2 * DIAPHRAGM VA. : VD/VDLO * DAMPER : VP * QUICK COUPLING : SQC * FLEXIBLE JOINT(STEEL) : FLXB * FLEXIBLE JOINT(RUBBER) : FLXR * FLEXIBLE JOINT(STEEL PTFE LINED) : FLXL * FLEXIBLE HOSE : FLXH * STEAM TRAP : ST * SPRAY NOZZLE : SPN * EMERGENCY SHOWER : SSH * STRAINER(Y-TYPE) : YSTR * STRAINER(T-TYPE) : TSTR * STRAINER(BUCKET-TYPE) : BSTR * ANCHOR PLATE : STOP * BIRD SCREEN : BS * ISOLATION KIT : IK * UNLOADING BOX : UB * AIR TRAP : AT * LOTO : LOTO * SIGHT GLASS : SG * PRESSURE GAUGE : PG * SHILED : SH * SPECIAL BOLT & NUT : BL/BL1												
INSULATION	CODE	N	CONDITION	PRESS. (kg/cm2g)	TEMP. (°C)	AREA W14						
	THICK.	-	DESIGN	3.3	60	UNIT 4FA						
			OPERATING	3.0	AMB	REF. PLAN DWG. CJ-M15W14-PI-A30-040010-A		25.01.24	APPROVED FOR CONSTRUCTION	황래중	안남후	박동영
						REF. P & ID CJ-M15W14-PR-A20-000315						
						REV. NO.	DATE	DESCRIPTION	BY	CHK	APP	

