


PROJECT NO.: 22328D

PROJECT TITLE : M15X Ph2 Project

1 OF 1

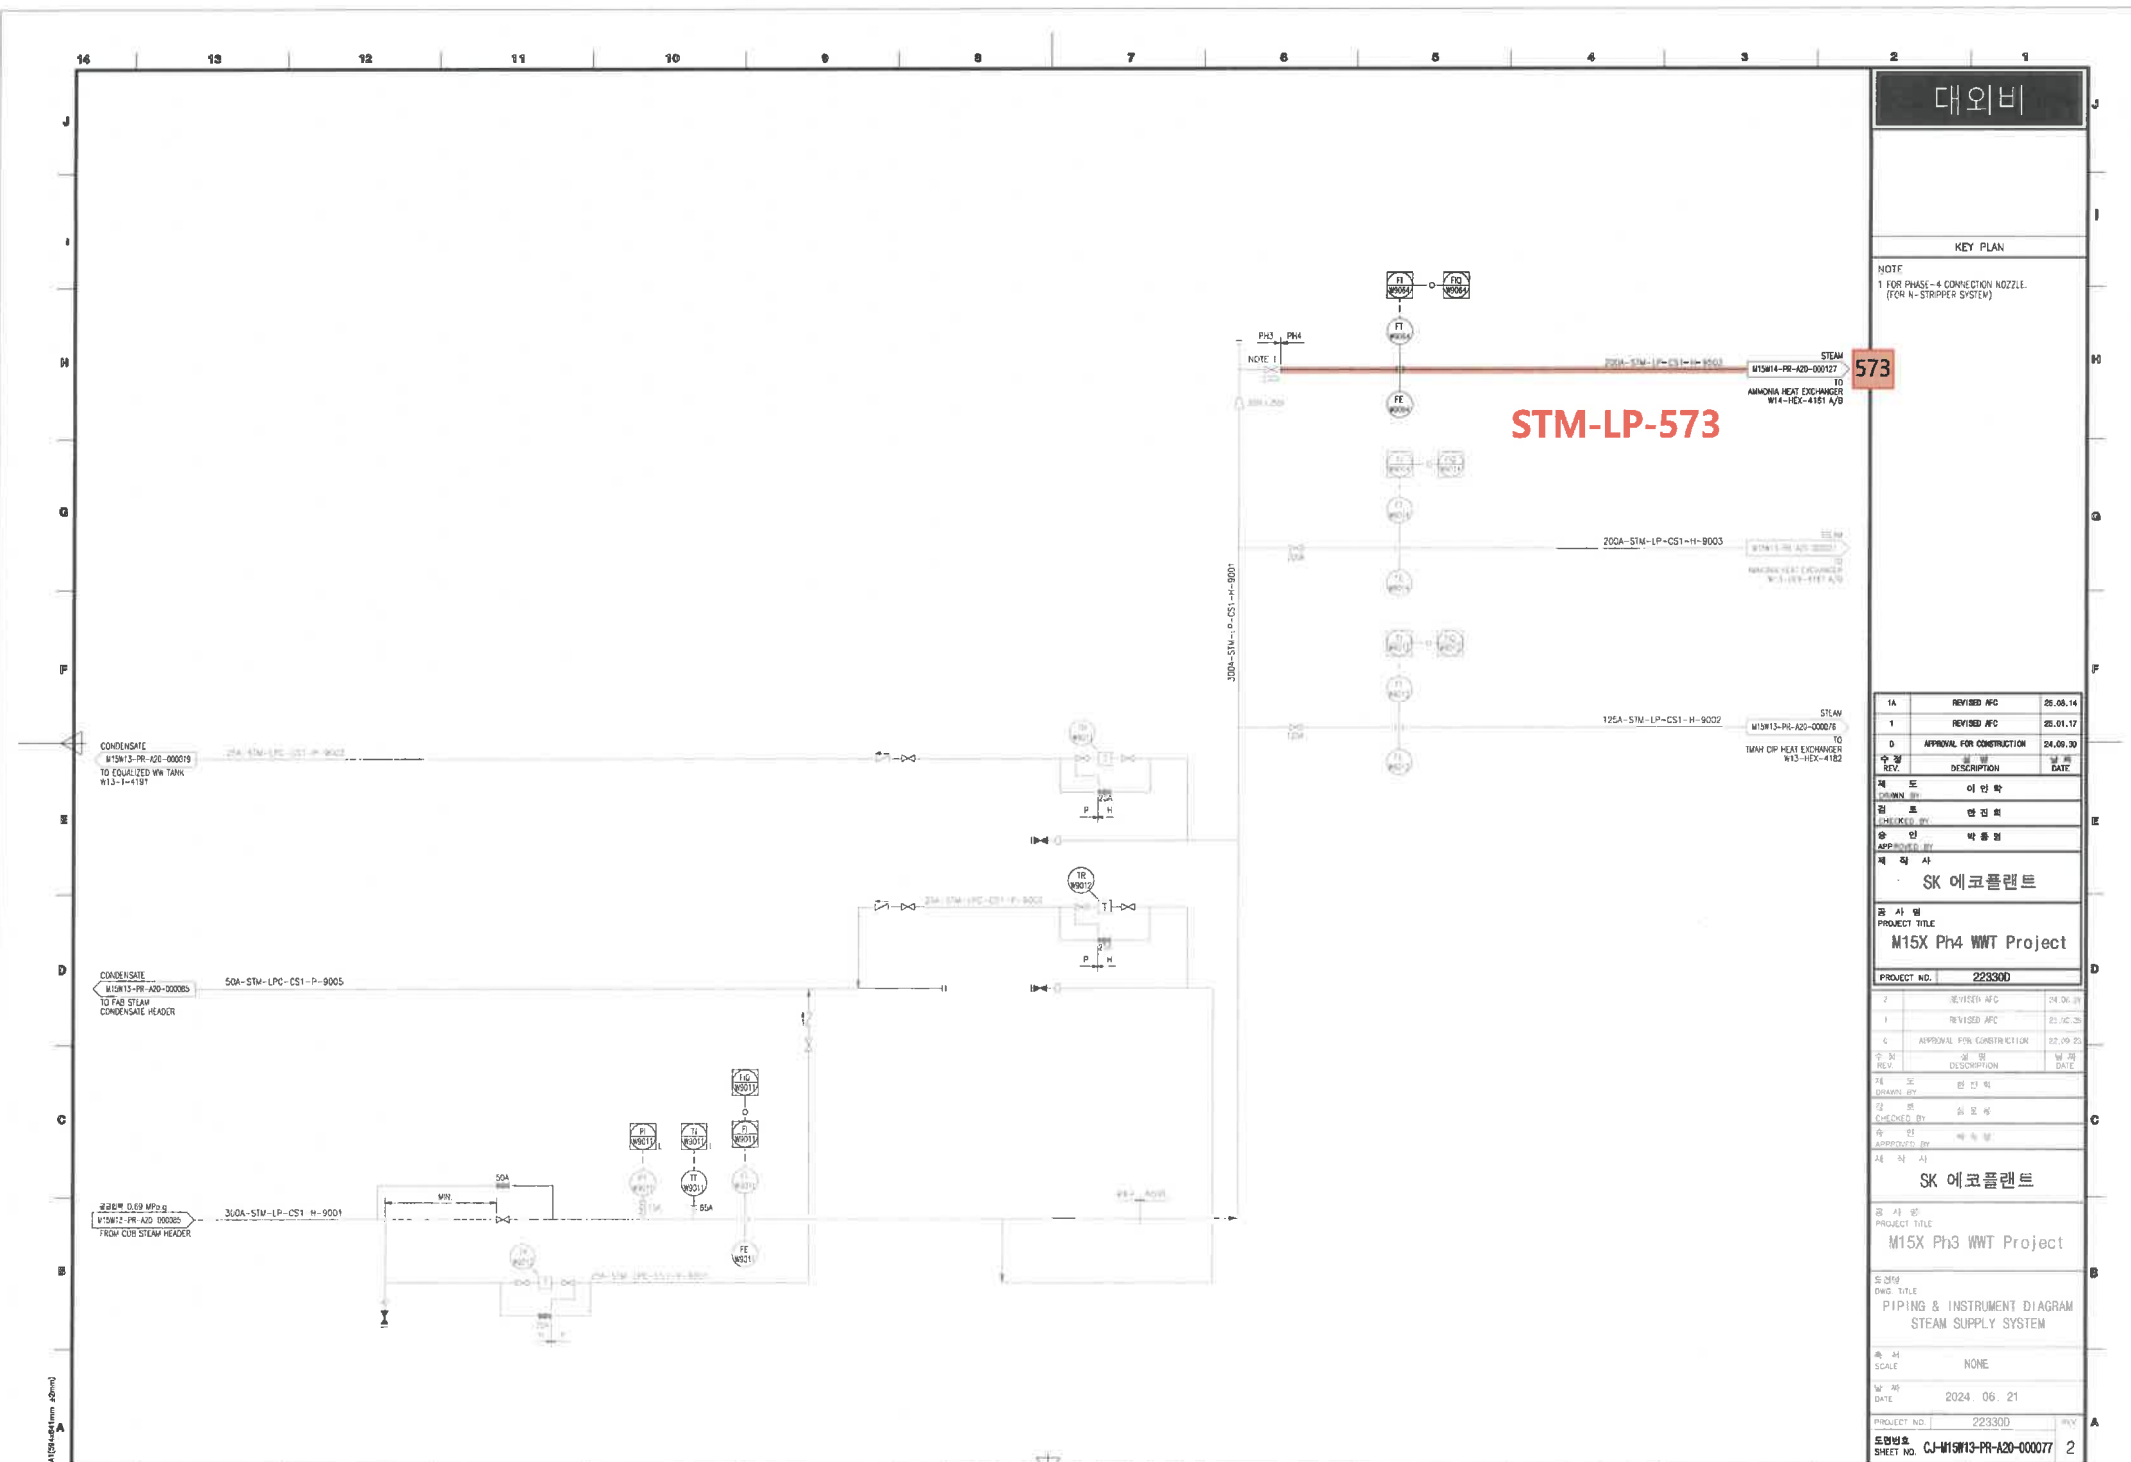

대외비

KEY PLAN
NOTE
1 FOR PHASE-4 CONNECTION NOZZLE.
(FOR N-STRIPPER SYSTEM)

573

STM-LP-573

1A	REVISED A/C	25.05.14
1	REVISED A/C	25.01.17
0	APPROVAL FOR CONSTRUCTION	24.09.20

주최	설계	날짜
REV	DESCRIPTION	DATE
제 도	이 인 학	
검 토	안 진 희	
승 인	박 용 정	
적 의 사		


SK 에코플랜트
공 사 명
PROJECT TITLE
M15X Ph4 WWT Project
PROJECT NO. 223300

2	REVISED A/C	24.05.14
1	REVISED A/C	23.05.25
0	APPROVAL FOR CONSTRUCTION	22.09.20

주최	설계	날짜
REV	DESCRIPTION	DATE
제 도	이 인 학	
검 토	안 진 희	
승 인	박 용 정	
적 의 사		

SK 에코플랜트
공 사 명
PROJECT TITLE
M15X Ph3 WWT Project
PIPING & INSTRUMENT DIAGRAM
STEAM SUPPLY SYSTEM

제 도	SCALE	NONE
날 짜	DATE	2024. 06. 21
PROJECT NO.	223300	REV
도면번호	SHEET NO. CJ-M15W13-PR-A20-000077	2

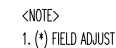


1

[illegible]



ITEM	SIZE	Q'TY	DESCRIPTION
CS1			
P	200A	73.8M	PIPE, CS SPSS250, ERW, BE - SCH 40
E90	200A	4EA	ELBOW 90 DEG SR, CS SPSS250, ERW, BE - SCH 40
F	200A	1EA	FLG SO, KS 10K, RF, CS SS275
G	200A	1EA	GASKET SPIRAL WOUND, KS 10K, RF, 3.0MM TH'K
B	200A	1SET	MACHINE BOLT & NUTS :SM45C & GAL'V / W WASHERS
IN	75tx200A	73.8MM	관 보온재(GRASS WOOL)

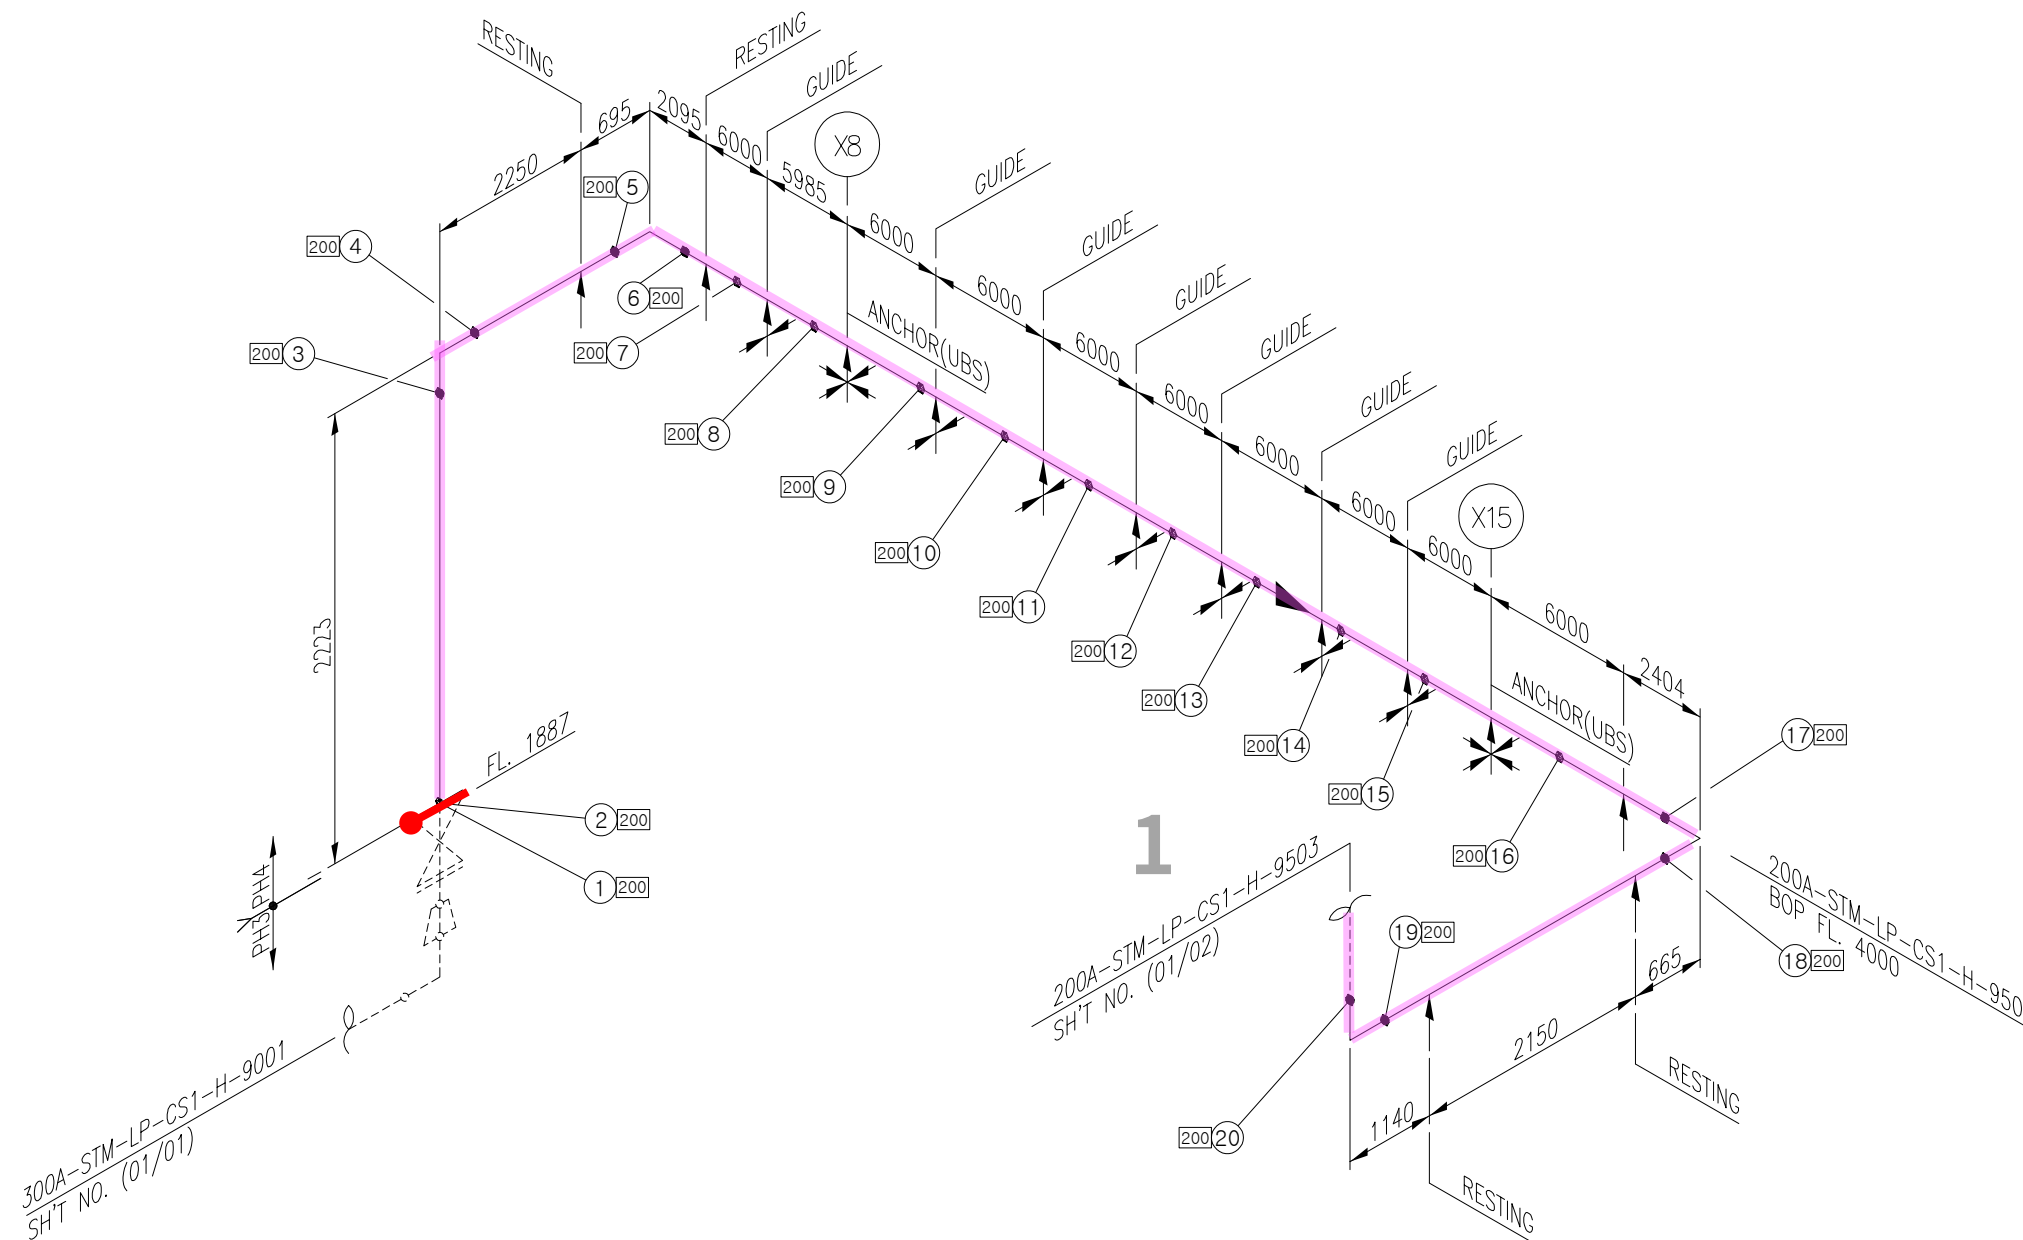

<NOTE>

1. (*) FIELD ADJUST

* PIPE : P/P1	* 90° ELBOW : E90	* 45° ELBOW : E45	* TEE : T	* RED.TEE : TR	* STUB-IN : STU	* REINFORCING PAD : RP	* CON.RED : RC	* ECC.RED : RE	* CON.SWAGE : RCS/RCS1	* ECC.SWAGE : RES/RES1	* NIPPLE : NP/NP1/NP2	* CAP : CAP/CAP1	* PLUG : PLG	* FULL COUPLING : FC	* HALF COUPLING : HF/HF1
* STUB-IN : STU	* SOCKET(HDPE/PVC) : SC	* SADDLE(HDPE) : SD	* FLANGE : F/F1	* GASKET : G/G1/G2	* BOLT & NUT : B/B1	* BLIND FLANGE : FB/FB1	* GATE VA. : VG/VG1/VG2	* BALL VA. : VB/VBLO/VB1/VB1LO/VB2/VB2LO	* BUTTERFLY VA. : VF/VF4	* CHECK VA. : VC/VC1/VC2/VC3/VC4/VC5/VC6/VC7					
* GLOBE VA. : VL/VL1/VL2	* DIAPHRAGM VA. : VD/VDLO	* DAMPER : VP	* QUICK COUPLING : SQC	* FLEXIBLE JOINT(STEEL) : FLXB	* FLEXIBLE JOINT(RUBBER) : FLXR	* FLEXIBLE JOINT(STEEL PTFE LINED) : FLXL	* FLEXIBLE HOSE : FLXH	* STEAM TRAP : ST	* SPRAY NOZZLE : SPN	* EMERGENCY SHOWER : SSH					
* STRAINER(Y-TYPE) : YSTR	* STRAINER(T-TYPE) : TSTR	* STRAINER(BUCKET-TYPE) : BSTR	* ANCHOR PLATE : STOP	* BIRD SCREEN : BS	* ISOLATION KIT : IK	* UNLOADING BOX : UB	* AIR TRAP : AT	* LOTO : LOTO	* SIGHT GLASS : SG	* PRESSURE GAUGE : PG	* SHILED : SH	* SPECIAL BOLT & NUT : BL/BL1			

INSULATION	CODE	H	CONDITION	PRESS. (kg/cm2g)	TEMP. (°C)	AREA W14							CONTRACTOR	PROJECT NAME	
	THICK.	75	DESIGN	9.8	198.0	UNIT 5FA								M15X Ph4 Project	
			OPERATING	7.0	170.0	REF. PLAN DWG. CJ-M15W14-PI-A30-050008-A		25.01.24	APPROVED FOR CONSTRUCTION	황래중	안남후	박동영	COMMODITY	STM-LP	JOB NO.
						REF. P & ID CJ-M15W14-PR-A20-000127							LINE NO.	200A-STM-LP-CS1-H-9503	SH'T NO. 02 / 02
							REV. NO.	DATE	DESCRIPTION	BY	CHK	APP'D			

경고 : 본 도면은 SK HYNIX의 기밀비밀 자료로서, 어떠한 경우에도 목적 외 사용, 복제, 제3자에게 공개, 누설 및 유출할 수 없으며, 회사는 유포자의 불법 사용으로 피해가 발생할 경우 유포자에게 민/형사상 책임을 요구할 수 있음

[illegible]

<NOTE>

1. (*) FIELD ADJUST

* PIPE : P/P1	* 90° ELBOW : E90	* 45° ELBOW : E45	* TEE : T	* RED.TEE : TR	* STUB-IN : STU	* REINFORCING PAD : RP	* CON.RED : RC	* ECC.RED : RE	* CON.SWAGE : RCS/RCS1	* ECC.SWAGE : RES/RES1	* NIPPLE : NP/NP1/NP2	* CAP : CAP/CAP1	* PLUG : PLG	* FULL COUPLING : FC	* HALF COUPLING : HF/HF1
* STUB-IN : STU	* SOCKET(HDPE/PVC) : SC	* SADDLE(HDPE) : SD	* FLANGE : F/F1	* GASKET : G/G1/G2	* BOLT & NUT : B/B1	* BLIND FLANGE : FB/FB1	* GATE VA. : VG/VG1/VG2	* BALL VA. : VB/VBLO/VB1/VB1LO/VB2/VB2LO	* BUTTERFLY VA. : VF/VF4	* CHECK VA. : VC/VC1/VC2/VC3/VC4/VC5/VC6/VC7					
* GLOBE VA. : VL/VL1/VL2	* DIAPHRAGM VA. : VD/VDLO	* DAMPER : VP	* QUICK COUPLING : SQC	* FLEXIBLE JOINT(STEEL) : FLXB	* FLEXIBLE JOINT(RUBBER) : FLXR	* FLEXIBLE JOINT(STEEL PTFE LINED) : FLXL	* FLEXIBLE HOSE : FLXH	* STEAM TRAP : ST	* SPRAY NOZZLE : SPN	* EMERGENCY SHOWER : SSH					
* STRAINER(Y-TYPE) : YSTR	* STRAINER(T-TYPE) : TSTR	* STRAINER(BUCKET-TYPE) : BSTR	* ANCHOR PLATE : STOP	* BIRD SCREEN : BS	* ISOLATION KIT : IK	* UNLOADING BOX : UB	* AIR TRAP : AT	* LOTO : LOTO	* SIGHT GLASS : SG	* PRESSURE GAUGE : PG	* SHILED : SH	* SPECIAL BOLT & NUT : BL/BL1			

INSULATION	CODE	H	CONDITION	PRESS. (kg/cm2g)	TEMP. (°C)	AREA W14							CONTRACTOR	PROJECT NAME	
	THICK.	75	DESIGN	9.8	198.0	UNIT RFA								M15X Ph4 Project	
			OPERATING	7.0	170.0	REF. PLAN DWG. CJ-M15W14-PI-A30-R10008-A		25.01.24	APPROVED FOR CONSTRUCTION	황래중	안남후	박동영	COMMODITY	STM-LP	JOB NO.
						REF. P & ID CJ-M15W13-PR-A20-000077							REV. NO.	DATE	DESCRIPTION

경고 : 본 도면은 SK HYNIX의 기밀비밀 자료로서, 어떠한 경우에도 목적 외 사용, 복제, 제3자에게 공개, 누설 및 유출할 수 없으며, 회사는 유전자 정보의 사용으로 피해가 발생할 경우 유전자에게 민/형사상 책임을 물을 수 있습니다.

PUNCH LIST

Project No : 22330D
Project Title : M15X Ph3 Project

Package No :
Date :

S/N	Drawing No	Description	Category A B C	Punch Clear Status			
				작성자		확인자	
				Name	Sign	Name	Sign
1							
2							
Remarks

A : Before Hydro Test

B : Before M/C

C : Before Commissioning