


DRAWING LIST FOR TEST PACKAGE

D-578


PROJECT NO.: 22328D

PROJECT TITLE : M15X Ph2 Project

No	PKG No	UNIT	LINE NUMBER			P&ID		REMARK
			ISO DRAWING No	SHEET	REV	P&ID No	REV	
1	578	4FA	OD110-D-HP1-N-9648-01	1 OF 1	0	CJ-M15W13-PR-A20-000084		
2	578	4FA	OD110-D-HP1-N-9649-01	1 OF 1	0	CJ-M15W13-PR-A20-000084		
3	578	4FA	OD110-D-HP1-N-9950-01	1 OF 1	0	CJ-M15W13-PR-A20-000084		
4	578	4FA	OD110-D-HP1-N-9951-01	1 OF 1	0	CJ-M15W13-PR-A20-000084		
5	578	4FA	OD160-D-HP1-N-9605-01	1 OF 2	0	CJ-M15W13-PR-A20-000084		
6	578	4FA	OD160-D-HP1-N-9605-02	2 OF 2	0	CJ-M15W13-PR-A20-000084		

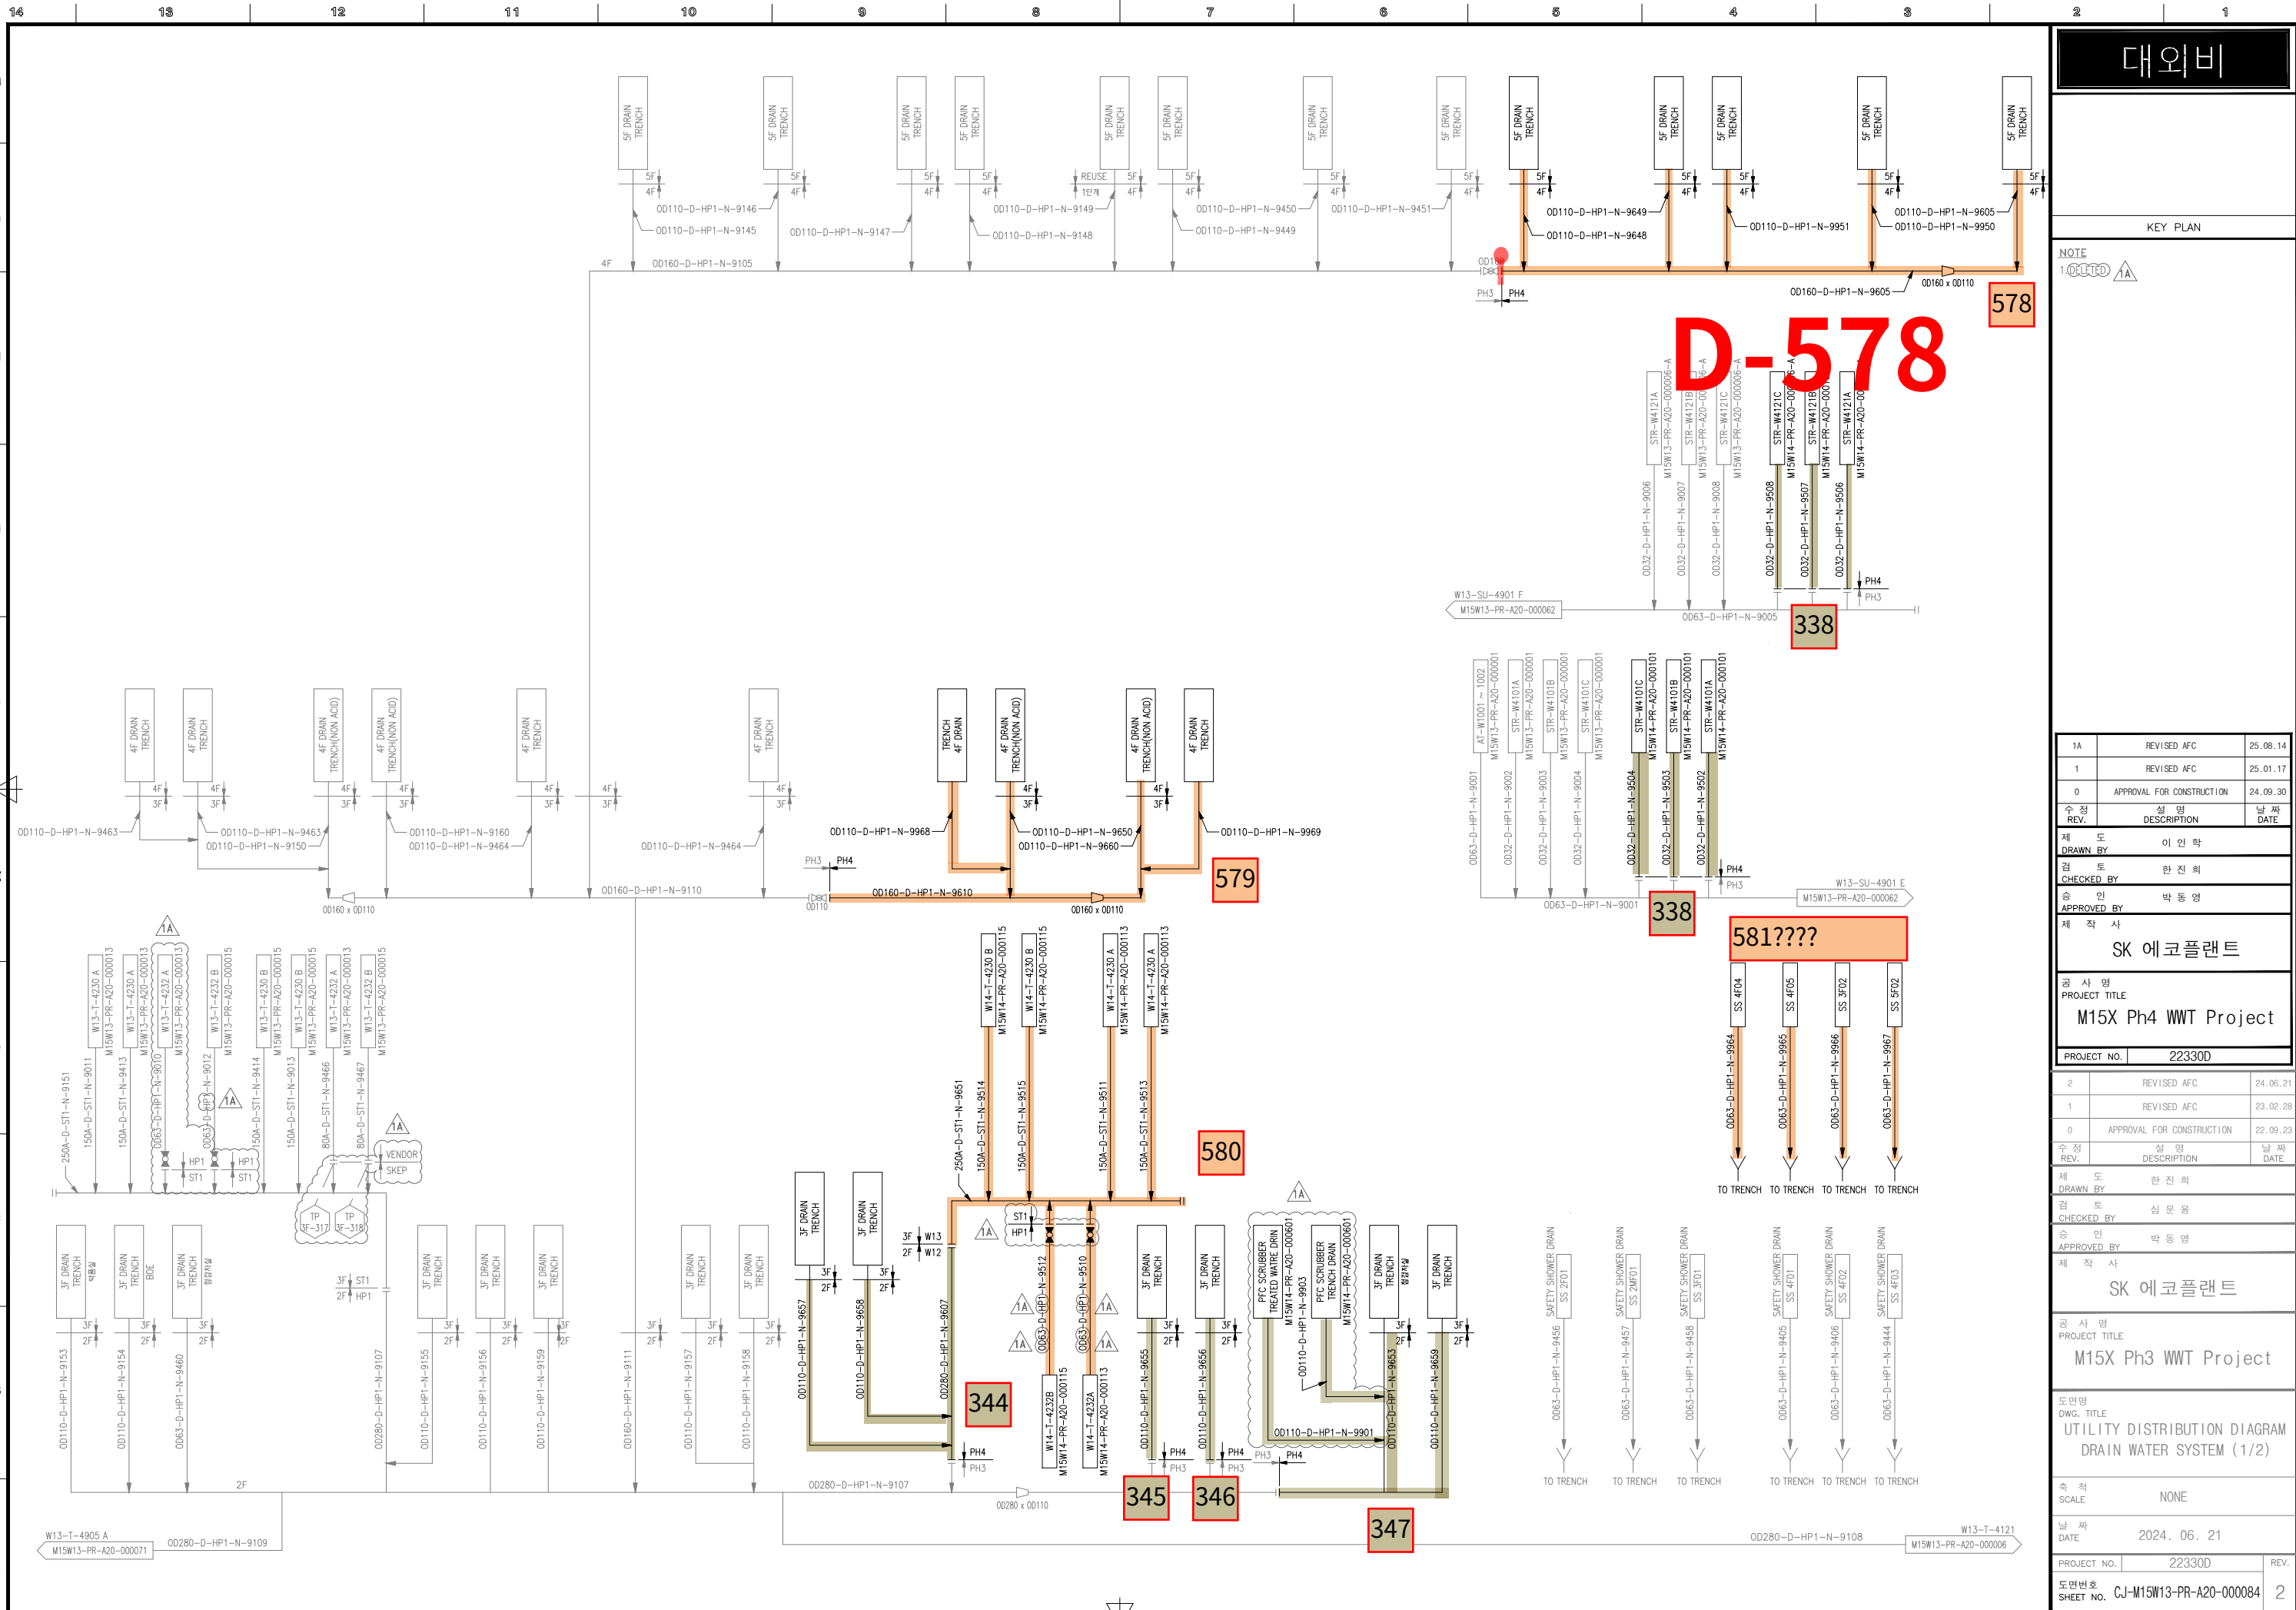


1A	REVISED AFC	25.08.14
1	REVISED AFC	25.01.17
0	APPROVAL FOR CONSTRUCTION	24.09.30
수정 REV.	설명 DESCRIPTION	날짜 DATE
제도 DRAWN BY	이인학	
검토 CHECKED BY	한진희	
승인 APPROVED BY	박동영	
제작사	SK 에코플랜트	
공사명 PROJECT TITLE	M15X Ph4 WWT Project	
PROJECT NO.	22330D	
2	REVISED AFC	24.06.21
1	REVISED AFC	23.02.28
0	APPROVAL FOR CONSTRUCTION	22.09.23
수정 REV.	설명 DESCRIPTION	날짜 DATE
제도 DRAWN BY	한진희	
검토 CHECKED BY	심우영	
승인 APPROVED BY	박동영	
제작사	SK 에코플랜트	
공사명 PROJECT TITLE	M15X Ph3 WWT Project	
도면명 DWG. TITLE	UTILITY DISTRIBUTION DIAGRAM DRAIN WATER SYSTEM (1/2)	
속척 SCALE	NONE	
날짜 DATE	2024. 06. 21	
PROJECT NO.	22330D	REV.
도면번호 SHEET NO.	CJ-M15W13-PR-A20-000084	2

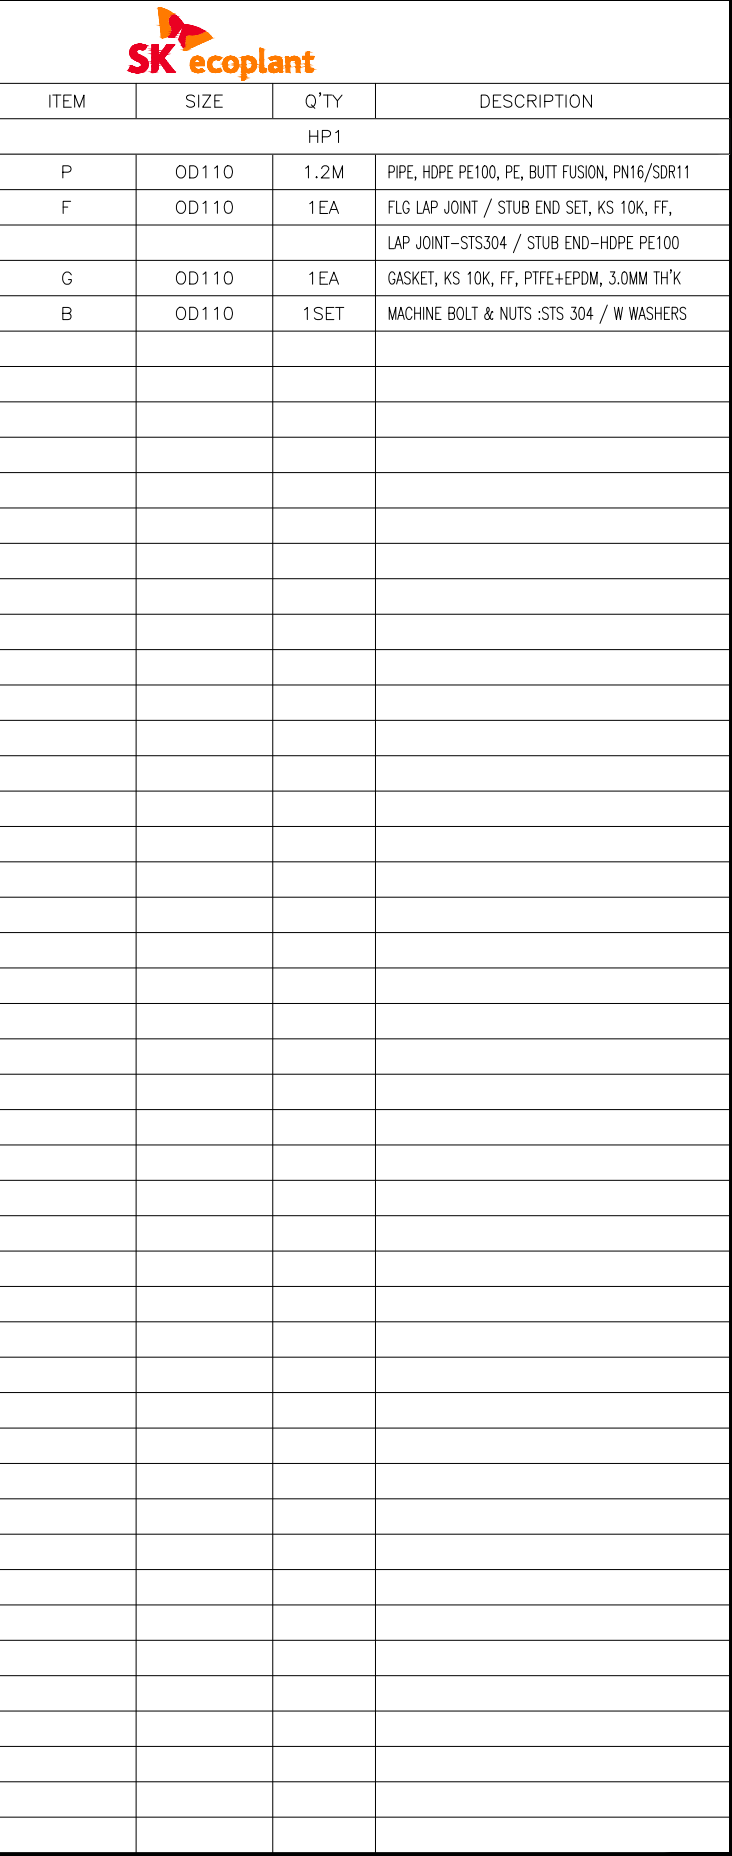

CLIENT  1

당고 : 해당 도면은 SK HYNIX의 기밀비밀 자료로서, 어떠한 경우에도 목적 외 사용, 복제, 제3자에게 공개, 누설 및 유출할 수 없으며, 회사나 유보자의 불법 사용으로 피해가 발생할 경우 유보자에게 민/형사상 책임을 요구할 수 있음

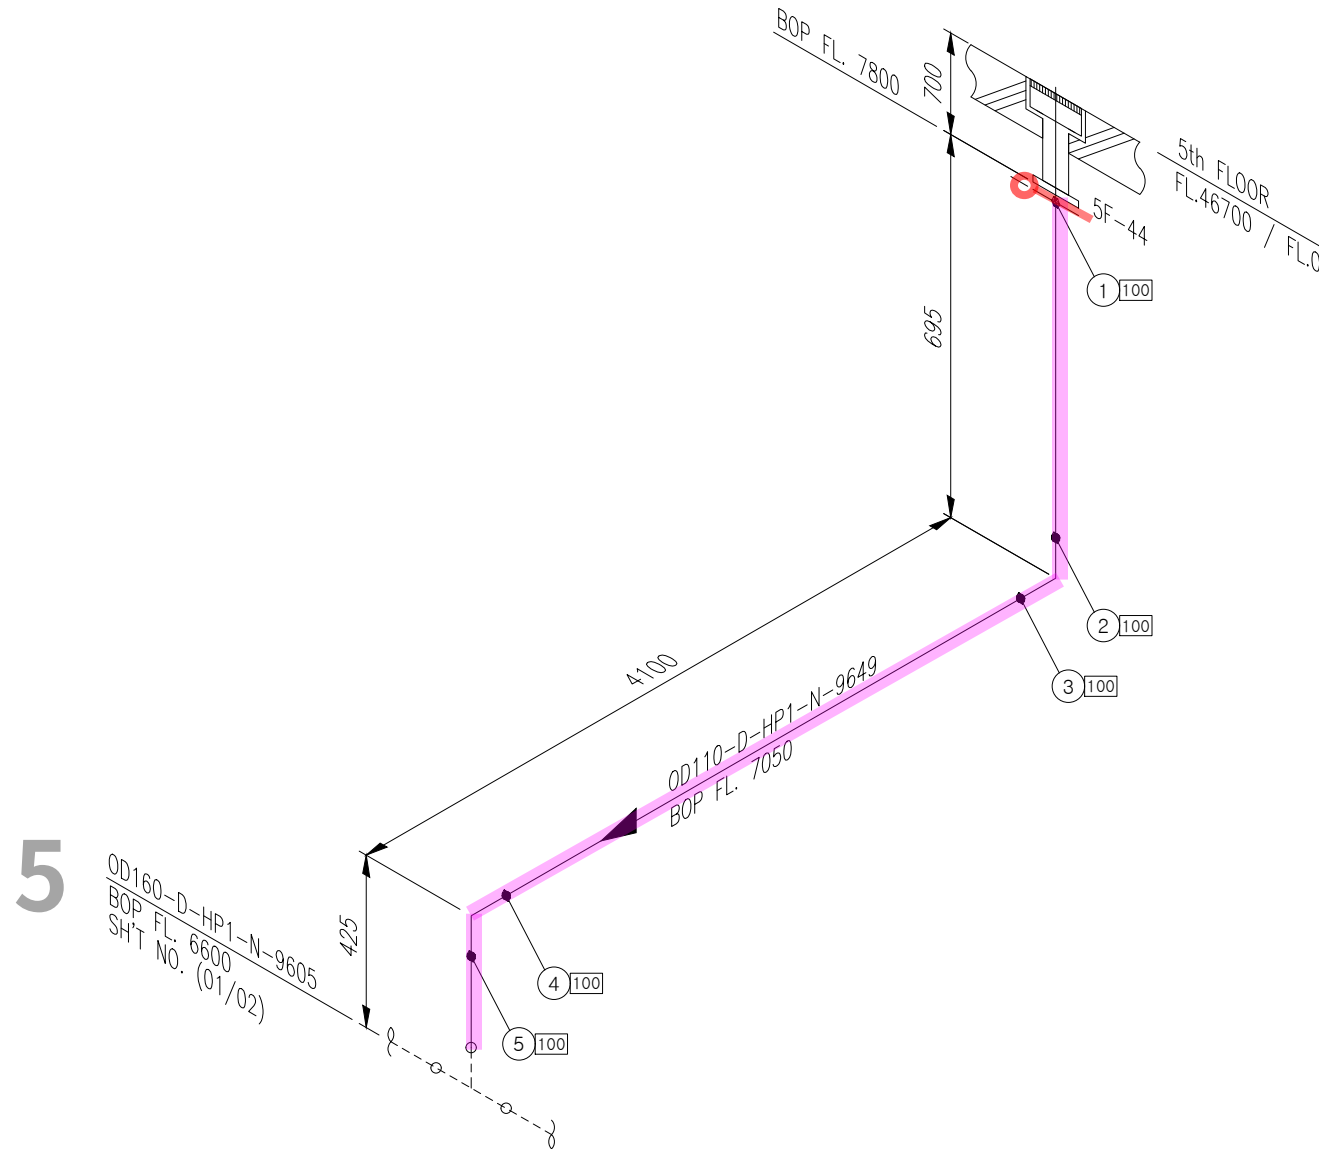[illegible]


<NOTE>

1. (*) FIELD ADJUST

* PIPE : P/P1	* 90° ELBOW : E90	* 45° ELBOW : E45	* TEE : T	* RED.TEE : TR	* STUB-IN : STU	* REINFORCING PAD : RP	* CON.RED : RC	* ECC.RED : RE	* CON.SWAGE : RCS/RCS1	* ECC.SWAGE : RES/RES1	* NIPPLE : NP/NP1/NP2	* CAP : CAP/CAP1	* PLUG : PLG	* FULL COUPLING : FC	* HALF COUPLING : HF/HF1
* STUB-IN : STU	* SOCKET(HDPE/PVC) : SC	* SADDLE(HDPE) : SD	* FLANGE : F/F1	* GASKET : G/G1/G2	* BOLT & NUT : B/B1	* BLIND FLANGE : FB/FB1	* GATE VA. : VG/VG1/VG2	* BALL VA. : VB/VBLO/VB1/VB1LO/VB2/VB2LO	* BUTTERFLY VA. : VF/VF4	* CHECK VA. : VC/VC1/VC2/VC3/VC4/VC5/VC6/VC7					
* GLOBE VA. : VL/VL1/VL2	* DIAPHRAGM VA. : VD/VDLO	* DAMPER : VP	* QUICK COUPLING : SQC	* FLEXIBLE JOINT(STEEL) : FLXB	* FLEXIBLE JOINT(RUBBER) : FLXR	* FLEXIBLE JOINT(STEEL PTFE LINED) : FLXL	* FLEXIBLE HOSE : FLXH	* STEAM TRAP : ST	* SPRAY NOZZLE : SPN	* EMERGENCY SHOWER : SSH					
* STRAINER(Y-TYPE) : YSTR	* STRAINER(T-TYPE) : TSTR	* STRAINER(BUCKET-TYPE) : BSTR	* ANCHOR PLATE : STOP	* BIRD SCREEN : BS	* ISOLATION KIT : IK	* UNLOADING BOX : UB	* AIR TRAP : AT	* LOTO : LOTO	* SIGHT GLASS : SG	* PRESSURE GAUGE : PG	* SHILED : SH	* SPECIAL BOLT & NUT : BL/BL1			

INSULATION	CODE	N	CONDITION	PRESS. (kg/cm2g)	TEMP. (°C)	AREA	W14								CONTRACTOR		PROJECT NAME	
	THICK.	—	DESIGN	1	60	UNIT	4FA								M15X Ph4 Project			
			OPERATING	ATM	AMB	REF. PLAN DWG. CJ-M15W14-PI-A30-040005-C								COMMODITY D	JOB NO.			
						REF. P & ID CJ-M15W13-PR-A20-000084		25.01.24	APPROVED FOR CONSTRUCTION	황래중	안남후	박동영	LINE NO. 0D110-D-HP1-N-9649		SH'T NO. 01 / 01		REV. 0	
							REV. NO.	DATE	DESCRIPTION	BY	CHK	APP'D						

경고 : 본 도면은 SK HYNIX의 기밀비밀 자료로서, 어떠한 경우에도 목적 외 사용, 복제, 제3자에게 공개, 누설 및 유출할 수 없으며, 회사는 유포자의 불법 사용으로 피해가 발생할 경우 유포자에게 민/형사상 책임을 요구할 수 있음

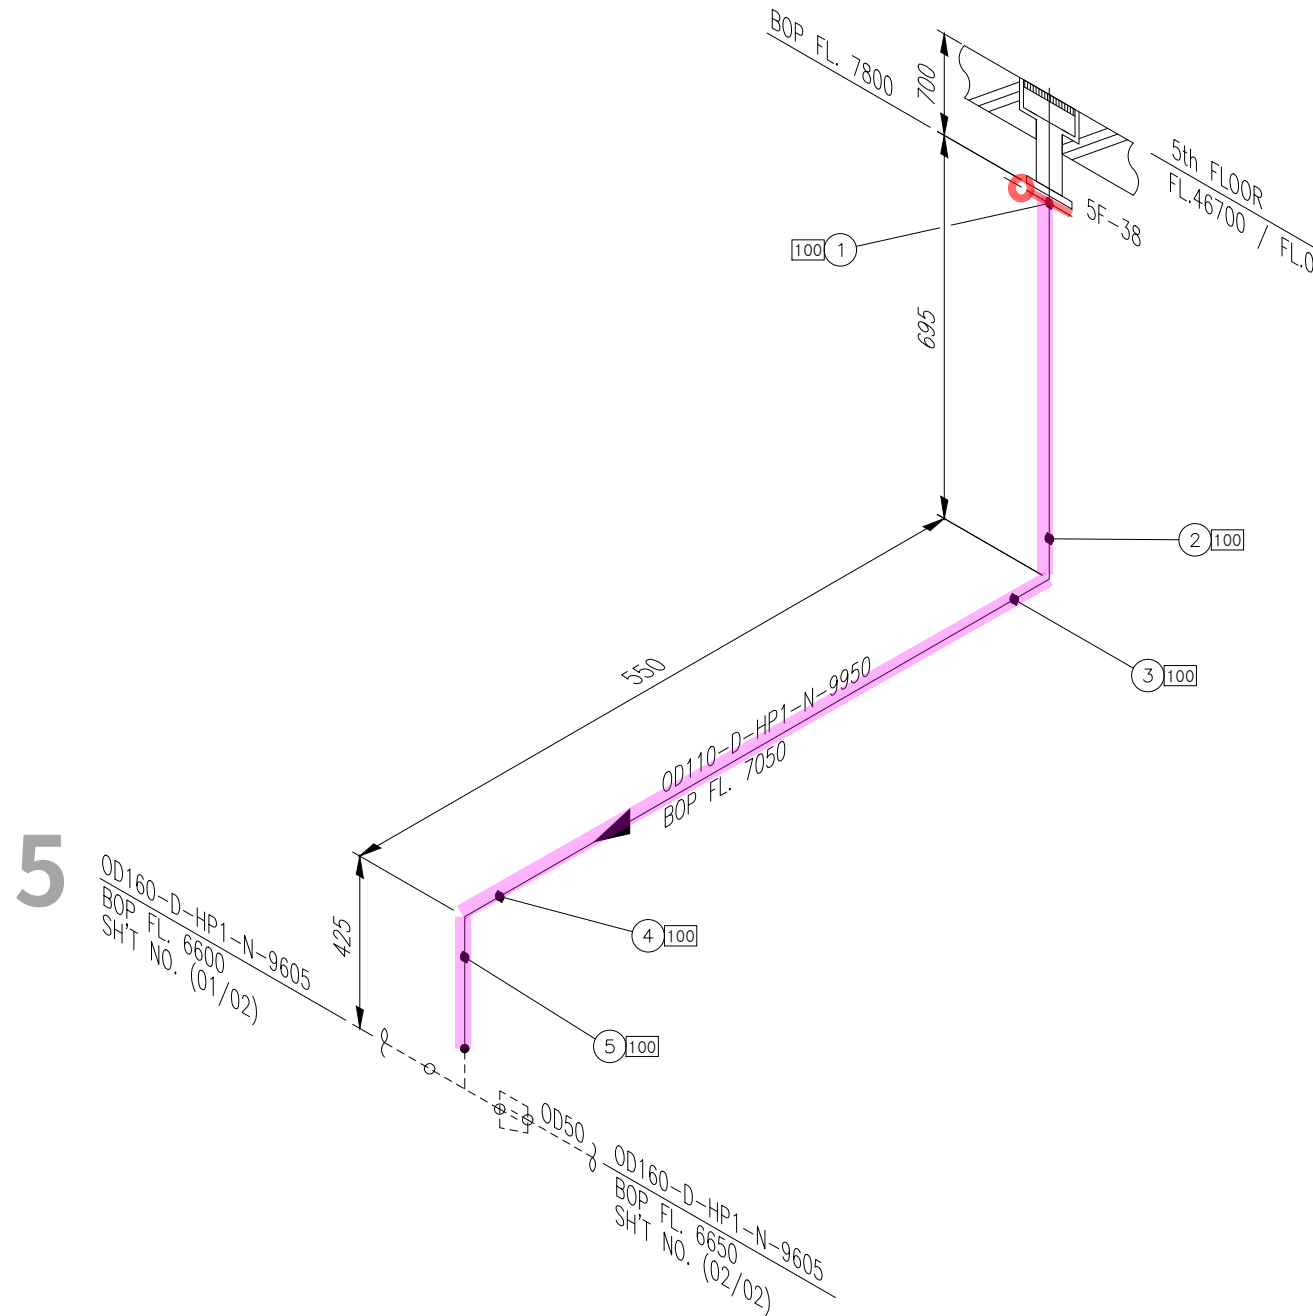[illegible]

<NOTE>

1. (*) FIELD ADJUST

* PIPE : P/P1	* 90° ELBOW : E90	* 45° ELBOW : E45	* TEE : T	* RED.TEE : TR	* STUB-IN : STU	* REINFORCING PAD : RP	* CON.RED : RC	* ECC.RED : RE	* CON.SWAGE : RCS/RCS1	* ECC.SWAGE : RES/RES1	* NIPPLE : NP/NP1/NP2	* CAP : CAP/CAP1	* PLUG : PLG	* FULL COUPLING : FC	* HALF COUPLING : HF/HF1
* STUB-IN : STU	* SOCKET(HDPE/PVC) : SC	* SADDLE(HDPE) : SD	* FLANGE : F/F1	* GASKET : G/G1/G2	* BOLT & NUT : B/B1	* BLIND FLANGE : FB/FB1	* GATE VA. : VG/VG1/VG2	* BALL VA. : VB/VBLO/VB1/VB1LO/VB2/VB2LO	* BUTTERFLY VA. : VF/VF4	* CHECK VA. : VC/VC1/VC2/VC3/VC4/VC5/VC6/VC7					
* GLOBE VA. : VL/VL1/VL2	* DIAPHRAGM VA. : VD/VDLO	* DAMPER : VP	* QUICK COUPLING : SQC	* FLEXIBLE JOINT(STEEL) : FLXB	* FLEXIBLE JOINT(RUBBER) : FLXR	* FLEXIBLE JOINT(STEEL PTFE LINED) : FLXL	* FLEXIBLE HOSE : FLXH	* STEAM TRAP : ST	* SPRAY NOZZLE : SPN	* EMERGENCY SHOWER : SSH					
* STRAINER(Y-TYPE) : YSTR	* STRAINER(T-TYPE) : TSTR	* STRAINER(BUCKET-TYPE) : BSTR	* ANCHOR PLATE : STOP	* BIRD SCREEN : BS	* ISOLATION KIT : IK	* UNLOADING BOX : UB	* AIR TRAP : AT	* LOTO : LOTO	* SIGHT GLASS : SG	* PRESSURE GAUGE : PG	* SHILED : SH	* SPECIAL BOLT & NUT : BL/BL1			

CLIENT



3

INSULATION	CODE	N	CONDITION	PRESS. (kg/cm ² g)	TEMP. (°C)	AREA	W14							CONTRACTOR	PROJECT NAME	
	THICK.	—	DESIGN	1	60	UNIT	4FA								M15X Ph4 Project	
			OPERATING	ATM	AMB	REF. PLAN DWG.								COMMODITY	JOB NO.	
						CJ-M15W14-PI-A30-040005-C								D	22330D	
						REF. P & ID			25.01.24	APPROVED FOR CONSTRUCTION	황래중	안남후	박동영	LINE NO.	SH'T NO.	REV.
						CJ-M15W13-PR-A20-000084		REV. NO.	DATE	DESCRIPTION	BY	CHK	APP'D	0D110-D-HP1-N-9950	01 / 01	0

경고 : 본 도면은 SK HYNIX의 기밀비밀 자료로서, 어떠한 경우에도 목적 외 사용, 복제, 제3자에게 공개, 누설 및 유출할 수 없으며, 회사는 유포자의 불법 사용으로 피해가 발생할 경우 유포자에게 민/형사상 책임을 요구할 수 있음

