


DRAWING LIST FOR TEST PACKAGE

D-579


PROJECT NO.: 22328D**PROJECT TITLE : M15X Ph2 Project**[illegible]

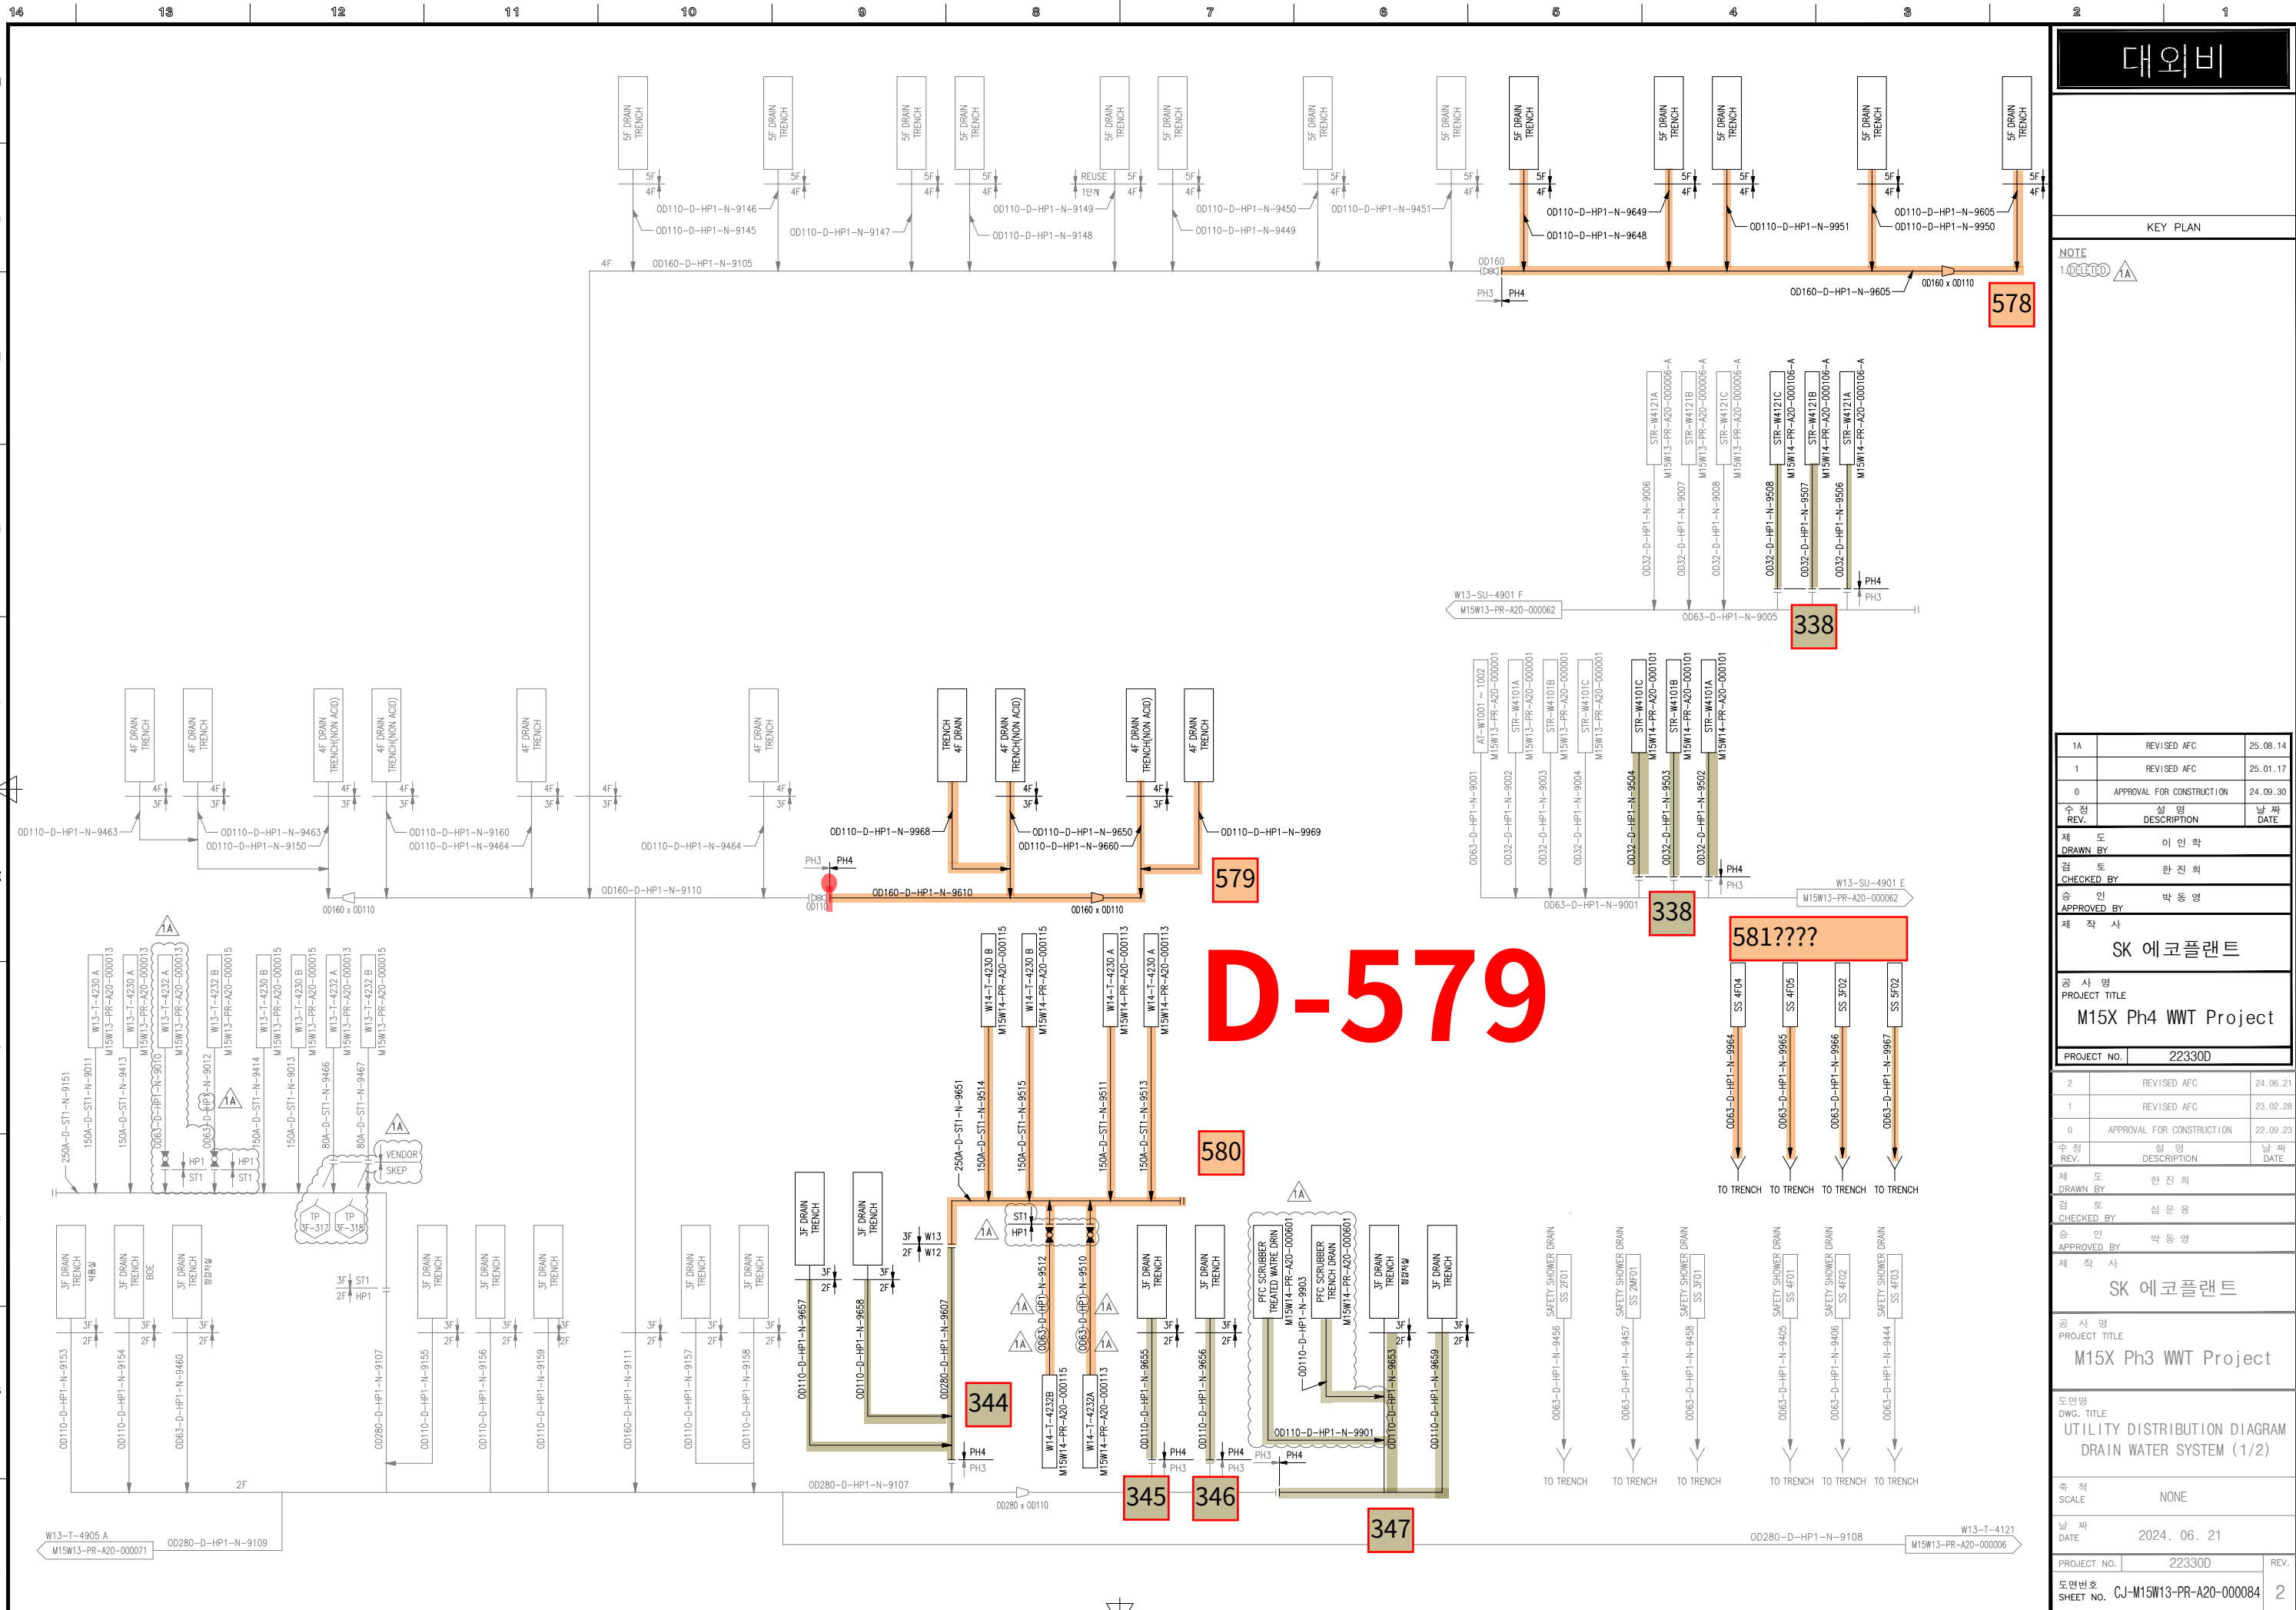

대외비		
KEY PLAN		
NOTE 1. (1/2) (1A)		
1A	REVISED AFC	25.08.14
1	REVISED AFC	25.01.17
0	APPROVAL FOR CONSTRUCTION	24.09.30
수정 REV.	설명 DESCRIPTION	날짜 DATE
제 도 이 인 학		
검 토 한 진 회		
승 인 박 동 영		
제 작 사 SK 에코플랜트		
공 사 명 PROJECT TITLE M15X Ph4 WWT Project		
PROJECT NO. 22330D		
2	REVISED AFC	24.06.21
1	REVISED AFC	23.02.28
0	APPROVAL FOR CONSTRUCTION	22.09.23
수정 REV.	설명 DESCRIPTION	날짜 DATE
제 도 한 진 회		
검 토 심 문 영		
승 인 박 동 영		
제 작 사 SK 에코플랜트		
공 사 명 PROJECT TITLE M15X Ph3 WWT Project		
도면명 DWG. TITLE UTILITY DISTRIBUTION DIAGRAM DRAIN WATER SYSTEM (1/2)		
속 척 SCALE NONE		
날 짜 DATE	2024. 06. 21	
PROJECT NO. 22330D	REV. 2	
도면번호 SHEET NO. CJ-M15W13-PR-A20-000084		





ITEM	SIZE	Q'TY	DESCRIPTION
HP1			
P	OD110	12.9M	PIPE, HDPE PE100, PE, BUTT FUSION, PN16/SDR11
E90	OD110	2EA	ELBOW 90 DEG, HDPE PE100, PE, BUTT FUSION,
			PN16/SDR11
T	OD110	1EA	TEE EQUAL, HDPE PE100, PE, BUTT FUSION, PN16/SDR11
F	OD110	1EA	FLG LAP JOINT / STUB END SET, KS 10K, FF,
			LAP JOINT--STS304 / STUB END--HDPE PE100
G	OD110	1EA	GASKET, KS 10K, FF, PTFE+EPDM, 3.0MM TH'K
B	OD110	1SET	MACHINE BOLT & NUTS :STS 304 / W WASHERS
E45	OD110	1EA	ELBOW 45 DEG, HDPE PE100, PE, BUTT FUSION,
			PN16/SDR11

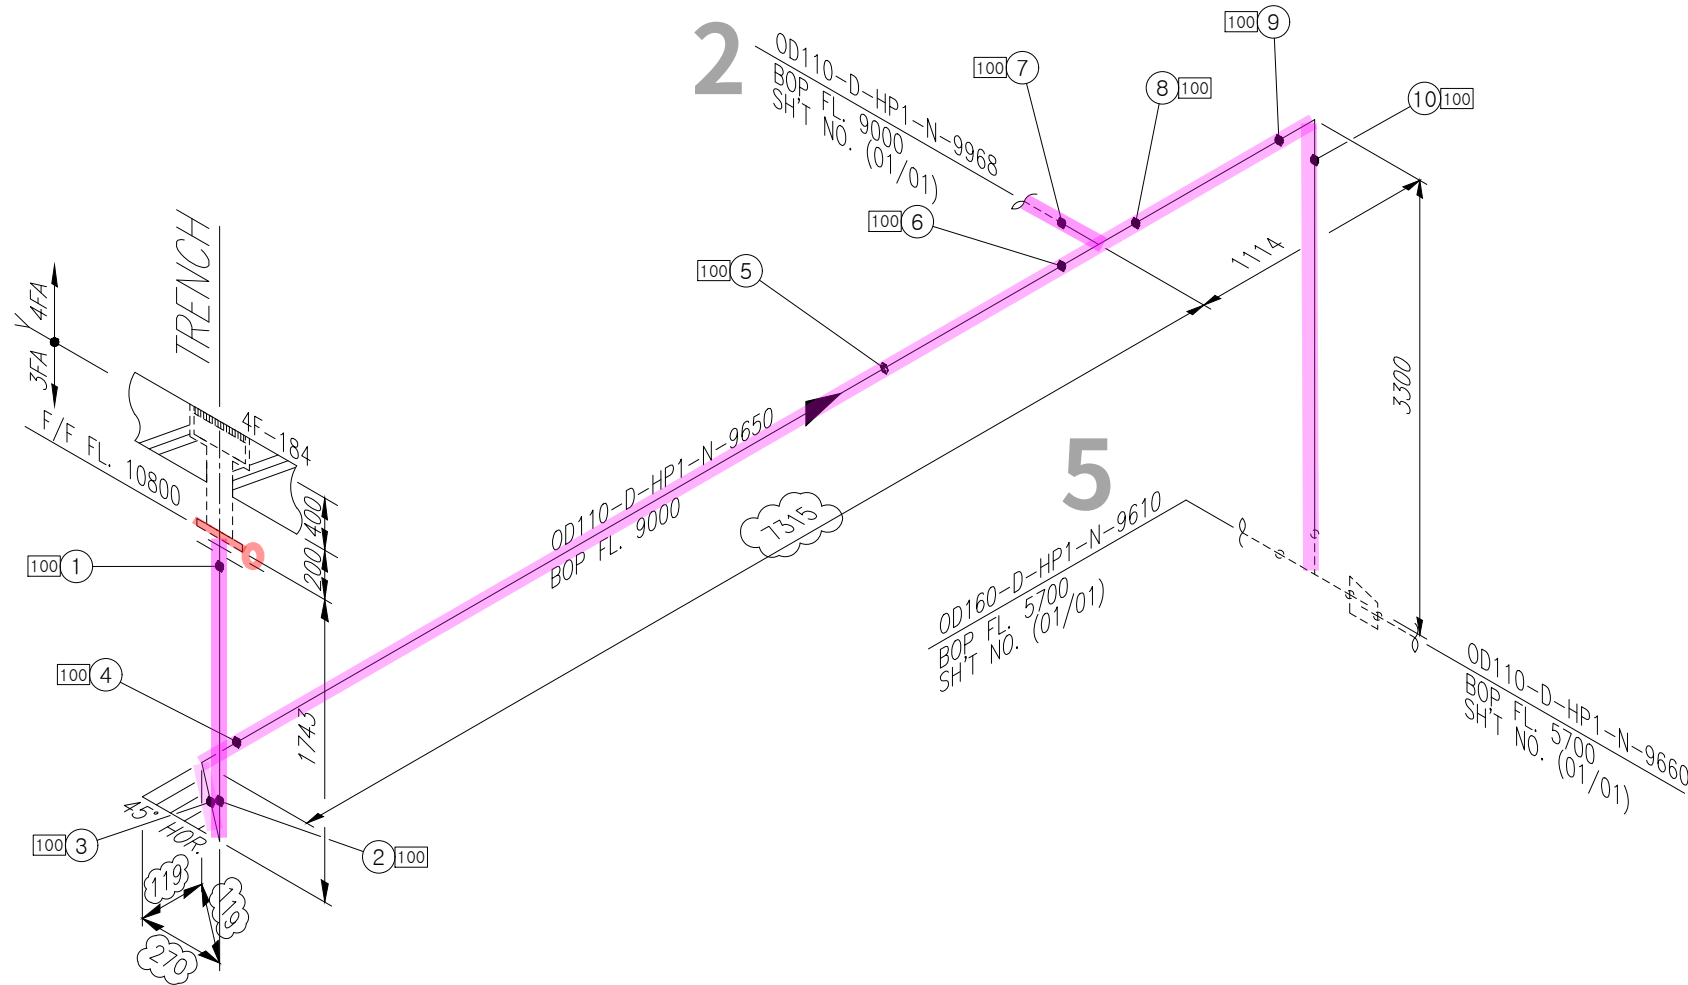

<NOTE>
1. TRAY & ANGLE, CHANNEL SUPPORT가 적용되는
배관 ELEVATION은 현장 맞춤으로 한다.
2. (*) FIELD ADJUST

* PIPE : P/P1	* 90° ELBOW : E90	* 45° ELBOW : E45	* TEE : T	* RED.TEE : TR	* STUB-IN : STU	* REINFORCING PAD : RP	* CON.RED : RC	* ECC.RED : RE	* CON.SWAGE : RCS/RCS1	* ECC.SWAGE : RES/RES1	* NIPPLE : NP/NP1/NP2	* CAP : CAP/CAP1	* PLUG : PLG	* FULL COUPLING : FC	* HALF COUPLING : HF/HF1
* STUB-IN : STU	* SOCKET(HDPE/PVC) : SC	* SADDLE(HDPE) : SD	* FLANGE : F/F1	* GASKET : G/G1/G2	* BOLT & NUT : B/B1	* BLIND FLANGE : FB/FB1	* GATE VA. : VG/VG1/VG2	* BALL VA. : VB/VB1/VB10/VB2/VB210	* BUTTERFLY VA. : VF/VF4	* CHECK VA. : VC/VC1/VC2/VC3/VC4/VC5/VC6/VC7					
* GLOBE VA. : VL/VL1/VL2	* DIAPHRAGM VA. : VD/VD10	* DAMPER : VP	* QUICK COUPLING : SQC	* FLEXIBLE JOINT(STEEL) : FLXB	* FLEXIBLE JOINT(RUBBER) : FLXR	* FLEXIBLE JOINT(STEEL PTFE LINED) : FLXL	* FLEXIBLE HOSE : FLXH	* STEAM TRAP : ST	* SPRAY NOZZLE : SPN	* EMERGENCY SHOWER : SSH					
* STRAINER(Y-TYPE) : YSTR	* STRAINER(T-TYPE) : TSTR	* STRAINER(BUCKET-TYPE) : BSTR	* ANCHOR PLATE : STOP	* BIRD SCREEN : BS	* ISOLATION KIT : IK	* UNLOADING BOX : UB	* AIR TRAP : AT	* LOTO : LOTO	* SIGHT GLASS : SG	* PRESSURE GAUGE : PG	* SHILED : SH	* SPECIAL BOLT & NUT : BL/BL1			

CLIENT		1	
			
CONTRACTOR		PROJECT NAME	
		M15X Ph4 Project	
영	COMMODITY	JOB NO.	
	D	22330D	
영	LINE NO.	SH'T NO.	REV.
D	OD110-D-HP1-N-9650	01 / 01	1

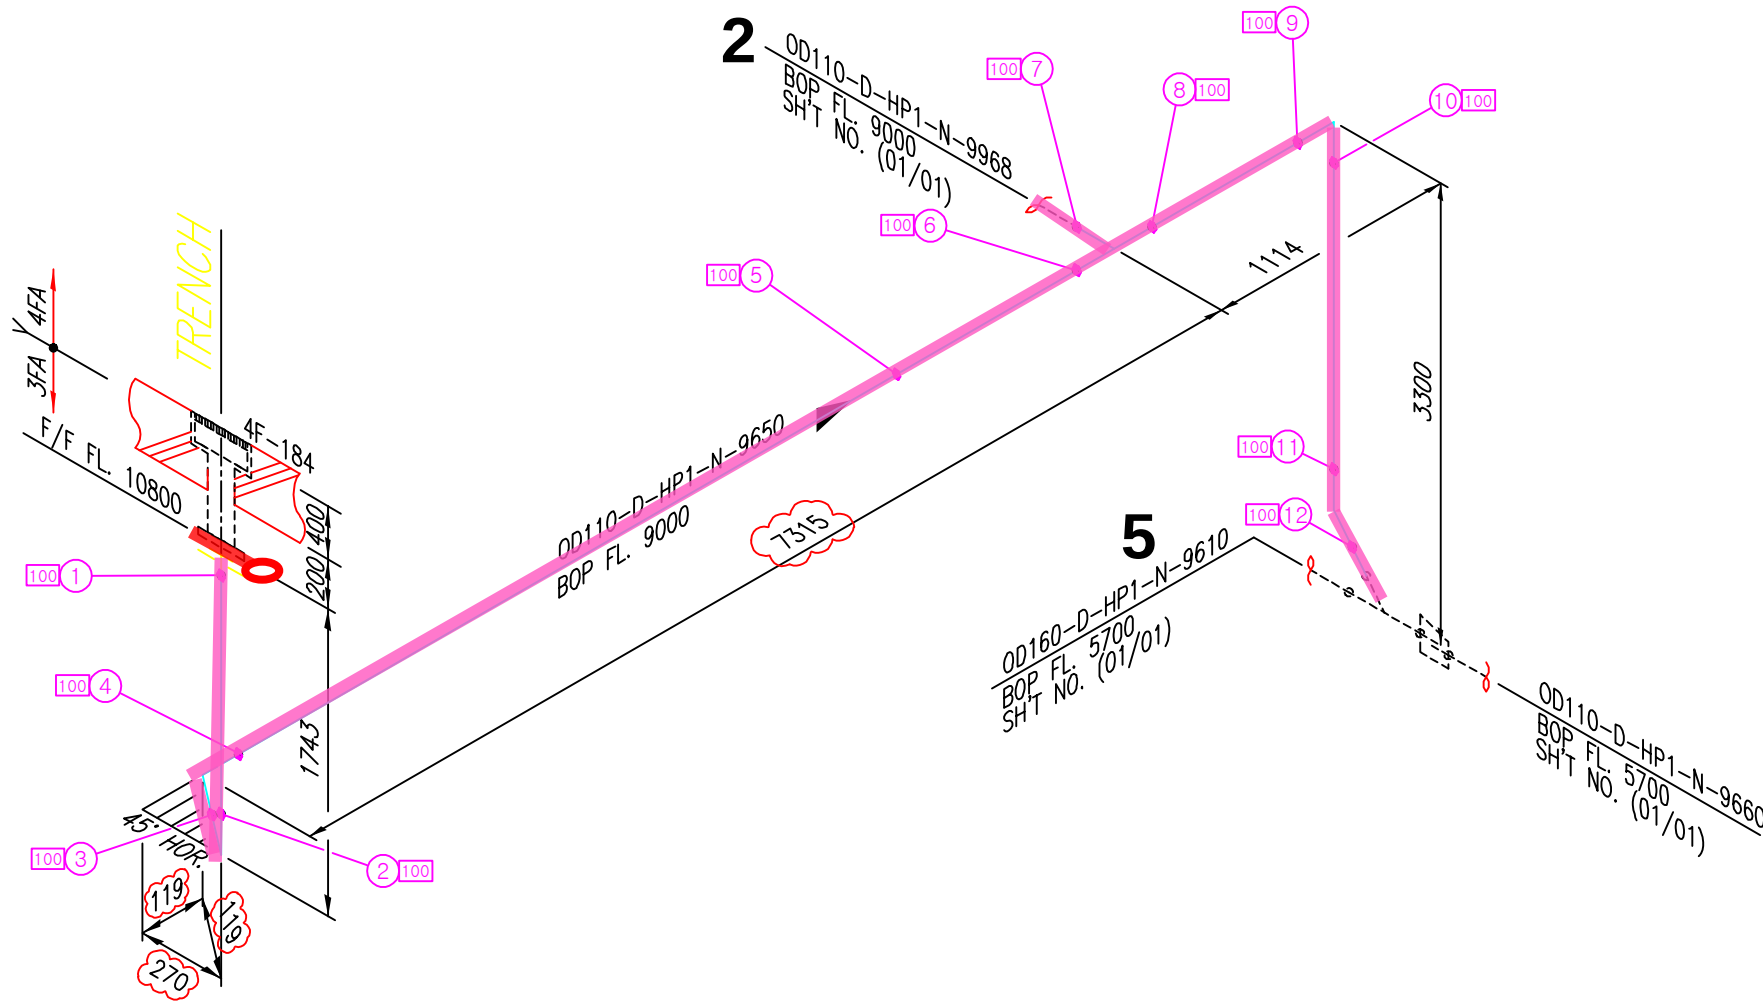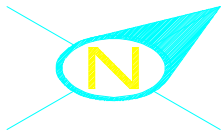

<NOTE>
1. TRAY & ANGLE,CHANNEL SUPPORT가 적용되는 배관 ELEVATION은 현장 맞춤으로 한다.
2. (*) FIELD ADJUST

* PIPE : P/P1 * 90° ELBOW : E90 * 45° ELBOW : E45 * TEE : T * RED.TEE : TR * STUB-IN : STU * REINFORCING PAD : RP * CON.RED : RC * ECC.RED : RE * CON.SWAGE : RCS/RCS1 * ECC.SWAGE : RES/RES1 * NIPPLE : NP/NP1/NP2 * CAP : CAP/CAP1 * PLUG : PLG * FULL COUPLING : FC * HALF COUPLING : HF/HF1
* STUB-IN : STU * SOCKET(HDPE/PVC) : SC * SADDLE(HDPE) : SD * FLANGE : F/F1 * GASKET : G/G1/G2 * BOLT & NUT : B/B1 * BLIND FLANGE : FB/FB1 * GATE VA. : VG/VG1/VG2 * BALL VA. : VB/VBLO/VB1/VB1LO/VB2/VB2LO * BUTTERFLY VA. : VF/VF4 * CHECK VA. : VC/VC1/VC2/VC3/VC4/VC5/VC6/VC7
* GLOBE VA. : VL/VL1/VL2 * DIAPHRAGM VA. : VD/VDLO * DAMPER : VP * QUICK COUPLING : SQC * FLEXIBLE JOINT(STEEL) : FLXB * FLEXIBLE JOINT(RUBBER) : FLXR * FLEXIBLE JOINT(STEEL PTFE LINED) : FLXL * FLEXIBLE HOSE : FLXH * STEAM TRAP : ST * SPRAY NOZZLE : SPN * EMERGENCY SHOWER : SSH
* STRAINER(Y-TYPE) : YSTR * STRAINER(T-TYPE) : TSTR * STRAINER(BUCKET-TYPE) : BSTR * ANCHOR PLATE : STOP * BIRD SCREEN : BS * ISOLATION KIT : IK * UNLOADING BOX : UB * AIR TRAP : AT * LOTO : LOTO * SIGHT GLASS : SG * PRESSURE GAUGE : PG * SHLED : SH * SPECIAL BOLT & NUT : BL/BL1


INSULATION	CODE	N	CONDITION	PRESS. (kg/cm2g)	TEMP. (°C)	AREA	W14								
	THICK.	-	DESIGN	1	60	UNIT	3FA								
			OPERATING	ATM	AMB	REF. PLAN DWG.	CJ-M15W14-PI-A30-030007-D	1	25.03.31	REVISED AS MARKED	황래중	안남후	박동영		
						REF. P. & ID	CJ-M15W13-PR-A20-000084	2	25.01.24	APPROVED FOR CONSTRUCTION	황래중	안남후	박동영		
								REV. NO.	DATE	DESCRIPTION	BY	CHK	APP'D		



ITEM	SIZE	Q'TY	DESCRIPTION
HP1			
P	OD110	12.9M	PIPE, HDPE PE100, PE, BUTT FUSION, PN16/SDR11
E90	OD110	2EA	ELBOW 90 DEG, HDPE PE100, PE, BUTT FUSION, PN16/SDR11
E45	OD110	1EA	ELBOW 45 DEG, HDPE PE100, PE, BUTT FUSION, PN16/SDR11
T	OD110	1EA	TEE EQUAL, HDPE PE100, PE, BUTT FUSION, PN16/SDR11
F	OD110	1EA	FLG LAP JOINT / STUB END SET, KS 10K, FF, LAP JOINT-ST304 / STUB END-HDPE PE100
G	OD110	1EA	GASKET, KS 10K, FF, PTFE+EPDM, 3.0MM TH'K
B	OD110	1SET	MACHINE BOLT & NUTS :STS 304 / W WASHERS

E45	OD110	1EA	ELBOW 45 DEG, HDPE PE100, PE, BUTT FUSION, PN16/SDR11
-----	-------	-----	---

CLIENT	SK hynix	1
CONTRACTOR	SK ecoplant	PROJECT NAME
COMMODITY	D	M15X Ph4 Project
LINE NO.	OD110-D-HP1-N-9650	JOB NO.
		22330D
		SH'T NO.
		01 / 01
		REV.
		1

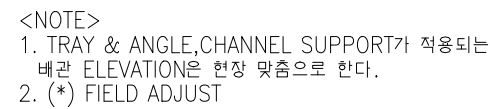


CLIENT



2

INSULATION	CODE	N	CONDITION	PRESS. (kg/cm2g)	TEMP. (°C)	AREA	W14							CONTRACTOR	PROJECT NAME	
	THICK.	-	DESIGN	1	60	UNIT	3FA								M15X Ph4 Project	
			OPERATING	ATM	AMB	REF. PLAN DWG.								COMMODITY	JOB NO.	
						CJ-M15W14-PI-A30-030008-D			25.01.24	APPROVED FOR CONSTRUCTION	황래중	안남후	박동영	D	22330D	
						REF. P & ID		REV.	DATE	DESCRIPTION	BY	CHK	APP'D	LINE NO.	SH'T NO.	REV.
						CJ-M15W13-PR-A20-000084								0D110-D-HP1-N-9668	01 / 01	0

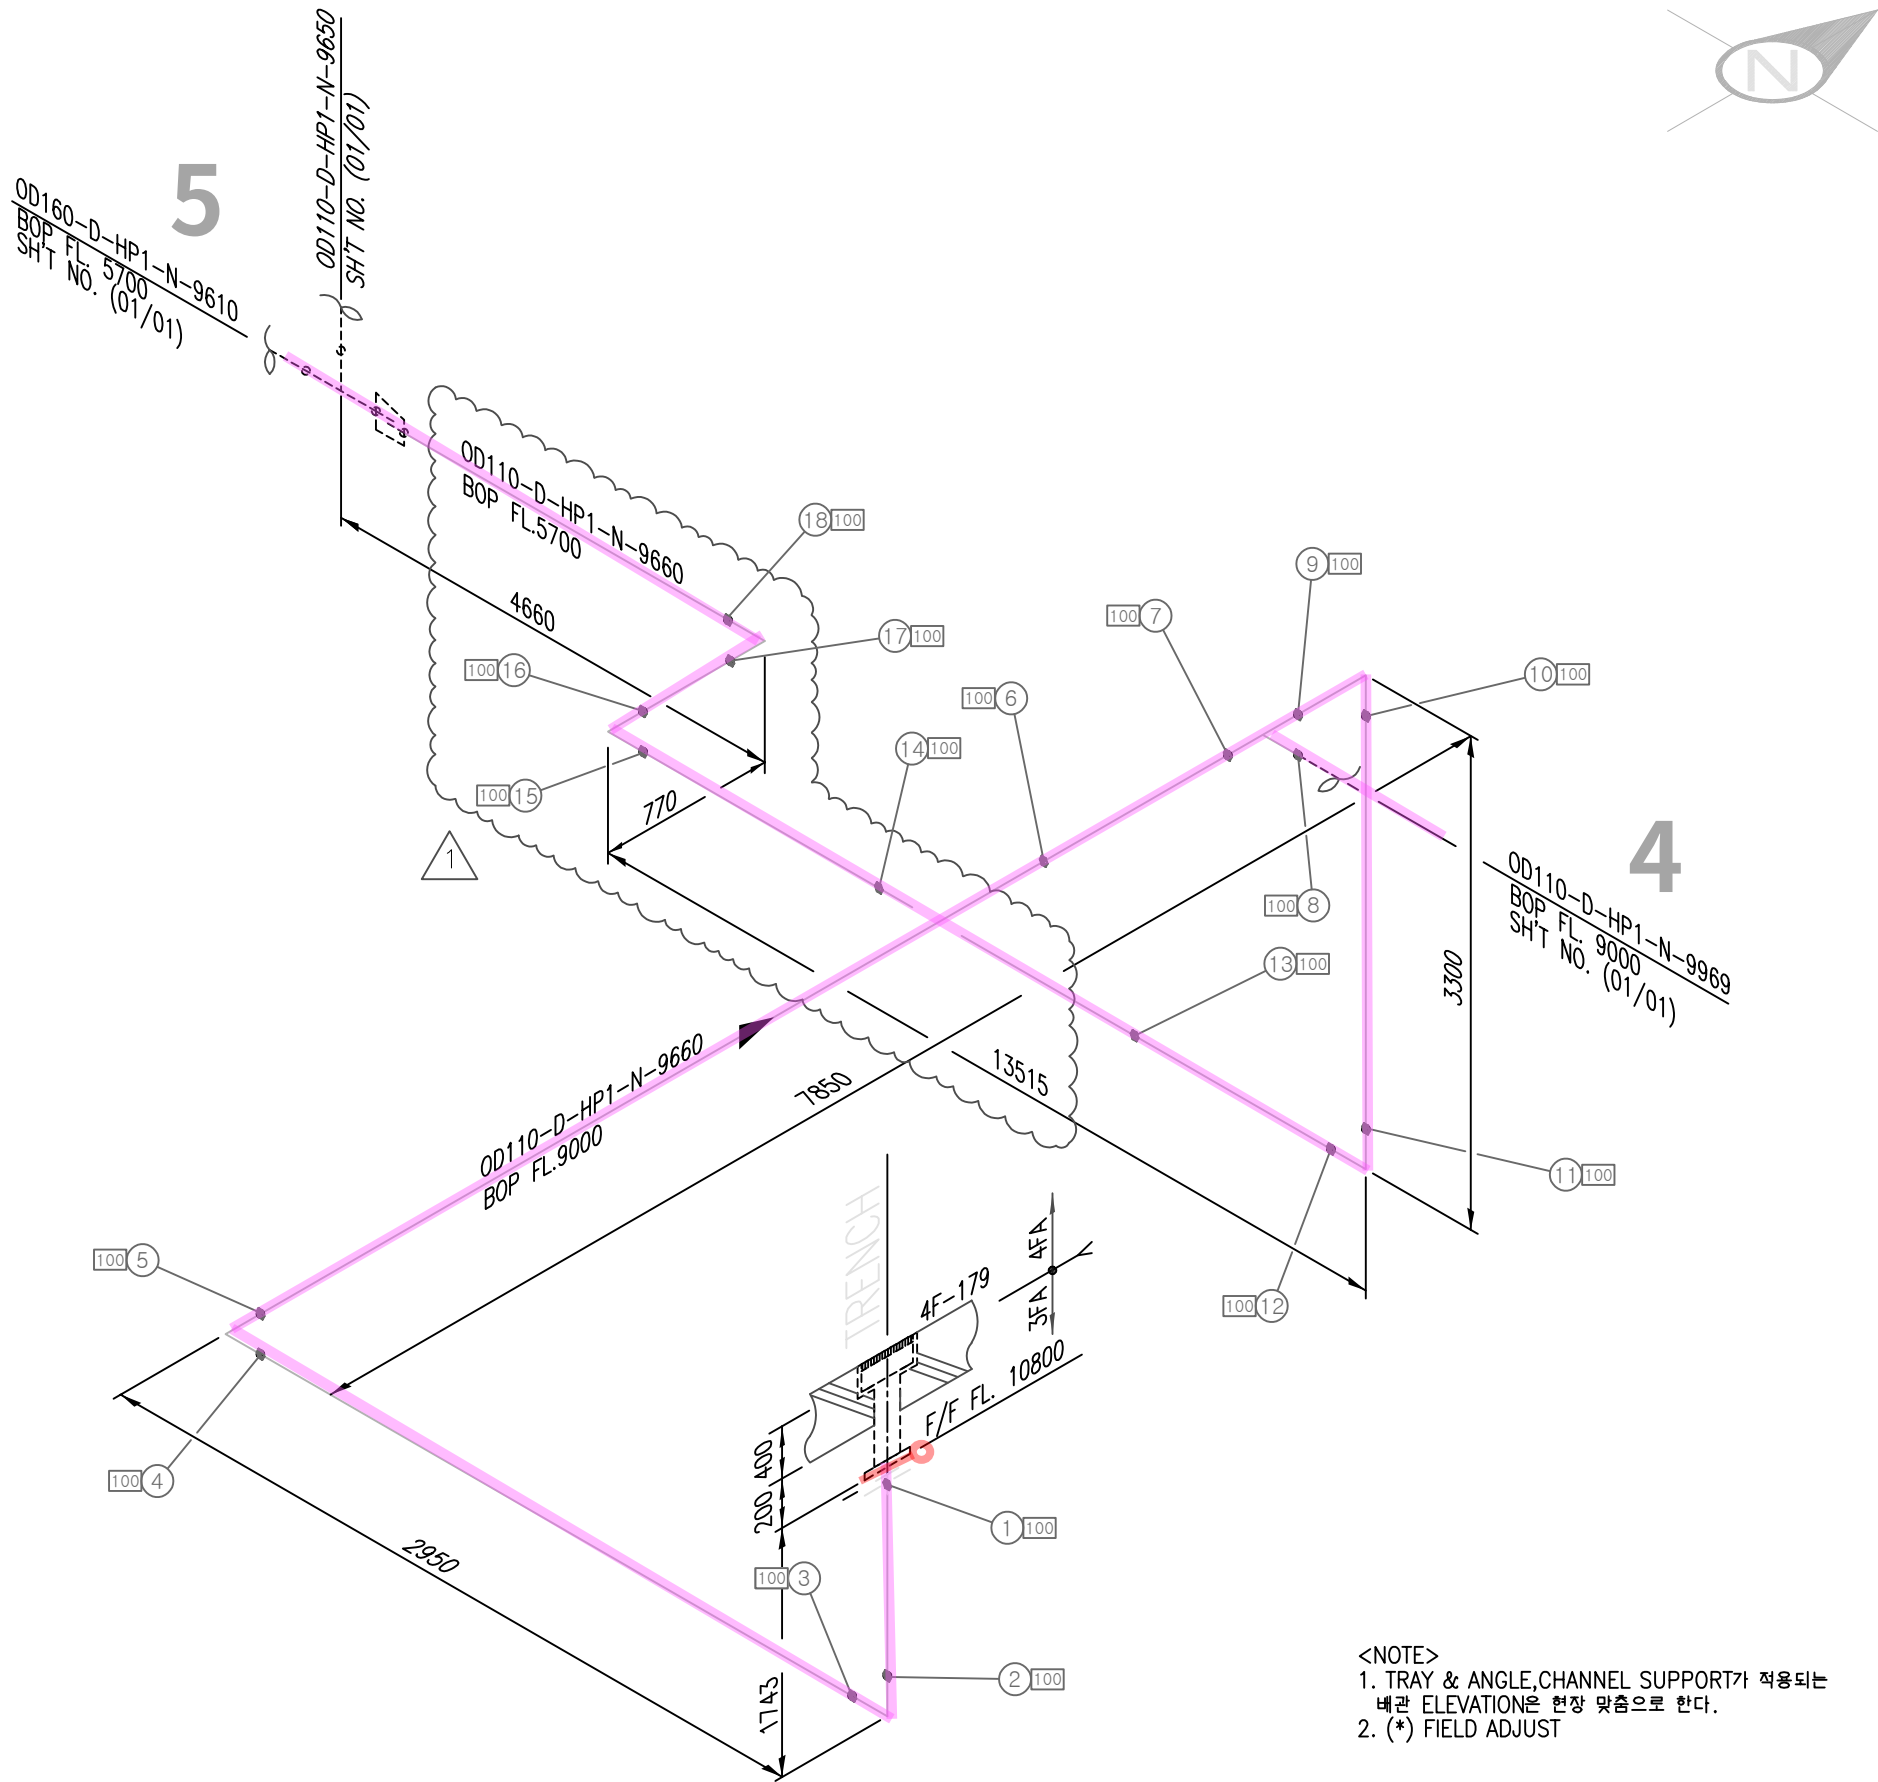

<NOTE>
1. TRAY & ANGLE, CHANNEL SUPPORT가 적용되는
배관 ELEVATION은 현장 맞춤으로 한다.
2. (*) FIELD ADJUST



ITEM	SIZE	Q'TY	DESCRIPTION
HP1			
P	OD110	34.1M	PIPE, HDPE PE100, PE, BUTT FUSION, PN16/SDR11
E90	OD110	6EA	ELBOW 90 DEG, HDPE PE100, PE, BUTT FUSION, PN16/SDR11
T	OD110	1EA	TEE EQUAL, HDPE PE100, PE, BUTT FUSION, PN16/SDR11
F	OD110	1EA	FLG LAP JOINT / STUB END SET, KS 10K, FF, LAP JOINT-ST304 / STUB END-HDPE PE100
G	OD110	1EA	GASKET, KS 10K, FF, PTFE+EPDM, 3.0MM TH'K
B	OD110	1SET	MACHINE BOLT & NUTS :STS 304 / W WASHERS

CLIENT



3

CONTRACTOR



COMMODITY

D


LINE NO.

OD110-D-HP1-N-9660

PROJECT NAME		M15X Ph4 Project
JOB NO.		22330D
SH'T NO.	REV.	
01 / 01	1	

* PIPE : P/P1 * 90° ELBOW : E90 * 45° ELBOW : E45 * TEE : T * RED.TEE : TR * STUB-IN : STU * REINFORCING PAD : RP * CON.RED : RC * ECC.RED : RE * CON.SWAGE : RCS/RCS1 * ECC.SWAGE : RES/RES1 * NIPPLE : NP/NP1/NP2 * CAP : CAP/CAP1 * PLUG : PLG * FULL COUPLING : FC * HALF COUPLING : HF/HF1
* STUB-IN : STU * SOCKET(HDPE/PVC) : SC * SADDLE(HDPE) : SD * FLANGE : F/F1 * GASKET : G/G1/G2 * BOLT & NUT : B/B1 * BLIND FLANGE : FB/FB1 * GATE VA. : VG/VG1/VG2 * BALL VA. : VB/VB1/VB2/VB3/VB4/VB5/VB6/VB7
* GLOBE VA. : VL/VL1/VL2 * DIAPHRAGM VA. : VD/VD1/VD2 * DAMPER : VP * QUICK COUPLING : SQC * FLEXIBLE JOINT(STEEL) : FLX * FLEXIBLE JOINT(RUBBER) : FLXR * FLEXIBLE JOINT(STEEL PTFE LINED) : FLXL * FLEXIBLE HOSE : FLXH * STEAM TRAP : ST * SPRAY NOZZLE : SPN * EMERGENCY SHOWER : SSH
* STRAINER(Y-TYPE) : YSTR * STRAINER(T-TYPE) : TSTR * STRAINER(BUCKET-TYPE) : BSTR * ANCHOR PLATE : STOP * BIRD SCREEN : BS * ISOLATION KIT : IK * UNLOADING BOX : UB * AIR TRAP : AT * LOTO : LOTO * SIGHT GLASS : SG * PRESSURE GAUGE : PG * SHILED : SH * SPECIAL BOLT & NUT : BL/BL1

INSULATION	CODE	N	CONDITION	PRESS. (kg/cm2g)	TEMP. (°C)	AREA	W14	REF. PLAN DWG. CJ-M15W14-PI-A30-030008-D	REF. P. & ID CJ-M15W13-PR-A20-000084	REV. NO.	DATE	DESCRIPTION	BY	CHK	APP'D	CONTRACTOR	PROJECT NAME
	THICK.	-	DESIGN	1	60	UNIT	3FA										
			OPERATING	ATM	AMB												

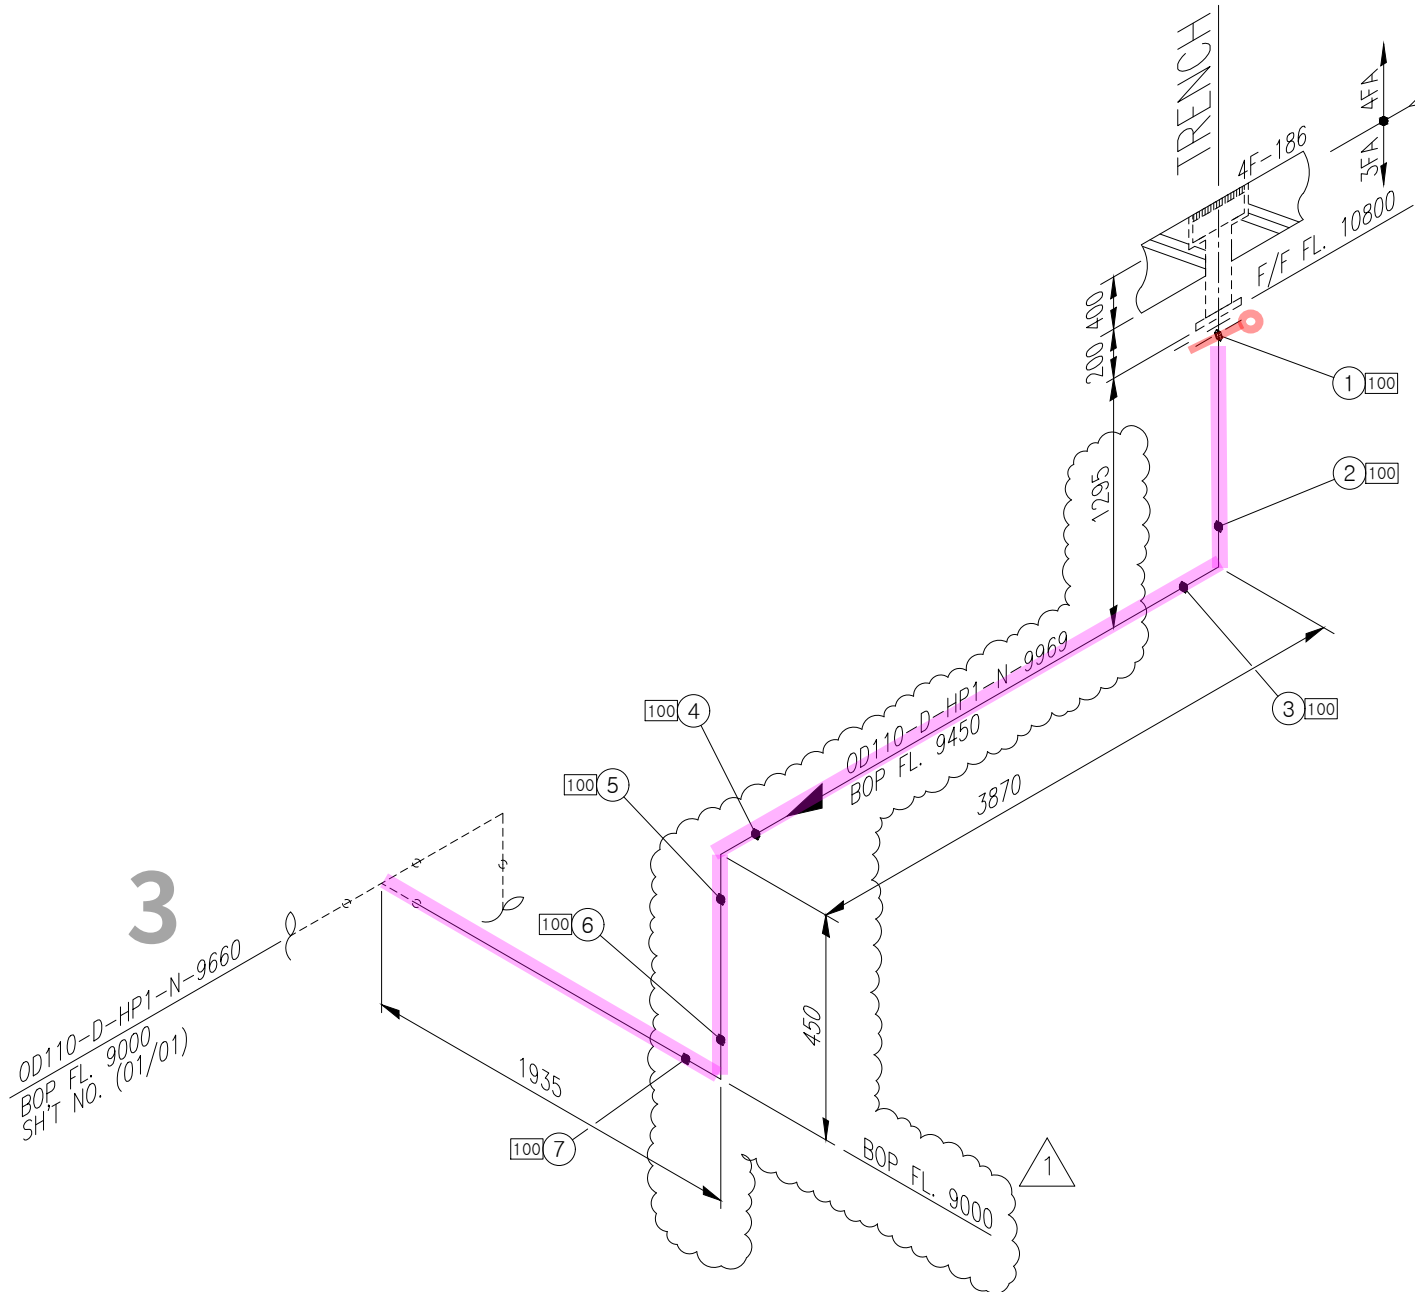[illegible]

<NOTE>
1. TRAY & ANGLE, CHANNEL SUPPORT가 적용되는
배관 ELEVATION은 현장 맞춤으로 한다.
2. (*) FIELD ADJUST

* PIPE : P/P1	* 90° ELBOW : E90	* 45° ELBOW : E45	* TEE : T	* RED.TEE : TR	* STUB-IN : STU	* REINFORCING PAD : RP	* CON.RED : RC	* ECC.RED : RE	* CON.SWAGE : RCS/RCS1	* ECC.SWAGE : RES/RES1	* NIPPLE : NP/NP1/NP2	* CAP : CAP/CAP1	* PLUG : PLG	* FULL COUPLING : FC	* HALF COUPLING : HF/HF1
* STUB-IN : STU	* SOCKET(HDPE/PVC) : SC	* SADDLE(HDPE) : SD	* FLANGE : F/F1	* GASKET : G/G1/G2	* BOLT & NUT : B/B1	* BLIND FLANGE : FB/FB1	* GATE VA. : VG/VG1/VG2	* BALL VA. : VB/VB1/VB10/VB2/VB210	* BUTTERFLY VA. : VF/VF4	* CHECK VA. : VC/VC1/VC2/VC3/VC4/VC5/VC6/VC7					
* GLOBE VA. : VL/VL1/VL2	* DIAPHRAGM VA. : VD/VD10	* DAMPER : VP	* QUICK COUPLING : SQC	* FLEXIBLE JOINT(STEEL) : FLXB	* FLEXIBLE JOINT(RUBBER) : FLXR	* FLEXIBLE JOINT(STEEL PTFE LINED) : FLXL	* FLEXIBLE HOSE : FLXH	* STEAM TRAP : ST	* SPRAY NOZZLE : SPN	* EMERGENCY SHOWER : SSH					
* STRAINER(Y-TYPE) : YSTR	* STRAINER(T-TYPE) : TSTR	* STRAINER(BUCKET-TYPE) : BSTR	* ANCHOR PLATE : STOP	* BIRD SCREEN : BS	* ISOLATION KIT : IK	* UNLOADING BOX : UB	* AIR TRAP : AT	* LOTO : LOTO	* SIGHT GLASS : SG	* PRESSURE GAUGE : PG	* SHILED : SH	* SPECIAL BOLT & NUT : BL/BL1			

INSULATION	CODE	N	CONDITION	PRESS. (kg/cm2g)	TEMP. (°C)	AREA	W14								CONTRACTOR		PROJECT NAME	
	THICK.	—	DESIGN	1	60	UNIT	3FA								M15X Ph4 Project			
			OPERATING	ATM	AMB	REF. PLAN DWG. CJ-M15W14-PI-A30-030008-D		25.03.31	REVISED AS MARKED	황래중	안남후	박동영	COMMODITY	D	JOB NO.			
						REF. P & ID CJ-M15W13-PR-A20-000084		25.01.24	APPROVED FOR CONSTRUCTION	황래중	안남후	박동영	LINE NO. OD110-D-HP1-N-9969	22330D				
							REV. NO.	DATE	DESCRIPTION	BY	CHK	APP'D		SH'T NO. 01 / 01	REV. 1			




CLIENT




4

CONTRACTOR		PROJECT NAME
		M15X Ph4 Project
명	COMMODITY D	JOB NO.
명		22330D
0	LINE NO. OD110-D-HP1-N-9969	SH'T NO. REV.
		01 / 01 1

INSULATION	CODE	N	CONDITION	PRESS. (kg/cm2g)	TEMP. (°C)	AREA	W14						
	THICK.	—	DESIGN	1	60	UNIT	3FA						
			OPERATING	ATM	AMB	REF. PLAN DWG.		1	25.03.31	REVISED AS MARKED	황래중	안남후	박동
						CJ-M15W14-PI-A30-030008-D		0	25.01.24	APPROVED FOR CONSTRUCTION	황래중	안남후	박동
						REF. P. & ID		REV. NO.	DATE	DESCRIPTION	BY	CHK	APP.
						CJ-M15W13-PR-A20-000084							

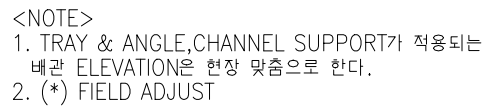

CLIENT		 5	
CONTRACTOR 		PROJECT NAME	
		M15X Ph4 Project	
영	COMMODITY	JOB NO.	
	D	22330D	
영	LINE NO.	SH'T NO.	REV.
D	OD160-D-HP1-N-9610	01 / 01	1

 INSULATION	CODE	N	CONDITION	PRESS. (kg/cm2g)	TEMP. (°C)	AREA W14							CONTRACTOR	PROJECT NAME	
	THICK.	-	DESIGN	1	60	UNIT 3FA								M15X Ph4 Project	
			OPERATING	ATM	AMB	REF. PLAN DWG. CJ-M15W14-PI-A30-030008-D		25.03.31	REVISED AS MARKED	황래중	안남후	박동영	COMMODITY	D	JOB NO.
						REF. P & ID CJ-M15W13-PR-A20-000084		25.01.24	APPROVED FOR CONSTRUCTION	황래중	안남후	박동영	LINE NO.	OD160-D-HP1-N-9610	SH'T NO. 01 / 01
							REV. NO.	DATE	DESCRIPTION	BY	CHK	APP'D			REV. 1