


DRAWING LIST FOR TEST PACKAGE

D-581

PROJECT NO.: 22328D

PROJECT TITLE : M15X Ph2 Project

No	PKG No	UNIT	LINE NUMBER			P&ID		REMARK
			ISO DRAWING No	SHEET	REV	P&ID No	REV	
1	581	4F	OD63-D-HP1-9964-01	1 OF 1	1	CJ-M15W13-PR-A20-000084	2	
2	581	4F	OD63-D-HP1-9965-01	1 OF 1	1	CJ-M15W13-PR-A20-000084	2	
3	581	3F	OD63-D-HP1-9966-01	1 OF 1	1	CJ-M15W13-PR-A20-000084	2	
4	581	5F	OD63-D-HP1-9967-01	1 OF 1	1	CJ-M15W13-PR-A20-000084	2	


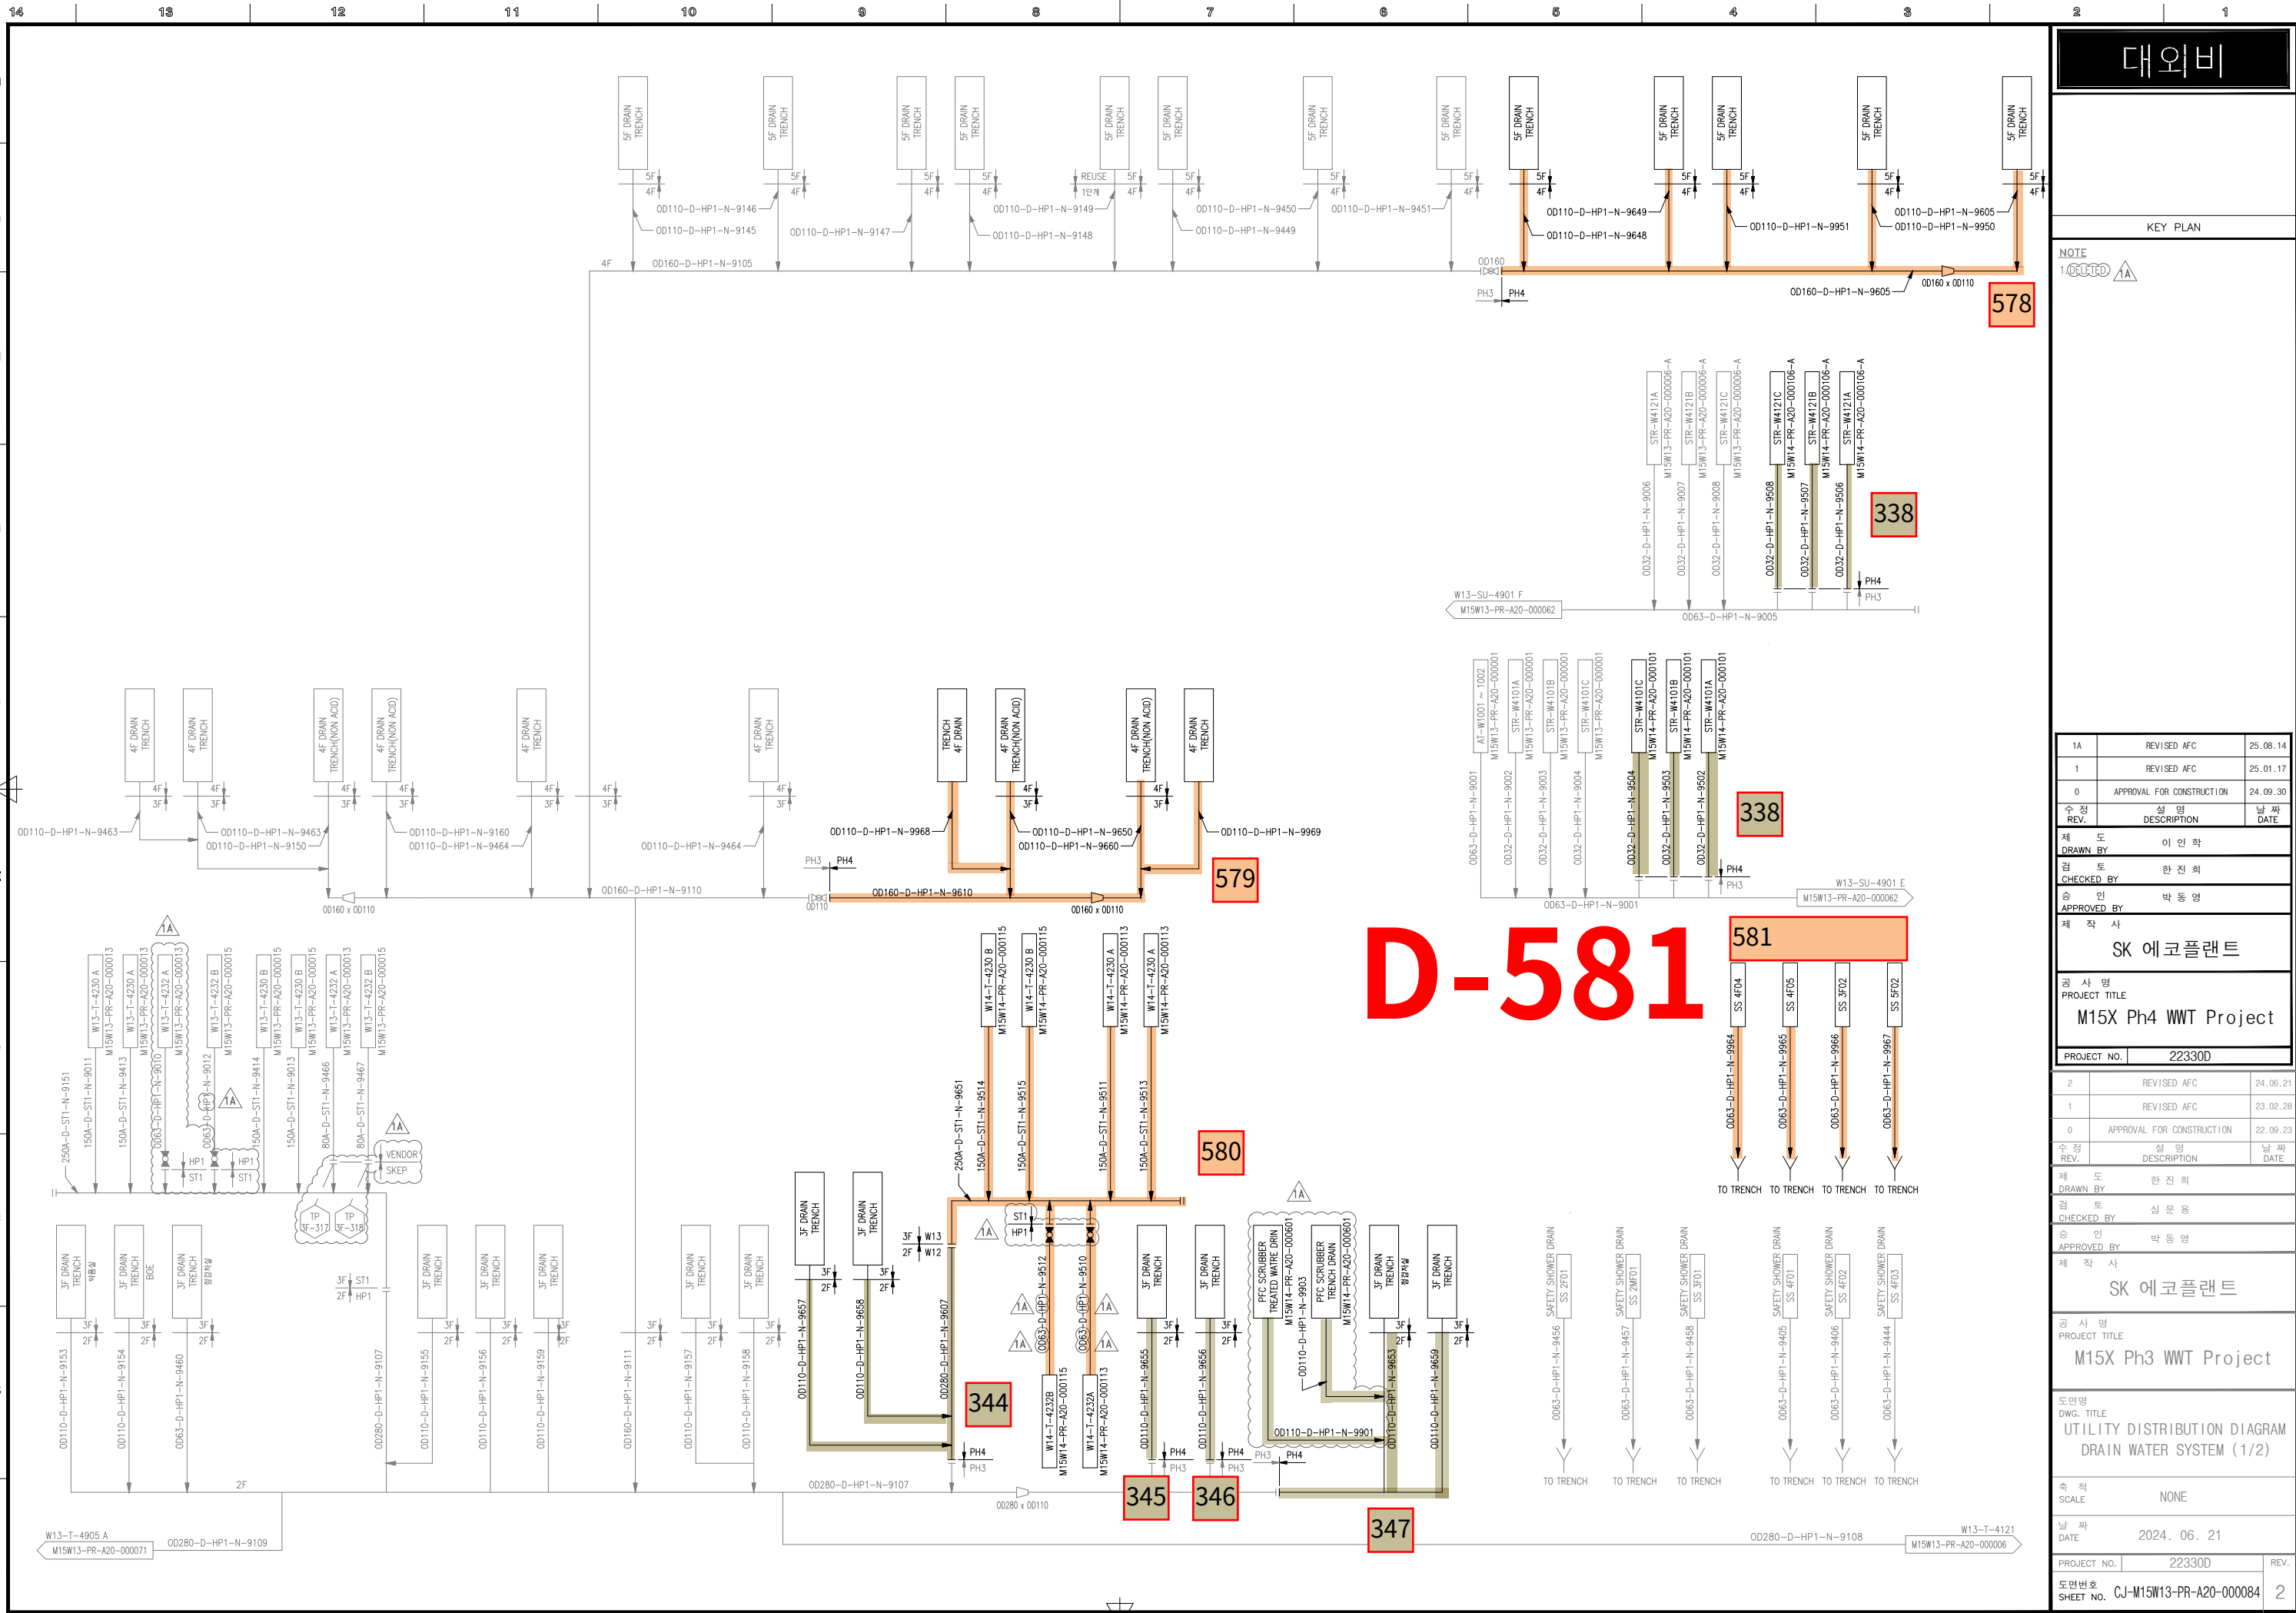


대외비



KEY PLAN

NOTE
1. (C) (D) 1A

1A	REVISED AFC	25.08.14
1	REVISED AFC	25.01.17
0	APPROVAL FOR CONSTRUCTION	24.09.30
수정 REV.	설명 DESCRIPTION	날짜 DATE
제 도 이 인 학		
검 토 한 진 회		
승 인 박 동 영		
APPROVED BY		
제 작 사 SK 에코플랜트		
공 사 명 PROJECT TITLE		
M15X Ph4 WWT Project		
PROJECT NO. 22330D		
2	REVISED AFC	24.06.21
1	REVISED AFC	23.02.28
0	APPROVAL FOR CONSTRUCTION	22.09.23
수정 REV.	설명 DESCRIPTION	날짜 DATE
제 도 한 진 회		
검 토 심 무 영		
승 인 박 동 영		
APPROVED BY		
제 작 사 SK 에코플랜트		
공 사 명 PROJECT TITLE		
M15X Ph3 WWT Project		
도면명 DWG. TITLE		
UTILITY DISTRIBUTION DIAGRAM DRAIN WATER SYSTEM (1/2)		
속 척 SCALE		
NONE		
날 짜 DATE		
2024. 06. 21		
PROJECT NO. 22330D		
도면번호 SHEET NO.		
CJ-M15W13-PR-A20-000084		
REV. 2		

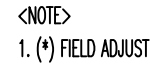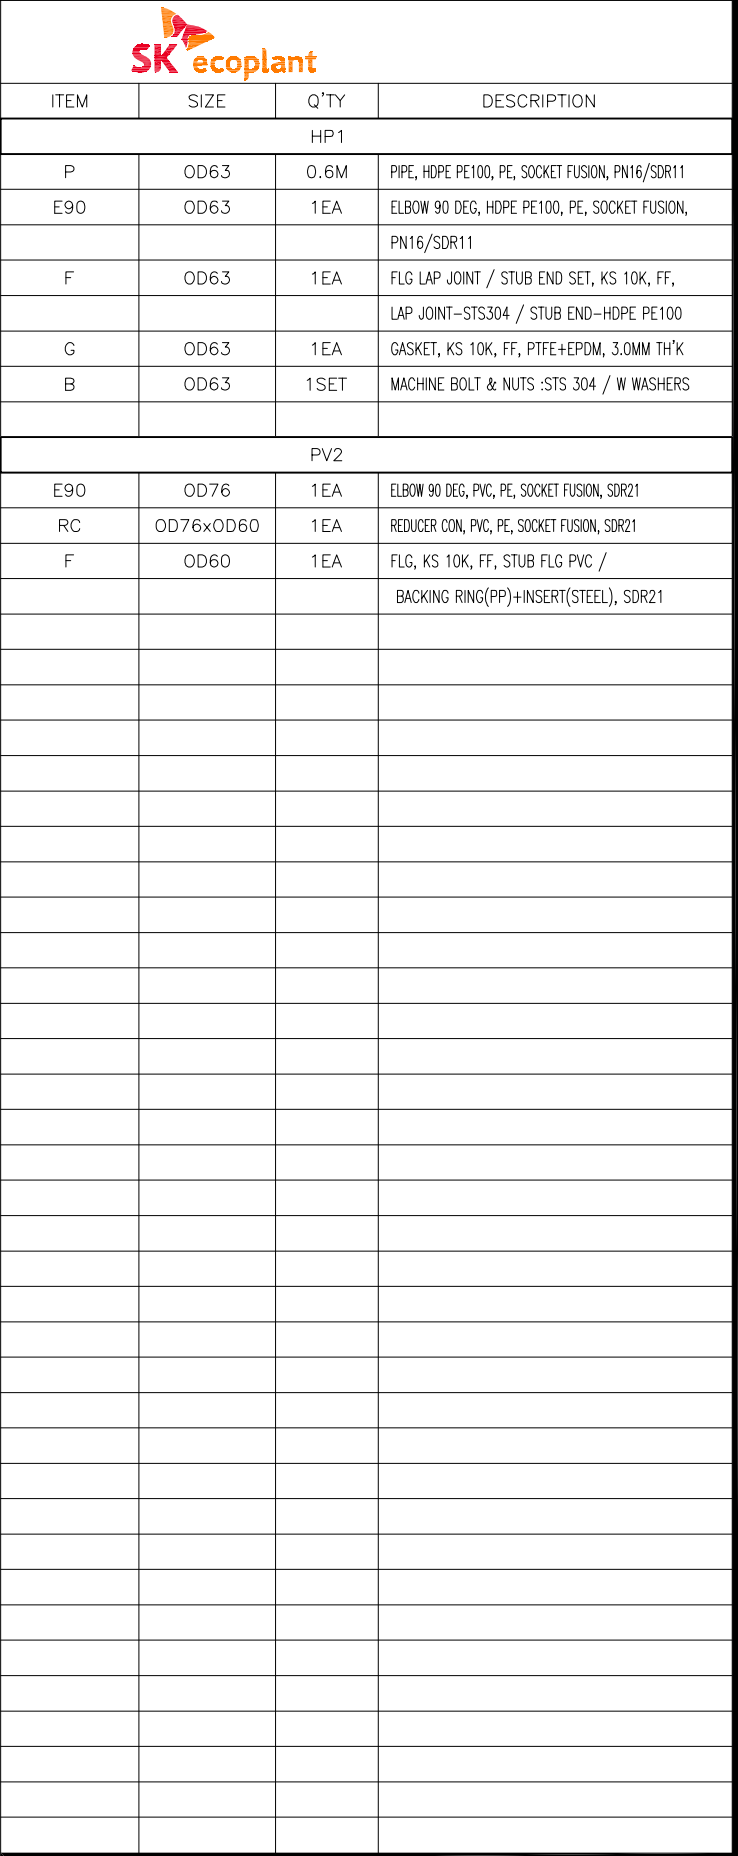

CLIENT		1	
			
CONTRACTOR		PROJECT NAME	
D		M15X Ph4 Project	
COMMODITY		JOB NO.	
D		22330D	
LINE NO.		SH'T NO.	REV.
OD63-D-HP1-N-9964		01 / 01	0

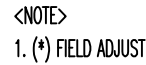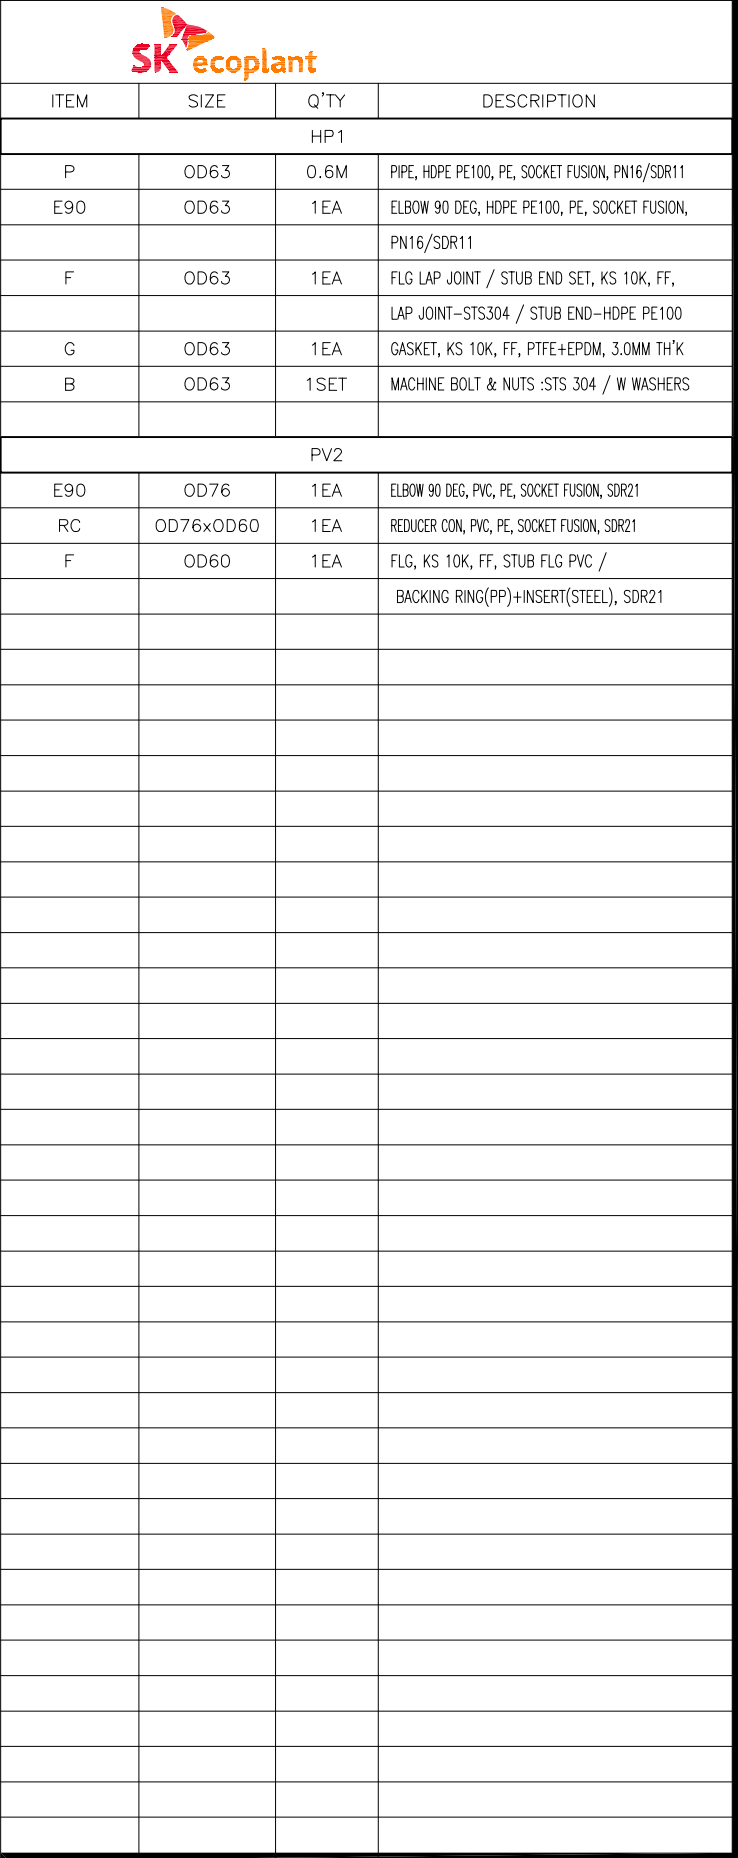

CLIENT				2	
CONTRACTOR			PROJECT NAME		
			M15X Ph4 Project		
COMMODITY			JOB NO.		
D			22330D		
LINE NO.			SH'T NO.		REV.
OD63-D-HP1-N-9965			01 / 01		0

INSULATION	CODE	-	CONDITION	PRESS. (kg/cm2g)	TEMP. (°C)	AREA	W13							CONTRACTOR 	PROJECT NAME	
	THICK.	-	DESIGN	1.00	60	UNIT	4FA								M15X Ph4 Project	
			OPERATING			REF. PLAN DWG. CJ-M15W14-PI-A30-040007-A								COMMODITY D	JOB NO. 22330D	
						REF. P & ID CJ-M15W13-PR-A20-000084			23.02.28	APPROVED FOR CONSTRUCTION	정경만	이광면	박동영	LINE NO. 0D63-D-HP1-N-9965	SH'T NO. 01 / 01	REV. 0
								REV. NO.	DATE	DESCRIPTION	BY	CHK	APP'D			



CLIENT  3

CONTRACTOR 		PROJECT NAME M15X Ph4 Project	
COMMODITY D		JOB NO. 22330D	
LINE NO. OD63-D-HP1-N-9966	SH'T NO. 01 / 01	REV. 0	



CLIENT



4

CONTRACTOR 

PROJECT NAME
M15X Ph3 Project

COMMODITY	D
-----------	---

JOB NO. 22330D

LINE NO.	OD63-D-HP1-N-9967
----------	-------------------

SH'T NO. 01 / 01	REV. 0
---------------------	-----------