

DRAWING LIST FOR TEST PACKAGE



AIR-MX-585

PROJECT NO.: 22328D

PROJECT TITLE : M15X Ph2 Project

No	PKG No	UNIT	LINE NUMBER			P&ID		REMARK
			ISO DRAWING No	SHEET	REV	P&ID No	REV	
1	585	R2FA	150A-AIR-MX-ST1-N-7001-01	1 OF 1	1	CJ-M15W14-PR-A20-000501	1A	
2	585	R2FA	150A-AIR-MX-ST1-N-7002-01	1 OF 1	0	CJ-M15W14-PR-A20-000509	1A	
3	585	R1MF	50A-AIR-MX-ST1-N-7003-01	1 OF 1	0	CJ-M15W14-PR-A20-000509	1A	
4	585	R2FA	50A-AIR-MX-ST1-N-7003-01	1 OF 1	0	CJ-M15W14-PR-A20-000504	1A	

ITEM NO.	W14-T-4710
SERVICE	BRINE COLLECTION TANK
QTY	1
TYPE	RECTANGULAR
SIZE	W x L x H 0.5 x 5.775 x 7.05 (EH 2.05) 5.0 x 5.3 x 14.05 (EH 12.55)
CAPA	m3 (963 (EH 923))
HRT	hr 2.5
MATL	P.C. + FRP

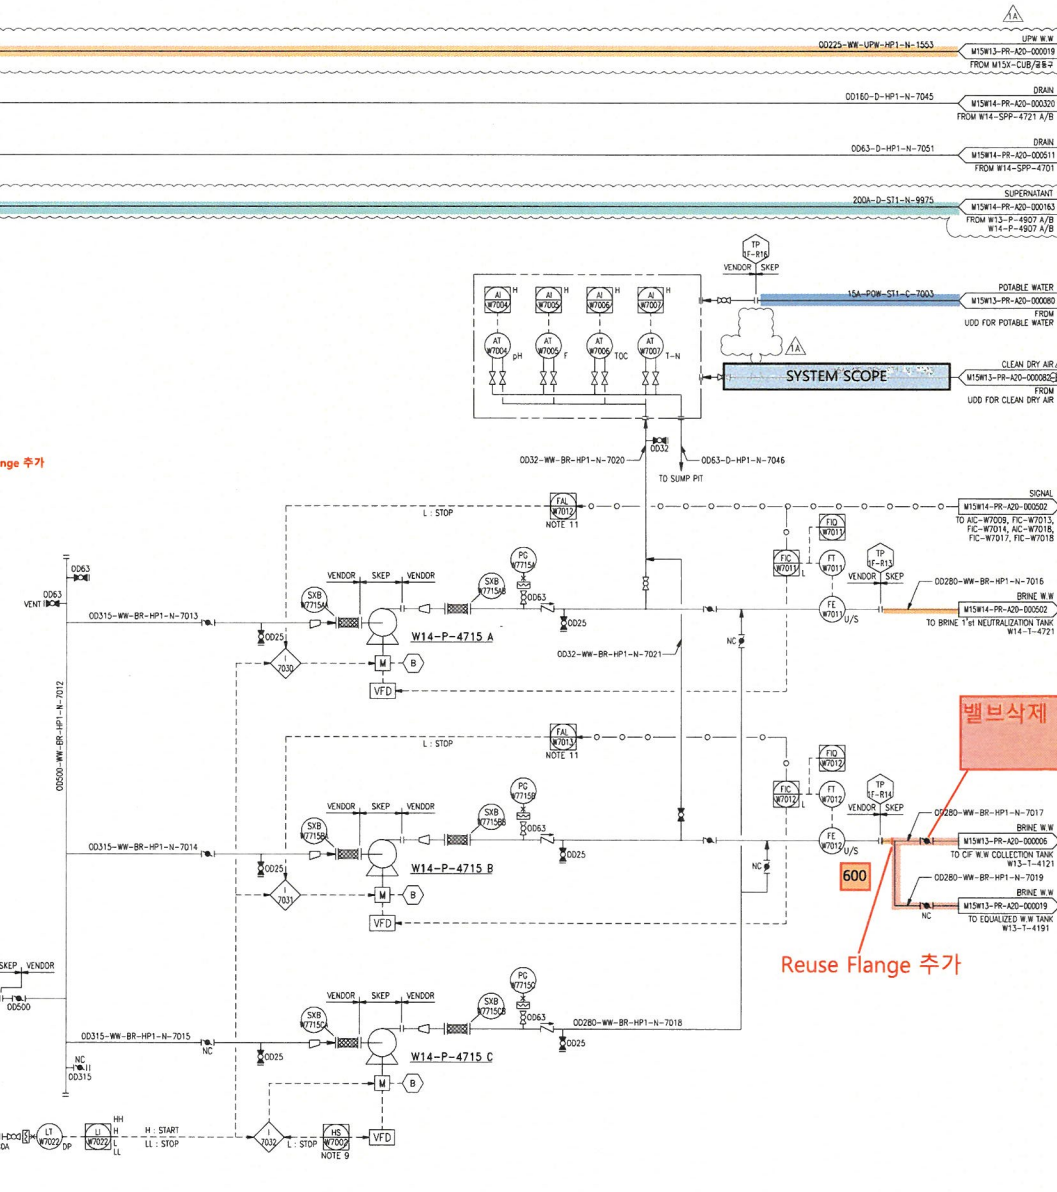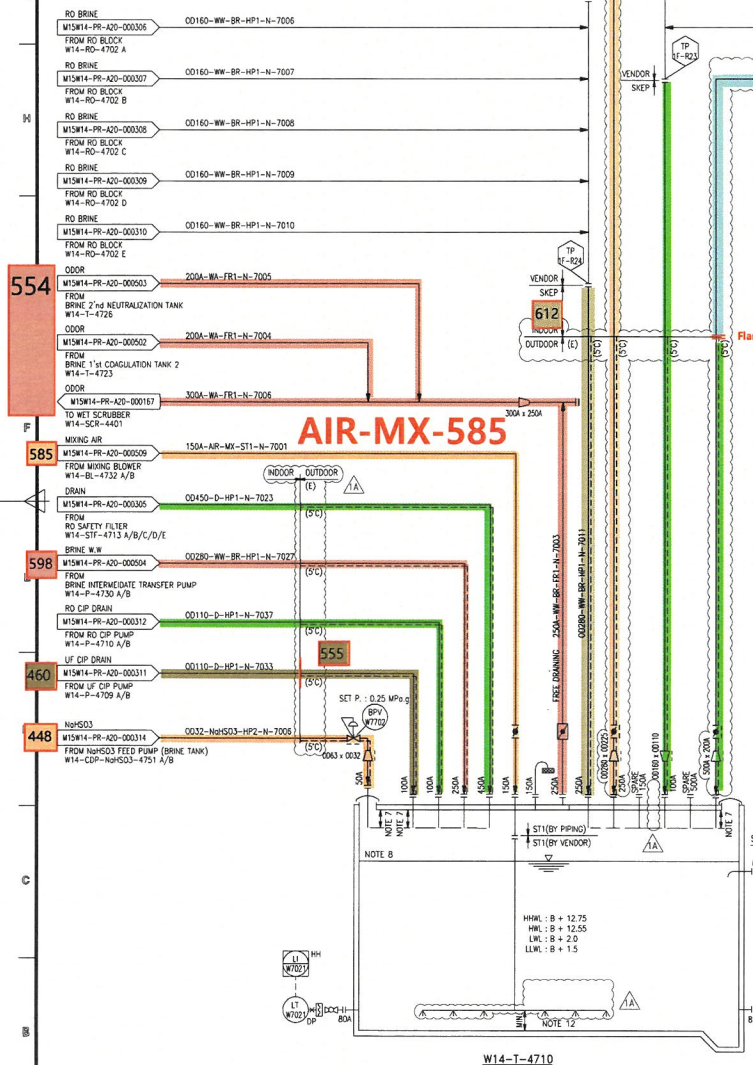

대외비

KEY PLAN (1F)

NOTE

1. TANK H/W 이하로 연결되는 모든 BLOCK 배관 설치함

2. 배관 단방향으로 흐름 표시하여 차단할 수 있는 CHAIN VALVE 또는 PLATFORM 구멍을

3. MANHOLE : 2m 이상 설치함

4. MANHOLE COVER : FRP

5. 5.0인치 CLOSE VALVE는 LOTO 설치

6. CENTRIFUGAL PUMP

7. TANK 내 유압 : CASING / IMPELLER

8. 4인치 FRP LINING TANKER SLEEVE: SUS304 + FRP LINING 48"

9. FIC-W7011/W7012를 대체함


10. INTERLOCK NO. 1-7030/7031/7032 (W14-P-4715 A/B/C AUTO STOP) : REMOTE STATUS W14-T-4710 LEVEL (LW-W7022) LOW STOP 및 W14-T-4715 A/B DISCHARGE FLOW (FAL-W7011/W7012) LOW STOP


11. BRINE TRANSFER PUMP RUN # 302 # 부하 용량

12. (DIFFUSER HOLE 또는 배관배치에 관한) 상세 사항은 VENDORMI에 문의함

REVISED A/C	25.06.14
REVISED A/C	25.01.17
APPROVAL FOR CONSTRUCTION	24.10.31
수정	설명
DRWING BY	이인혁
검	한진희
CHECKED BY	한진희
승인	박동영
APPROVED BY	박동영
제	사
SK 예코플랜트	
공 사 명	
PROJECT TITLE	
M15X Ph4 WWT Project	
도면명	
DWG. TITLE	
PIPING & INSTRUMENT DIAGRAM	
BRINE COLLECTION TANK & TRANSFER PUMP	
축척	
SCALE	
NONE	
날짜	
DATE	
2025. 08. 14	
PROJECT NO.	223300
도면번호	CJ-W15W14-PR-A20-000501
SHEET NO.	1A

ITEM NO.	W14-P-4715 A/B/C
SERVICE	BRINE TRANSFER PUMP
QTY	2 + 1
TYPE	CENTRIFUGAL (VVVF)
CAPA	m3/hr ea x mm
250 x 30 (D 29MPa)	
MATL	ALLOY20/ALLOY20
POWER [kW]	(37) 1/1A

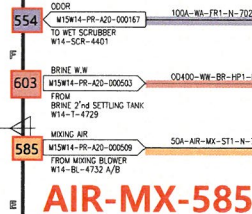
[illegible]

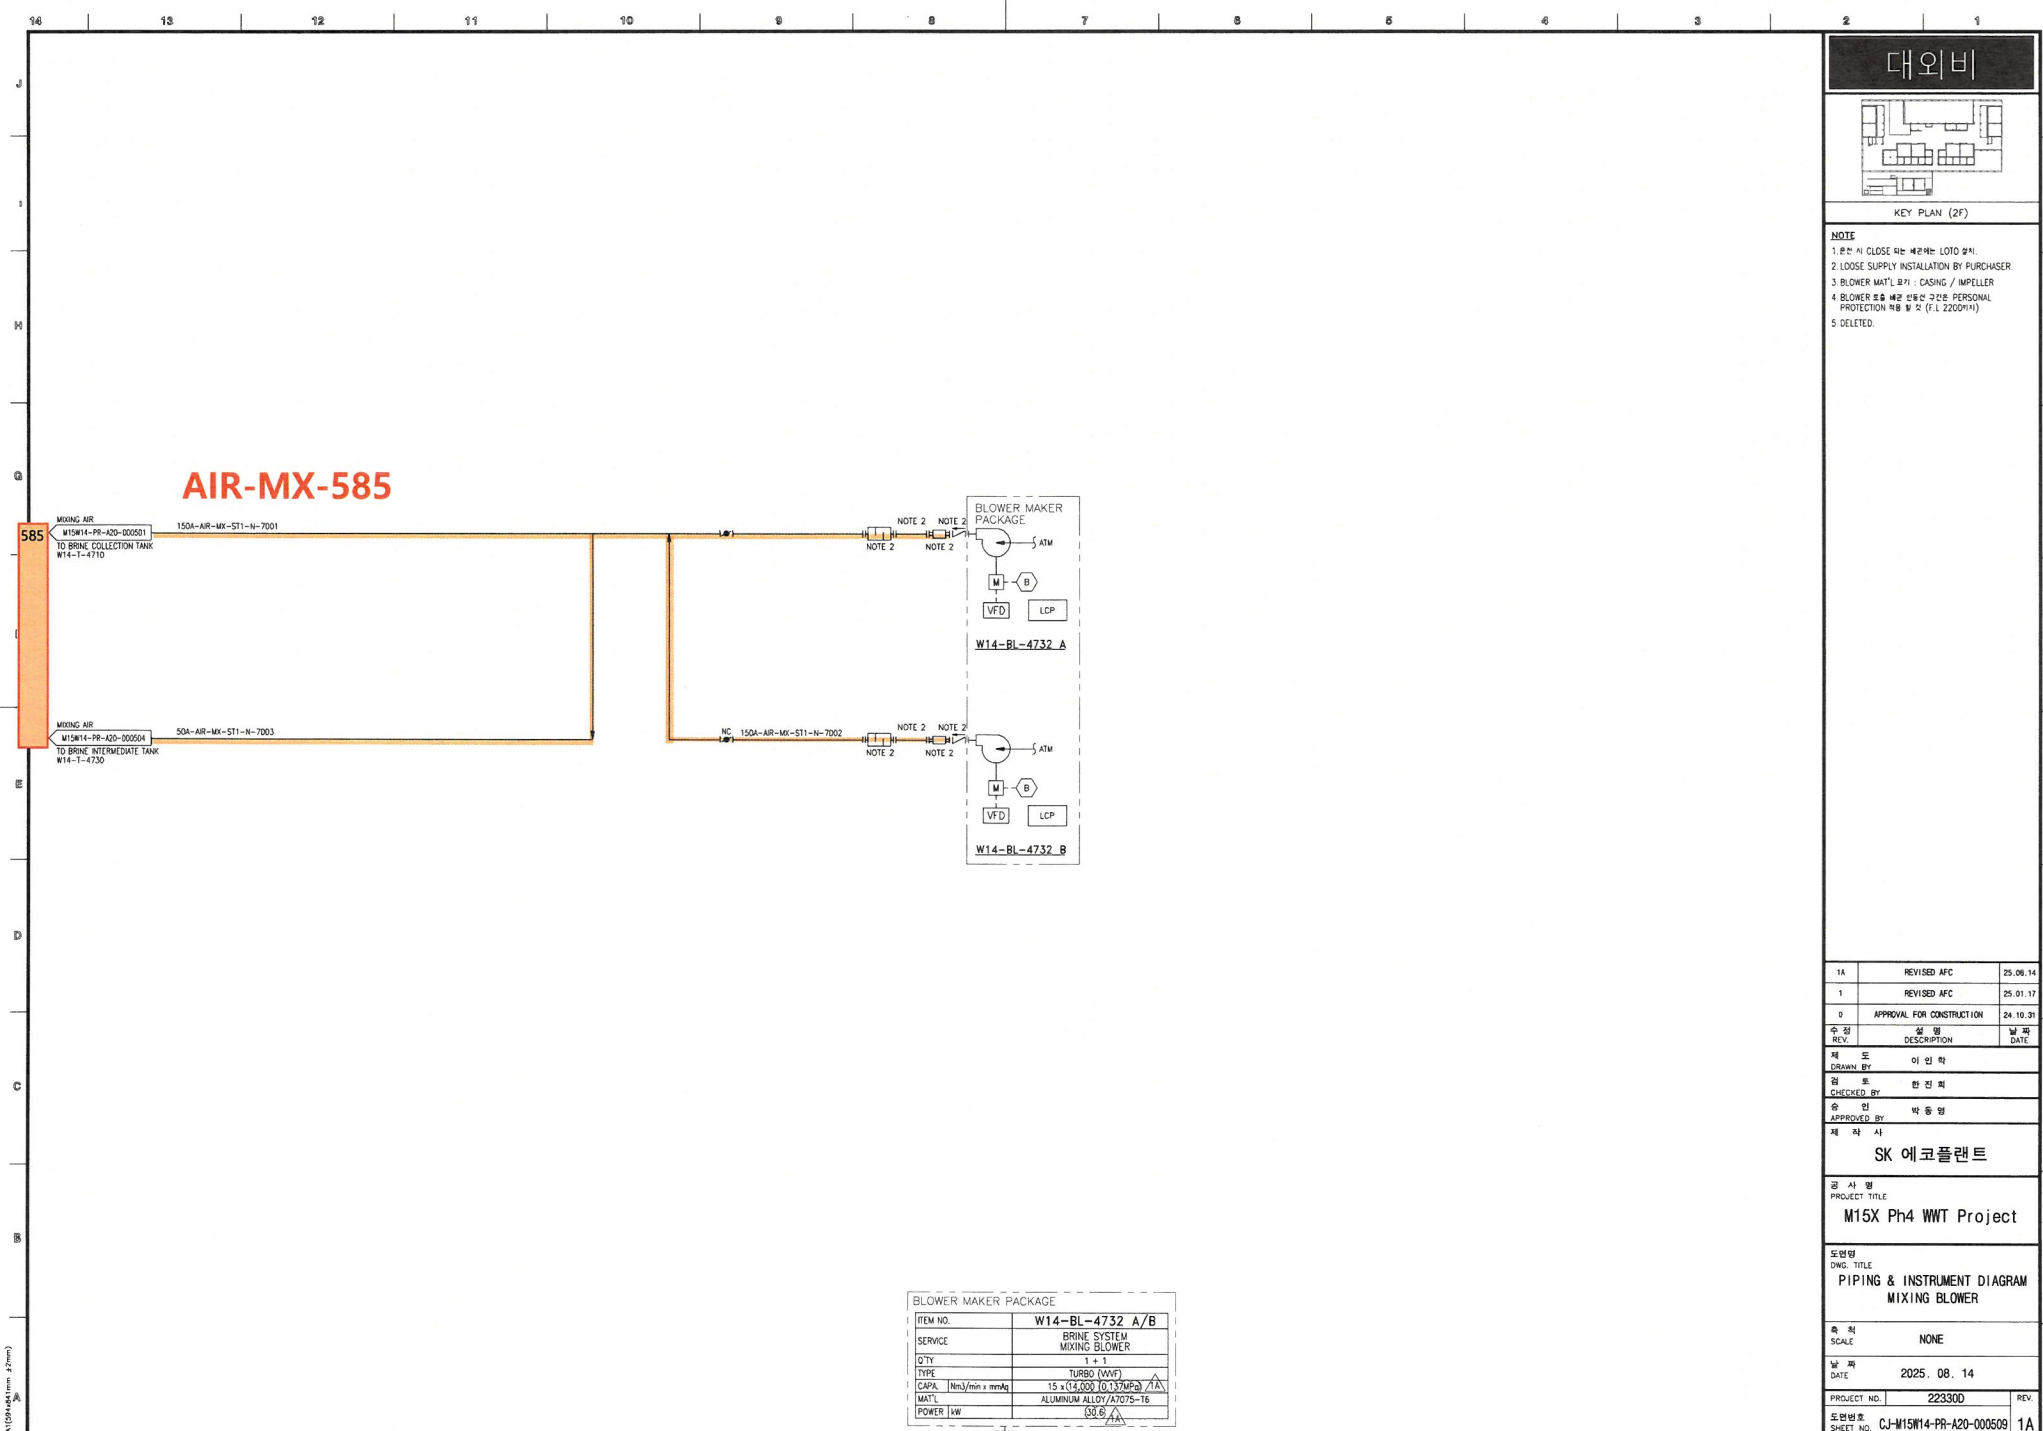

BLOWER MAKER PACKAGE	
ITEM NO.	W14-BL-4732 A/B
SERVICE	BRINE SYSTEM MIXING BLOWER
QTY	1 + 1
TYPE	TURBO (VVVF)
CAPAL	15 x (14,000 TO 13,700Pa) / 1A
MATL	ALUMINUM ALLOY (A7075-T6)
POWER [kW]	33.6 / 1A

대외비

KEY PLAN (2F)

NOTE

1. 본 시 CLOSE 또는 해체는 LOTO 실시.
2. LOOSE SUPPLY INSTALLATION BY PURCHASER.
3. BLOWER MATL. 표기 : CASING / IMPELLER
4. BLOWER 조립 해체 전 안전 수칙을 PERSONAL PROTECTION 착용 필수 (F.L. 2200mm)
5. DELETED

1A	REVISED AFC	25.06.14
1	REVISED AFC	25.01.17
0	APPROVAL FOR CONSTRUCTION	24.10.31
수정 REV.	설명 DESCRIPTION	날짜 DATE
제 도 인 자	이 인 자	
검 査 인 자	한 진 희	
승 인 인 자	박 동 영	
제 작 사	SK 에코플랜트	
공 사 명 PROJECT TITLE	M15X Ph4 WWT Project	
도면명 DWG. TITLE	PIPING & INSTRUMENT DIAGRAM MIXING BLOWER	
축 척 SCALE	NONE	
날 짜 DATE	2025. 08. 14	
PROJECT NO.	223300	REV.
도면번호 SHEET NO.	CJ-M15W14-PR-A20-000509	1A



참고: 본 도면은 SK HYNIX의 기업비밀 자료로서, 어떠한 경우에도 복제 및 사용, 분제, 제3자에게 공개, 누설 및 유출할 수 없으며, 회사는 유표자의 불법 사용으로 피해가 발생할 경우 유표자에게 민/형사상 책임을 요구할 수 있음.




CLIENT



2


[illegible]

경고 : 본 도면은 SK HYNIX의 기업비밀 자료로서, 어떠한 경우에도 목적 외 사용, 복제, 제3자에게 공개, 누설 및 유출할 수 없으며, 회사는 유도자의 불법 사용으로 피해가 발생할 경우 유도자에게 민/형사상 책임을 요구할 수 있음.

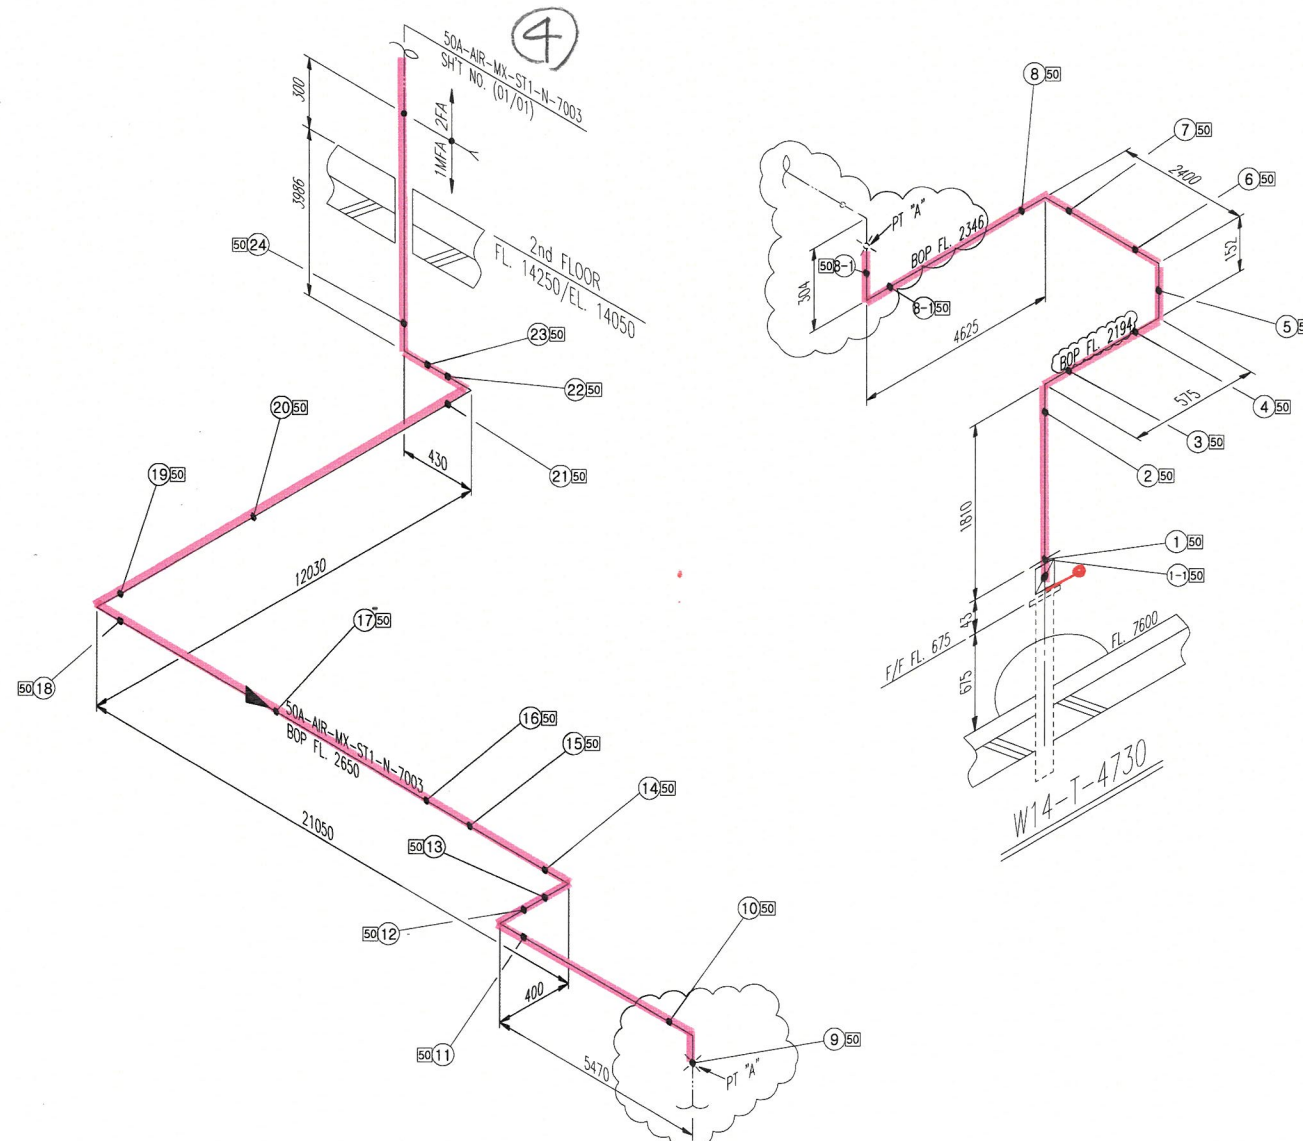


* PIPE: P/P1	* 90° ELBOW: E90	* 45° ELBOW: E45	* TEE: T	* RED TEE: TR	* STUB-IN: STU	* REINFORCING PAD: RP	* CON. RED: RC	* ECC. RED: RE	* CON. SWAGE: RCS/RCS1	* ECC. SWAGE: RES/RES1	* NIPPLE: NP/NP1/NP2	* CAP: CAP/CAP1	* PLUG: PLG	* FULL COUPLING: FC	* HALF COUPLING: HF/HF1
* STUB-IN: STU	* SOCKET(HOPE/PC): SC	* SADDLE(HOPE): SD	* FLANGE: F/F1	* GASKET: G/G1/G2	* BOLT & NUT: B/B1	* BLIND FLANGE: FB/FB1	* GATE VA.: VG/G1/VG2	* BALL VA.: VB/VB1/VB10/VB2/VB20	* BUTTERFLY VA.: VF/VF4	* CHECK VA.: VC/VC1/VC2/VC3/VC4/VC5/VC7					
* GLOBE VA.: VL/VL1/VL2	* DIAPHRAGM VA.: VD/VD0	* DAMPER: VP	* QUICK COUPLING: SQC	* FLEXIBLE JOINT(STEEL): FLXB	* FLEXIBLE JOINT(RUBBER): FLXR	* FLEXIBLE JOINT(STEEL PIPE LINED): FLXL	* FLEXIBLE HOSE: FLXH	* STEAM TRAP: ST	* SPRAY NOZZLE: SPN	* EMERGENCY SHOWER: SSH					
* STRAINER(Y-TYPE): YSTR	* STRAINER(T-TYPE): TSTR	* STRAINER(BUCKET-TYPE): BSTR	* ANCHOR PLATE: STOP	* BIRD SCREEN: BS	* ISOLATION KIT: IK	* UNLOADING BOX: UB	* AIR TRAP: AT	* LOTO: LOTO	* SIGHT GLASS: SG	* PRESSURE GAUGE: PG	* SHILED: SH	* SPECIAL BOLT & NUT: BL/BL1			

경고 : 본 도면은 SK HYNIX의 기밀비밀 자료로서, 어떠한 경우에도 목적 외 사용, 복제, 제3자에게 공개, 누설 및 유출할 수 없으며, 회사는 유도자의 불법 사용으로 피해가 발생할 경우 유도자에게 민/형사상 책임을 요구할 수 있음.

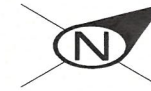

ITEM	SIZE	Q'TY	DESCRIPTION
ST1			
P	50A	32.3M	PIPE, STS 304TP, ERW, BE - SCH 10S
E90	50A	7EA	ELBOW 90 DEG LR, STS304, ERW, BE - SCH 10S

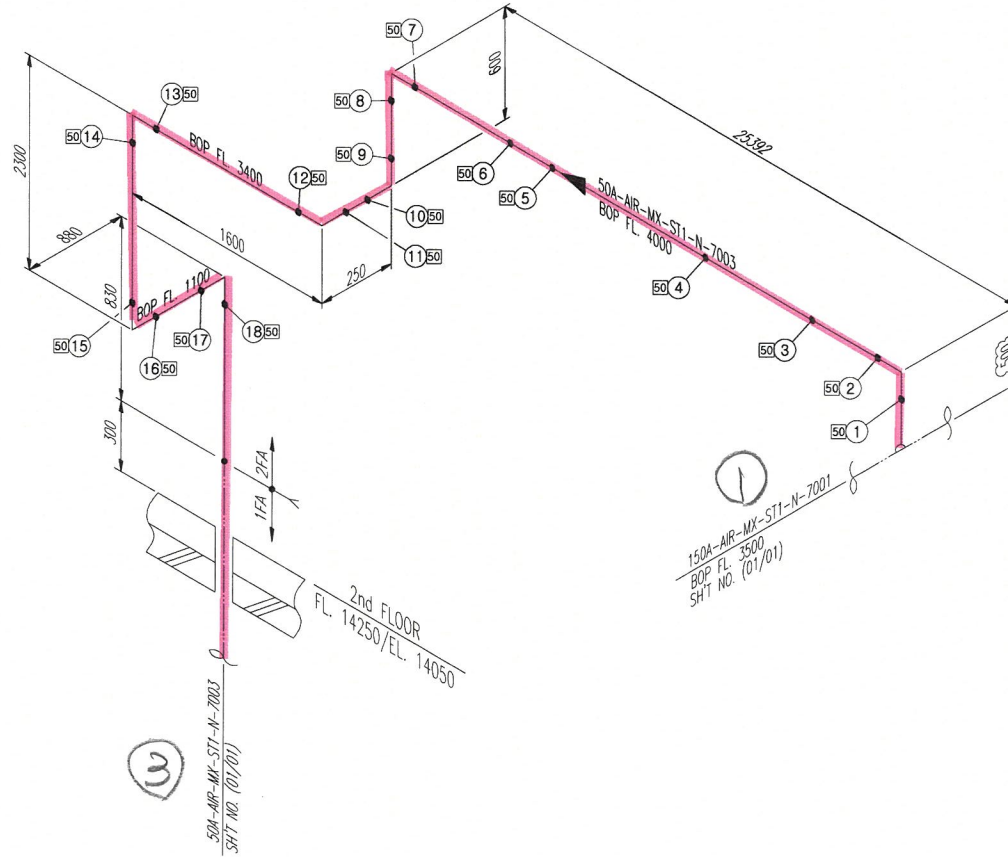

<NOTE>
1. (*) FIELD ADJUST

* PIPE : P/P1 * 90° ELBOW : E90 * 45° ELBOW : E45 * TEE : T * RED TEE : TR * STUB-IN : STU * REINFORCING PAD : RP * CON.RED : RC * ECC.RED : RE * CON.SWAGE : RCS/RCS1 * ECC.SWAGE : RES/RES1 * NIPPLE : NP/NP1/NP2 * CAP : CAP/CAP1 * PLUG : PLG * FULL COUPLING : FC * HALF COUPLING : HF/HF1
* STUB-IN : STU * SOCKET(HDPE/PVC) : SC * SADDLE(HDPE) : SD * FLANGE : F/F1 * GASKET : G/G1/G2 * BOLT & NUT : B/B1 * BLIND FLANGE : FB/FB1 * GATE VA : VG/VG1/VG2 * BALL VA : VB/VBLO/VB1/VB1LO/VB2/VB2LO * BUTTERFLY VA : VF/VF4 * CHECK VA : VC/VC1/VC2/VC3/VC4/VC5/VC6/VC7
* GLOBE VA : VL/VL1/VL2 * DIAPHRAGM VA : VD/VDLO * DAMPER : VP * QUICK COUPLING : SQC * FLEXIBLE JOINT(STEEL) : FLXJ * FLEXIBLE JOINT(RUBBER) : FLXR * FLEXIBLE JOINT(STEEL PIPE LINED) : FLXL * FLEXIBLE HOSE : FLXH * STEAM TRAP : ST * SPRAY NOZZLE : SPN * EMERGENCY SHOWER : SSH
* STRAINER(Y-TYPE) : YSTR * STRAINER(T-TYPE) : TSTR * STRAINER(BUCKET-TYPE) : BSTR * ANCHOR PLATE : STOP * BIRD SCREEN : BS * ISOLATION KIT : IK * UNLOADING BOX : UB * AIR TRAP : AT * LOTO : LOTO * SIGHT GLASS : SG * PRESSURE GAUGE : PG * SHIELD : SH * SPECIAL BOLT & NUT : BL/BL1

INSULATION	CODE	N	CONDITION	PRESS. (kg/cm2g)	TEMP. (°C)	AREA	W14							CONTRACTOR	PROJECT NAME
	THICK.	-	DESIGN	6.4	60	UNIT	R2FA								M15X Ph4 Project
			OPERATING	4	AMB	REF. PLAN DWG.								COMMODITY	JOB NO.
						CJ-M15W14-PI-A30-020016-B								AIR-MX	22330D
						REF. P & ID								LINE NO.	SH'T NO.
						CJ-M15W14-PR-A20-000504,000509								50A-AIR-MX-ST1-N-7003	01 / 01
								REV. NO.	DATE	DESCRIPTION	BY	CHK	APP'D		REV.

경고 : 본 도면은 SK HYNIX의 기밀비밀 자료로서, 어떠한 경우에도 목적 외 사용, 복제, 제3자에게 공개, 누설 및 유출할 수 없으며, 회사는 유표자의 불법 사용으로 피해가 발생할 경우 유표자에게 민/형사상 책임을 요구할 수 있음.

PUNCH LIST

Project No : 22330D

Package No :

Project Title : M15X Ph3 Project

Date :

S/N	Drawing No	Description	Category A B C	Punch Clear Status			
				작성자		확인자	
				Name	Sign	Name	Sign
1							
2							
Remarks

- A : Before Hydro Test
- B : Before M/C
- C : Before Commissioning