



DRAWING LIST FOR TEST PACKAGE

PROJECT NO.: 22328D

PROJECT TITLE : M15X Ph2 Project

STM-LPC-586

No	PKG No	UNIT	LINE NUMBER			P&ID		REMARK
			ISO DRAWING No	SHEET	REV	P&ID No	REV	
1	586	4FA	80A-STM-LPC-CS1-P-9514-01	1 OF 1	1	CJ-M15W14-PR-A20-000112	1A	
2	586	4FA	80A-STM-LPC-CS1-P-9515-01	1 OF 1	1	CJ-M15W14-PR-A20-000114	1A	
3	586	5FA	80A-STM-LPC-CS1-P-9514-01	1 OF 1	0	CJ-M15W14-PR-A20-000127	1A	
4	586	RFA	80A-STM-LPC-CS1-P-9514-01	1 OF 1	0	CJ-M15W14-PR-A20-000127	1A	

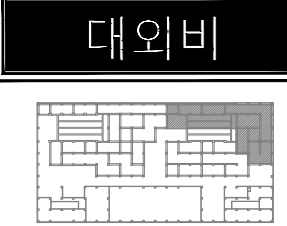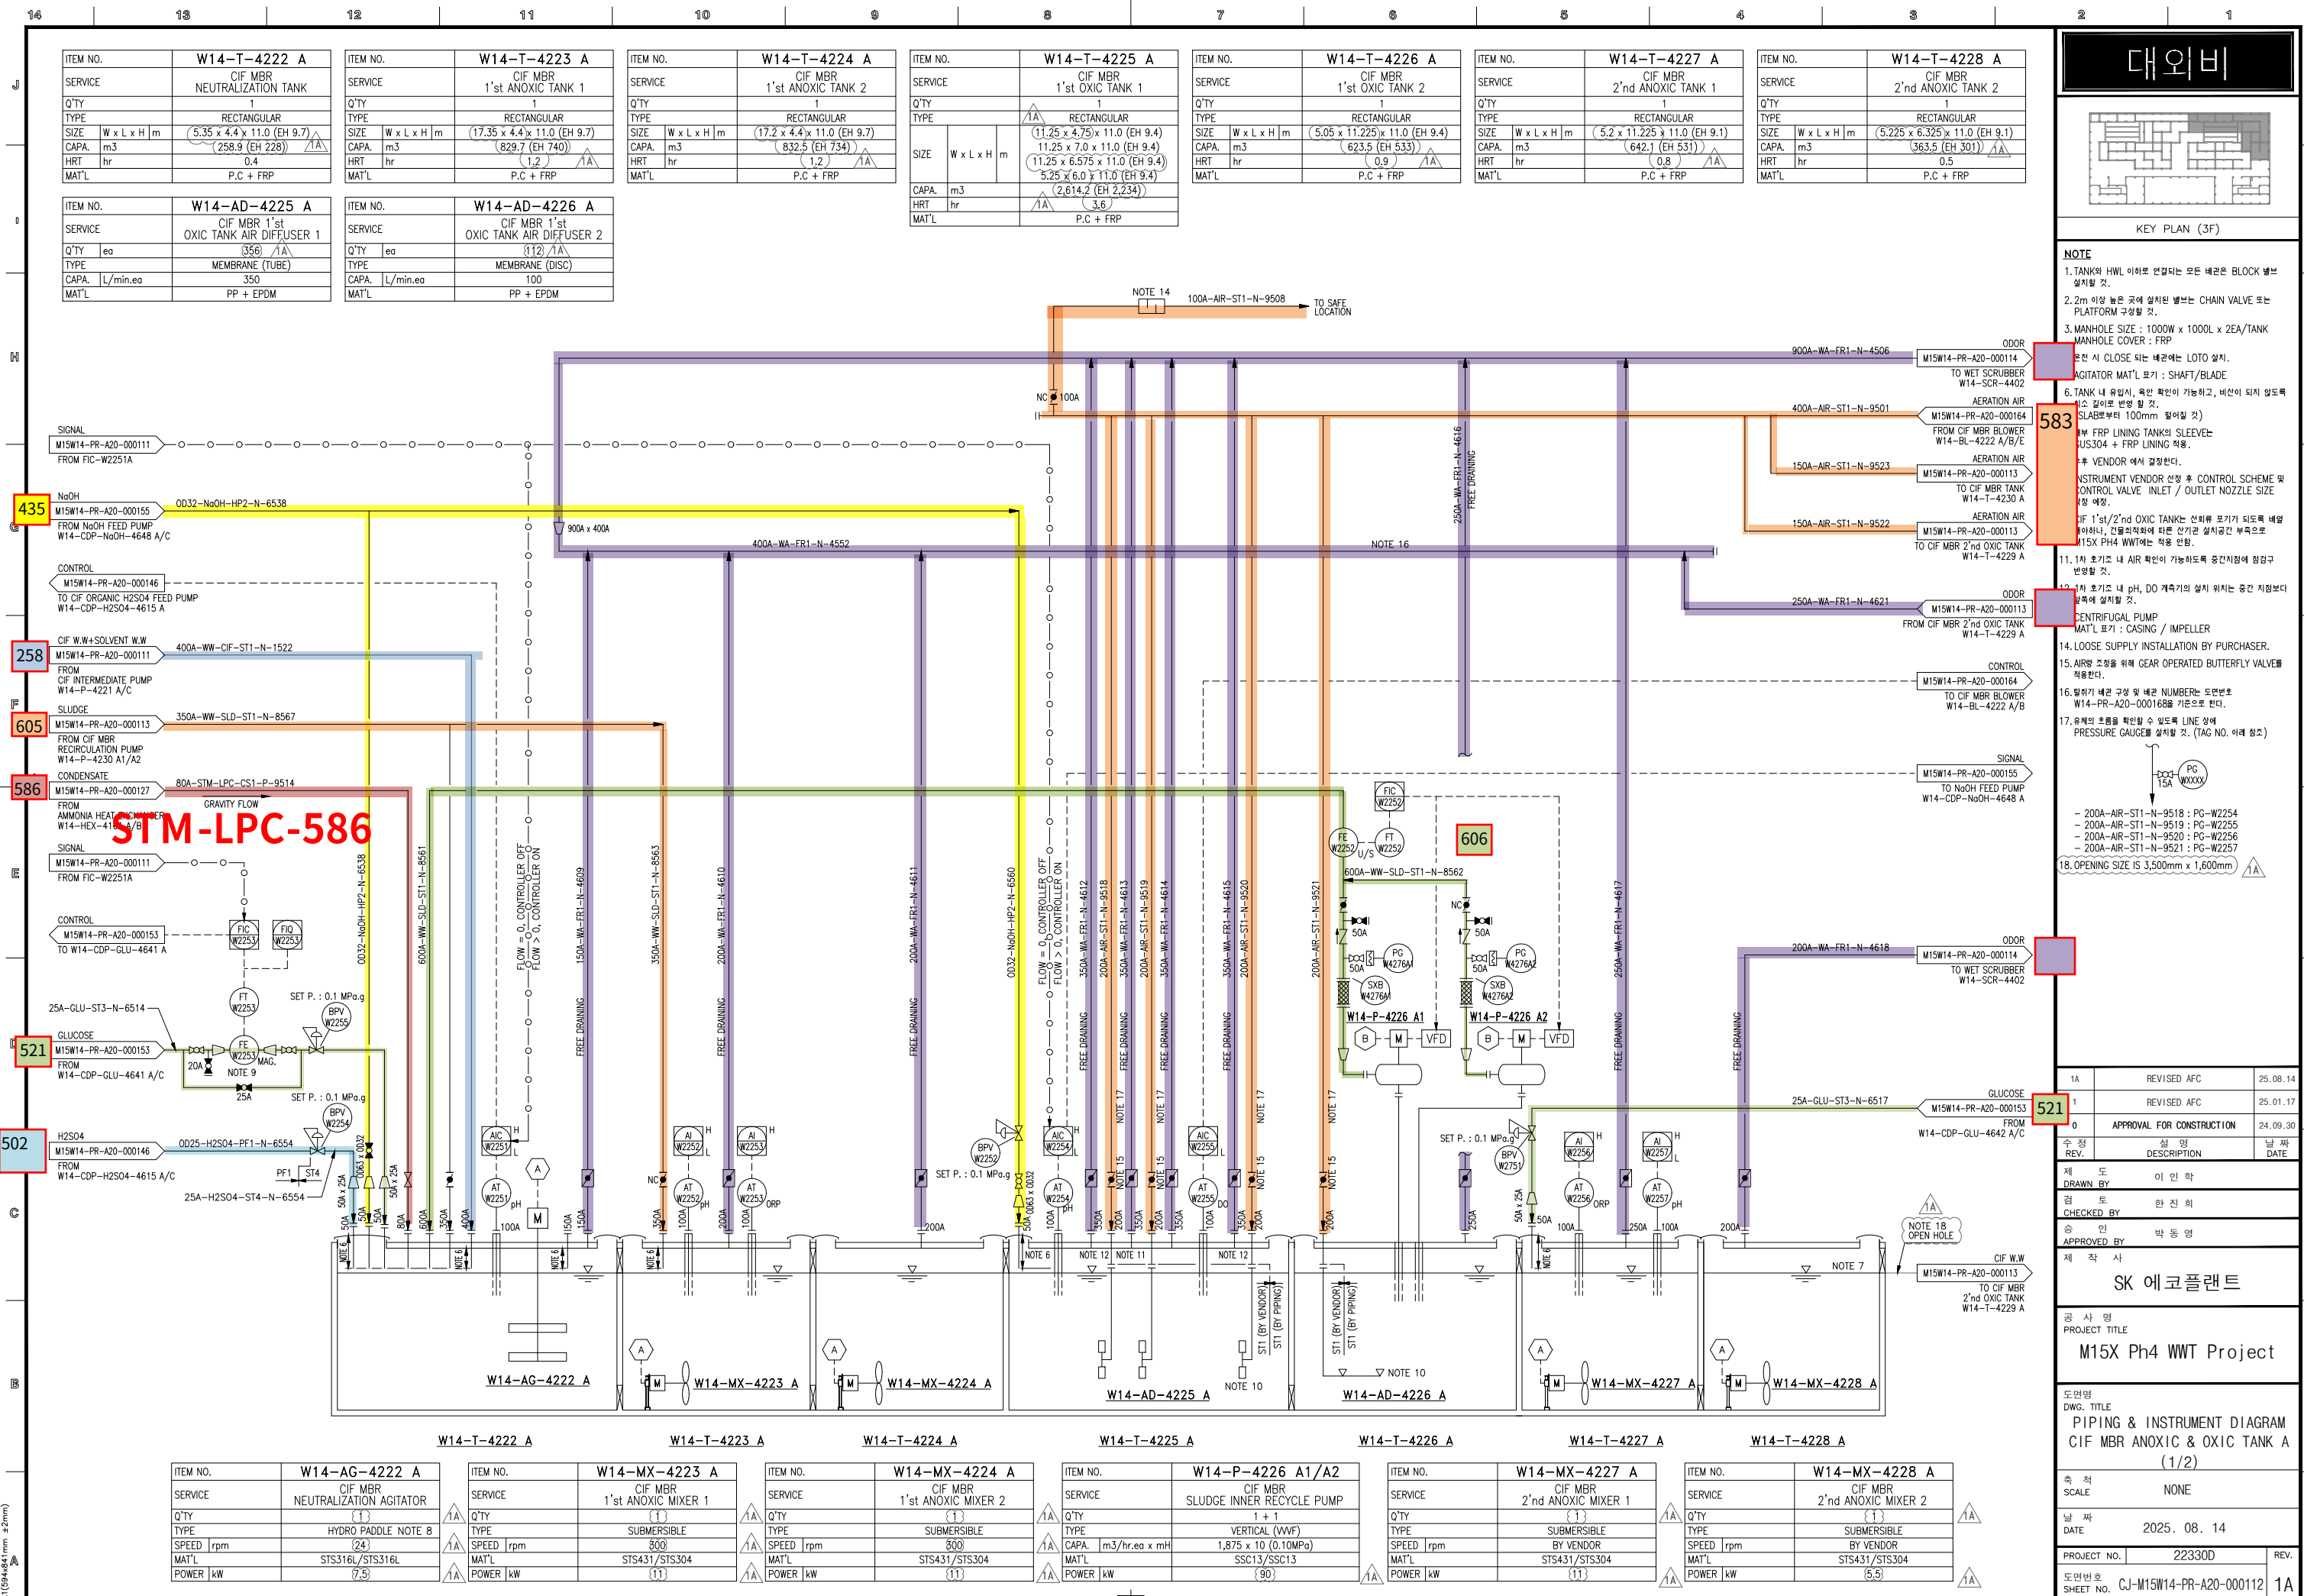

- NOTE
1. TANK의 HWL 이하로 연결되는 모든 배관은 BLOCK 별보 설치할 것.
 2. 2m 이상 높은 곳에 설치된 배관은 CHAIN VALVE 또는 PLATFORM 구성할 것.
 3. MANHOLE SIZE : 1000W x 1000L x 2EA/TANK MANHOLE COVER : FRP
 4. 운전 시 CLOSE 되는 배관에는 LOTO 설치.
 5. AGITATOR MAT'L 표기 : SHAFT/BLADE
 6. TANK 내 유입시, 폭탄 확인이 가능하고, 배선이 되지 않도록 최소 길이로 반영 할 것.
 7. FRP LINING TANK의 SLEEVE는 SUS304 + FRP LINING 적용.
 8. 이후 VENDOR 에서 결정한다.
 9. INSTRUMENT VENDOR 선정 후 CONTROL SCHEME 및 CONTROL VALVE INLET / OUTLET NOZZLE SIZE 결정 예정.
 10. CIF 1st/2nd OXIC TANK는 전회류 포기가 되도록 배설 하여야나, 건물외곽에 따른 산기온 설치공간 부족으로 115X PH4 WWT에는 적용 안함.
 11. 1차 호기조 내 AIR 확인이 가능하도록 중간지점에 점검구 반영할 것.
 12. 1차 호기조 내 pH, DO 계측기의 설치 위치는 중간 지점보다 상부에 설치할 것.
 13. CENTRIFUGAL PUMP MAT'L 표기 : CASING / IMPELLER
 14. LOOSE SUPPLY INSTALLATION BY PURCHASER.
 15. AIR용 조정을 위해 GEAR OPERATED BUTTERFLY VALVE를 적용한다.
 16. 말리기 배관 구성 및 배관 NUMBER는 도면번호 W14-PR-A20-000168을 기준으로 한다.
 17. 유체의 흐름을 확인할 수 있도록 LINE 상에 PRESSURE GAUGE를 설치할 것. (TAG NO. 아래 참조)
 18. OPENING SIZE IS 3,500mm x 1,600mm

- 200A-AIR-ST1-N-9518 : PG-W2254
- 200A-AIR-ST1-N-9519 : PG-W2255
- 200A-AIR-ST1-N-9520 : PG-W2256
- 200A-AIR-ST1-N-9521 : PG-W2257

1A

1A	REVISED AFC	25.08.14
1	REVISED AFC	25.01.17
0	APPROVAL FOR CONSTRUCTION	24.09.30

수정	실명	날짜
REV.	DESCRIPTION	DATE
제	도	인
DRAWN BY	이인학	
검	토	회
CHECKED BY	한진희	
승	인	명
APPROVED BY	박동영	
제	작	사

SK 에코플랜트

공 사 명
PROJECT TITLE
M15X Ph4 WWT Project

도면명
DWG. TITLE
PIPING & INSTRUMENT DIAGRAM
CIF MBR ANOXIC & OXIC TANK A
(1/2)

속 척
SCALE
NONE

날 짜
DATE
2025. 08. 14

PROJECT NO. 22330D
SHEET NO. CJ-M15W14-PR-A20-000112 R1
도면번호
REVISION
1A

ITEM NO.		W14-T-4228 B	
SERVICE		CIF MBR 2'nd ANOXIC TANK 2	
Q'TY		1	
TYPE		RECTANGULAR	
SIZE	W x L x H m	5.35 x 5.275 x 11.0 (EH 9.1)	
CAPA.	m3	(310.4 (EH 257))	
HRT	hr	1A 0.4	
MAT'L		P.C + FRP	


200A-WA-FR1-N-4619

200A-WA-FR1-N-4633

FROM CIF MBR TANK
W14-T-4230 A

ODOR




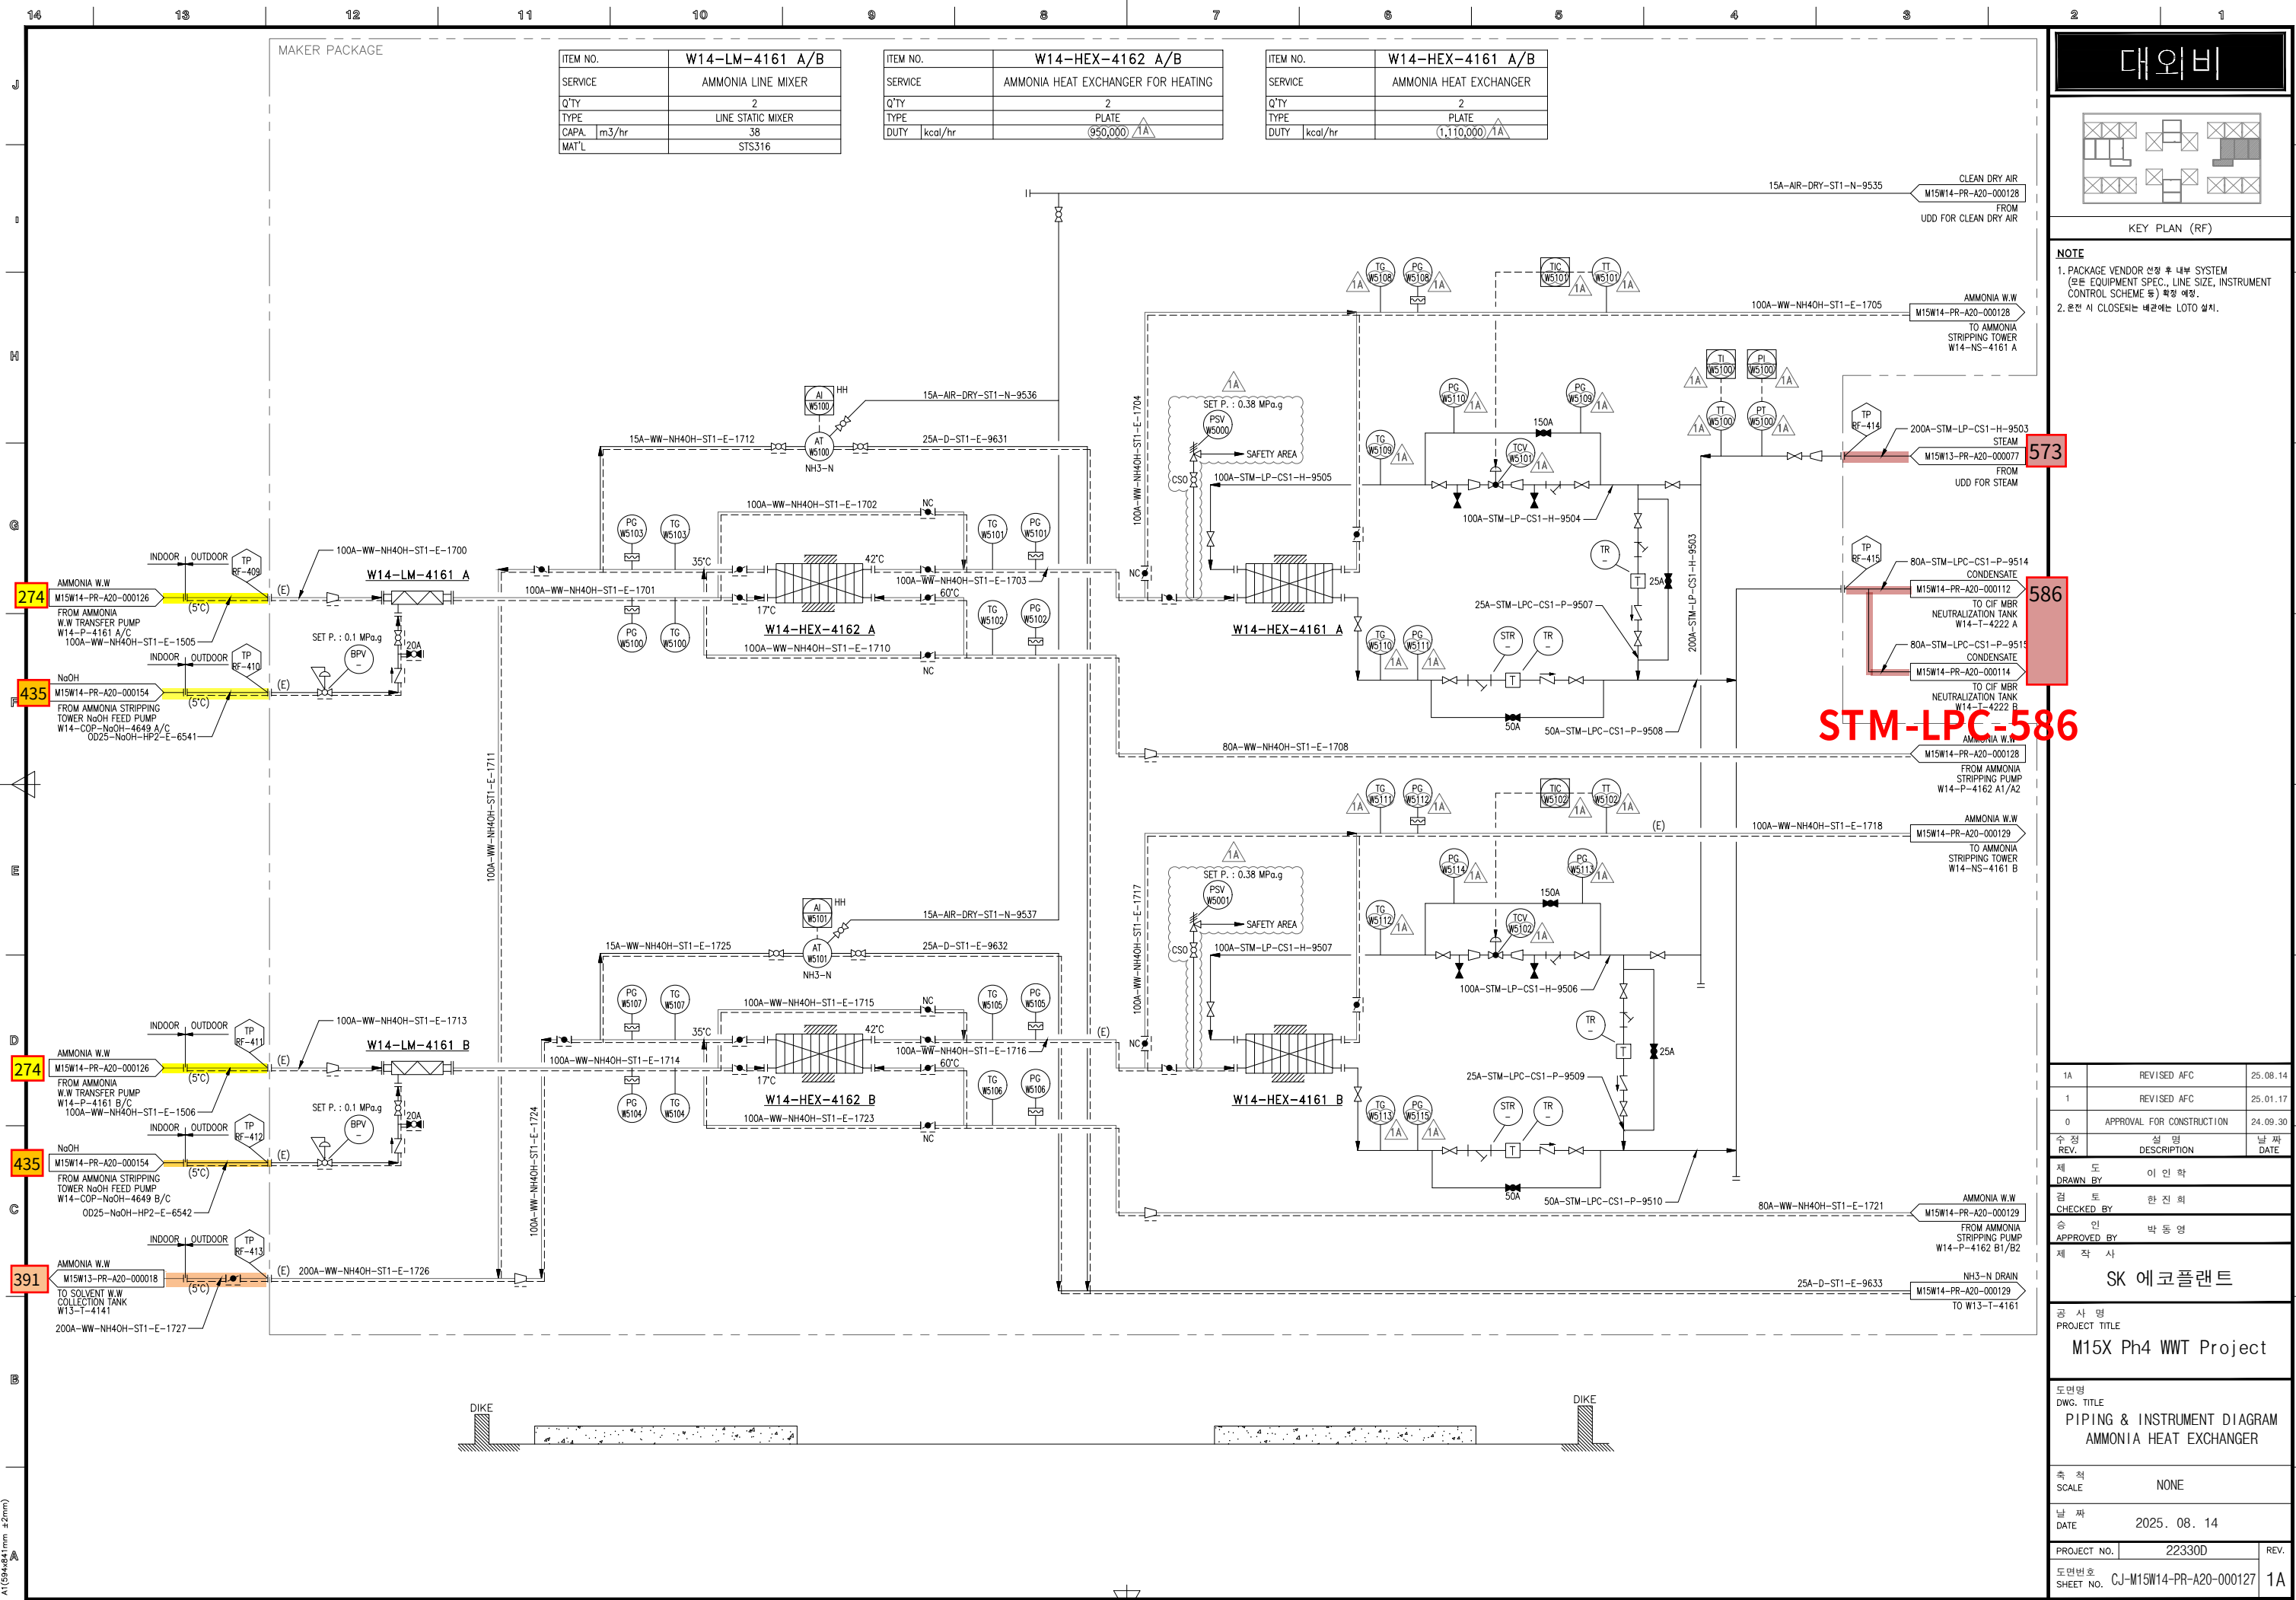





CONTRACTOR		PROJECT NAME	
		M15X Ph4 Project	
COMMODITY		JOB NO.	
STM-LPC		22330D	
LINE NO.	80A-STM-LPC-CS1-P-9514	SH'T NO. 01 / 01	REV. 0

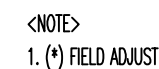

INSULATION	CODE	P	CONDITION	PRESS. (kg/cm2g)	TEMP. (°C)	AREA W14						
	THICK.	40	DESIGN	9.8	198	UNIT 5FA						
			OPERATING	7	170	REF. PLAN DWG. CJ-M15W14-PI-A30-050008-A						
						REF. P & ID CJ-M15W14-PR-A20-000127		25.01.24	APPROVED FOR CONSTRUCTION	황래중	안남후	박동
							REV. NO.	DATE	DESCRIPTION	BY	CHK	APP

[illegible]

<NOTE>

1. (*) FIELD ADJUST

3

* PIPE : P/P1	* 90° ELBOW : E90	* 45° ELBOW : E45	* TEE : T	* RED.TEE : TR	* STUB-IN : STU	* REINFORCING PAD : RP	* CON.RED : RC	* ECC.RED : RE	* CON.SWAGE : RCS/RCS1	* ECC.SWAGE : RES/RES1	* NIPPLE : NP/NP1/NP2	* CAP : CAP/CAP1	* PLUG : PLG	* FULL COUPLING : FC	* HALF COUPLING : HF/HF1
* STUB-IN : STU	* SOCKET(HDPE/PVC) : SC	* SADDLE(HDPE) : SD	* FLANGE : F/F1	* GASKET : G/G1/G2	* BOLT & NUT : B/B1	* BLIND FLANGE : FB/FB1	* GATE VA. : VG/VG1/VG2	* BALL VA. : VB/VB1/VB10/VB2/VB210	* BUTTERFLY VA. : VF/VF4	* CHECK VA. : VC/VC1/VC2/VC3/VC4/VC5/VC6/VC7					
* GLOBE VA. : VL/VL1/VL2	* DIAPHRAGM VA. : VD/VD10	* DAMPER : VP	* QUICK COUPLING : SQC	* FLEXIBLE JOINT(STEEL) : FLXB	* FLEXIBLE JOINT(RUBBER) : FLXR	* FLEXIBLE JOINT(STEEL PTFE LINED) : FLXL	* FLEXIBLE HOSE : FLXH	* STEAM TRAP : ST	* SPRAY NOZZLE : SPN	* EMERGENCY SHOWER : SSH					
* STRAINER(Y-TYPE) : YSTR	* STRAINER(T-TYPE) : TSTR	* STRAINER(BUCKET-TYPE) : BSTR	* ANCHOR PLATE : STOP	* BIRD SCREEN : BS	* ISOLATION KIT : IK	* UNLOADING BOX : UB	* AIR TRAP : AT	* LOTO : LOTO	* SIGHT GLASS : SG	* PRESSURE GAUGE : PG	* SHILED : SH	* SPECIAL BOLT & NUT : BL/BL1			

INSULATION	CODE	P	CONDITION	PRESS. (kg/cm2g)	TEMP. (°C)	AREA W14						CONTRACTOR		PROJECT NAME		
	THICK.	40	DESIGN	9.8	198	UNIT RFA								M15X Ph4 Project		
			OPERATING	7	170	REF. PLAN DWG. CJ-M15W14-PI-A30-R10008-A						COMMODITY STM-LPC		JOB NO.		
								25.01.24	APPROVED FOR CONSTRUCTION	황래중	안남후	박동영	22330D			
						REF. P & ID CJ-M15W14-PR-A20-000127	REV. NO.	DATE	DESCRIPTION	BY	CHK	APP'D	LINE NO.	80A-STM-LPC-CS1-P-9514	SH'T NO. 01 / 01	REV. 0

경고 : 본 도면은 SK HYNIX의 기업비밀 자료로서, 어떠한 경우에도 목적 외 사용, 복제, 제3자에게 공개, 누설 및 유출될 수 없으며, 회사는 유포자의 불법 사용으로 피해가 발생할 경우 유포자에게 민/형사상 책임을 요구할 수 있음