

DRAWING LIST FOR TEST PACKAGE

PROJECT NO.: 22328D

PROJECT TITLE : M15X Ph2 Project

CAOH2-588

No	PKG No	UNIT	LINE NUMBER			P&ID		REMARK
			ISO DRAWING No	SHEET	REV	P&ID No	REV	
1	588	3FA	80A-CAOH2-ST3-N-6546-01	1 OF 1	1	CJ-M15W14-PR-A20-000143	2A	
2	588	3FA	80A-CAOH2-ST3-N-6552-01	1 OF 1	1	CJ-M15W14-PR-A20-000143	2A	

ITEM NO.	W14-T-CAOH2-4601 C	
SERVICE	Ca(OH)2 STORAGE TANK	
Q'TY	1	
TYPE	VERTICAL & CYLINDRICAL	
SIZE	ID x H	3.6 x 5.0 (EH(4.2) / 2A)
CAPA	m3	51 (EH(4.3) / 2A)
MAT'L	C.S + EPOXY	

ITEM NO.	W14-AG-4601 C	
SERVICE	Ca(OH)2 STORAGE TANK AGITATOR	
Q'TY	1	
TYPE	SAW PITCHED PADDLE	
CAPA	rpm	(9.9) / 2A
MAT'L	STS304/STS304	
POWER	kW	(5.5) / 2A

ITEM NO.	W14-CDP-CAOH2-4602 A/B	
SERVICE	Ca(OH)2 FEED PUMP	
Q'TY	1 + 1	
TYPE	ROTARY LOBE (WVF)	
CAPA	m3/h.ea x MPa	28 x 0.7
MAT'L	(NBR/GC250/SCM440)	
POWER	kW	(15) / 2A

대외비

KEY PLAN (3F)

NOTE

1. CaOH2 배관의 ELBOW 부분은 FLANGE 설치할 것.

2. 2m 이상 높은 곳에 설치된 밸브는 CHAIN VALVE 또는 PLATFORM 구성할 것.

3. CHEMICAL UNLOADING STATION에서 LEVEL을 볼 수 있도록 한다.

4. P&ID에 표기된 모든 ELECTRIC POWER는 VENDOR PRINT 참조 후 작성할 것.

5. 소석회 TANK 내 4개의 BAFFLE PLATE를 설치할 것 2A

6. 약품종류에 따라 LINE 색상을 구분하여야 한다.

7. 운전 시 CLOSE 되는 배관에는 LOTO 설치.

8. AGITATOR MAT'L 표기 : SHAFT/BLADE

9. CHEMICAL STORAGE TANK CURB 및 PUMP AREA에서 발생되는 DRAIN은 인근의 TRENCH로 배수되어야, DRAIN HEADER로 이동한다.

10. INTERLOCK NO. I-4611 (W14-CDP-CAOH2-4602 A/B AUTO STOP) : REMOTE STATUS에서 W14-T-CAOH2-4601 C LEVEL (LI-W6052C) LOW LOW STOP.

11. RING MAIN LINE SCHEMATIC.

SCHMATIC DRAWING

12. 7개 VENDOR LOOSE PART 공급.


13. INTERNAL PSV 설치 할 것.

14. 소석회 주입 펌프 AREA에는 비산 방지막을 설치한다.

15. INTERNAL PSV SET PRESSURE : 0.8 Mpaq 1A


2A	REVISED AFC	25.08.14
2	REVISED AFC	25.01.17
1	REVISED AFC	24.10.31
정	실	날
정	명	짜
EV.	DESCRIPTION	DATE
제	도	이
인	인	학
DRAWN BY	이 인 학	
검	한	회
TO	진	
CHECKED BY	회	
수	인	
인	박	
APPROVED BY	동	
제	작	
사	사	
SK 에코플랜트		
공 사 명		
PROJECT TITLE		
M15X Ph4 WWT Project		
도면명		
DWG. TITLE		
PIPING & INSTRUMENT DIAGRAM		
Ca(OH)2 STORAGE TANK & FEED PUMP (2/2)		
속		
SCALE		
NONE		
날		
DATE		
2025. 08. 14		
PROJECT NO.		22330D
도면번호		
SHEET NO.		CJ-M15W14-PR-A20-000143
		2A

CAOH2-588

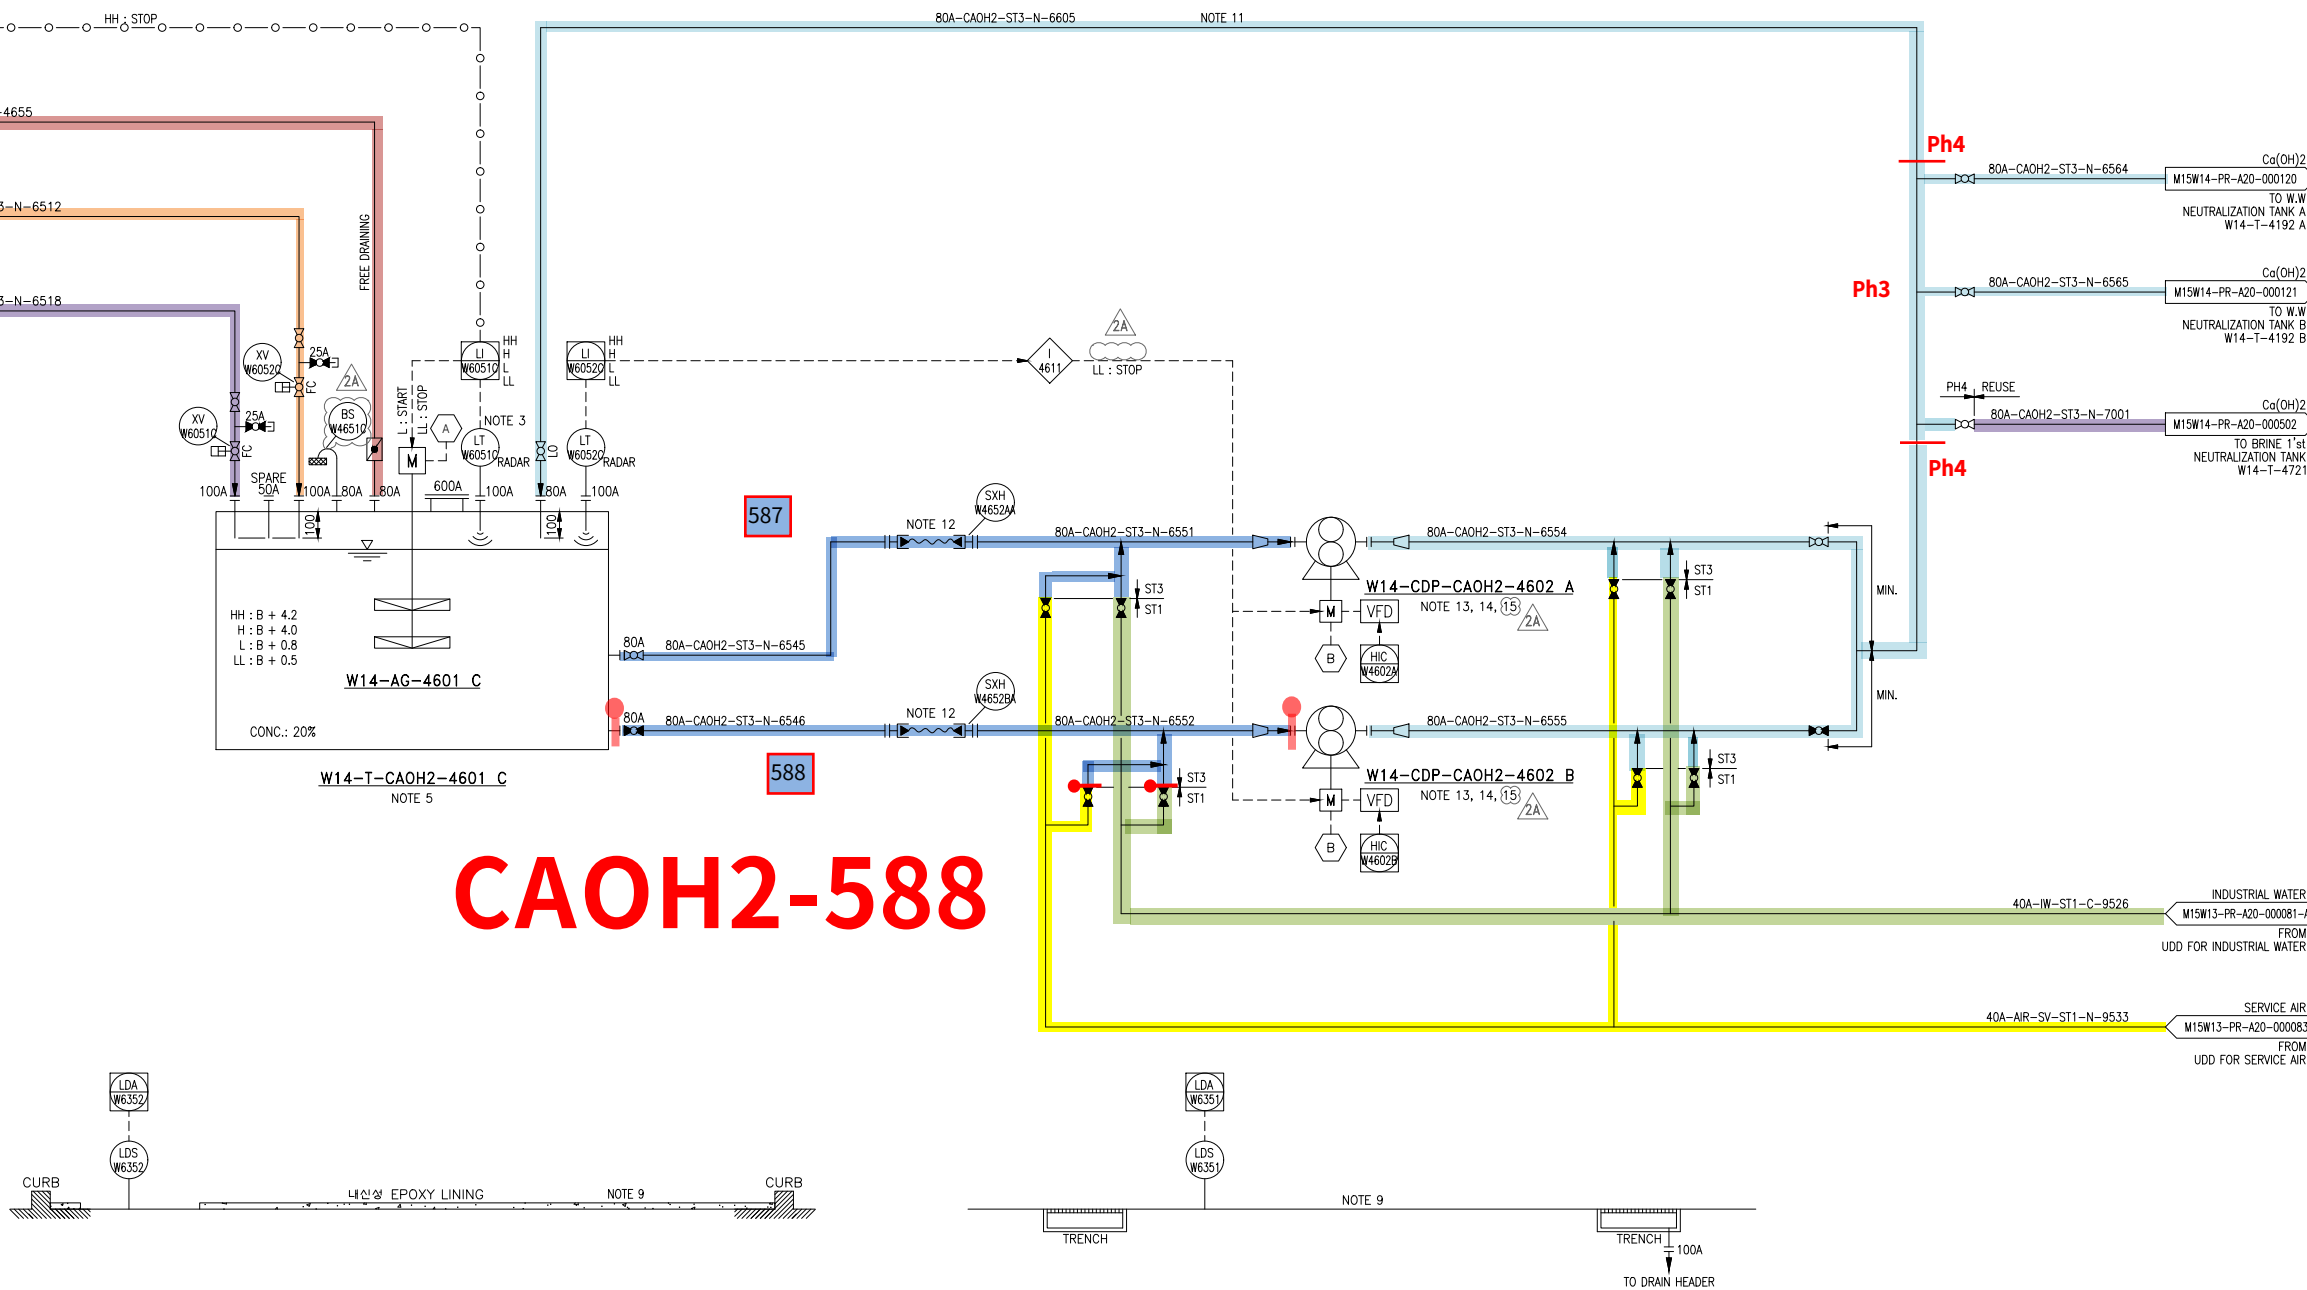



ITEM	SIZE	Q'TY	DESCRIPTION
ST3			
P	80A	1.9M	PIPE, STS 304TP, ERW, BE – SCH 10S
F	80A	2EA	FLG SO, KS 10K, RF, STS304
G	80A	2EA	GASKET, KS 10K, RF, PTFE+EPDM, 3.0MM TH'K
B	80A	2SET	MACHINE BOLT & NUTS :STS 304 / W WASHERS
SH	80A	3EA	SHIELD
VB	80A	1EA	BALL VALVE, KS 10K, RF FLG'D, BODY-SSC13 /
			TRIM-ST3304 / SEAT-PTFE, FB, LEVER
LOTO	80A	1EA	LOTO

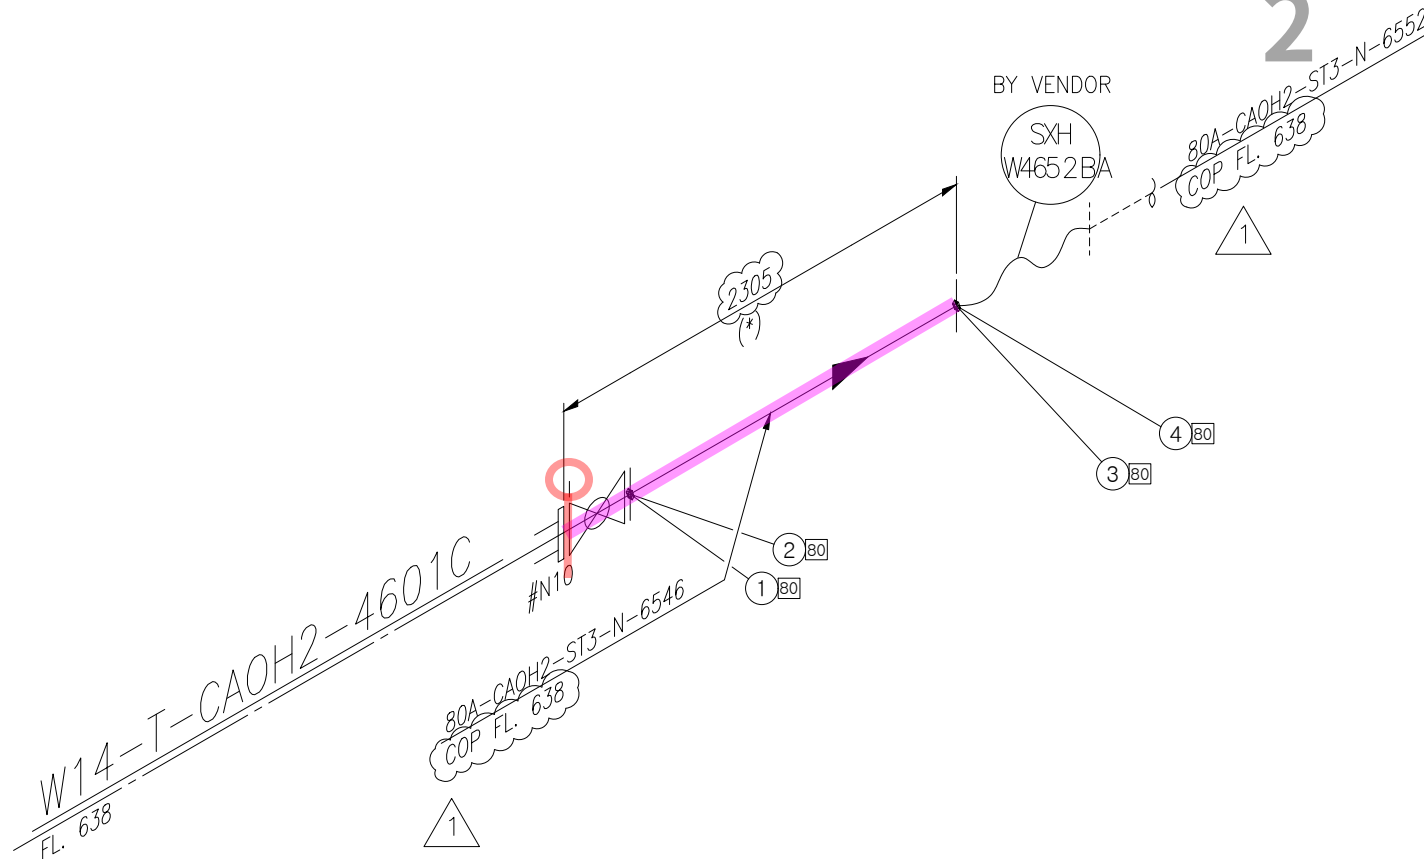

<NOTE>

1. (*) FIELD ADJUST

* PIPE : P/P1	* 90° ELBOW : E90	* 45° ELBOW : E45	* TEE : T	* RED.TEE : TR	* STUB-IN : STU	* REINFORCING PAD : RP	* CON.RED : RC	* ECC.RED : RE	* CON.SWAGE : RCS/RCS1	* ECC.SWAGE : RES/RES1	* NIPPLE : NP/NP1/NP2	* CAP : CAP/CAP1	* PLUG : PLG	* FULL COUPLING : FC	* HALF COUPLING : HF/HF1
* STUB-IN : STU	* SOCKET(HDPE/PVC) : SC	* SADDLE(HDPE) : SD	* FLANGE : F/F1	* GASKET : G/G1/G2	* BOLT & NUT : B/B1	* BLIND FLANGE : FB/FB1	* GATE VA. : VG/VG1/VG2	* BALL VA. : VB/VB1/VB10/VB2/VB210	* BUTTERFLY VA. : VF/VF4	* CHECK VA. : VC/VC1/VC2/VC3/VC4/VC5/VC6/VC7					
* GLOBE VA. : VL/VL1/VL2	* DIAPHRAGM VA. : VD/VD10	* DAMPER : VP	* QUICK COUPLING : SQC	* FLEXIBLE JOINT(STEEL) : FLXB	* FLEXIBLE JOINT(RUBBER) : FLXR	* FLEXIBLE JOINT(STEEL PTFE LINED) : FLXL	* FLEXIBLE HOSE : FLXH	* STEAM TRAP : ST	* SPRAY NOZZLE : SPN	* EMERGENCY SHOWER : SSH					
* STRAINER(Y-TYPE) : YSTR	* STRAINER(T-TYPE) : TSTR	* STRAINER(BUCKET-TYPE) : BSTR	* ANCHOR PLATE : STOP	* BIRD SCREEN : BS	* ISOLATION KIT : IK	* UNLOADING BOX : UB	* AIR TRAP : AT	* LOTO : LOTO	* SIGHT GLASS : SG	* PRESSURE GAUGE : PG	* SHILED : SH	* SPECIAL BOLT & NUT : BL/BL1			

INSULATION	CODE	N	CONDITION	PRESS. (kg/cm2g)	TEMP. (°C)	AREA W14								CONTRACTOR		PROJECT NAME	
	THICK.	—	DESIGN	1.0	60	UNIT 3FA								M15X Ph4 Project			
			OPERATING	ATM	AMB	REF. PLAN DWG. CJ-M15W14-PI-A30-030008-A		25.03.31	REVISED AS MARKED	황래중	안남후	박동영	COMMODITY	CAOH2	JOB NO.		
						REF. P & ID CJ-M15W14-PR-A20-000143		25.01.24	APPROVED FOR CONSTRUCTION	황래중	안남후	박동영	22330D				
							REV. NO.	DATE	DESCRIPTION	BY	CHK	APP'D	LINE NO.	80A-CAOH2-ST3-N-6546	SH'T NO. 01 / 01	REV. 1	

경고 : 본 회장의 임의 또는 SK HYNIX의 기밀 자료를로서, 어떠한 경우에도 본 회장의 허락 없이 제3자에게 공개, 누설, 복제, 배포, 대여, 전수, 또는 기타 방법으로 외부에 유출, 공개, 누설, 또는 기타 방법으로 제3자에게 제공되는 것을 금지하며, 위법행위 시 민/형사상 책임을 지고 고발할 수 있다.



1. (*) FIELD ADJUST

CLIENT



2

CONTRACTOR 