


MBW-590

1 OF 1

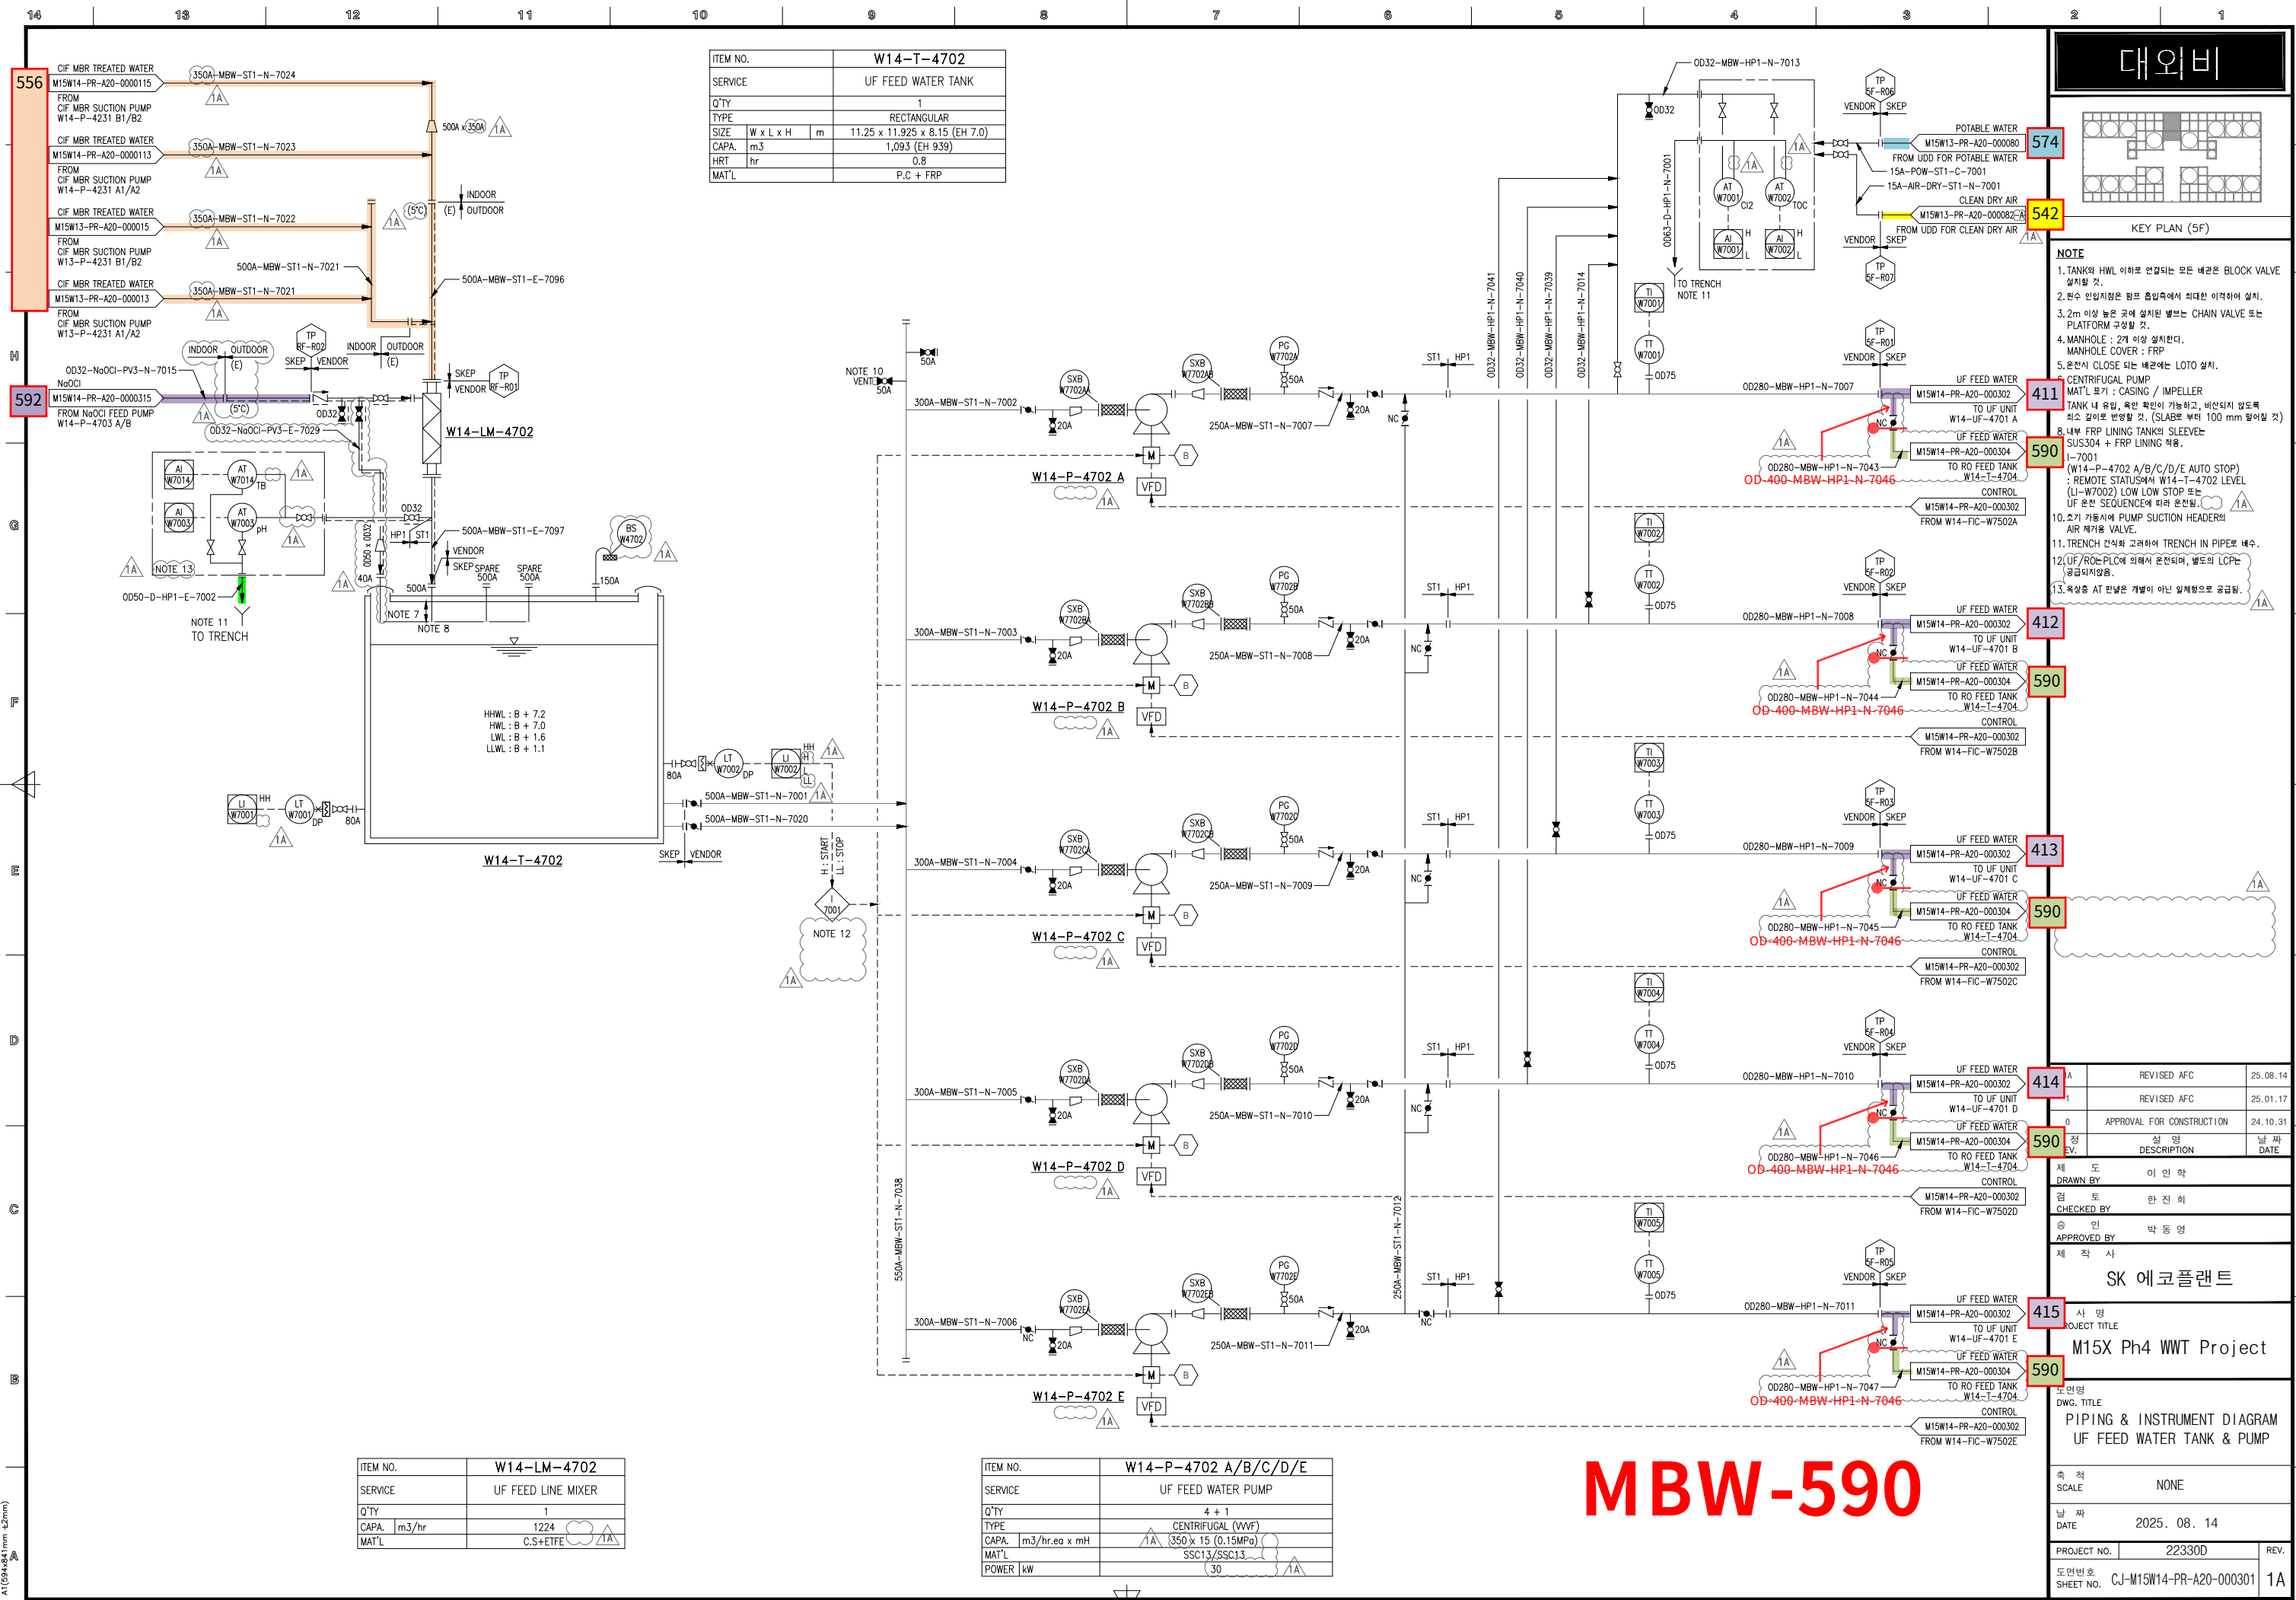

ITEM NO.	W14-T-4702
SERVICE	UF FEED WATER TANK
Q'TY	1
TYPE	RECTANGULAR
SIZE	W x L x H m 11.25 x 11.925 x 8.15 (EH 7.0)
CAPA.	m3 1,093 (EH 939)
HRT	hr 0.8
MAT'L	P.C + FRP

ITEM NO.	W14-LM-4702
SERVICE	UF FEED LINE MIXER
Q'TY	1
CAPA.	m3/hr 1224
MAT'L	C.S+ETFE

ITEM NO.	W14-P-4702 A/B/C/D/E
SERVICE	UF FEED WATER PUMP
Q'TY	4 + 1
TYPE	CENTRIFUGAL (VVF)
CAPA.	m3/hr.ea x mH 1A (350 x 15 (0.15MPa))
MAT'L	SSC13/SSC13
POWER	kW 30


대외비


KEY PLAN (5F)

NOTE
1. TANK의 HWL 이하로 연결되는 모든 배관은 BLOCK VALVE 설치할 것.
2. 환수 인입지점은 펌프 흡입측에서 최대한 이격하여 설치.
3. 2m 이상 높은 곳에 설치된 밸브는 CHAIN VALVE 또는 PLATFORM 구성할 것.
4. MANHOLE : 2개 이상 설치한다.
5. 온전시 CLOSE 되는 배관에는 LOTO 설치.
CENTRIFUGAL PUMP
MAT'L 표기 : CASING / IMPELLER
TANK 내 유입, 유출 확인 가능하고, 비산되지 않도록 최소 길이로 변경할 것. (SLAB로부터 100 mm 떨어질 것)
8. FRP LINING TANK의 SLEEVE는 SUS304 + FRP LINING 적용.
9. W14-P-4702 A/B/C/D/E AUTO STOP : REMOTE STATUS에서 W14-T-4702 LEVEL (L-W7002) LOW STOP 또는 UF 온전 SEQUENCE에 따라 온전됨.
10. 초기 가동시에 PUMP SUCTION HEADER의 AIR 제거용 VALVE.
11. TRENCH 잔여물 고려하여 TRENCH IN PIPE로 배수.
12. UF/ROE PLC에 의해서 온전되며, 별도의 LCP는 공급되지 않음.
13. 옥상층 AT 핀날은 개별이 아닌 일체형으로 공급됨.

411	REVISED AFC	25.08.14
590	REVISED AFC	25.01.17
412	APPROVAL FOR CONSTRUCTION	24.10.31
590	실명	날짜
413	DESCRIPTION	DATE
414	제 도	이 인 학
590	검 토	한 진 희
415	승 인	박 동 영
590	제 작 사	
SK 에코플랜트		
사 명		
PROJECT TITLE		
M15X Ph4 WWT Project		
도면명		
DWG. TITLE		
PIPING & INSTRUMENT DIAGRAM		
UF FEED WATER TANK & PUMP		
속 측		
SCALE		
NONE		
날 짜		
DATE		
2025. 08. 14		
PROJECT NO.		
22330D		
REV.		
도면번호		
SHEET NO.		
CJ-M15W14-PR-A20-000301		
1A		

MBW-590

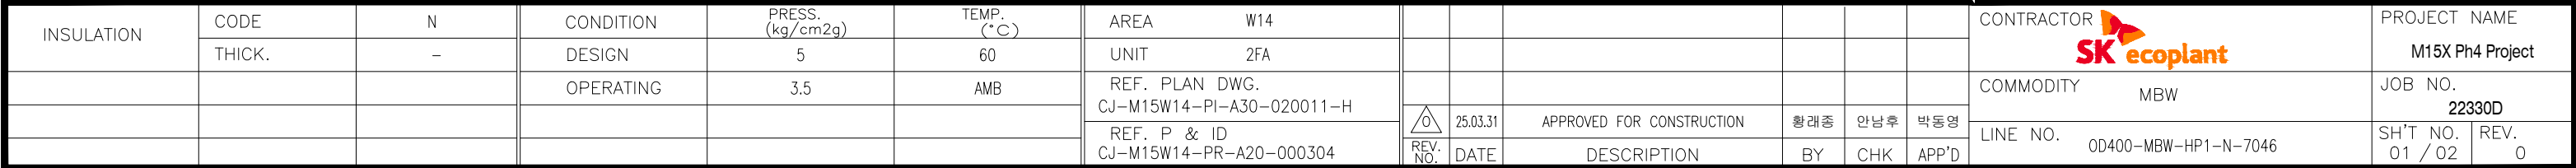

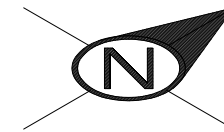


1. TRAY & ANGLE, CHANNEL SUPPORT가 적용되는 배관 ELEVATION은 현장 맞춤으로 한다.
2. (*) FIELD ADJUST



2

CONTRACTOR 

경고 : 본 문헌은 SK HYNIX의 기밀비밀 자료로서, 어떠한 경우에도 무단으로 복제, 제3자에게 공개, 누설 또는 기타 방법으로 유출되어서는 안 됩니다. 이 회사는 모든 포자의 사용에 동의함으로써 그 권리를 포기하고, 발생할 경우 유권자에게 미/항사상 재판을 청구할 수 있는 권한을 잃습니다.

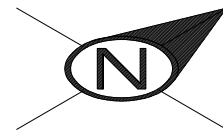

1. (*) FIELD ADJUST
2. TRAY & ANGLE, CHANNEL SUPPORT가 적용되는
배관 ELEVATION은 현장 맞춤으로 한다.

CLIENT



5

정고 : 고 인 의 이 SK HYNIX의 기 어비밀 자로로서, 어떠한 중우에 도 목적 외 사용, 복제, 제3자에게 공개, 누설 및 기타 무단으로 사용되거나 유출될 경우, 회사나 본포자의 명의로 허락받지 않은 상태에서 사용되거나 유출될 경우, 본회에게 발생하한 손해액에 상응하는 금액을 지급할 것을 약한다.