


DRAWING LIST FOR TEST PACKAGE

PROJECT NO.: 22328D


PROJECT TITLE : M15X Ph2 Project

TW-ST1-591

No	PKG No	UNIT	LINE NUMBER			P&ID		REMARK
			ISO DRAWING No	SHEET	REV	P&ID No	REV	
1	591	1FA	400A-TW-ST1-N-7010-01	1 OF 1	1	CJ-M15W14-PR-A20-000305	1A	
2	591	2FA	250A-TW-ST1-E-7048-01	1 OF 1	0	CJ-M15W14-PR-A20-000313	1A	
3	591	2FA	400A-TW-ST1-E-7010-01	1 OF 1	1	CJ-M15W14-PR-A20-000304	1A	

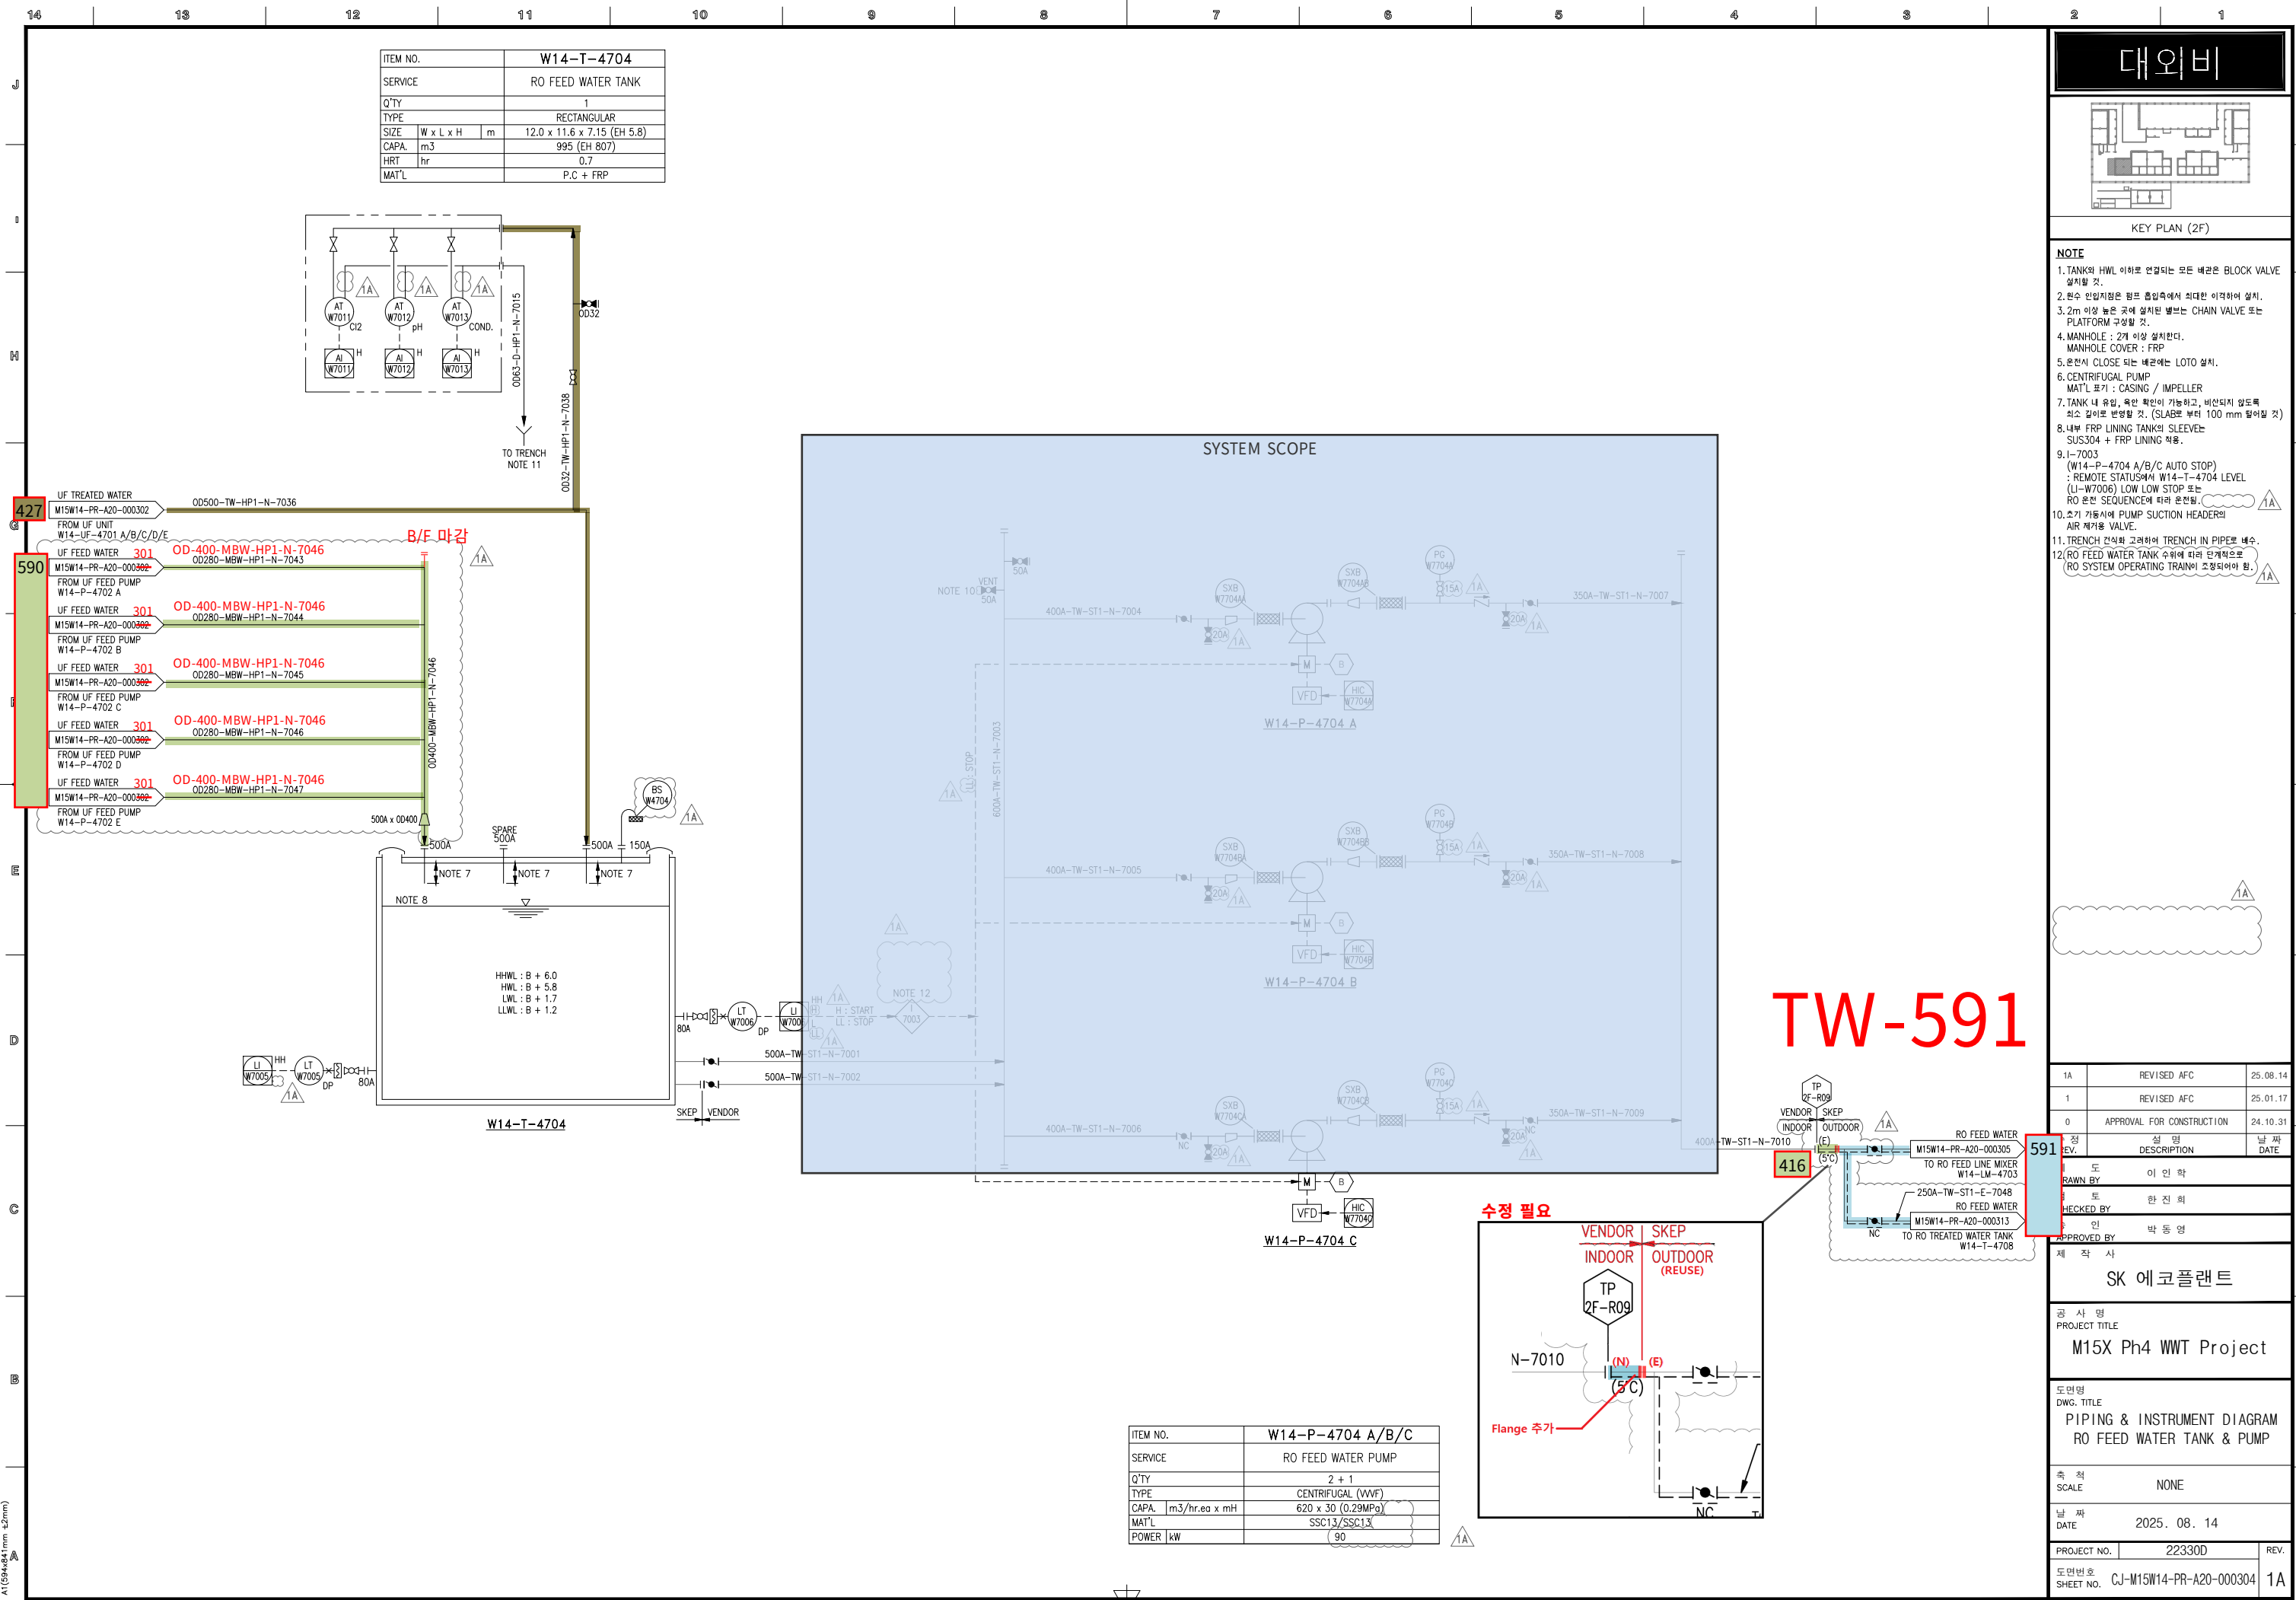

대외비

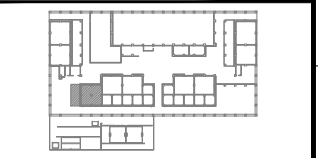

KEY PLAN (2F)

- NOTE**
1. TANK의 HWL 이하로 연결되는 모든 배관은 BLOCK VALVE 설치할 것.
 2. 환수 인입지점은 환로 흡입측에서 최대한 이격하여 설치.
 3. 2m 이상 높은 곳에 설치된 밸브는 CHAIN VALVE 또는 PLATFORM 구성할 것.
 4. MANHOLE : 2개 이상 설치한다.
MANHOLE COVER : FRP
 5. 콘센트 CLOSE 되는 배관에는 LOTO 설치.
 6. CENTRIFUGAL PUMP
MAT'L 표기 : CASING / IMPELLER
 7. TANK 내 유입, 육안 확인이 가능하고, 비산되지 않도록 최소 길이로 반영할 것. (SLAB로부터 100 mm 떨어질 것)
 8. 내부 FRP LINING TANK의 SLEEVE는 SUS304 + FRP LINING 적용.
 9. 1-7003
(W14-P-4704 A/B/C AUTO STOP)
: REMOTE STATUS에 W14-T-4704 LEVEL (LI-W7005) LOW LOW STOP 또는 RO 운전 SEQUENCE에 따라 운전됨.
 10. 소기 가동시에 PUMP SUCTION HEADER의 AIR 제거용 VALVE.
 11. TRENCH 잔식화 고려하여 TRENCH IN PIPE로 배수.
 12. RO FEED WATER TANK 수위에 따라 단계적으로 RO SYSTEM OPERATING TRAIN에 조정되어야 함.

1A	REVISED AFC	25.08.14
1	REVISED AFC	25.01.17
0	APPROVAL FOR CONSTRUCTION	24.10.31

정	실	날
EV.	영	짜
	DESCRIPTION	DATE

인 박동영

제 작 사

SK 에코플랜트

공 사 명
PROJECT TITLE
M15X Ph4 WWT Project

도면명
DWG. TITLE
PIPING & INSTRUMENT DIAGRAM
RO FEED WATER TANK & PUMP

속 척
SCALE
NONE


날 짜
DATE
2025. 08. 14

PROJECT NO. 22330D


도면번호
SHEET NO. CJ-M15W14-PR-A20-000304

REV. 1A

TW-591

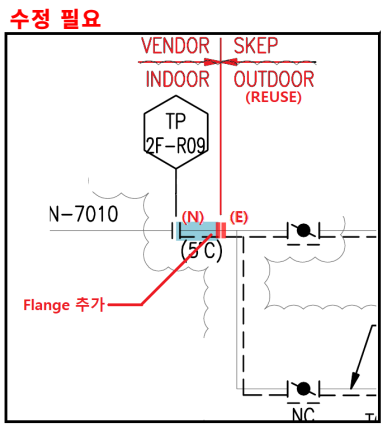

ITEM NO.	W14-P-4704 A/B/C
SERVICE	RO FEED WATER PUMP
Q'TY	2 + 1
TYPE	CENTRIFUGAL (WVF)
CAPA.	620 x 30 (0.29MPa)
MAT'L	SSC13/SSC13
POWER kW	90

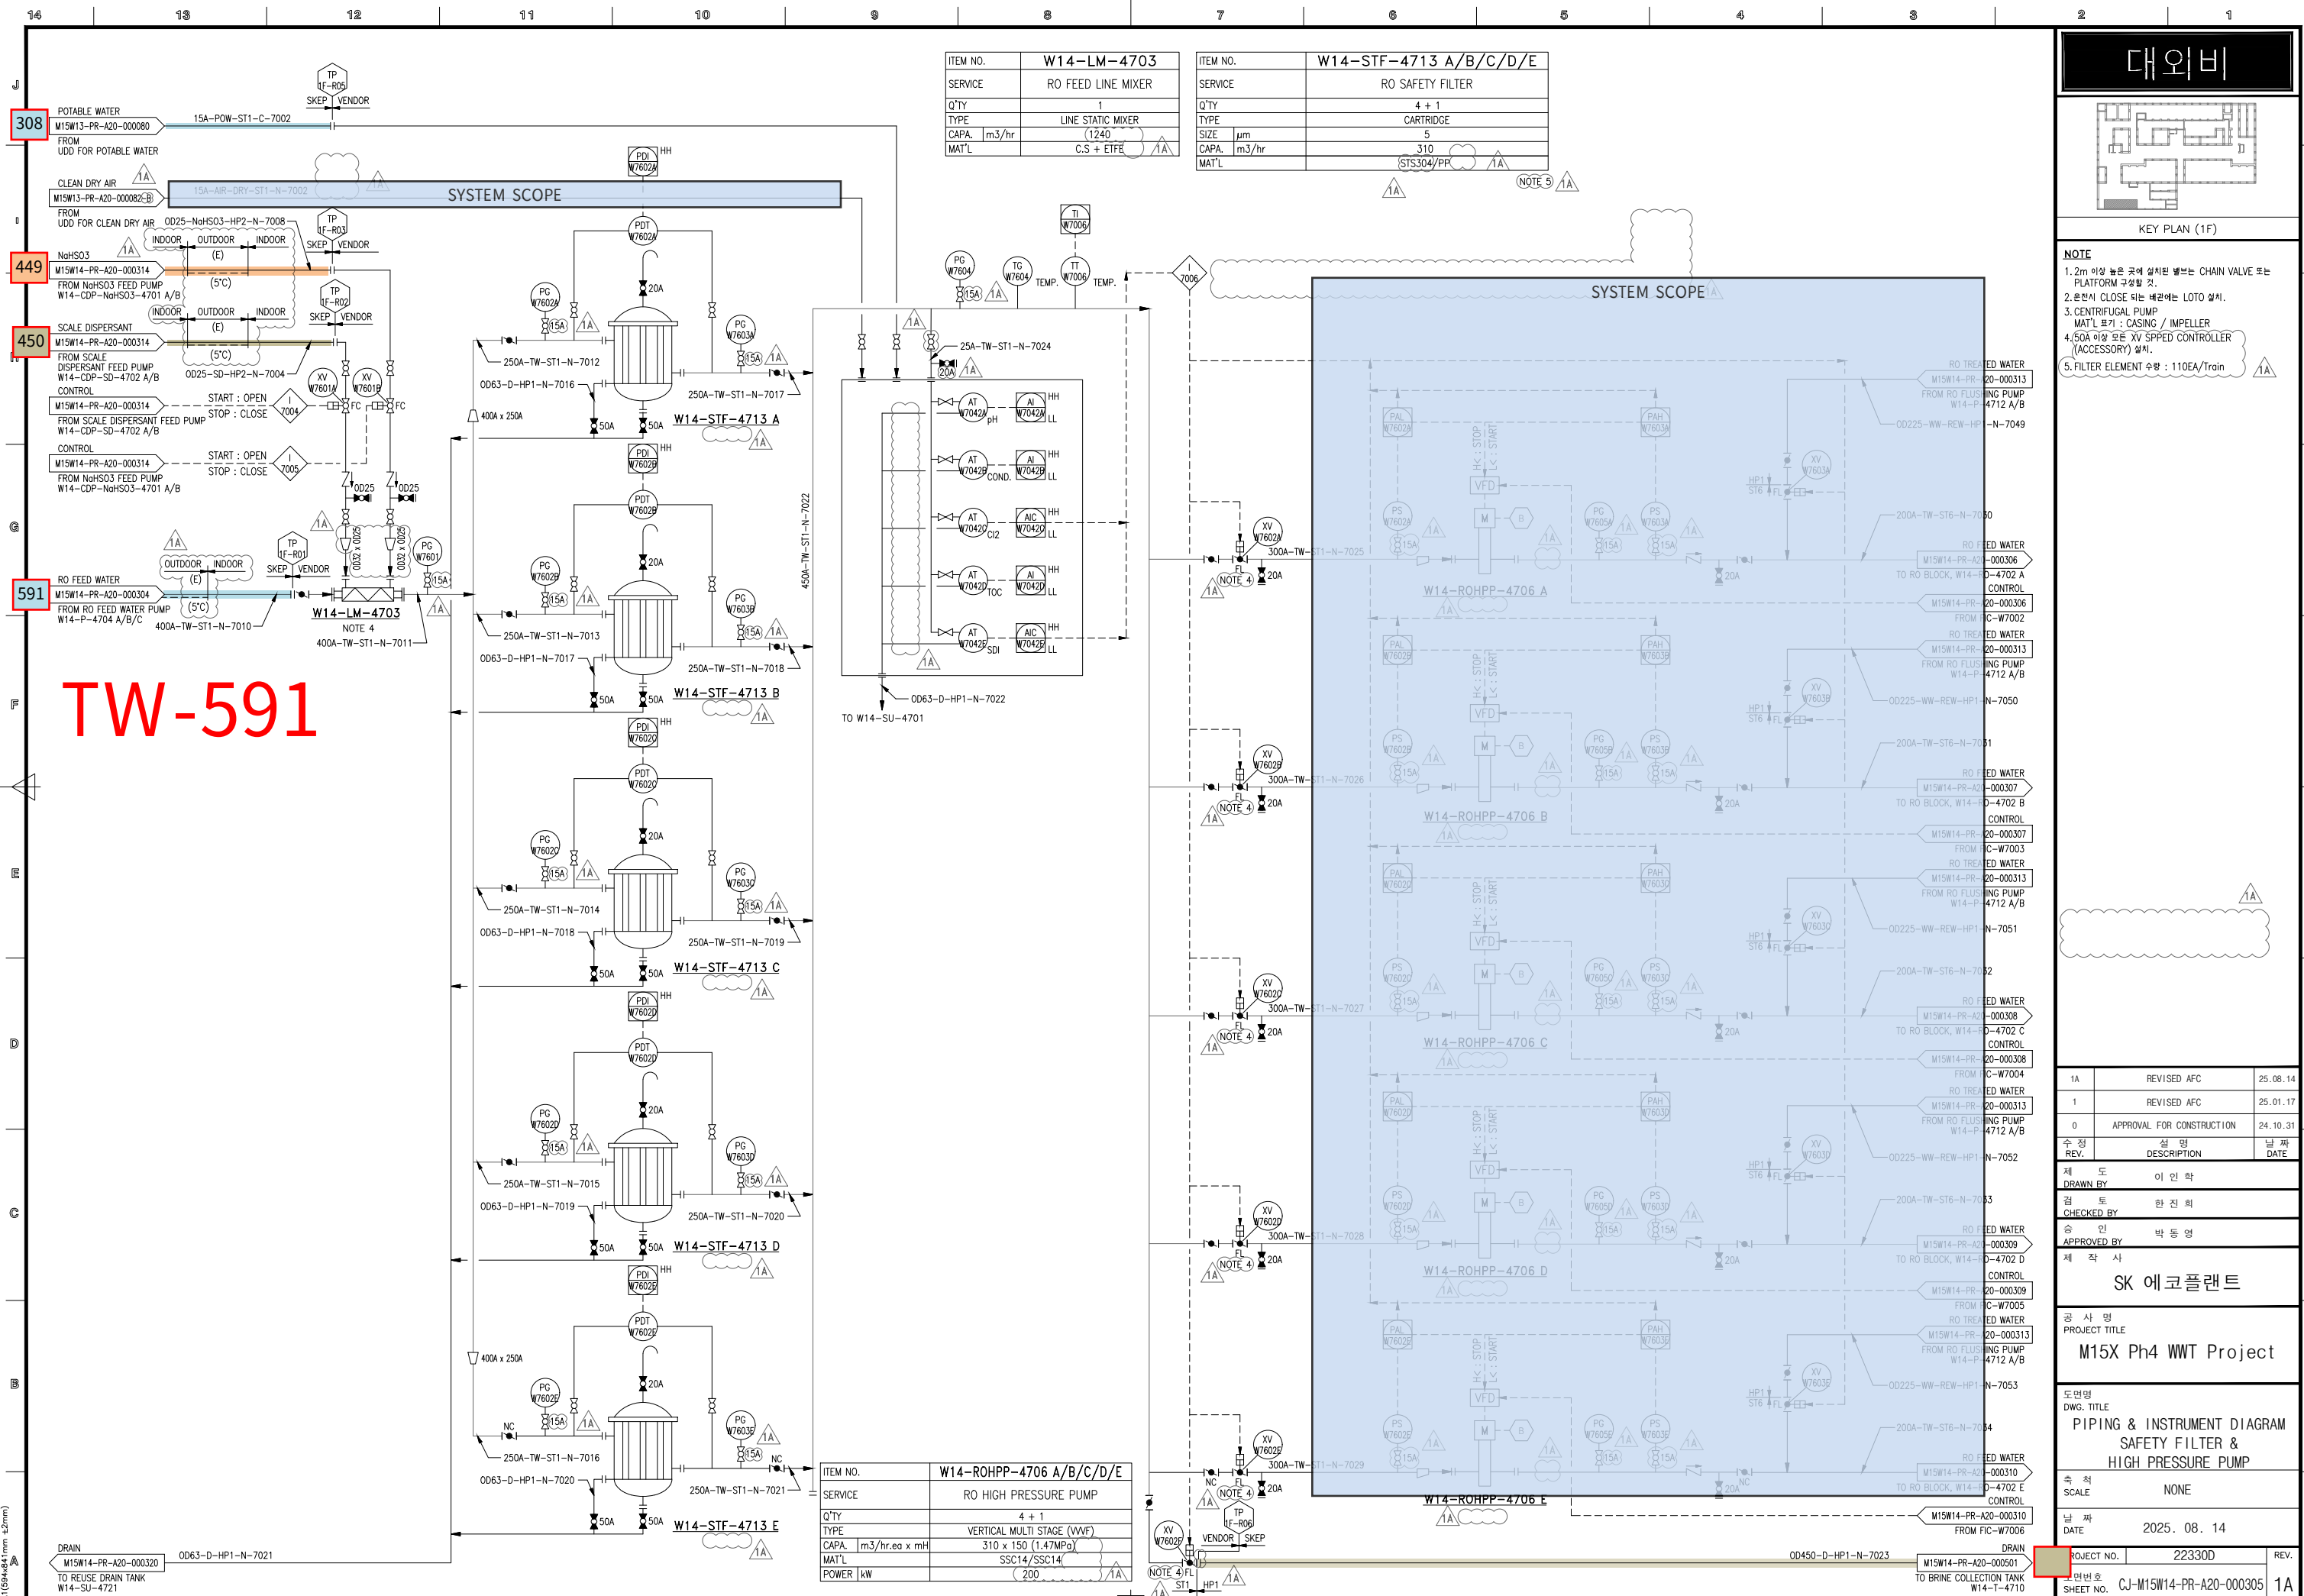

대외비

KEY PLAN (1F)

NOTE

1. 2m 이상 높은 곳에 설치된 밸브는 CHAIN VALVE 또는 PLATFORM 구성할 것.

2. 콘센트 CLOSE 되는 배관에는 LOTO 설치.

3. CENTRIFUGAL PUMP MAT'L 표기 : CASING / IMPELLER


4. 50A 이상 모든 XV SPED CONTROLLER (ACCESSORY) 설치.

5. FILTER ELEMENT 수명 : 110EA/Train

1A	REVISED AFC	25.08.14
1	REVISED AFC	25.01.17
0	APPROVAL FOR CONSTRUCTION	24.10.31
수정 REV.	실명 DESCRIPTION	날짜 DATE
제 도 이 인 학		
DRAWN BY		
검 토 한 진 회		
CHECKED BY		
승 인 박 동 명		
APPROVED BY		
제 작 사		
SK 에코플랜트		
공 사 명 PROJECT TITLE		
M15X Ph4 WWT Project		
도면명 DWG. TITLE		
PIPING & INSTRUMENT DIAGRAM SAFETY FILTER & HIGH PRESSURE PUMP		
속 척 SCALE		
NONE		
날 짜 DATE		
2025. 08. 14		
PROJECT NO.		22330D
REVISION NO.		CJ-M15W14-PR-A20-000305
SHEET NO.		1A

TW-591

#Users\TOP\Desktop\P&ID251013W[M15X Ph-4 for 인허가]CAD FILE_0910W\CJ-M15W14-PR-A20-000313 R1 P&ID FOR REUSE

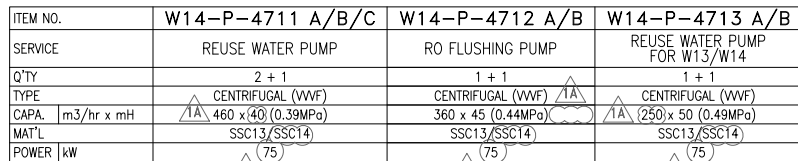

NOTE

1. TANK와 H/WL 이커로 연결되는 모든 배관은 BLOCK VALVE 설치됨.
2. 원천 인입지점은 배관 출구측에 최대 이격여가 설치.
2m 이상 높은 곳에 설치된 밸브는 CHAIN VALVE 또는 PLATFORM 구성됨.
3. MANHOLE : 2개 이상 설치됨.
MANHOLE COVER : FRP
5. 온천진 CLOSE 되는 배관에는 LOTO 설치.
6. CENTRIFUGAL PUMP
MAT' L : CASING / IMPELLER
7. TANK 내 유입, 유출 파이프가 커넥터, 변전지터 압도측 및 길로터 변전지터. (SLABE 보다 100 mm 철판이 갖.)
8. 배관 FRP LINING TANK의 SLEEVE는 SUS304 + FRP LINING 적용.

9. I-7007
(W14-P-4711 A/B/C AUTO STOP)
REMOTE STATUS에서 W14-T-4708 LEVEL (L1-W7008) LOW LOW STOP 또는 RO 온천인 SEQUENCE에 따라 자동정지.
(DETAIL 사항은 후주 VENDOR 선정 이후 확립됨.)

10. I-7008
(W14-P-4713 A/B AUTO STOP)
REMOTE STATUS에서 W14-T-4708 LEVEL (L1-W7008) LOW LOW STOP.

11. I-7016
(W14-P-4712 A/B AUTO STOP)
REMOTE STATUS에서 W14-T-4708 LEVEL (L1-W7008) LOW LOW STOP 또는 RO 온천인 SEQUENCE에 따라 자동정지.
(DETAIL 사항은 후주 VENDOR 선정 이후 확립됨.)

12. 스기 가동시에 PUMP SUCTION HEADER의 AIR 제거용 VALVE.

13. 공급 : VENDOR / 설치 : SKEP

14. UF/RO-PLC에 의해서 온천지터, 별도의 LCP는 공급되지않음.

수 정 REV.	설 명 DESCRIPTION	날 짜 DATE
-------------	--------------------	-------------

제 도 이 인 학

DRAWN BY
검 토 회 지 회

CHECKED BY _____ 안 전 회

승 인 박 동 영
APPROVED BY

제 작 사

SK 에코플랜트

100% 90% 80% 70% 60% 50% 40% 30% 20% 10% 0%

PROJECT TITLE

M15X Ph4 WWT Project

도면명

PIPING & INSTRUMENT DIAGRAM

REFUSE PUMP

TABLE 1 (cont.)

측 척
SCALE NONE

SCALE NONE

날 짜
DATE 2025. 08. 14


PROJECT NO.	22330D	REV.
-------------	--------	------

도면번호 01 M15W14 PD 100 000010 1 A

SHEET NO. CJ-M15W14-PR-A20-000313

20-10 FOR DE

WARRANT FOR RE

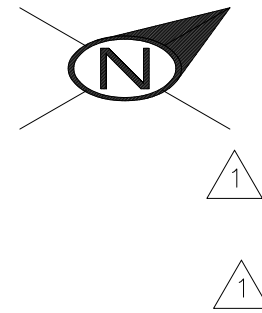[illegible]

CLIENT		1	
			
영	COMMODITY	TW	PROJECT NAME M15X Ph4 Project
영	LINE NO.	400A-TW-ST1-N-7010	JOB NO. 22330D
D			SH'T NO. 01 / 01
			REV. 1

* PIPE : P/P1 * 90° ELBOW : E90 * 45° ELBOW : E45 * TEE : T * RED.TEE : TR * STUB-IN : STU * REINFORCING PAD : RP * CON.RED : RC * ECC.RED : RE * CON.SWAGE : RCS/RCS1 * ECC.SWAGE : RES/RES1 * NIPPLE : NP/NP1/NP2 * CAP : CAP/CAP1 * PLUG : PLG * FULL COUPLING : FC * HALF COUPLING : HF/HF1 * STUB-IN : STU * SOCKET(HDPE/PVC) : SC * SADDLE(HDPE) : SD * FLANGE : F/F1 * GASKET : G/G1/G2 * BOLT & NUT : B/B1 * BLIND FLANGE : FB/FB1 * GATE VA. : VG/VG1/VG2 * BALL VA. : VB/VBLO/VB1/VB1LO/VB2/VB2LO * BUTTERFLY VA. : VF/VF4 * CHECK VA. : VC/VC1/VC2/VC3/VC4/VC5/VC6/VC7 * GLOBE VA. : VL/VL1/VL2 * DIAPHRAGM VA. : VD/VDLO * DAMPER : VP * QUICK COUPLING : SQC * FLEXIBLE JOINT(STEEL) : FLXB * FLEXIBLE JOINT(RUBBER) : FLXR * FLEXIBLE JOINT(STEEL PTFE LINED) : FLXL * FLEXIBLE HOSE : FLXH * STEAM TRAP : ST * SPRAY NOZZLE : SPN * EMERGENCY SHOWER : SSH * STRAINER(Y-TYPE) : YSTR * STRAINER(T-TYPE) : TSTR * STRAINER(BUCKET-TYPE) : BSTR * ANCHOR PLATE : STOP * BIRD SCREEN : BS * ISOLATION KIT : IK * UNLOADING BOX : UB * AIR TRAP : AT * LOTO : LOTO * SIGHT GLASS : SG * PRESSURE GAUGE : PG * SHILED : SH * SPECIAL BOLT & NUT : BL/BL1													
INSULATION	CODE	N	CONDITION	PRESS. (kg/cm2g)	TEMP. (°C)	AREA	W14						
	THICK.	-	DESIGN	6.4	60	UNIT	R1FA						
			OPERATING	4	AMB	REF. PLAN DWG. CJ-M15W14-PI-A30-010017-C			25.03.31	REVISED AS MARKED	황래중	안남후	박동
						REF. P & ID CJ-M15W14-PR-A20-000305			25.01.24	APPROVED FOR CONSTRUCTION	황래중	안남후	박동
								REV. NO.	DATE	DESCRIPTION	BY	CHK	APP

