

DRAWING LIST FOR TEST PACKAGE

PROJECT NO.: 22328D

PROJECT TITLE : M15X Ph2 Project



WW-REW-596

| No | PKG No | UNIT | LINE NUMBER               |        |     | P&ID                    |     | REMARK |
|----|--------|------|---------------------------|--------|-----|-------------------------|-----|--------|
|    |        |      | ISO DRAWING No            | SHEET  | REV | P&ID No                 | REV |        |
| 1  | 596    | 1MF  | 200A-WW-REW-ST1-N-7044-01 | 1 OF 1 | 1   | CJ-M15W14-PR-A20-000313 | 1A  |        |
|    |        |      |                           |        |     |                         |     |        |
|    |        |      |                           |        |     |                         |     |        |
# WW-REW-596

|          |                                          |
|----------|------------------------------------------|
| ITEM NO. | W14-T-4709                               |
| SERVICE  | REUSE EMERGENCY TANK                     |
| Q'TY     | 1                                        |
| TYPE     | RECTANGULAR                              |
| SIZE     | W x L x H   m 8.1 x 3.15 x 7.45 (EH 5.0) |
| CAPA.    | m3 190.1 (EH 127.6)                      |
| MAT'L    | P.C + FRP                                |

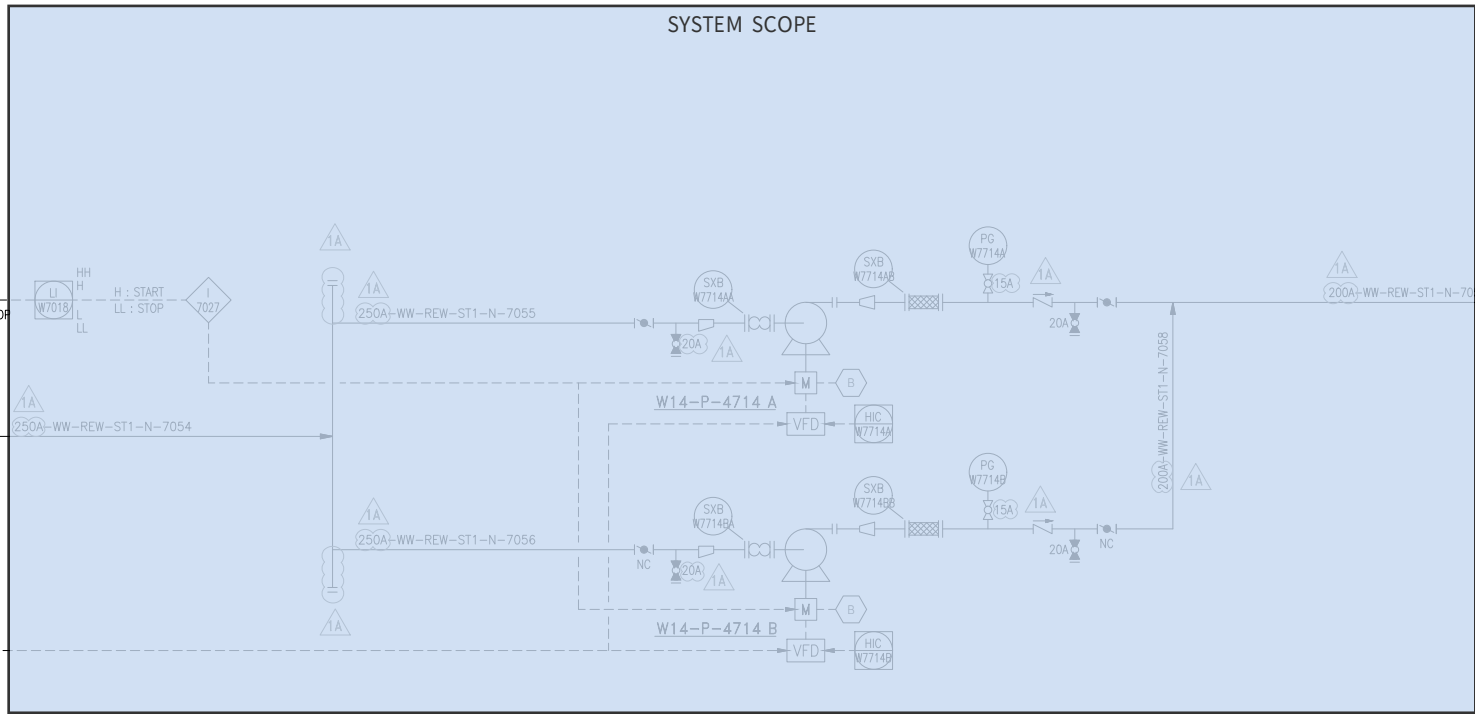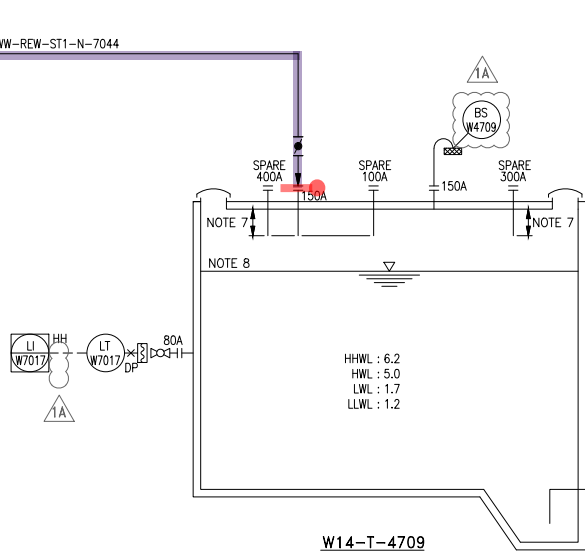

|          |                               |
|----------|-------------------------------|
| ITEM NO. | W14-P-4714 A/B                |
| SERVICE  | REUSE EMERGENCY TANK PUMP     |
| Q'TY     | 1 + 1                         |
| TYPE     | CENTRIFUGAL (WVF)             |
| CAPA.    | m3/hr x mH 250 x 50 (0.49MPa) |
| MAT'L    | SSC13(SSC14)                  |
| POWER    | kw 75                         |

대외비

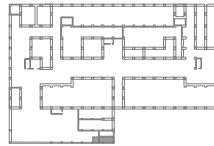

KEY PLAN (1F)

## NOTE

- TANK의 HWL 이하로 연결되는 모든 배관은 BLOCK VALVE 설치할 것.
- 관수 인입지점은 펌프 흡입측에서 최대한 이격하여 설치.
- 2m 이상 높은 곳에 설치된 밸브는 CHAIN VALVE 또는 PLATFORM 구성할 것.
- MANHOLE : 2개 이상 설치한다.  
MANHOLE COVER : FRP
- 온전시 CLOSE 되는 배관에는 LOTO 설치.
- CENTRIFUGAL PUMP  
MAT'L 표기 : CASING / IMPELLER
- TANK 내 유입, 유출 확인이 가능하고, 비산되지 않도록 최소 길이로 반영할 것 (SLAB로 부터 100 mm 떨어질 것)
- 내부 FRP LINING TANK의 SLEEVE는 SUS304 + FRP LINING 적용.
- 1-7027  
(W14-P-4714 A/B AUTO STOP)  
: REMOTE STATUS에서 W14-T-4710 LEVEL (LI-W7018) LOW LOW STOP.

|         |                           |          |
|---------|---------------------------|----------|
| 1A      | REVISED AFC               | 25.08.14 |
| 1       | REVISED AFC               | 25.01.17 |
| 0       | APPROVAL FOR CONSTRUCTION | 24.10.31 |
| 수정 REV. | 실명 DESCRIPTION            | 날짜 DATE  |

|             |       |
|-------------|-------|
| 제 도         | 이 인 학 |
| DRAWN BY    |       |
| 검 토         | 한 진 희 |
| CHECKED BY  |       |
| 승 인         | 박 동 영 |
| APPROVED BY |       |

SK 에코플랜트


공 사 명  
PROJECT TITLE  
M15X Ph4 WWT Project

도면명  
DWG. TITLE  
PIPING & INSTRUMENT DIAGRAM  
REUSE EMERGENCY TANK & PUMP

축 척  
SCALE  
NONE

날 짜  
DATE  
2025. 08. 14

|                   |                         |      |  |
|-------------------|-------------------------|------|--|
| PROJECT NO.       | 22330D                  | REV. |  |
| 도면번호<br>SHEET NO. | CJ-M15W14-PR-A20-000321 | 1A   |  |

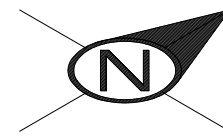

CLIENT  1

|   |                     |                                  |  |
|---|---------------------|----------------------------------|--|
| CONTRACTOR<br> |                     | PROJECT NAME<br>M15X Ph4 Project |  |
| COMMODITY<br>WW-REW                                                                                 |                     | JOB NO.<br>22330D                |  |
| LINE NO.<br>200A-WW-REW-ST1-N-7044                                                                  | SH'T NO.<br>01 / 01 | REV.<br>1                        |  |