

DRAWING LIST FOR TEST PACKAGE


PROJECT NO.: 22328D

PROJECT TITLE : M15X Ph2 Project

WW-BR-600


No	PKG No	UNIT	LINE NUMBER			P&ID		REMARK
			ISO DRAWING No	SHEET	REV	P&ID No	REV	
1	600	1FA	OD280-WW-BR-HP1-N-7017-02	2 OF 2	1	CJ-M15W14-PR-A20-000501	1A	
2	600	2FA	OD280-WW-BR-HP1-E-7017-01	1 OF 1	1	CJ-M15W14-PR-A20-000501	1A	

ITEM NO.	W14-T-4710
SERVICE	BRINE COLLECTION TANK
Q'TY	1
TYPE	RECTANGULAR
SIZE	W x L x H m (14.5) x 5.775 x 7.05 (EH 7.05) 5.0 x 5.3 x (14.05 (EH 12.55))
CAPA.	m3 (963 (EH 923))
HRT	hr 2.5
MAT'L	P.C + FRP

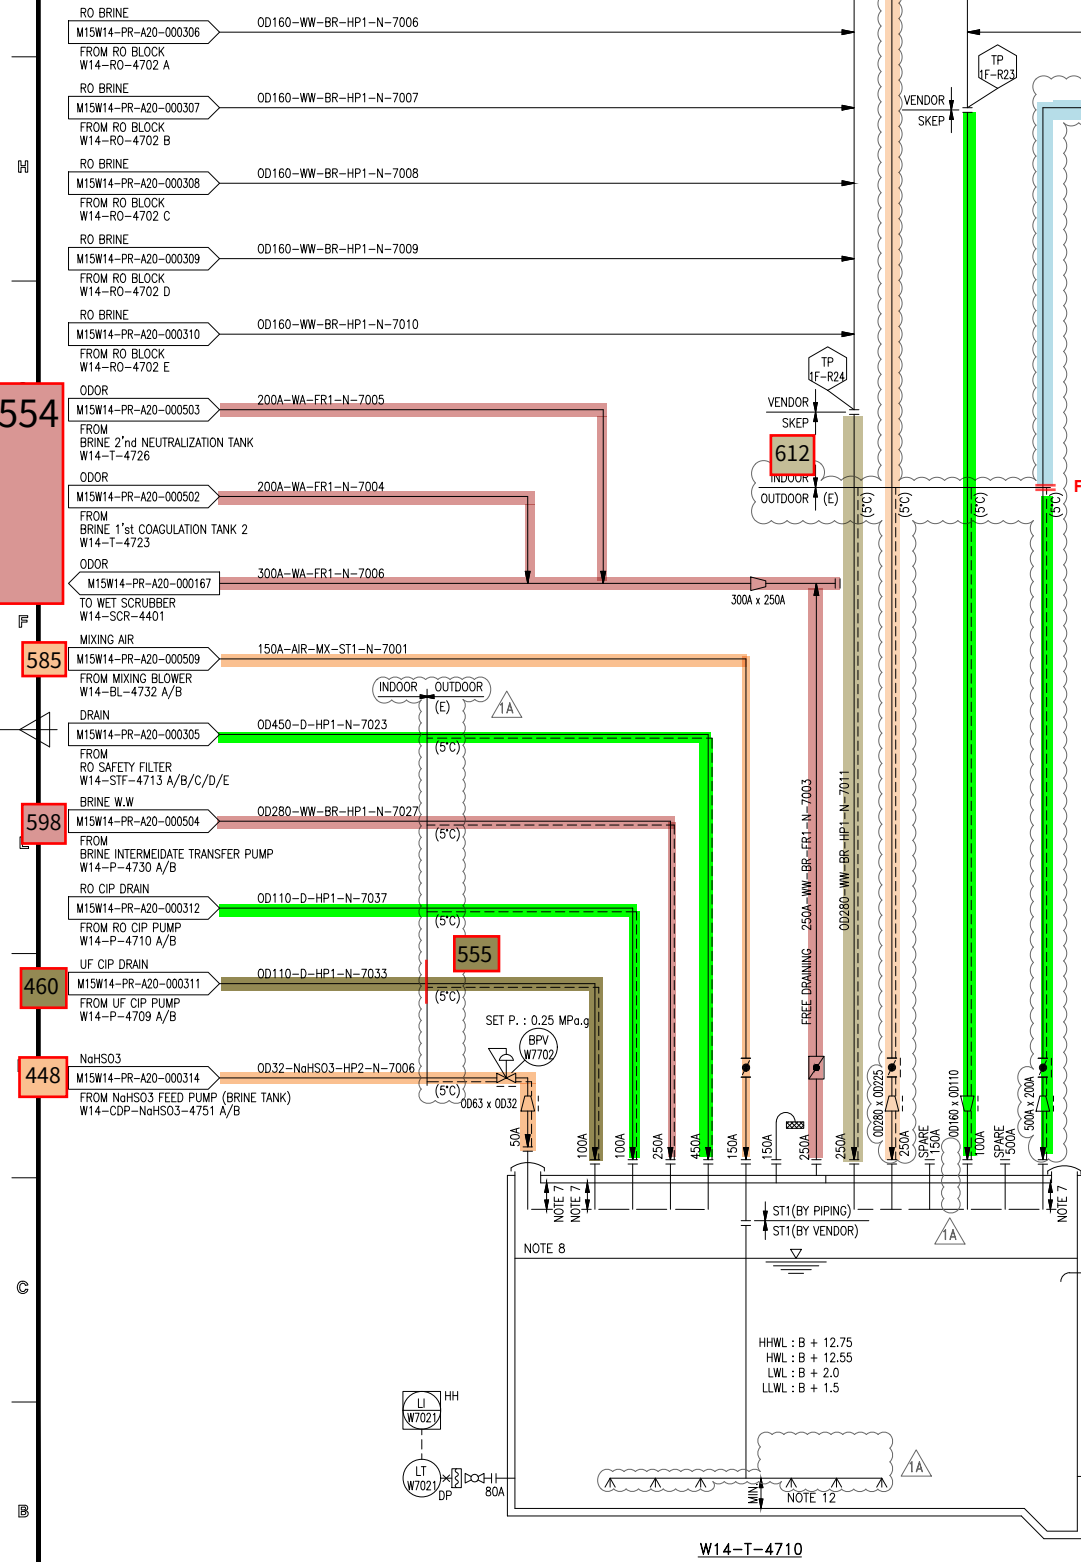


ITEM NO.	W14-P-4715 A/B/C
SERVICE	BRINE TRANSFER PUMP
Q'TY	2 + 1
TYPE	CENTRIFUGAL (WVF)
CAPA.	m3/hr.ea x mH 250 x 30 (0.29MPa)
MAT'L	ALLOY20/ALLOY20
POWER kW	(37)

Flange 추가

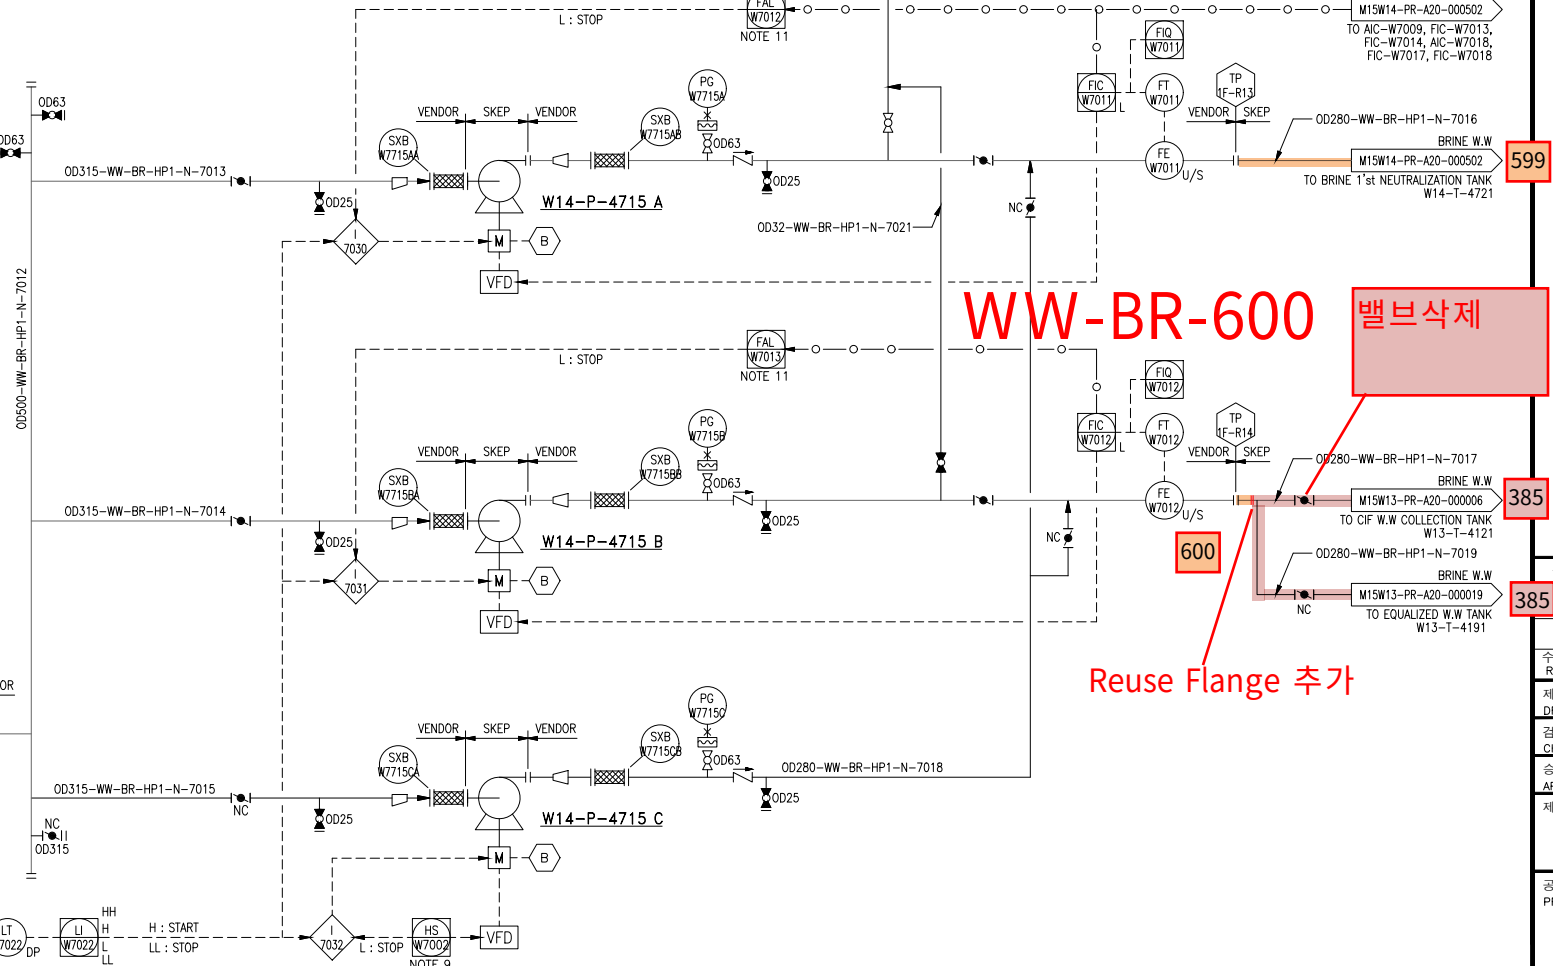


ITEM NO.	W14-T-4710
SERVICE	BRINE COLLECTION TANK
Q'TY	1
TYPE	RECTANGULAR
SIZE	W x L x H m (14.5) x 5.775 x 7.05 (EH 7.05) 5.0 x 5.3 x (14.05 (EH 12.55))
CAPA.	m3 (963 (EH 923))
HRT	hr 2.5
MAT'L	P.C + FRP

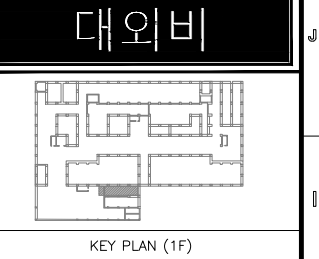


- NOTE
1. TANK의 HWL 이하로 연결되는 모든 배관은 BLOCK 별의 설치할 것
 2. 환수 인입지점은 펌프 흡입측에서 최대한 이격하여 설치
 3. 2m 이상 높은 곳에 설치된 밸브는 CHAIN VALVE 또는 PLATFORM 구성할 것
 4. MANHOLE : 2개 이상 설치한다.
MANHOLE COVER : FRP
 5. 환전시 CLOSE 되는 배관에는 LOTO 설치
 6. CENTRIFUGAL PUMP
MAT'L 표기 : CASING / IMPELLER
 7. TANK 내 유입, 유출 확인이 가능하고, 비산되지 않도록 최소 길이로 반영할 것 (SLAB로부터 100mm 떨어진 것)
 8. 내부 FRP LINING TANK의 SLEEVE는 SUS304 + FRP LINING 적용
 9. FIC-W7011/W7012 중 선택은전
 10. INTERLOCK NO. 1-7030/7031/7032 (W14-P-4715 A/B/C AUTO STOP)
: REMOTE STATUS에서 W14-T-4710 LEVEL (LI-W7022) LOW LOW STOP 또는 W14-P-4715 A/B DISCHARGE FLOW (FAL-W7011/W7012) LOW STOP
 11. BRINE TRANSFER PUMP RUN 후 30초 후 부터 동작한다.
 12. (DIFFUSER HOLE 및 배관배치의 관련된 상세 설계는 VENDOR가 수행한다.)


REVISED AFC	25.08.14
REVISED AFC	25.01.17
0 APPROVAL FOR CONSTRUCTION	24.10.31
정 EV. 설명 DESCRIPTION	날 짜 DATE
도 이 인 학	
DRAWN BY	
토 한 진 희	
CHECKED BY	
인 박 동 영	
APPROVED BY	
작 사	
SK 에코플랜트	
공사명 PROJECT TITLE	
M15X Ph4 WWT Project	
도면명 DWG. TITLE	
PIPING & INSTRUMENT DIAGRAM	
BRINE COLLECTION TANK &	
TRANSFER PUMP	
척 SCALE	NONE
날 짜 DATE	2025. 08. 14
PROJECT NO.	22330D
도면번호 SHEET NO.	CJ-M15W14-PR-A20-000501
REV.	1A

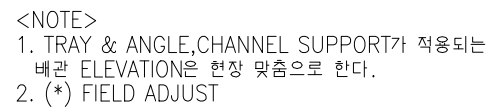

CLIENT  1


[illegible]

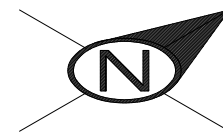

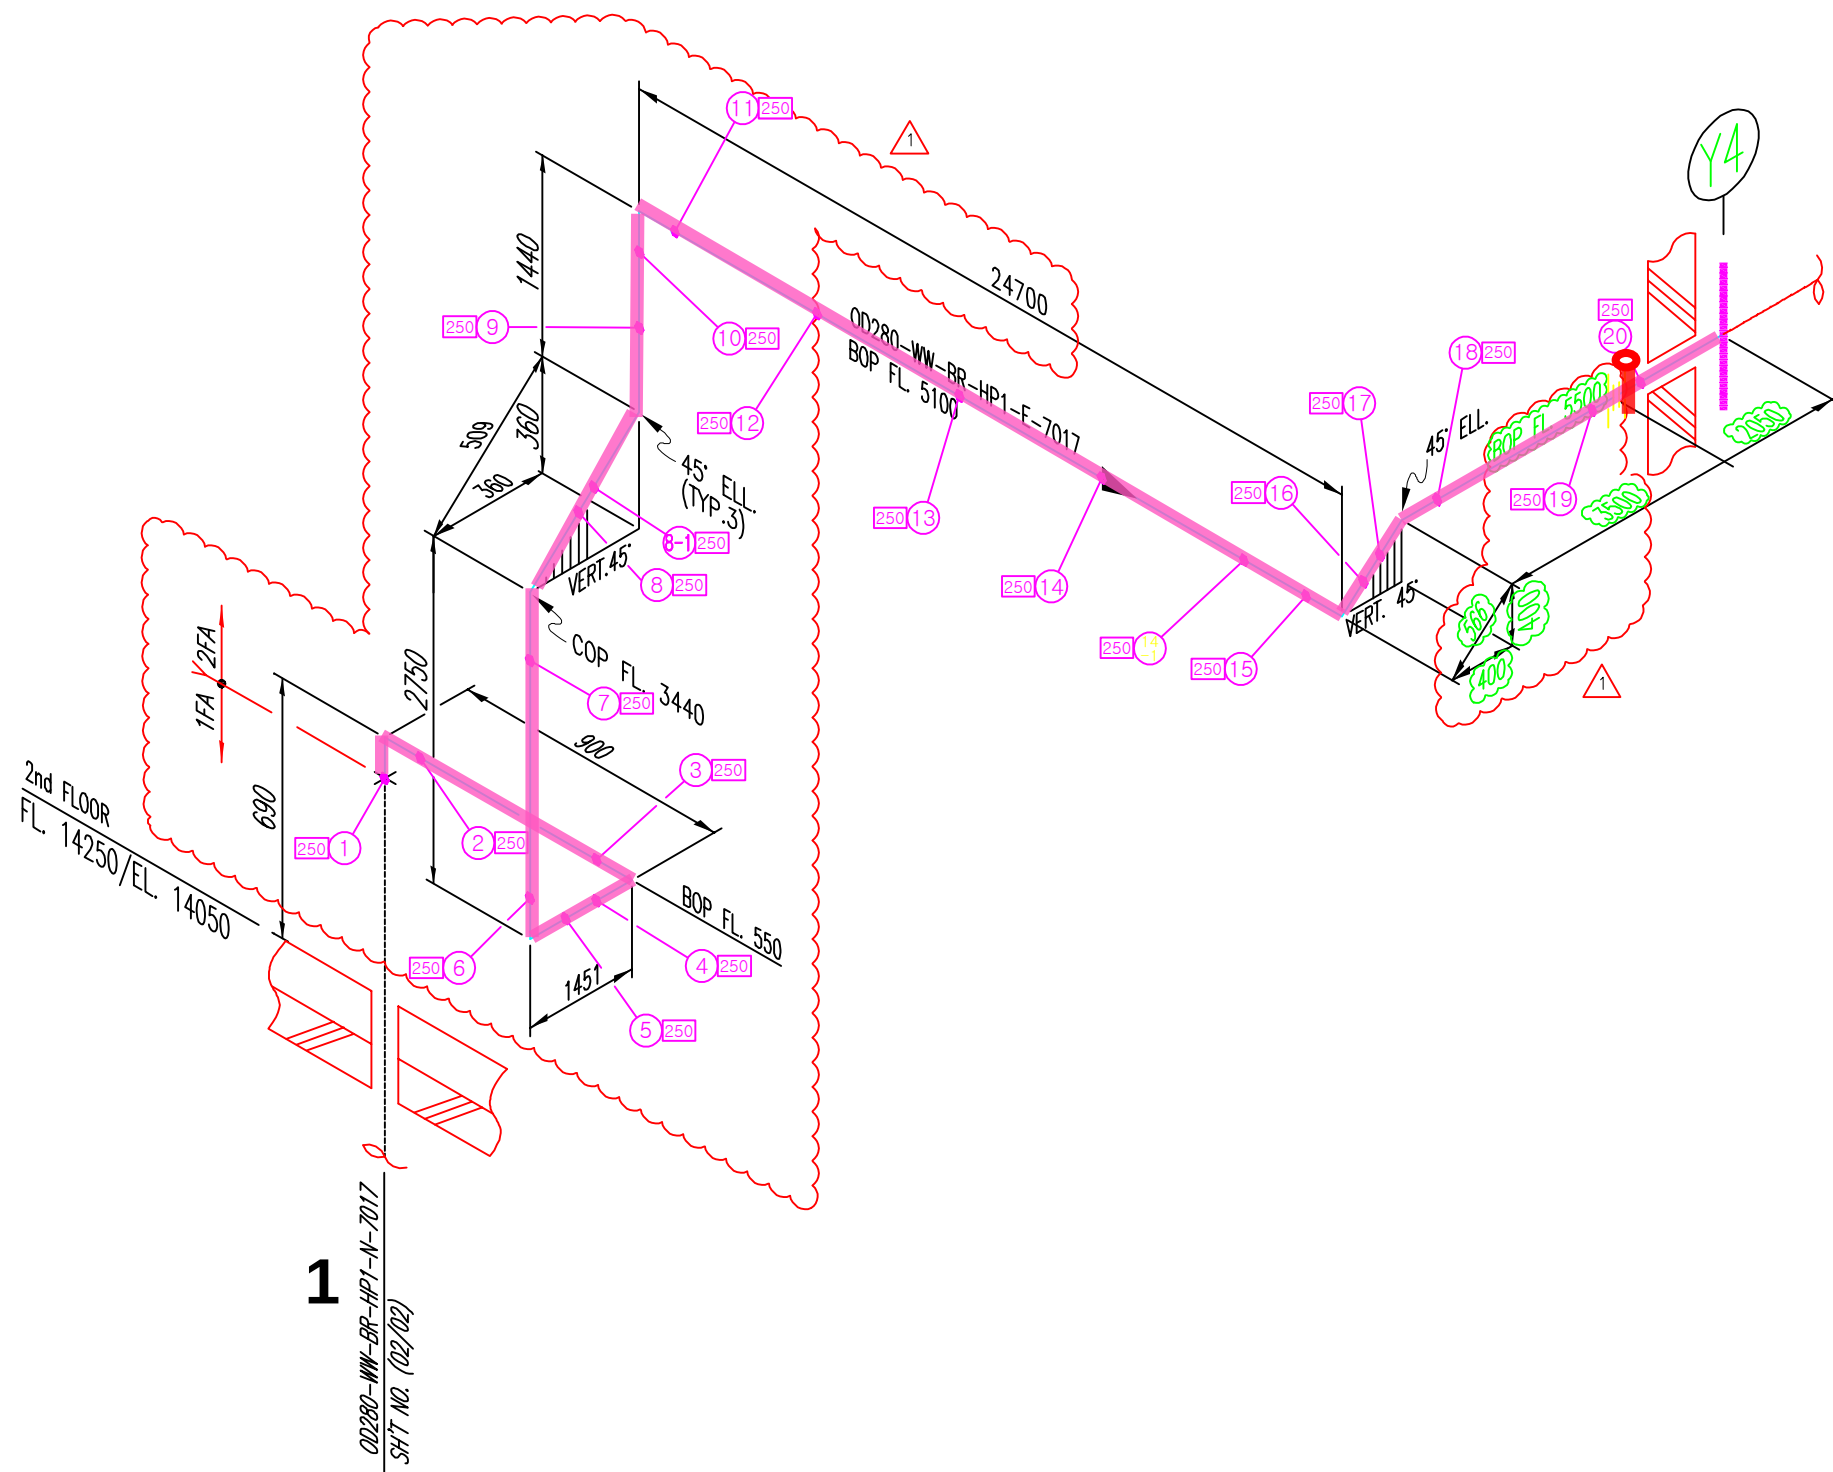

1. TRAY & ANGLE, CHANNEL SUPPORT가 적용되는
배관 ELEVATION은 현장 맞춤으로 한다.
2. (*) FIELD ADJUST

INSULATION	CODE	E	CONDITION	PRESS. (kg/cm2g)	TEMP. (°C)	AREA	W14						
	THICK.	25	DESIGN	10	60	UNIT	R2FA						
			OPERATING	7.5	AMB	REF. PLAN DWG.			25.03.31	REVISED AS MARKED	황래중	안남후	박동영
						CJ-M15W14-PI-A30-010018-A			24.12.20	APPROVED FOR CONSTRUCTION	황래중	안남후	박동영
						REF. P. & ID		REV. NO.	DATE	DESCRIPTION	BY	CHK	APP
						CJ-M15W14-PR-A20-000501							

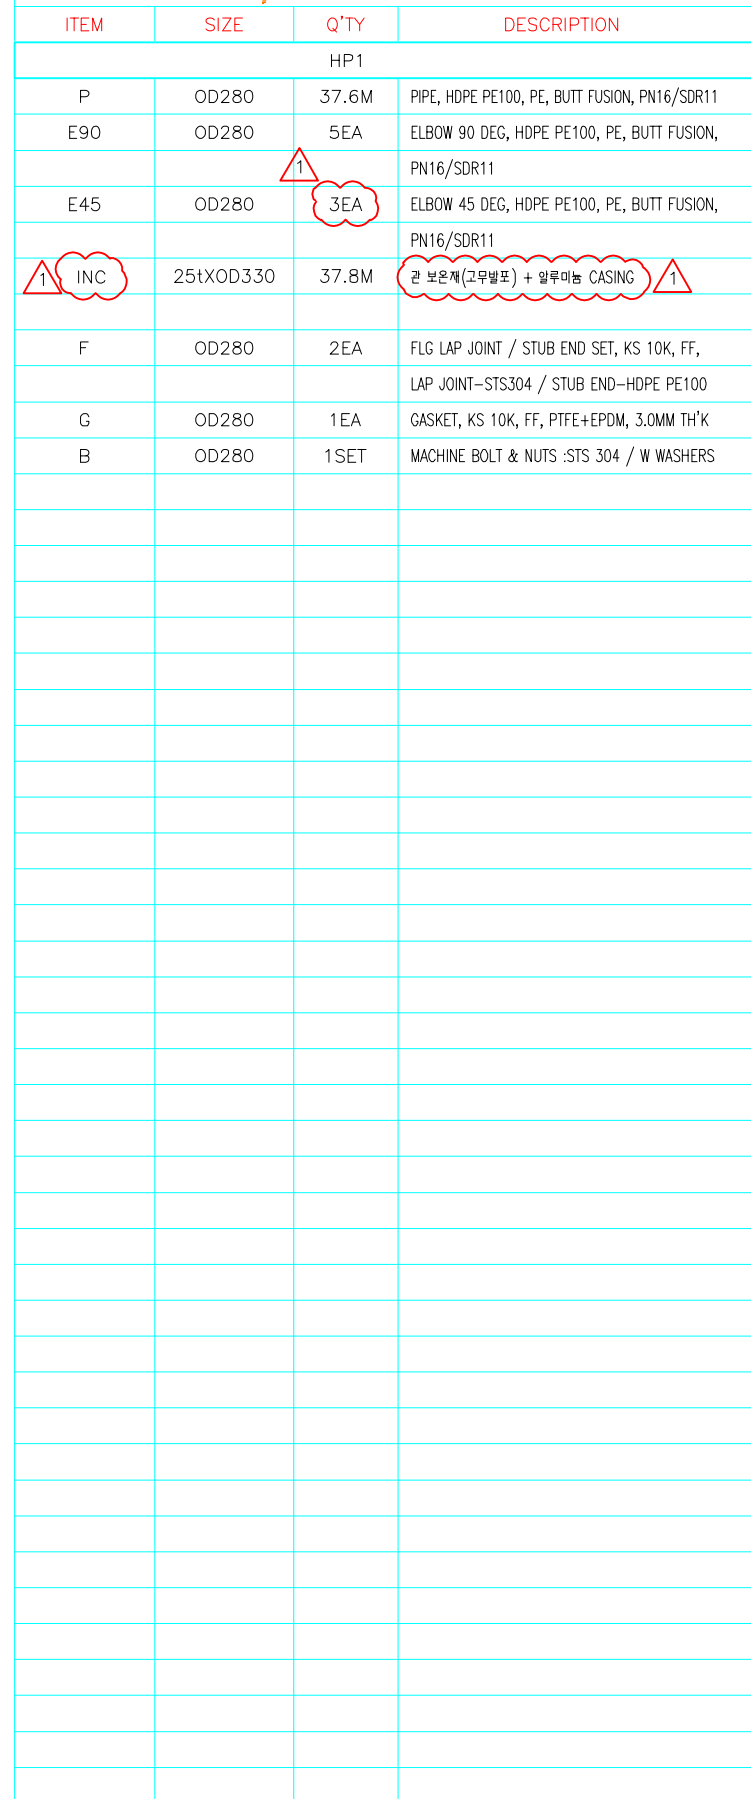

2

CONTRACTOR 		PROJECT NAME M15X Ph4 Project	
COMMODITY WW—BR		JOB NO. 22330D	
LINE NO. OD280—WW—BR—HP1—E—7017	SH'T NO. 01 / 01		REV. 1