


DRAWING LIST FOR TEST PACKAGE

PROJECT NO.: 22328D

PROJECT TITLE : M15X Ph2 Project

WW-SLD-602

No	PKG No	UNIT	LINE NUMBER			P&ID		REMARK
			ISO DRAWING No	SHEET	REV	P&ID No	REV	
1	602	1MF	150A-WW-SLD-ST1-N-7006-01	1 OF 1	0	CJ-M15W14-PR-A20-000503	1A	
2	602	1MF	150A-WW-SLD-ST1-N-7007-01	1 OF 1	0	CJ-M15W14-PR-A20-000503	1A	
3	602	1MF	150A-WW-SLD-ST1-N-7008-01	1 OF 1	0	CJ-M15W14-PR-A20-000503	1A	
4	602	1MF	40A-IW-ST1-C-7006-03	3 OF 4	0	CJ-M15W14-PR-A20-000503	1A	
5	602	1MF	40A-IW-ST1-C-7006-04	4 OF 4	0	CJ-M15W14-PR-A20-000503	1A	
6	602	1MF	40A-AIR-SV-ST1-C-7006-03	3 OF 4	0	CJ-M15W14-PR-A20-000503	1A	
7	602	1MF	40A-AIR-SV-ST1-C-7006-04	4 OF 4	0	CJ-M15W14-PR-A20-000503	1A	

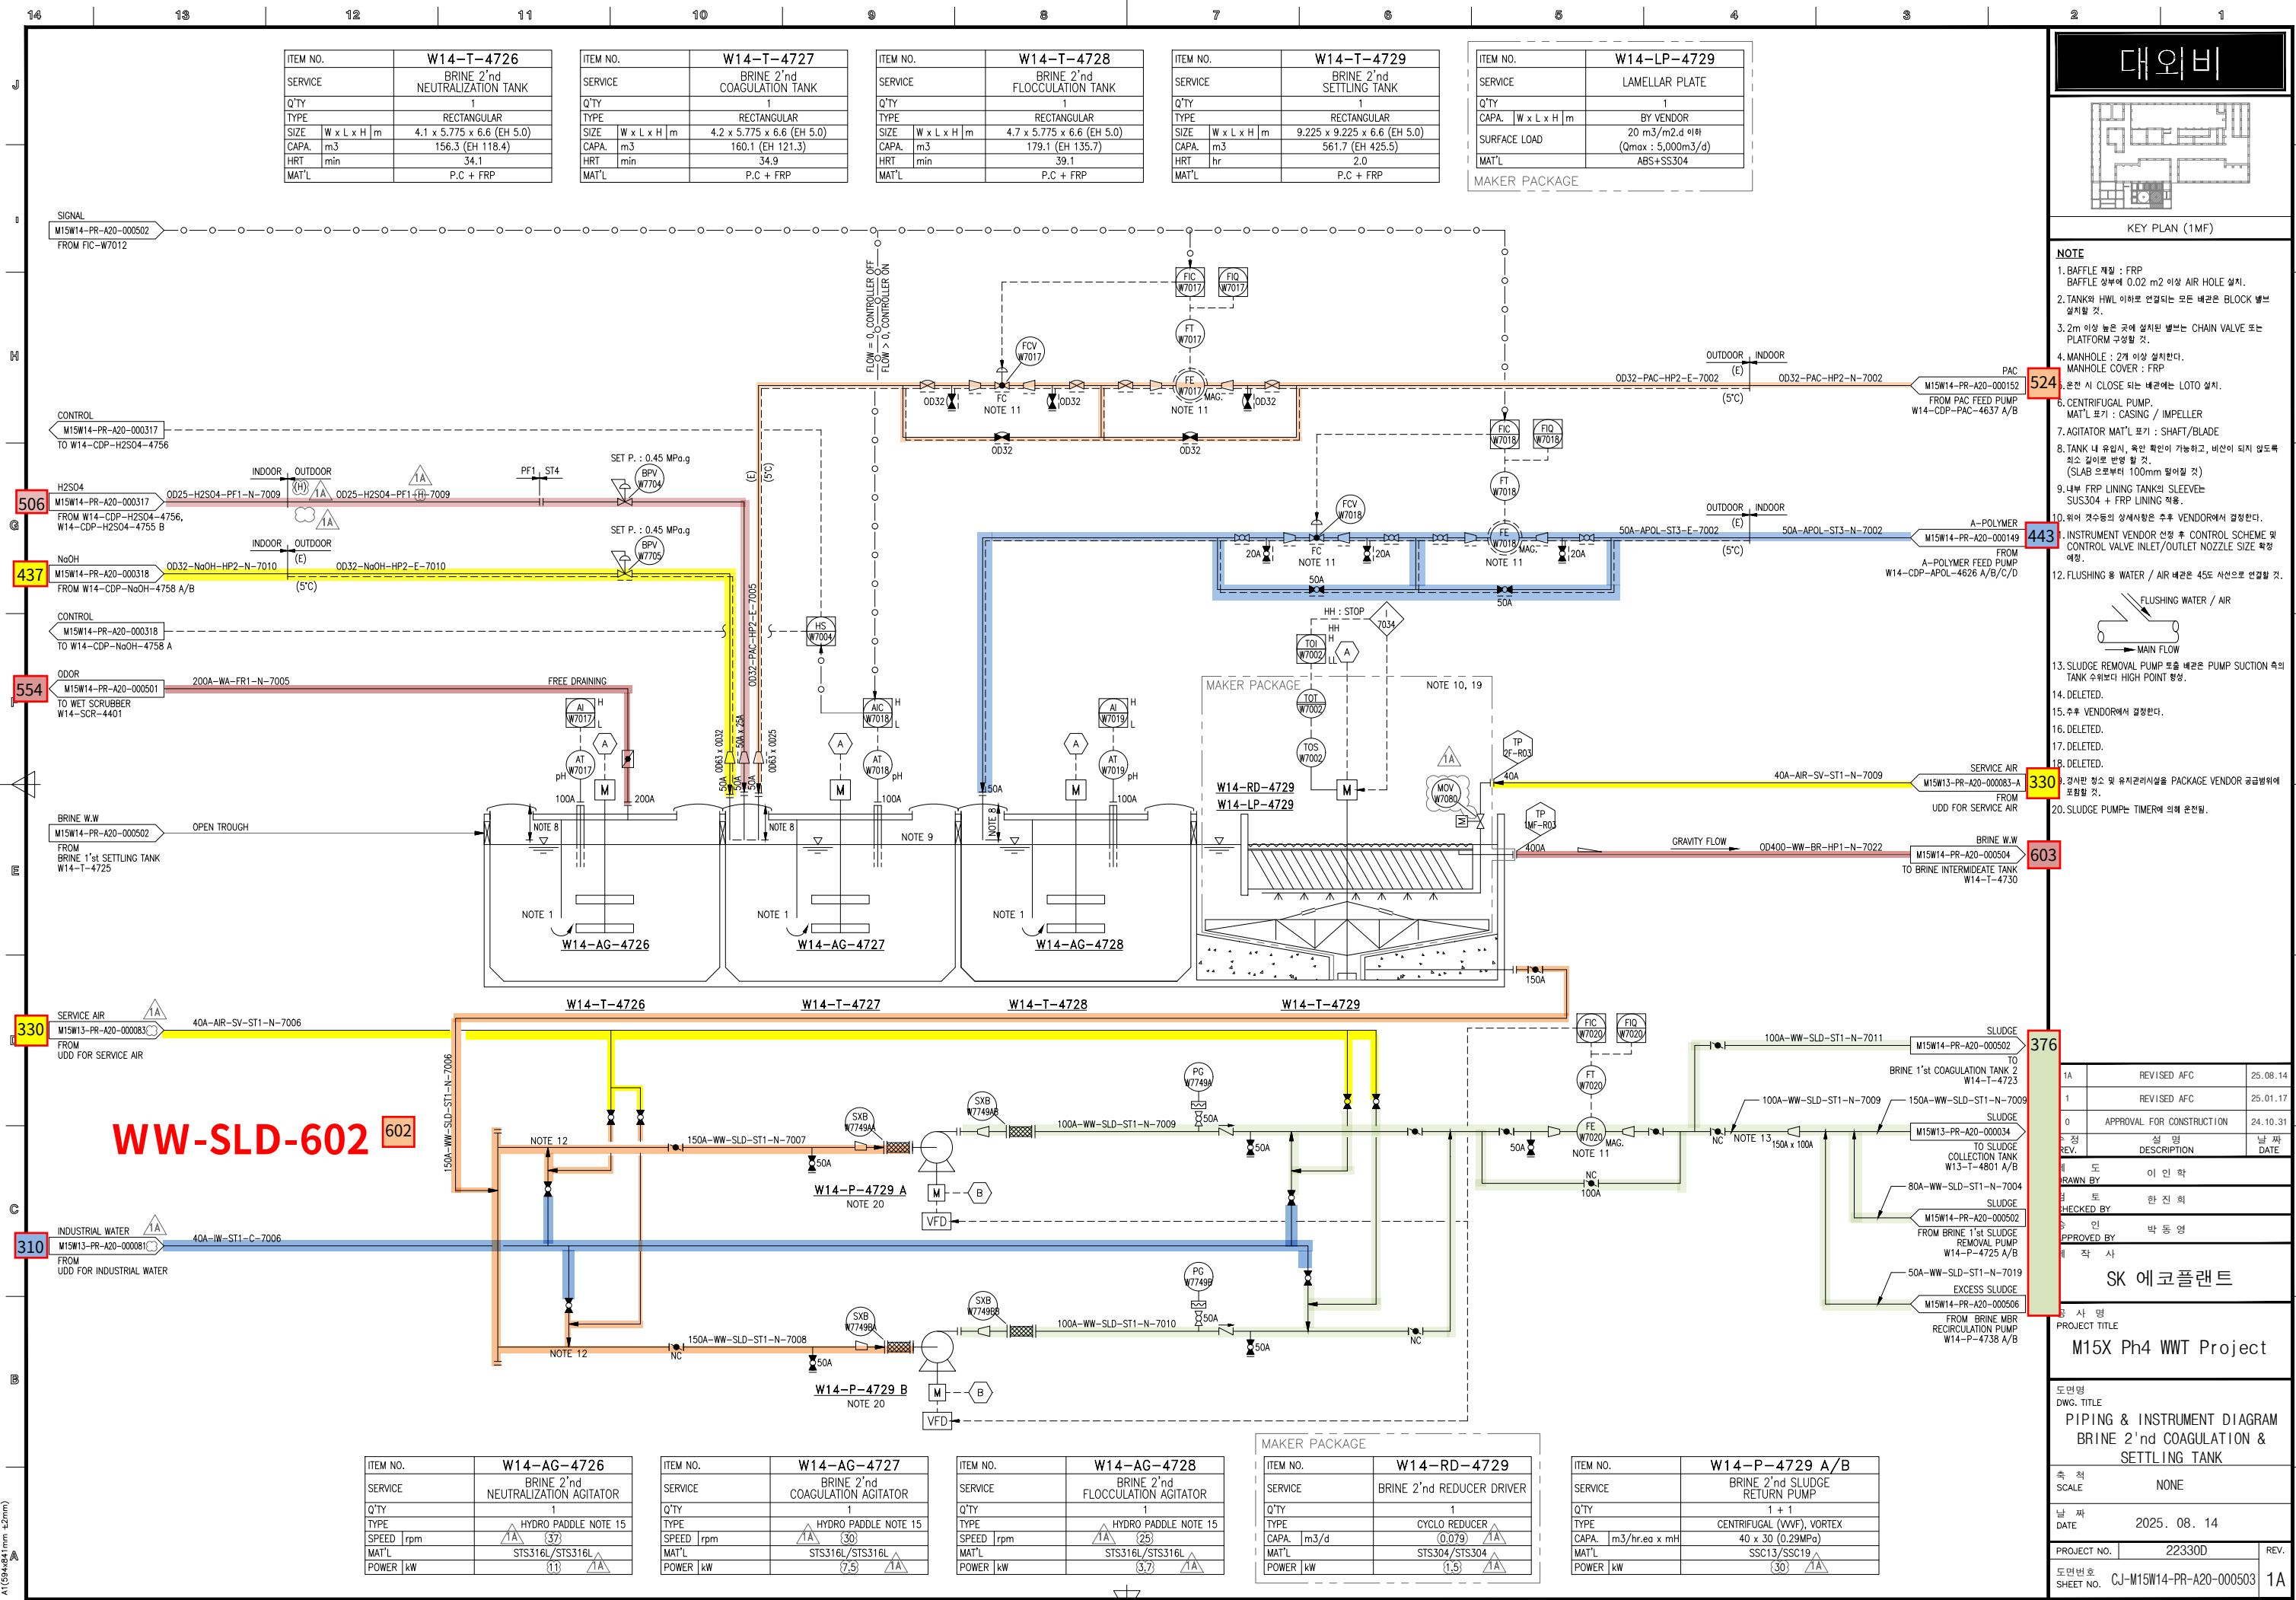

대외비

KEY PLAN (1MF)

- NOTE
1. BAFFLE 재질 : FRP
BAFFLE 상부에 0.02 m2 이상 AIR HOLE 설치.
 2. TANK와 HWL 이하로 연결되는 모든 배관은 BLOCK 밸브 설치할 것.
 3. 2m 이상 높은 곳에 설치된 밸브는 CHAIN VALVE 또는 PLATFORM 구성할 것.
 4. MANHOLE : 2개 이상 설치한다.
MANHOLE COVER : FRP
 5. 온천 시 CLOSE 되는 배관은 LOTO 설치.
 6. CENTRIFUGAL PUMP.
MAT'L 표기 : CASING / IMPELLER
 7. AGITATOR MAT'L 표기 : SHAFT/BLADE
 8. TANK 내 유입시, 육안 확인이 가능하고, 비산이 되지 않도록 최소 길이로 반영 할 것.
(SLAB으로부터 100mm 떨어질 것)
 9. 내부 FRP LINING TANK의 SLEEVE는 SUS304 + FRP LINING 적용.
 10. 뒤어 것수등의 상세사상은 추후 VENDOR에서 결정한다.
 11. INSTRUMENT VENDOR 선정 후 CONTROL SCHEME 및 CONTROL VALVE INLET/OUTLET NOZZLE SIZE 확정 예정.
 12. FLUSHING 용 WATER / AIR 배관은 45도 서언으로 연결할 것.
 13. SLUDGE REMOVAL PUMP 토출 배관은 PUMP SUCTION 속의 TANK 수위보다 HIGH POINT 향상.
 14. DELETED.
 15. 추후 VENDOR에서 결정한다.
 16. DELETED.
 17. DELETED.
 18. DELETED.
 19. DELETED.
 20. SLUDGE PUMP는 TIMER에 의해 운전됨.

1A	REVISED AFC	25.08.14
1	REVISED AFC	25.01.17
0	APPROVAL FOR CONSTRUCTION	24.10.31
수정	실명	날짜
REV.	DESCRIPTION	DATE
도	이인학	
검	한진희	
HECKED BY		
승인	박동명	
APPROVED BY		
작사		

SK 에코플랜트

공 사 명
PROJECT TITLE

M15X Ph4 WWT Project

도면명
DWG. TITLE

PIPING & INSTRUMENT DIAGRAM
BRINE 2nd COAGULATION & SETTLING TANK

속 척
SCALE

NONE

날 짜
DATE

2025. 08. 14

PROJECT NO.

22330D

REV.

A

도면번호
SHEET NO.

CJ-M15W14-PR-A20-000503

1A

ITEM NO.	W14-T-4726
SERVICE	BRINE 2nd NEUTRALIZATION TANK
Q'TY	1
TYPE	RECTANGULAR
SIZE	W x L x H m 4.1 x 5.775 x 6.6 (EH 5.0)
CAPA.	m3 156.3 (EH 118.4)
HRT	min 34.1
MAT'L	P.C + FRP

ITEM NO.	W14-T-4727
SERVICE	BRINE 2nd COAGULATION TANK
Q'TY	1
TYPE	RECTANGULAR
SIZE	W x L x H m 4.2 x 5.775 x 6.6 (EH 5.0)
CAPA.	m3 160.1 (EH 121.3)
HRT	min 34.9
MAT'L	P.C + FRP

ITEM NO.	W14-T-4728
SERVICE	BRINE 2nd FLOCCULATION TANK
Q'TY	1
TYPE	RECTANGULAR
SIZE	W x L x H m 4.7 x 5.775 x 6.6 (EH 5.0)
CAPA.	m3 179.1 (EH 135.7)
HRT	min 39.1
MAT'L	P.C + FRP

ITEM NO.	W14-T-4729
SERVICE	BRINE 2nd SETTLING TANK
Q'TY	1
TYPE	RECTANGULAR
SIZE	W x L x H m 9.225 x 9.225 x 6.6 (EH 5.0)
CAPA.	m3 561.7 (EH 425.5)
HRT	hr 2.0
MAT'L	P.C + FRP

ITEM NO.	W14-LP-4729
SERVICE	LAMELLAR PLATE
Q'TY	1
CAPA.	W x L x H m BY VENDOR
SURFACE LOAD	20 m3/m2.d 이하 (Qmax : 5,000m3/d)
MAT'L	ABS+SS304

ITEM NO.	W14-AG-4726
SERVICE	BRINE 2nd NEUTRALIZATION AGITATOR
Q'TY	1
TYPE	HYDRO PADDLE NOTE 15
SPEED	rpm (37)
MAT'L	STS316L/STS316L
POWER	kw (1)

ITEM NO.	W14-AG-4727
SERVICE	BRINE 2nd COAGULATION AGITATOR
Q'TY	1
TYPE	HYDRO PADDLE NOTE 15
SPEED	rpm (30)
MAT'L	STS316L/STS316L
POWER	kw (7.5)

ITEM NO.	W14-AG-4728
SERVICE	BRINE 2nd FLOCCULATION AGITATOR
Q'TY	1
TYPE	HYDRO PADDLE NOTE 15
SPEED	rpm (25)
MAT'L	STS316L/STS316L
POWER	kw (3.7)


ITEM NO.	W14-RD-4729
SERVICE	BRINE 2nd REDUCER DRIVER
Q'TY	1
TYPE	CYCLO REDUCER
CAPA.	m3/d (0.079)
MAT'L	STS304/STS304
POWER	kw (1.5)

ITEM NO.	W14-P-4729 A/B
SERVICE	BRINE 2nd SLUDGE RETURN PUMP
Q'TY	1 + 1
TYPE	CENTRIFUGAL (VVF), VORTEX
CAPA.	m3/hr.ea x mH 40 x 30 (0.29MPa)
MAT'L	SSC13/SSC19
POWER	kw (30)



ITEM	SIZE	Q'TY	DESCRIPTION
ST1			
P	150A	0.9M	PIPE, STS 304TP, ERW, BE – SCH 10S
T	150A	1EA	TEE EQUAL, STS304, ERW, BE – SCH 10S
VF	150A	1EA	BUTTERFLY VALVE, KS 10K, WAFER RF, BODY–GCD450 /
			TRIM–STS304 / EPDM–LINED, GEAR
F	150A	1EA	FLG SO, KS 10K, RF, STS304
BL	150A	1SET	MACHINE BOLT & NUTS :STS 304 / W WASHERS(SPECIAL)

		ST1	
P	150A	5.8M	PIPE, STS 304TP, ERW, BE – SCH 10S
F1	150A	2EA	FLG S0, KS 10K, FF, STS304
STOP	150A	1EA	ANCHOR PLATE
G1	150A	1EA	GASKET, KS 10K, FF, PTFE+EPDM, 3.0MM TH'K
B	150A	1SET	MACHINE BOLT & NUTS :STS 304 / W WASHERS
		FR1	
P2	150A	0.7M	PIPE, FRP(MANUFACTURER STD), PE/BUTT-JOINT, 4.5T
F2	150A	1EA	FLG, KS 10K, FF, FRP(MANUFACTURER STD), BUTT-JOINT

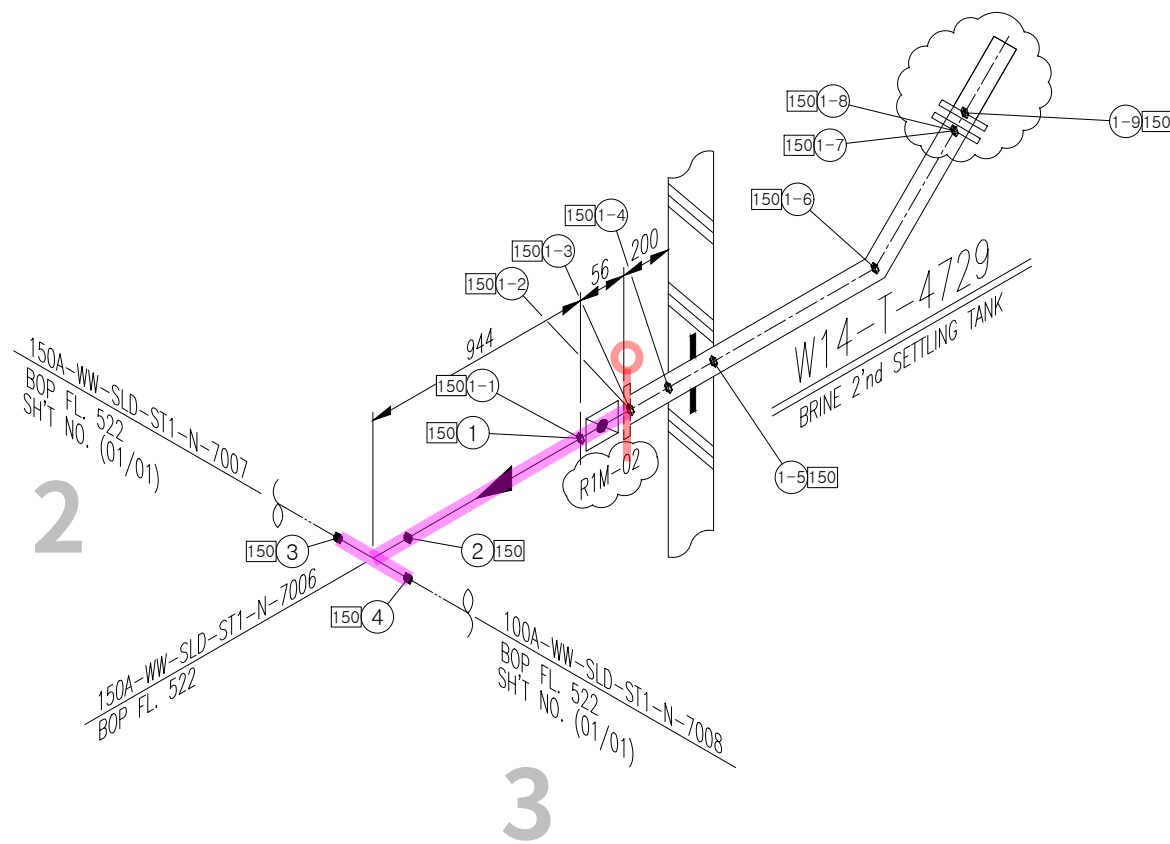


<NOTE>
1. (*) FIELD ADJUST

* PIPE : P/P1	* 90° ELBOW : E90	* 45° ELBOW : E45	* TEE : T	* RED.TEE : TR	* STUB-IN : STU	* REINFORCING PAD : RP	* CON.RED : RC	* ECC.RED : RE	* CON.SWAGE : RCS/RCS1	* ECC.SWAGE : RES/RES1	* NIPPLE : NP/NP1/NP2	* CAP : CAP/CAP1	* PLUG : PLG	* FULL COUPLING : FC	* HALF COUPLING : HF/HF1
* STUB-IN : STU	* SOCKET(HDPE/PVC) : SC	* SADDLE(HDPE) : SD	* FLANGE : F/F1	* GASKET : G/G1/G2	* BOLT & NUT : B/B1	* BLIND FLANGE : FB/FB1	* GATE VA. : VG/VG1/VG2	* BALL VA. : VB/VBLO/VB1/VB1O/VB2/VB2LO	* BUTTERFLY VA. : VF/VF4	* CHECK VA. : VC/VC1/VC2/VC3/VC4/VC5/VC6/VC7					
* GLOBE VA. : VL/VL1/VL2	* DIAPHRAGM VA. : VD/VDLO	* DAMPER : VP	* QUICK COUPLING : SQC	* FLEXIBLE JOINT(STEEL) : FLXB	* FLEXIBLE JOINT(RUBBER) : FLXR	* FLEXIBLE JOINT(STEEL PTFE LINED) : FLXL	* FLEXIBLE HOSE : FLXH	* STEAM TRAP : ST	* SPRAY NOZZLE : SPN	* EMERGENCY SHOWER : SSH					
* STRAINER(Y-TYPE) : YSTR	* STRAINER(T-TYPE) : TSTR	* STRAINER(BUCKET-TYPE) : BSTR	* ANCHOR PLATE : STOP	* BIRD SCREEN : BS	* ISOLATION KIT : IK	* UNLOADING BOX : UB	* AIR TRAP : AT	* LOTO : LOTO	* SIGHT GLASS : SG	* PRESSURE GAUGE : PG	* SHILED : SH	* SPECIAL BOLT & NUT : BL/BL1			

INSULATION	CODE	N	CONDITION	PRESS. (kg/cm2g)	TEMP. (°C)	AREA W14								CONTRACTOR	PROJECT NAME	
	THICK.	—	DESIGN	6.4	60	UNIT R1MF									M15X Ph4 Project	
			OPERATING	4	AMB	REF. PLAN DWG. CJ-M15W14-PI-A30-020016-A		25.01.24	APPROVED FOR CONSTRUCTION	황래중	안남후	박동영	COMMODITY WW-SLD	JOB NO. 22330D		
					REF. P & ID CJ-M15W14-PR-A20-000503	LINE NO.								150A-WW-SLD-ST1-N-7006	SH'T NO. 01 / 01	REV. 0
							REV. NO.	DATE	DESCRIPTION	BY	CHK	APP'D				

경고 : 본 도면은 SK HYNIX의 기밀비밀 자료로서, 어떠한 경우에도 목적 외 사용, 복제, 제3자에게 공개, 누설 및 무단 배포할 수 없으며, 회사는 유포자의 무단 사용으로 피해가 발생할 경우 유포자에게 민/형사상 책임을 요구할 수 있습니다.

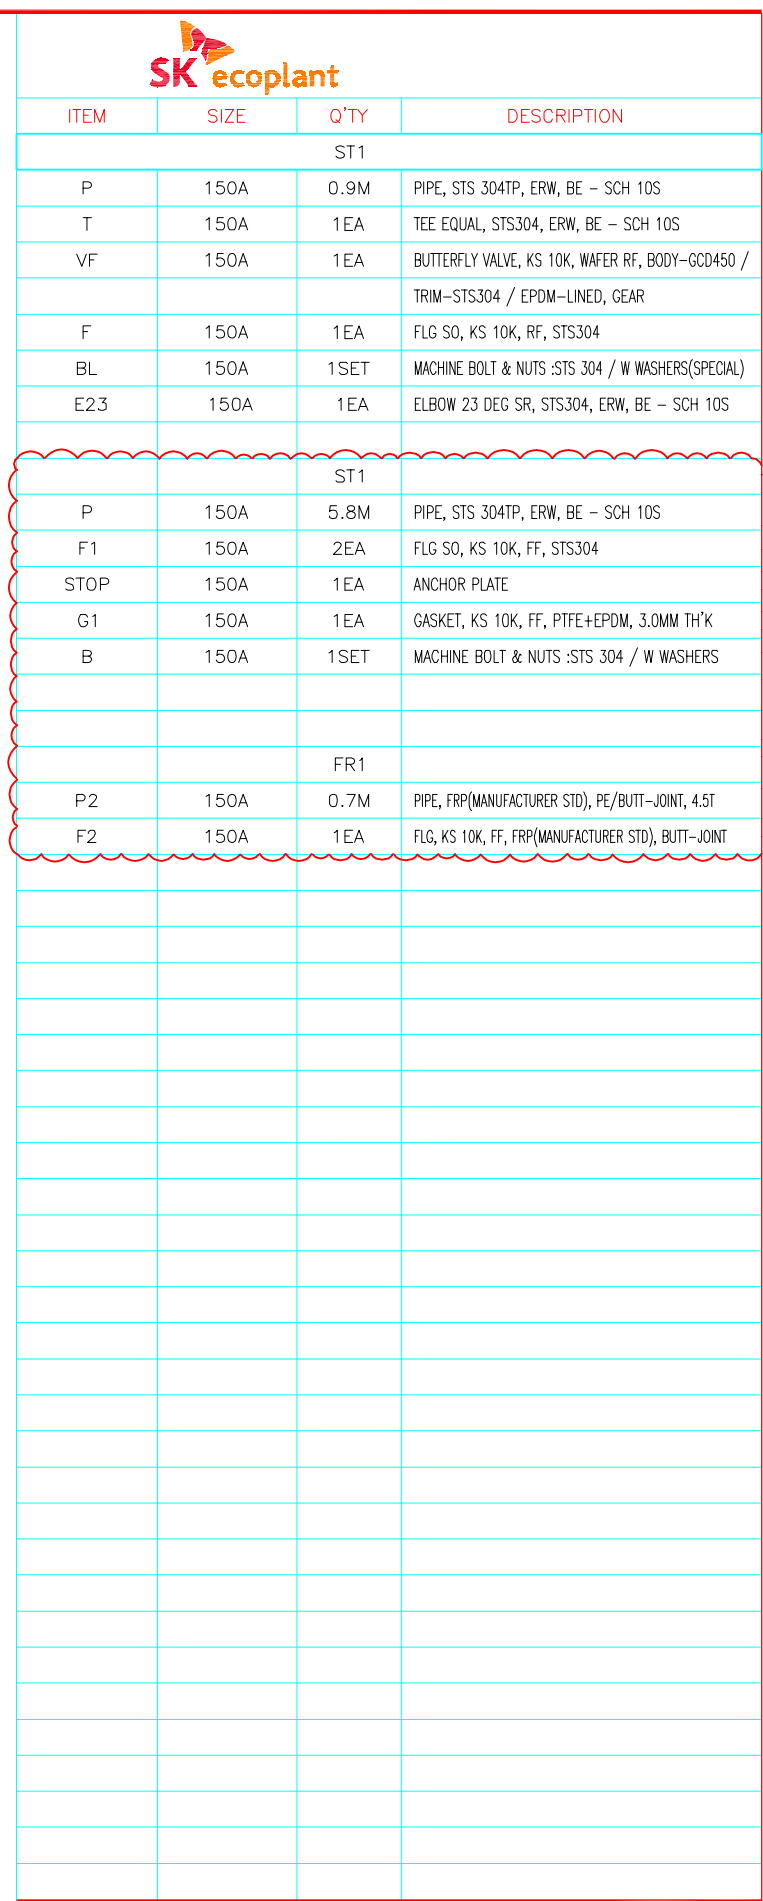

CLIENT SK hynix 1

INSULATION	CODE	N	CONDITION	PRESS. (kg/cm2g)	TEMP. (°C)	AREA	W14							CONTRACTOR	PROJECT NAME		
	THICK.	—	DESIGN	6.4	60	UNIT	R1MF								M15X Ph4 Project		
			OPERATING	4	AMB	REF. PLAN DWG.	CJ-M15W14-PI-A30-020016-A								COMMODITY	WW-SLD	JOB NO.
						REF. P. & ID	CJ-M15W14-PR-A20-000503		25.01.24	APPROVED FOR CONSTRUCTION	황래중	안남후	박동영	LINE NO.	150A-WW-SLD-ST1-N-7006	SH'T NO.	REV.
						REV. NO.			DATE	DESCRIPTION	BY	CHK	APP'D			01 / 01	0




2


CLIENT  2

CONTRACTOR 		PROJECT NAME M15X Ph4 Project	
COMMODITY WW-SLD		JOB NO. 22330D	
LINE NO. 150A-WW-SLD-ST1-N-7007	SH'T NO. 01 / 01		REV. 0

경고 : 본 도면은 SK HYNIX의 기밀비밀 자료로서, 어떠한 경우에도 목적 외 사용, 복제, 제3자에게 공개, 누설 및 유출할 수 없으며, 회사는 유포자의 불법 사용으로 피해가 발생할 경우 유포자에게 민/형사상 책임을 요구할 수 있음

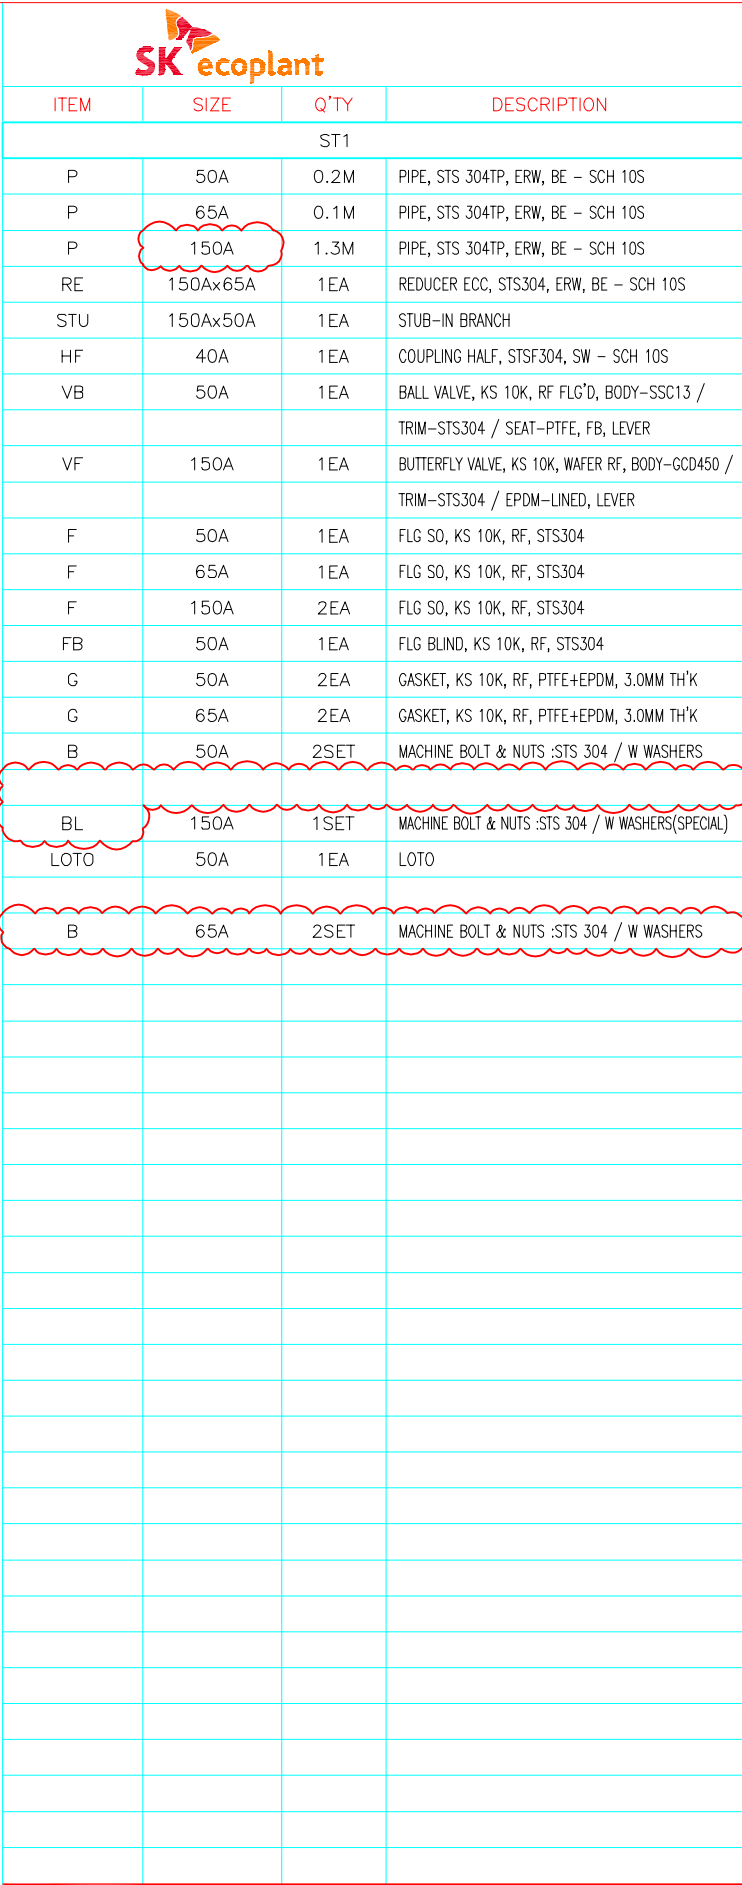

CLIENT		2	
		PROJECT NAME	
		M15X Ph4 Project	
COMMODITY		JOB NO.	
WW-SLD		22330D	
LINE NO.	150A-WW-SLD-ST1-N-7007	SH'T NO.	REV.
		01 / 01	0

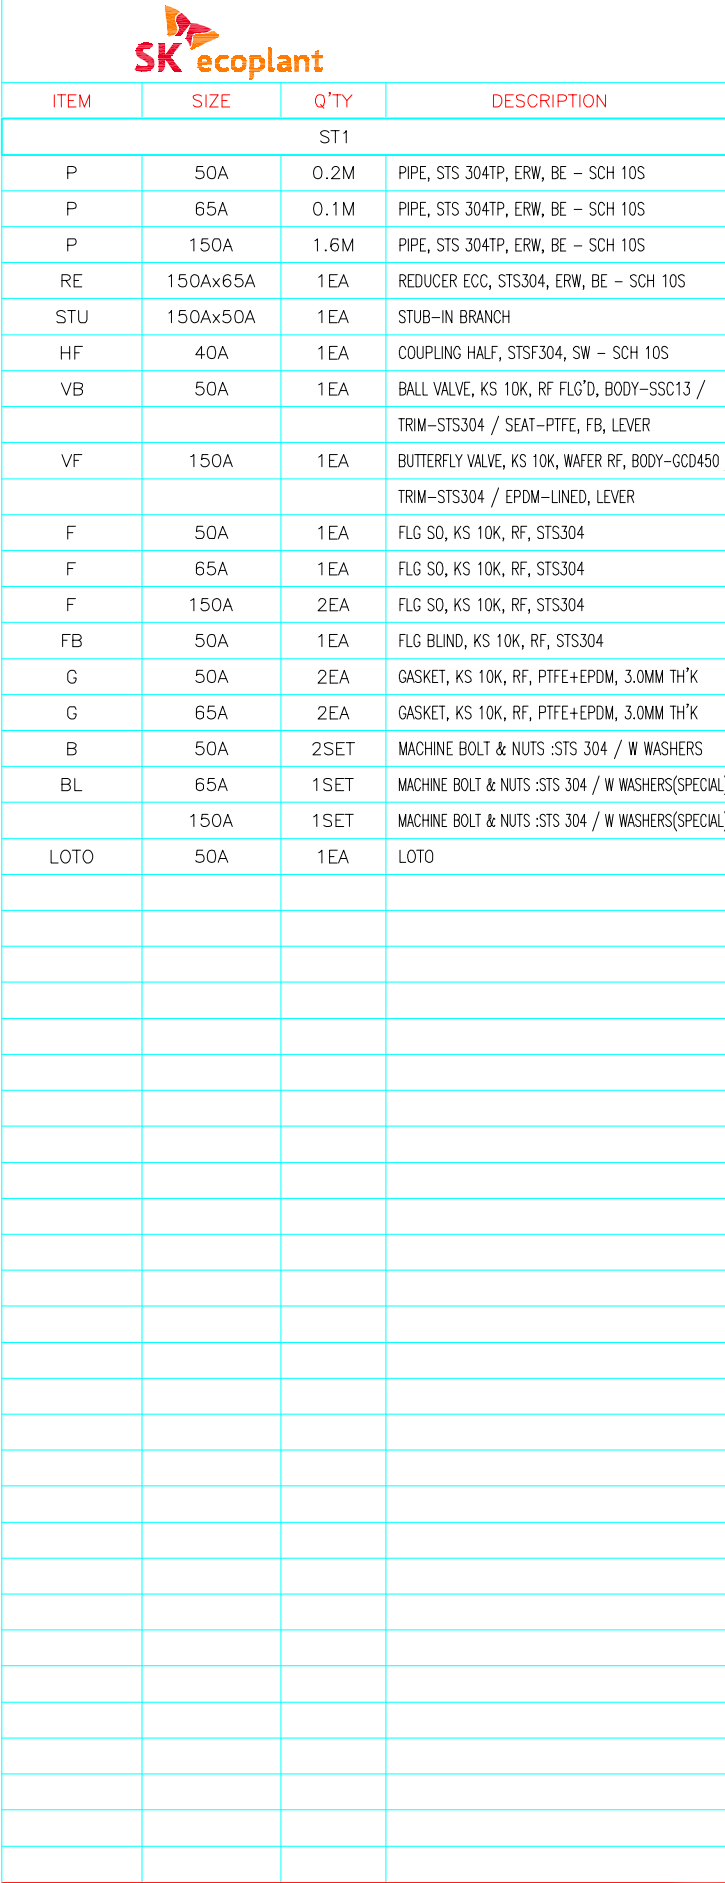

CLIENT				3	
CONTRACTOR			PROJECT NAME		
			M15X Ph4 Project		
COMMODITY			JOB NO.		
WW-SLD			22330D		
LINE NO.			SH'T NO.		REV.
150A-WW-SLD-ST1-N-7008			01 / 01		0

[illegible]

<NOTE>
1. (*) FIELD ADJUST

* PIPE : P/P1	* 90° ELBOW : E90	* 45° ELBOW : E45	* TEE : T	* RED.TEE : TR	* STUB-IN : STU	* REINFORCING PAD : RP	* CON.RED : RC	* ECC.RED : RE	* CON.SWAGE : RCS/RCS1	* ECC.SWAGE : RES/RES1	* NIPPLE : NP/NP1/NP2	* CAP : CAP/CAP1	* PLUG : PLG	* FULL COUPLING : FC	* HALF COUPLING : HF/HF1
* STUB-IN : STU	* SOCKET(HDPE/PVC) : SC	* SADDLE(HDPE) : SD	* FLANGE : F/F1	* GASKET : G/G1/G2	* BOLT & NUT : B/B1	* BLIND FLANGE : FB/FB1	* GATE VA. : VG/VG1/VG2	* BALL VA. : VB/VB1/VB1.1/VB2/VB2.0	* BUTTERFLY VA. : VF/VF4	* CHECK VA. : VC/VC1/VC2/VC3/VC4/VC5/VC6/VC7					
* GLOBE VA. : VL/VL1/VL2	* DIAPHRAGM VA. : VD/VD0	* DAMPER : VP	* QUICK COUPLING : SQC	* FLEXIBLE JOINT(STEEL) : FLXB	* FLEXIBLE JOINT(RUBBER) : FLXR	* FLEXIBLE JOINT(STEEL PTFE LINED) : FLXL	* FLEXIBLE HOSE : FLXH	* STEAM TRAP : ST	* SPRAY NOZZLE : SPN	* EMERGENCY SHOWER : SSH					
* STRAINER(Y-TYPE) : YSTR	* STRAINER(T-TYPE) : TSTR	* STRAINER(BUCKET-TYPE) : BSTR	* ANCHOR PLATE : STOP	* BIRD SCREEN : BS	* ISOLATION KIT : IK	* UNLOADING BOX : UB	* AIR TRAP : AT	* LOTO : LOTO	* SIGHT GLASS : SG	* PRESSURE GAUGE : PG	* SHILED : SH	* SPECIAL BOLT & NUT : BL/BL1			

CLIENT



4

INSULATION	CODE	C	CONDITION	PRESS. (kg/cm2g)	TEMP. (°C)	AREA W14						CONTRACTOR 	PROJECT NAME		
	THICK.	25	DESIGN	13.5	60	UNIT R1MF							M15X Ph4 Project		
			OPERATING	10	AMB	REF. PLAN DWG.						COMMODITY IW	JOB NO.		
						CJ-M15W14-PI-A30-010018-C		25.01.24	APPROVED FOR CONSTRUCTION	황래중	안남후		박동영	22330D	
						REF. P & ID	REV. NO.	DATE	DESCRIPTION	BY	CHK	APP'D	LINE NO. 40A-IW-ST1-C-7006	SH'T NO.	REV.
						CJ-M15W14-PR-A20-000503								03 / 04	0

경고 : 본 도면은 SK HYNIX의 기밀비밀 자료로서, 어떠한 경우에도 목적 외 사용, 복제, 제3자에게 공개, 누설 및 유출할 수 없으며, 회사는 유포자의 불법 사용으로 피해가 발생할 경우 유포자에게 민/형사상 책임을 요구할 수 있음.

[illegible]

<NOTE>
1. (*) FIELD ADJUST

* PIPE : P/P1	* 90° ELBOW : E90	* 45° ELBOW : E45	* TEE : T	* RED.TEE : TR	* STUB-IN : STU	* REINFORCING PAD : RP	* CON.RED : RC	* ECC.RED : RE	* CON.SWAGE : RCS/RCS1	* ECC.SWAGE : RES/RES1	* NIPPLE : NP/NP1/NP2	* CAP : CAP/CAP1	* PLUG : PLG	* FULL COUPLING : FC	* HALF COUPLING : HF/HF1
* STUB-IN : STU	* SOCKET(HDPE/PVC) : SC	* SADDLE(HDPE) : SD	* FLANGE : F/F1	* GASKET : G/G1/G2	* BOLT & NUT : B/B1	* BLIND FLANGE : FB/FB1	* GATE VA. : VG/VG1/VG2	* BALL VA. : VB/VB1/VB1.1/VB2/VB2.0	* BUTTERFLY VA. : VF/VF4	* CHECK VA. : VC/VC1/VC2/VC3/VC4/VC5/VC6/VC7					
* GLOBE VA. : VL/VL1/VL2	* DIAPHRAGM VA. : VD/VD0	* DAMPER : VP	* QUICK COUPLING : SQC	* FLEXIBLE JOINT(STEEL) : FLXB	* FLEXIBLE JOINT(RUBBER) : FLXR	* FLEXIBLE JOINT(STEEL PTFE LINED) : FLXL	* FLEXIBLE HOSE : FLXH	* STEAM TRAP : ST	* SPRAY NOZZLE : SPN	* EMERGENCY SHOWER : SSH					
* STRAINER(Y-TYPE) : YSTR	* STRAINER(T-TYPE) : TSTR	* STRAINER(BUCKET-TYPE) : BSTR	* ANCHOR PLATE : STOP	* BIRD SCREEN : BS	* ISOLATION KIT : IK	* UNLOADING BOX : UB	* AIR TRAP : AT	* LOTO : LOTO	* SIGHT GLASS : SG	* PRESSURE GAUGE : PG	* SHILED : SH	* SPECIAL BOLT & NUT : BL/BL1			



CLIENT



5

INSULATION	CODE	C	CONDITION	PRESS. (kg/cm2g)	TEMP. (°C)	AREA W14							CONTRACTOR	PROJECT NAME	
	THICK.	25	DESIGN	13.5	60	UNIT R1MF								M15X Ph4 Project	
			OPERATING	10	AMB	REF. PLAN DWG.							COMMODITY	JOB NO.	
						CJ-M15W14-PI-A30-010018-C		25.01.24	APPROVED FOR CONSTRUCTION	황래중	안남후	박동영	IW	22330D	
						REF. P & ID CJ-M15W14-PR-A20-000503		REV. NO.	DATE	DESCRIPTION	BY	CHK	APP'D	LINE NO.	SH'T NO.
													40A-IW-ST1-C-7006	04 / 04	0

경고 : 본 도면은 SK HYNIX의 기밀비밀 자료로서, 어떠한 경우에도 목적 외 사용, 복제, 제3자에게 공개, 누설 및 유통할 수 없으며, 회사는 유포자의 불법 사용으로 피해가 발생할 경우 유포자에게 민/형사상 책임을 요구할 수 있음.

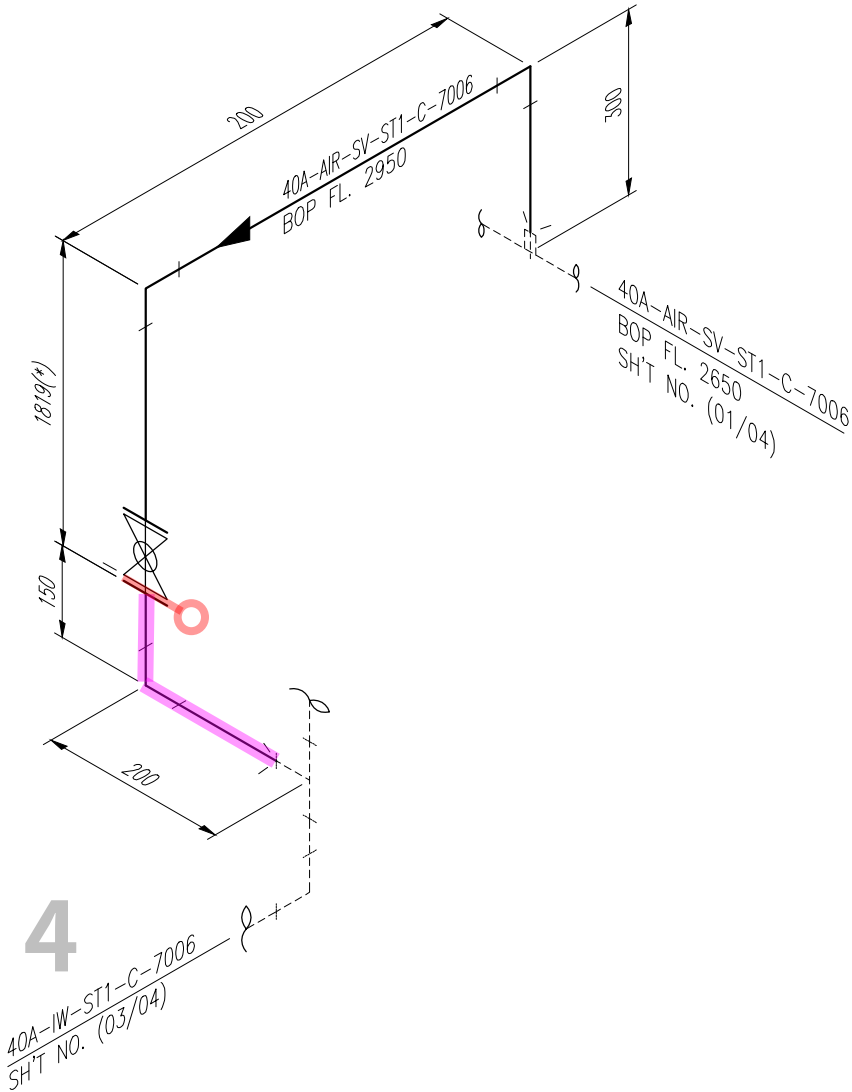
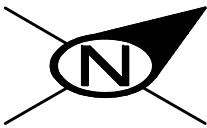


<NOTE>
1. (*) FIELD ADJUST

* PIPE : P/P1 * 90° ELBOW : E90 * 45° ELBOW : E45 * TEE : T * RED.TEE : TR * STUB-IN : STU * REINFORCING PAD : RP * CON.RED : RC * ECC.RED : RE * CON.SWAGE : RCS/RCS1 * ECC.SWAGE : RES/RES1 * NIPPLE : NP/NP1/NP2 * CAP : CAP/CAP1 * PLUG : PLG * FULL COUPLING : FC * HALF COUPLING : HF/HF1
* STUB-IN : STU * SOCKET(HDPE/PVC) : SC * SADDLE(HDPE) : SD * FLANGE : F/F1 * GASKET : G/G1/G2 * BOLT & NUT : B/B1 * BLIND FLANGE : FB/FB1 * GATE VA. : VG/VG1/VG2 * BALL VA. : VB/VBLO/VB1/VB1LO/VB2/VB2LO * BUTTERFLY VA. : VF/VF4 * CHECK VA. : VC/VC1/VC2/VC3/VC4/VC5/VC6/VC7
* GLOBE VA. : VL/VL1/VL2 * DIAPHRAGM VA. : VD/VDLO * DAMPER : VP * QUICK COUPLING : SQC * FLEXIBLE JOINT(STEEL) : FLXB * FLEXIBLE JOINT(RUBBER) : FLXR * FLEXIBLE JOINT(STEEL PTFE LINED) : FLXL * FLEXIBLE HOSE : FLXH * STEAM TRAP : ST * SPRAY NOZZLE : SPN * EMERGENCY SHOWER : SSH
* STRAINER(Y-TYPE) : YSTR * STRAINER(T-TYPE) : TSTR * STRAINER(BUCKET-TYPE) : BSTR * ANCHOR PLATE : STOP * BIRD SCREEN : BS * ISOLATION KIT : IK * UNLOADING BOX : UB * AIR TRAP : AT * LOTO : LOTO * SIGHT GLASS : SG * PRESSURE GAUGE : PG * SHILED : SH * SPECIAL BOLT & NUT : BL/BL1

INSULATION	CODE	N	CONDITION	PRESS. (kg/cm2g)	TEMP. (°C)	AREA	W14									CONTRACTOR	PROJECT NAME
	THICK.	-	DESIGN	10	60	UNIT	R1MF									SK ecoplant	M15X Ph4 Project
			OPERATING	7.5	AMB	REF. PLAN DWG.										COMMODITY	JOB NO.
						CJ-M15W14-PI-A30-010017-D										AIR-SV	22330D
						REF. P & ID										LINE NO.	SH'T NO.
						CJ-M15W14-PR-A20-000502										40A-AIR-SV-ST1-C-7006	03 / 04
																	REV.
																	0

경고 : 본 도면은 SK HYNIX의 기밀비밀 자료로서, 어떠한 경우에도 목적 외 사용, 복제, 제3자에게 공개, 누설 및 유출할 수 없으며, 회사는 유포자의 불법 사용으로 피해가 발생할 경우 유포자에게 민/형사상 책임을 요구할 수 있음.

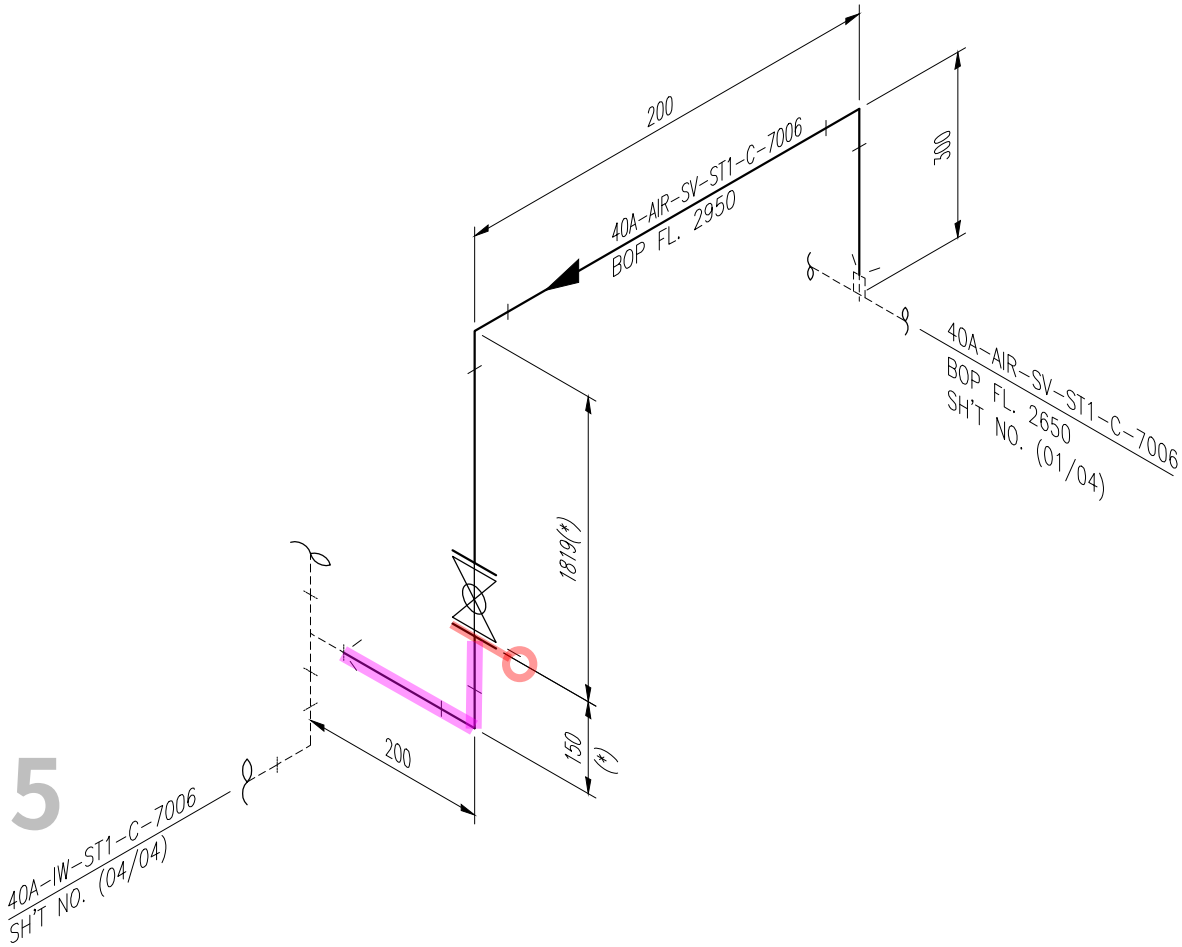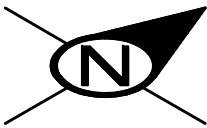

<NOTE>
1. (*) FIELD ADJUST

* PIPE : P/P1 * 90° ELBOW : E90 * 45° ELBOW : E45 * TEE : T * RED.TEE : TR * STUB-IN : STU * REINFORCING PAD : RP * CON.RED : RC * ECC.RED : RE * CON.SWAGE : RCS/RCS1 * ECC.SWAGE : RES/RES1 * NIPPLE : NP/NP1/NP2 * CAP : CAP/CAP1 * PLUG : PLG * FULL COUPLING : FC * HALF COUPLING : HF/HF1
* STUB-IN : STU * SOCKET(HDPE/PVC) : SC * SADDLE(HDPE) : SD * FLANGE : F/F1 * GASKET : G/G1/G2 * BOLT & NUT : B/B1 * BLIND FLANGE : FB/FB1 * GATE VA. : VG/VG1/VG2 * BALL VA. : VB/VBLO/VB1/VB1LO/VB2/VB2LO * BUTTERFLY VA. : VF/VF4 * CHECK VA. : VC/VC1/VC2/VC3/VC4/VC5/VC6/VC7
* GLOBE VA. : VL/VL1/VL2 * DIAPHRAGM VA. : VD/VDLO * DAMPER : VP * QUICK COUPLING : SQC * FLEXIBLE JOINT(STEEL) : FLXB * FLEXIBLE JOINT(RUBBER) : FLXR * FLEXIBLE JOINT(STEEL PTFE LINED) : FLXL * FLEXIBLE HOSE : FLXH * STEAM TRAP : ST * SPRAY NOZZLE : SPN * EMERGENCY SHOWER : SSH
* STRAINER(Y-TYPE) : YSTR * STRAINER(T-TYPE) : TSTR * STRAINER(BUCKET-TYPE) : BSTR * ANCHOR PLATE : STOP * BIRD SCREEN : BS * ISOLATION KIT : IK * UNLOADING BOX : UB * AIR TRAP : AT * LOTO : LOTO * SIGHT GLASS : SG * PRESSURE GAUGE : PG * SHILED : SH * SPECIAL BOLT & NUT : BL/BL1

INSULATION	CODE	N	CONDITION	PRESS. (kg/cm2g)	TEMP. (°C)	AREA	W14									CONTRACTOR	PROJECT NAME
	THICK.	-	DESIGN	10	60	UNIT	R1MF									SK ecoplant	M15X Ph4 Project
			OPERATING	7.5	AMB	REF. PLAN DWG.										COMMODITY	AIR-SV
						CJ-M15W14-PI-A30-010017-D										LINE NO.	40A-AIR-SV-ST1-C-7006
						REF. P & ID										SH'T NO.	04 / 04
						CJ-M15W14-PR-A20-000502										REV.	0
								REV. NO.	25.01.24	APPROVED FOR CONSTRUCTION	황래중	안남후	박동영				

경고 : 본 도면은 SK HYNIX의 기밀비밀 자료로서, 어떠한 경우에도 목적 외 사용, 복제, 제3자에게 공개, 누설 및 유출할 수 없으며, 회사는 유포자의 불법 사용으로 피해가 발생할 경우 유포자에게 민/형사상 책임을 요구할 수 있음.