



DRAWING LIST FOR TEST PACKAGE

PROJECT NO.: 22328D

PROJECT TITLE : M15X Ph2 Project

WW-SLD-606

No	PKG No	UNIT	LINE NUMBER			P&ID		REMARK
			ISO DRAWING No	SHEET	REV	P&ID No	REV	
1	606	4FA	600A-WW-SLD-ST1-N-8561-01	1 OF 1	1	CJ-M15W14-PR-A20-000112	1A	
2	606	4FA	600A-WW-SLD-ST1-N-8562-01	1 OF 1	0	CJ-M15W14-PR-A20-000112	1A	

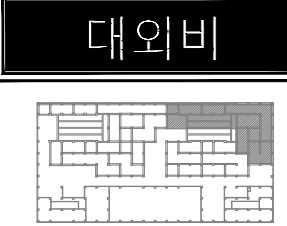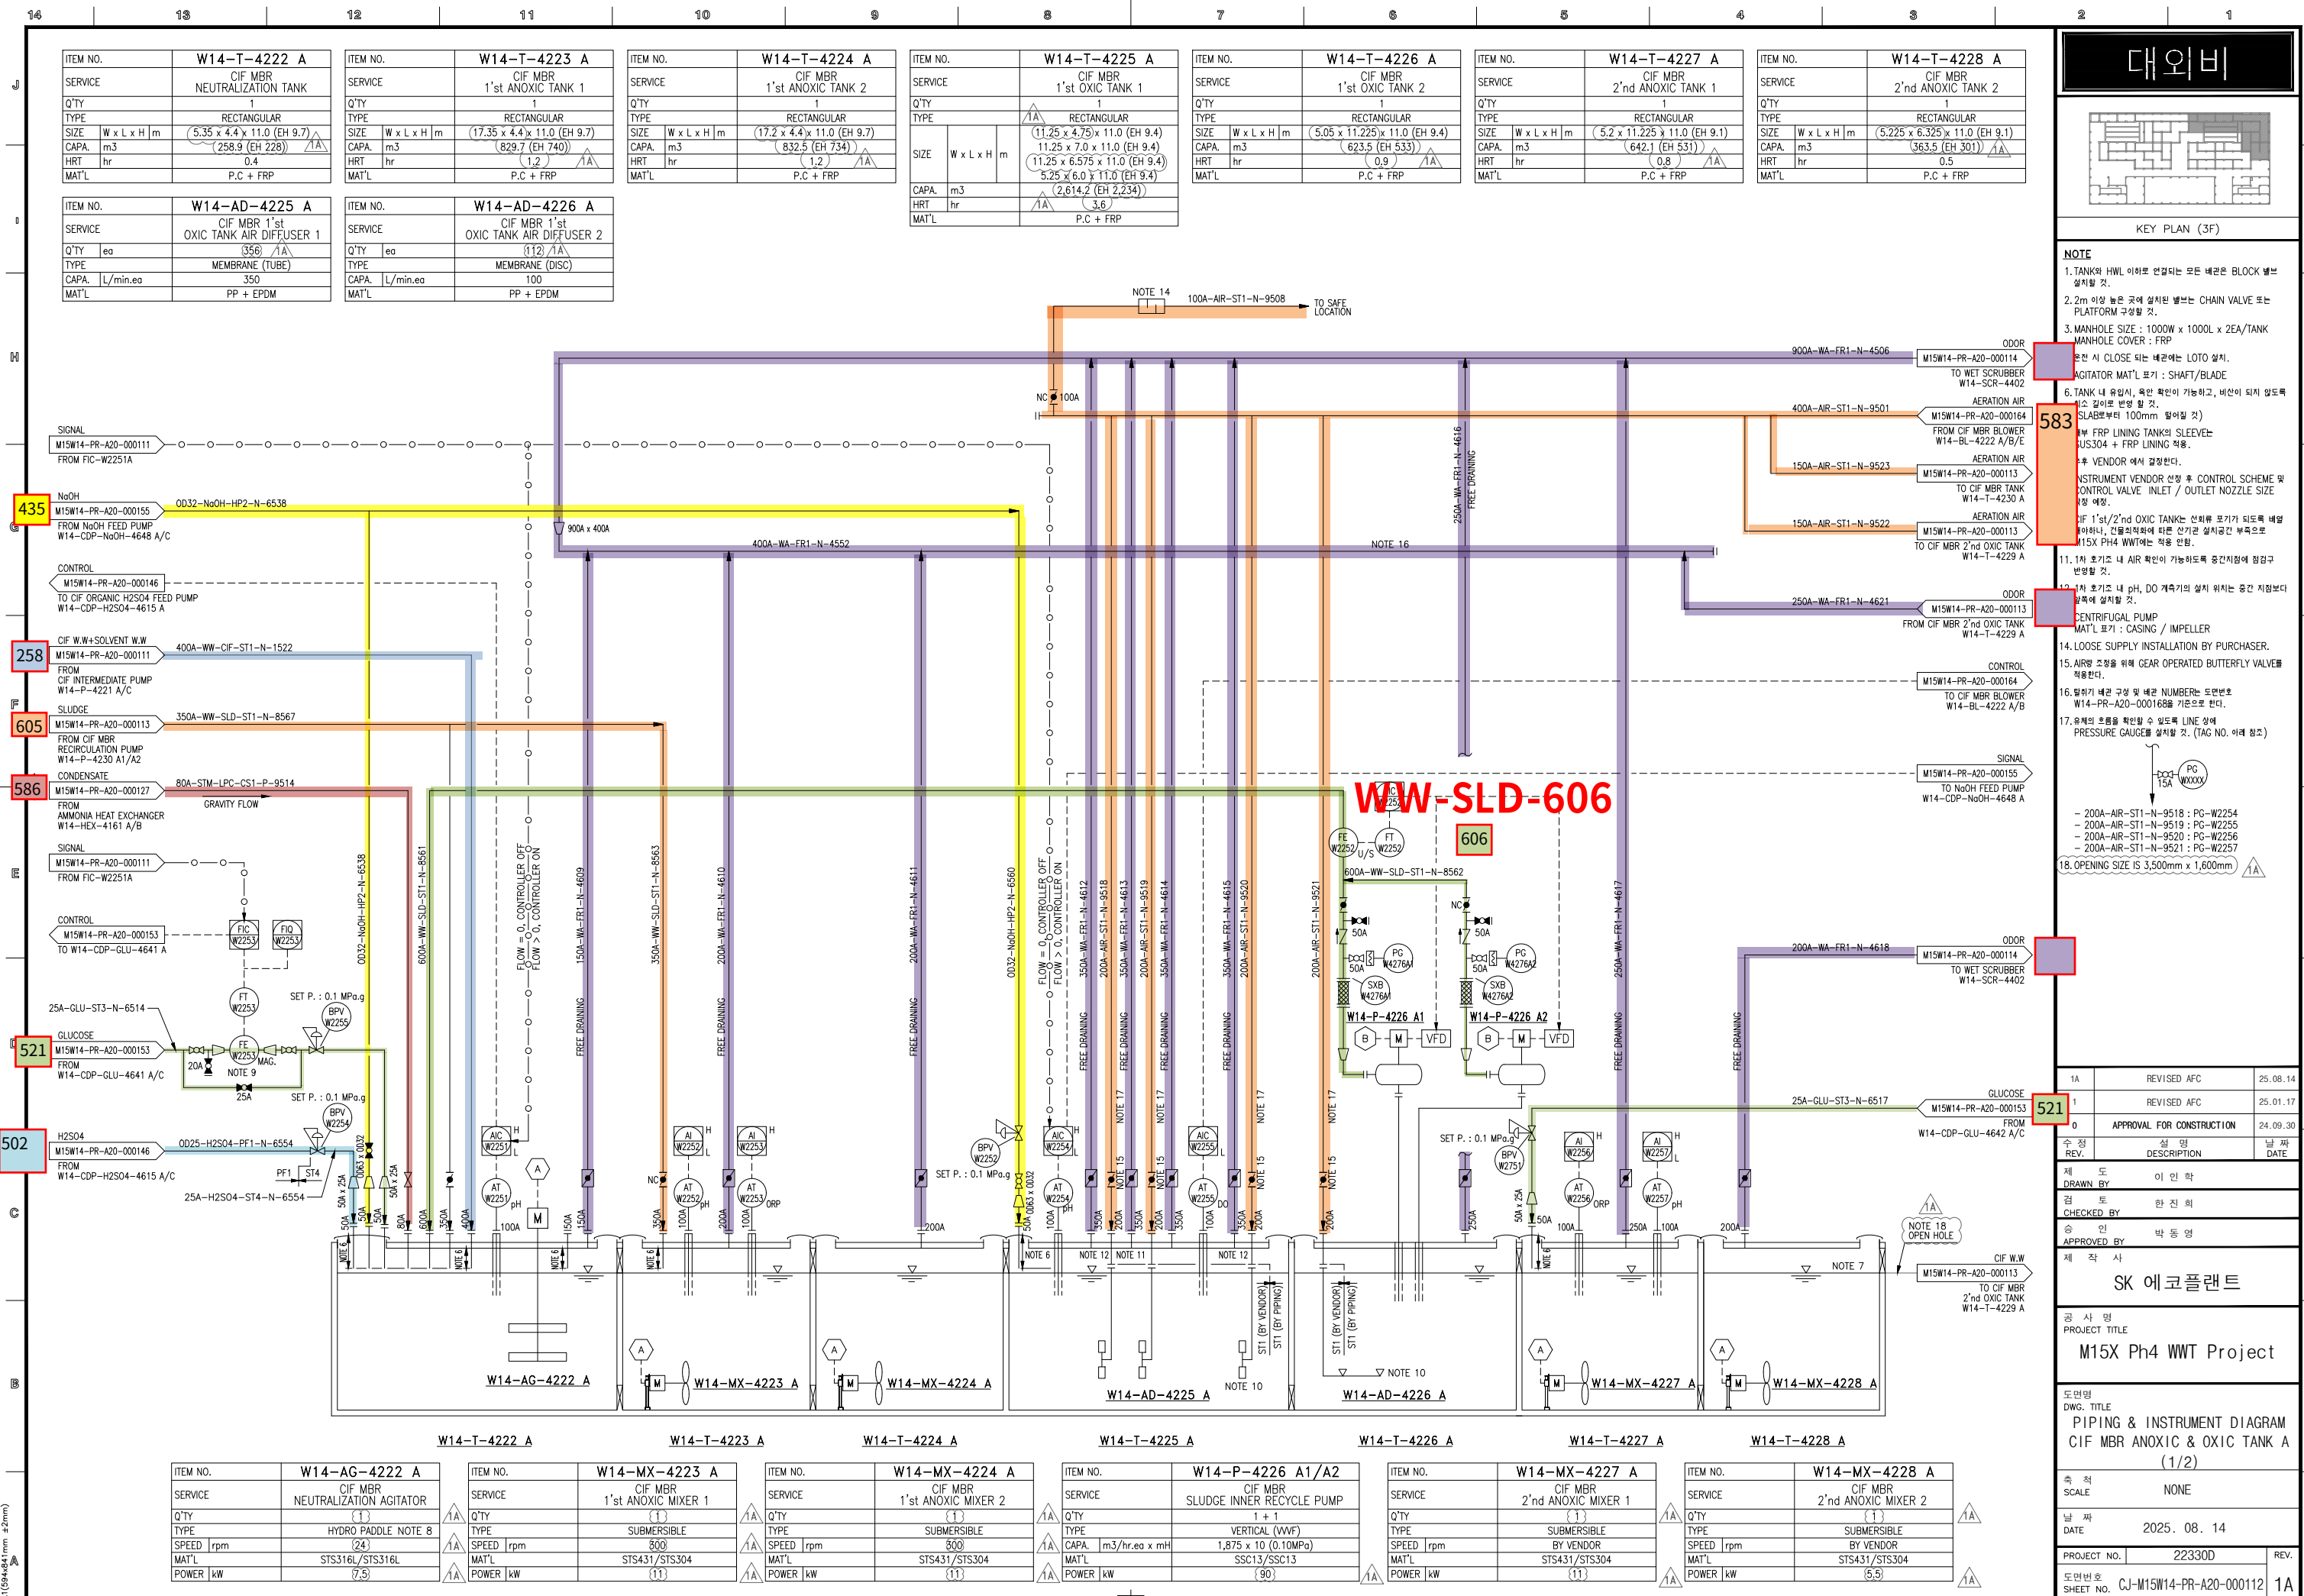

- NOTE
1. TANK의 HWL 이하로 연결되는 모든 배관은 BLOCK 별보 설치할 것.
 2. 2m 이상 높은 곳에 설치된 배관은 CHAIN VALVE 또는 PLATFORM 구성할 것.
 3. MANHOLE SIZE : 1000W x 1000L x 2EA/TANK MANHOLE COVER : FRP
 4. 운전 시 CLOSE 되는 배관에는 LOTO 설치.
 5. AGITATOR MAT'L 표기 : SHAFT/BLADE
 6. TANK 내 유입시, 폭탄 확인이 가능하고, 배선이 되지 않도록 최소 길이로 반영 할 것.
 7. FRP LINING TANK의 SLEEVE는 SUS304 + FRP LINING 적용.
 8. 이후 VENDOR 에서 결정한다.
 9. INSTRUMENT VENDOR 선정 후 CONTROL SCHEME 및 CONTROL VALVE INLET / OUTLET NOZZLE SIZE 결정.
 10. CIF 1st/2nd OXIC TANK는 전회류 포기가 되도록 배설 하여야나, 건물외벽에 따른 산기온 설치공간 부족으로 115X PH4 WWT에는 적용 안함.
 11. 1차 호기조 내 AIR 확인이 가능하도록 중간지점에 점검구 반영할 것.
 12. 1차 호기조 내 pH, DO 계측기의 설치 위치는 중간 지점보다 상부에 설치할 것.
 13. CENTRIFUGAL PUMP MAT'L 표기 : CASING / IMPELLER
 14. LOOSE SUPPLY INSTALLATION BY PURCHASER.
 15. AIR용 조정을 위해 GEAR OPERATED BUTTERFLY VALVE를 적용한다.
 16. 말리기 배관 구성 및 배관 NUMBER는 도면번호 W14-PR-A20-000168을 기준으로 한다.
 17. 유체의 흐름을 확인할 수 있도록 LINE 상에 PRESSURE GAUGE를 설치할 것. (TAG NO. 아래 참조)
 18. OPENING SIZE IS 3,500mm x 1,600mm

- 200A-AIR-ST1-N-9518 : PG-W2254
- 200A-AIR-ST1-N-9519 : PG-W2255
- 200A-AIR-ST1-N-9520 : PG-W2256
- 200A-AIR-ST1-N-9521 : PG-W2257

1A	REVISED AFC	25.08.14
1	REVISED AFC	25.01.17
0	APPROVAL FOR CONSTRUCTION	24.09.30
수정	실명	날짜
REV.	DESCRIPTION	DATE
제	도	인
DRAWN BY	이인학	
검	토	한진희
CHECKED BY		
승	인	박동영
APPROVED BY		
제	작	사

SK 에코플랜트

공	사	명
PROJECT TITLE		
M15X Ph4 WWT Project		
도면명		
DWG. TITLE		
PIPING & INSTRUMENT DIAGRAM		
CIF MBR ANOXIC & OXIC TANK A		
(1/2)		
속	척	
SCALE	NONE	
날	짜	
DATE	2025. 08. 14	
PROJECT NO.	22330D	REV.
도면번호		
SHEET NO.	CJ-M15W14-PR-A20-000112	1A

