

DRAWING LIST FOR TEST PACKAGE

PROJECT NO.: 22328D



PROJECT TITLE : M15X Ph2 Project

WW-SLD-609

No	PKG No	UNIT	LINE NUMBER			P&ID		REMARK
			ISO DRAWING No	SHEET	REV	P&ID No	REV	
1	609	4FA	600A-WW-SLD-ST1-N-8571-01	1 OF 1	0	CJ-M15W14-PR-A20-000114	1A	
2	609	4FA	600A-WW-SLD-ST1-N-8572-01	1 OF 1	0	CJ-M15W14-PR-A20-000114	1A	

ITEM NO.	W14-T-4228 B		
SERVICE	CIF MBR 2'nd ANOXIC TANK 2		
Q'TY	1		
TYPE	RECTANGULAR		
SIZE	W x L x H m	(5.35 x 5.275 x 11.0 (EH 9.1)	
CAPA.	m ³	310.4 (EH 257)	
HRT	hr	1A	0.4
MAT'L	P.C + FRP		

x 200A
 200A-WA-FR1-N-4619
 M15W14-PR-A20-0001
 FROM CIF MBR TAN
 W14-T-4230
 ODC
 200A-WA-FR1-N-4633
 M15W14-PR-A20-0001

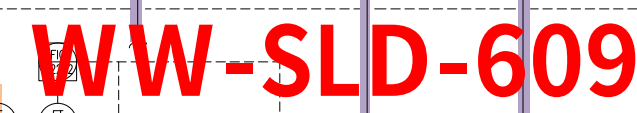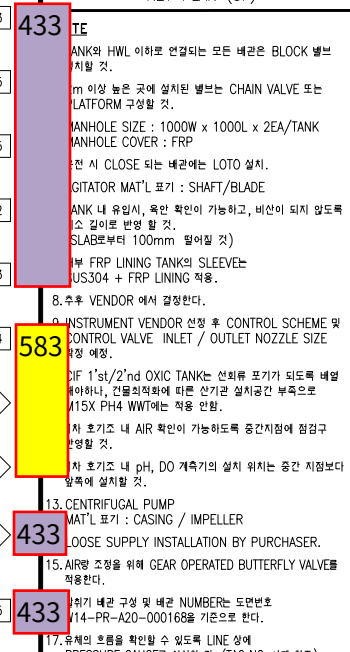

B	(2/2)
2	축척 SCALE
1A	NONE
	날짜 DATE
	2025. 08
	PROJECT NO.
	223
	도면번호

521

1A	REVISED AFC	25.08.14
1	REVISED AFC	25.08.17
0	APPROVAL FOR CONSTRUCTION	24.09.30
수정 REV.	설 명 DESCRIPTION	날 짜 DATE
제 도 DRAWN BY	이 인 학	
검 토 CHECKED BY	한 진 희	
승 인 APPROVED BY	박 동 영	
제 작 사		
SK 에코플랜트		
공 사 명 PROJECT TITLE		
M15X Ph4 WWT Project		
도면명 DWG. TITLE		
PIPING & INSTRUMENT DIAGRAM CIF MBR ANOXIC & OXIC TANK B (2/2)		
축 척 SCALE		
NONE		
날 짜 DATE		
2025. 08. 14		
PROJECT NO.		22330D
SHEET NO.		CJ-M15W14-PR-A20-000114
		REV.
		1A

