

DRAWING LIST FOR TEST PACKAGE


PROJECT NO.: 22328D

PROJECT TITLE : M15X Ph2 Project

WW-SLD-610


No	PKG No	UNIT	LINE NUMBER			P&ID		REMARK
			ISO DRAWING No	SHEET	REV	P&ID No	REV	
1	610	1FA	250A-WW-SLD-ST1-N-7017-02	2 OF 2	1	CJ-M15W14-PR-A20-000505	1A	
2	610	2FA	250A-WW-SLD-ST1-E-7017-01	1 OF 1	1	CJ-M15W14-PR-A20-000506	1A	

ITEM NO.	W14-AD-4734	
SERVICE	BRINE MBR 1 st OXIC TANK AIR DIFFUSER 1	
Q'TY	ea	70
TYPE	MEMBRANE (TUBE)	
CAPA.	L/min.ea	350
MAT'L	PP + EPDM	

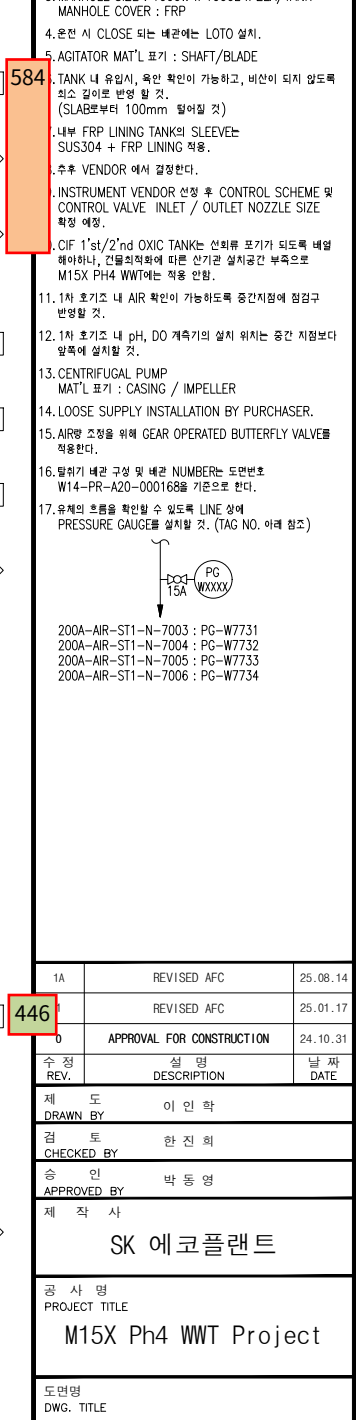

ITEM NO.	W14-MX-4736	
SERVICE	BRINE MBR 2'nd ANOXIC MIXER	
Q'TY	1	
TYPE	SUBMERSIBLE	
SPEED	rpm	(1800) 1A
MAT'L	STS431/STS304	
POWER	kW	(5.5) 1A

1A	REVISED AFC	25.08.14
6	REVISED AFC	25.01.17
0	APPROVAL FOR CONSTRUCTION	24.10.11
수 정 REV.	설 명 DESCRIPTION	날 짜 DATE
제 도 DRAWN BY	이 인 학	
검 토 CHECKED BY	한 진 희	
승 인 APPROVED BY	박 동 영	
제 작 사		
SK 에코플랜트		
공 사 명 PROJECT TITLE		
M15X Ph4 WWT Project		
도면명 DWG. TITLE		
PIPING & INSTRUMENT DIAGRAM BRINE MBR ANOXIC & OXIC TANK		
축 측 SCALE	NONE	
날 짜 DATE	2025. 08. 14	
PROJECT NO.	22330D	REV.
도면번호 SHEET NO.	CJ-M15W14-PR-A20-000505	1A

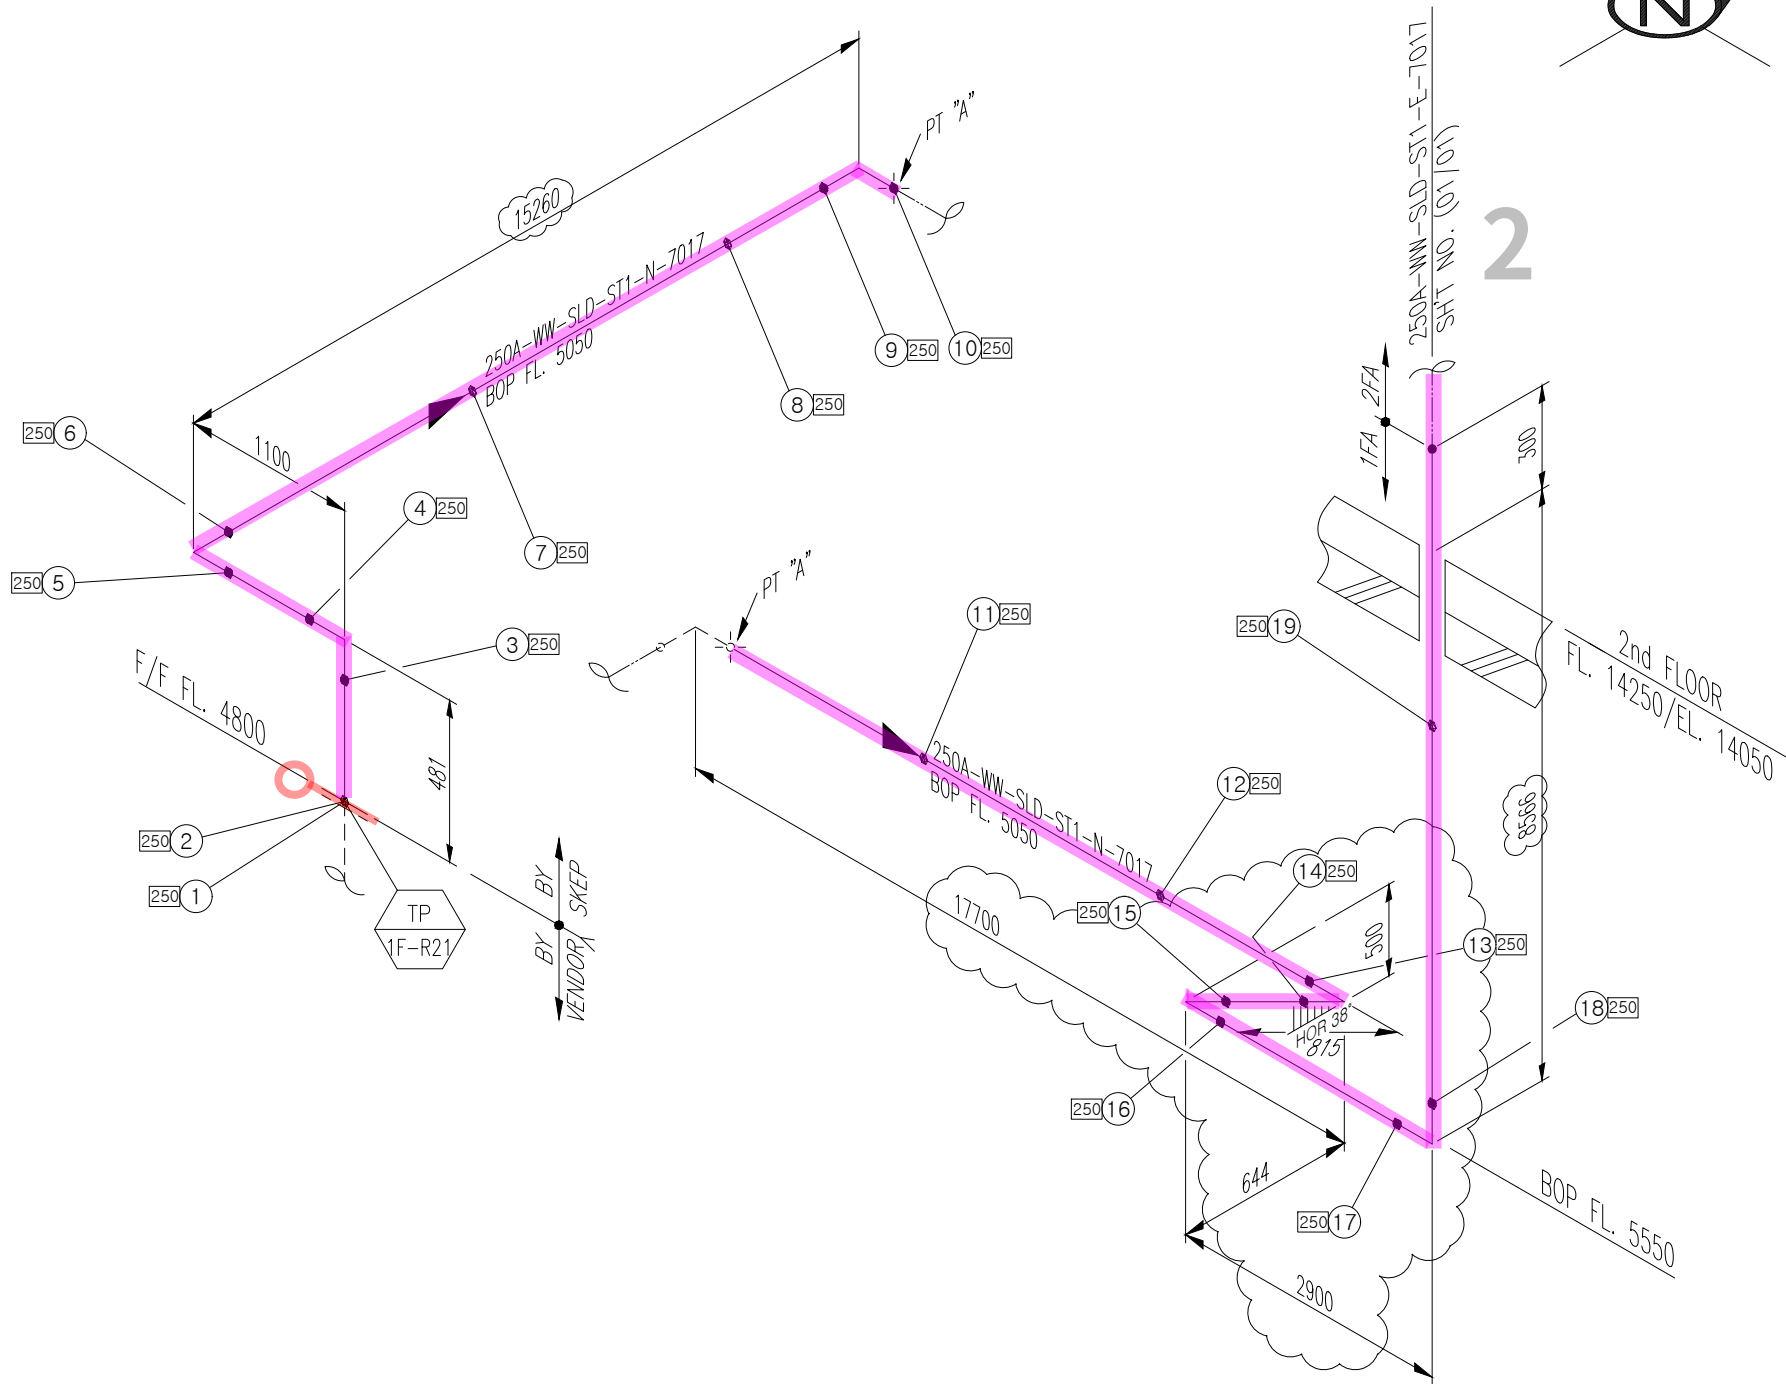

<NOTE>
1. (*) FIELD ADJUST

* PIPE : P/P1 * 90° ELBOW : E90 * 45° ELBOW : E45 * TEE : T * RED.TEE : TR * STUB-IN : STU * REINFORCING PAD : RP * CON.RED : RC * ECC.RED : RE * CON.SWAGE : RCS/RCS1 * ECC.SWAGE : RES/RES1 * NIPPLE : NP/NP1/NP2 * CAP : CAP/CAP1 * PLUG : PLG * FULL COUPLING : FC * HALF COUPLING : HF/HF1
* STUB-IN : STU * SOCKET(HDPE/PVC) : SC * SADDLE(HDPE) : SD * FLANGE : F/F1 * GASKET : G/G1/G2 * BOLT & NUT : B/B1 * BLIND FLANGE : FB/FB1 * GATE VA. : VG/VG1/VG2 * BALL VA. : VB/VBLO/VB1/VB2LO * BUTTERFLY VA. : VF/VF4 * CHECK VA. : VC/VC1/VC2/VC3/VC4/VC5/VC6/VC7
* GLOBE VA. : VL/VL1/VL2 * DIAPHRAGM VA. : VD/VDLO * DAMPER : VP * QUICK COUPLING : SQC * FLEXIBLE JOINT(STEEL) : FLXB * FLEXIBLE JOINT(RUBBER) : FLXR * FLEXIBLE JOINT(STEEL PIPE LINED) : FLXL * FLEXIBLE HOSE : FLXH * STEAM TRAP : ST * SPRAY NOZZLE : SPN * EMERGENCY SHOWER : SSH
* STRAINER(Y-TYPE) : YSTR * STRAINER(T-TYPE) : TSTR * STRAINER(BUCKET-TYPE) : BSTR * ANCHOR PLATE : STOP * BIRD SCREEN : BS * ISOLATION KIT : IK * UNLOADING BOX : UB * AIR TRAP : AT * LOTO : LOTO * SIGHT GLASS : SG * PRESSURE GAUGE : PG * SHILED : SH * SPECIAL BOLT & NUT : BL/BL1

INSULATION	CODE	N	CONDITION	PRESS. (kg/cm2g)	TEMP. (°C)	AREA	W14								CONTRACTOR	PROJECT NAME
	THICK.	—	DESIGN	6.4	60	UNIT	R1FA								M15X Ph4 Project	
			OPERATING	4	AMB	REF. PLAN DWG. CJ-M15W14-PI-A30-010016-A		1	25.03.31	REVISED AS MARKED	황래중	안남후	박동영	COMMODITY	WW-SLD	JOB NO.
						REF. P & ID CJ-M15W14-PR-A20-000506		0	25.01.24	APPROVED FOR CONSTRUCTION	황래중	안남후	박동영	LINE NO. 250A-WW-SLD-ST1-N-7017	SH'T NO. 02 / 02	REV. 1
								REV. NO.	DATE	DESCRIPTION	BY	CHK	APP'D			

경고 : 본 도면은 SK HYNIX의 기밀비밀 자료로서, 어떠한 경우에도 목적 외 사용, 복제, 제3자에게 공개, 누설 및 유출할 수 없으며, 회사는 유포자의 불법 사용으로 피해가 발생할 경우 유포자에게 민/형사상 책임을 요구할 수 있음.

