


DRAWING LIST FOR TEST PACKAGE

PROJECT NO.: 22328D

PROJECT TITLE : M15X Ph2 Project

H2SO4-617

No	PKG No	UNIT	LINE NUMBER			P&ID		REMARK
			ISO DRAWING No	SHEET	REV	P&ID No	REV	
1	617	4FA	OD25-H2SO4-PF1-N-6538-01	1 OF 2	0	CJ-M15W14-PR-A20-000145	1A	
2	617	4FA	OD25-H2SO4-PF1-N-6538-02	2 OF 2	0	CJ-M15W14-PR-A20-000145	1A	
3	617	5FA	OD25-H2SO4-PF1-N-6538-01	1 OF 1	0	CJ-M15W14-PR-A20-000145	1A	
4	617	RFA	OD25-H2SO4-PF1-E-6538-01	1 OF 1	1	CJ-M15W14-PR-A20-000145	1A	

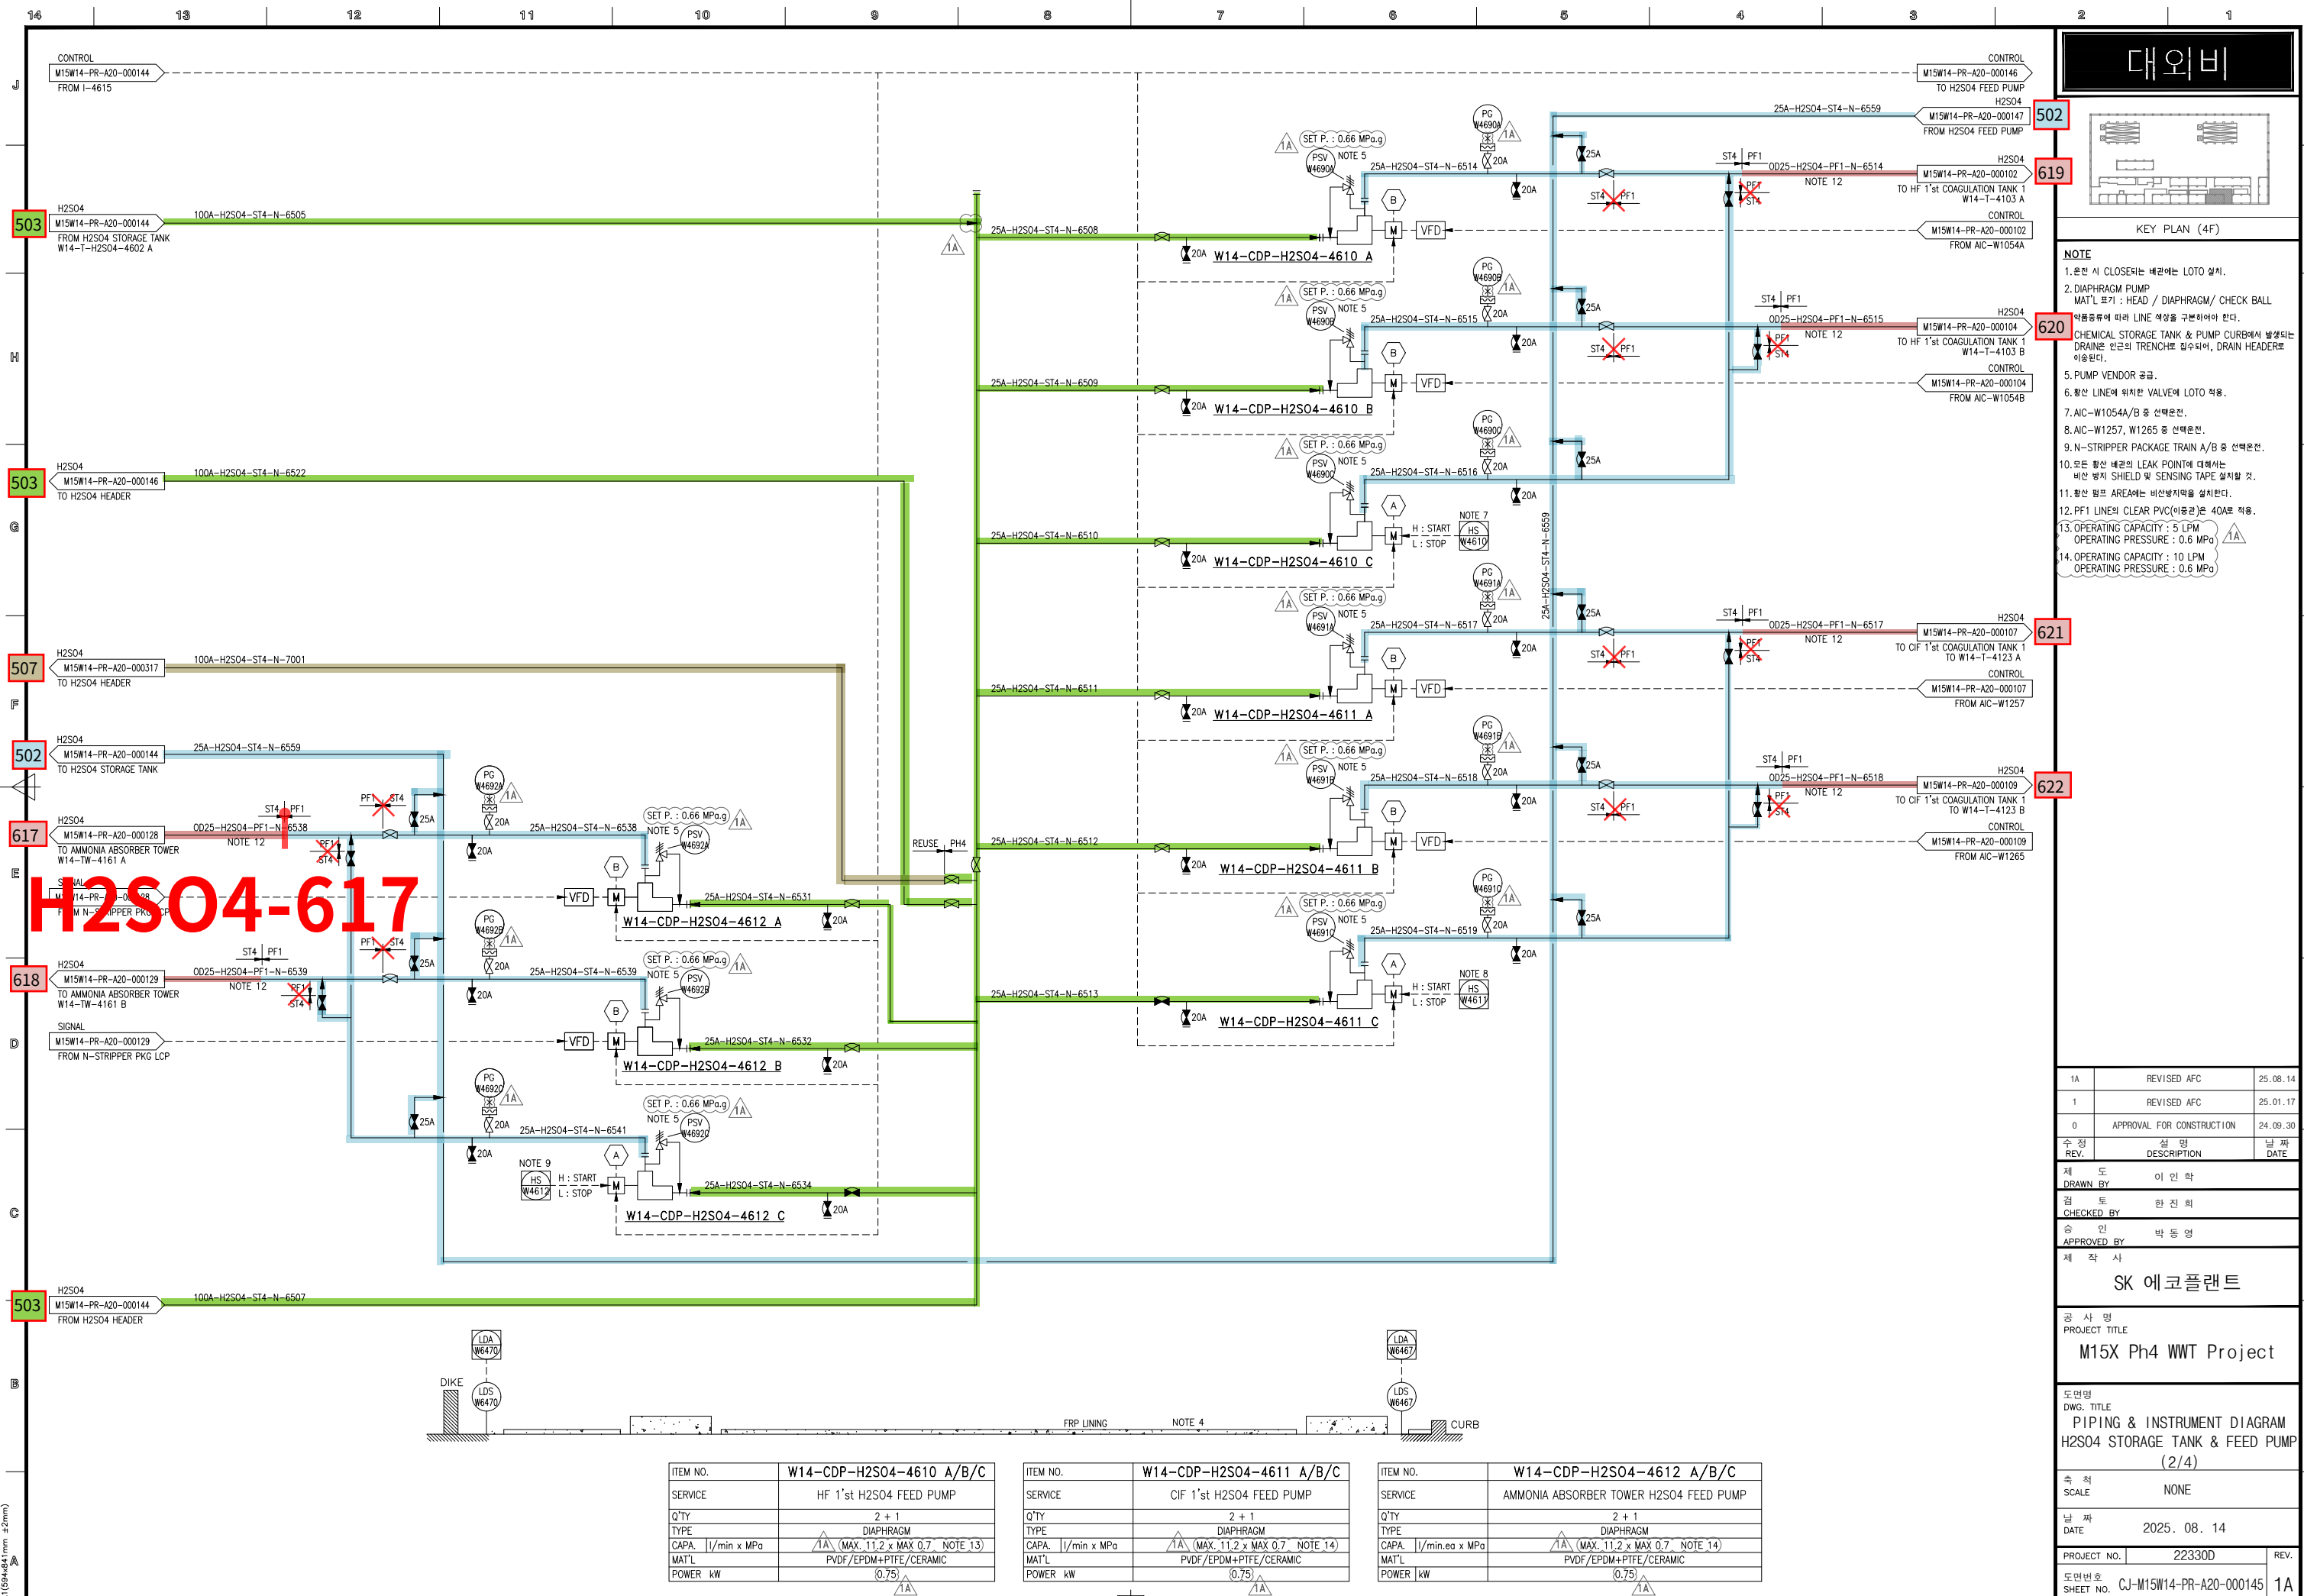

대외비

KEY PLAN (4F)

NOTE

1. 운전 시 CLOSE되는 배관에는 LOTO 설치.
2. DIAPHRAGM PUMP
MAT'L 표기 : HEAD / DIAPHRAGM/ CHECK BALL
약품종류에 따라 LINE 색상을 구분하여야 한다.
3. CHEMICAL STORAGE TANK & PUMP CURB에서 발생하는 DRAIN은 인근의 TRENCH로 침수되어, DRAIN HEADER로 이송된다.
4. 5. PUMP VENDOR 공급.
6. 황산 LINE에 위치한 VALVE에 LOTO 적용.
7. AIC-W1054A/B 중 선택운전.
8. AIC-W1257, W1265 중 선택운전.
9. N-STRIPPER PACKAGE TRAIN A/B 중 선택운전.
10. 모든 황산 배관의 LEAK POINT에 대해서는 비산 방지 SHIELD 및 SENSING TAPE 설치할 것.
11. 황산 침트 AREA에는 비산방지막을 설치한다.
12. PF1 LINE의 CLEAR PVC(이동관)은 40A로 적용.
13. OPERATING CAPACITY : 5 LPM
OPERATING PRESSURE : 0.6 MPa
14. OPERATING CAPACITY : 10 LPM
OPERATING PRESSURE : 0.6 MPa

1A	REVISED AFC	25.08.14
1	REVISED AFC	25.01.17
0	APPROVAL FOR CONSTRUCTION	24.09.30
수정	실명	날짜
REV.	DESCRIPTION	DATE
제 도	이 인 학	
DRAWN BY		
검 토	한 진 희	
CHECKED BY		
승 인	박 동 영	
APPROVED BY		
제 작 사		
SK 에코플랜트		
공 사 명	PROJECT TITLE	
M15X Ph4 WWT Project		
도면명	DWG. TITLE	
PIPING & INSTRUMENT DIAGRAM		
H2SO4 STORAGE TANK & FEED PUMP		
(2/4)		
속 측	SCALE	
NONE		
날 짜	DATE	
2025. 08. 14		
PROJECT NO.	22330D	REV.
도면번호	SHEET NO.	1A
CJ-M15W14-PR-A20-000145		

ITEM NO.	W14-CDP-H2SO4-4610 A/B/C	ITEM NO.	W14-CDP-H2SO4-4611 A/B/C	ITEM NO.	W14-CDP-H2SO4-4612 A/B/C
SERVICE	HF 1'st H2SO4 FEED PUMP	SERVICE	CIF 1'st H2SO4 FEED PUMP	SERVICE	AMMONIA ABSORBER TOWER H2SO4 FEED PUMP
Q'TY	2 + 1	Q'TY	2 + 1	Q'TY	2 + 1
TYPE	DIAPHRAGM	TYPE	DIAPHRAGM	TYPE	DIAPHRAGM
CAPA. l/min x MPa	1A (MAX. 11.2 x MAX 0.7 NOTE 13)	CAPA. l/min x MPa	1A (MAX. 11.2 x MAX 0.7 NOTE 14)	CAPA. l/min.ea x MPa	1A (MAX. 11.2 x MAX 0.7 NOTE 14)
MAT'L	PVDF/EPDM+PTFE/CERAMIC	MAT'L	PVDF/EPDM+PTFE/CERAMIC	MAT'L	PVDF/EPDM+PTFE/CERAMIC
POWER kW	(0.75)	POWER kW	(0.75)	POWER kW	(0.75)



ST4			
P	25A	0.7M	PIPE, STS 304TP+PTFE Lined, ERW – SCH 10S
T	25A	1EA	TEE EQUAL, STSF304+PTFE Lined, ERW – SCH 10S
F	25A	4EA	FLG S0, KS 10K, RF, STS304+PTFE Lined
G	25A	4EA	GASKET, KS 10K, RF, PTFE, 3.0MM TH'K
B1	25A	4SET	MACHINE BOLT & NYLON NUTS :STS 304 / W WASHERS
SH	25A	3EA	SHIELD



CLIENT  1

INSULATION	CODE	N	CONDITION	PRESS. (kg/cm2g)	TEMP. (°C)	AREA	W14							CONTRACTOR	PROJECT NAME		
	THICK.	—	DESIGN	6.7	60	UNIT	4FA								M15X Ph4 Project		
			OPERATING	6.1	AMB	REF. PLAN DWG.	CJ-M15W14-PI-A30-040013-A		25.01.24	APPROVED FOR CONSTRUCTION	황래중	안남후	박동영	COMMODITY	H2SO4	JOB NO.	
						REF. P & ID	CJ-M15W14-PR-A20-000145							REV. NO.	DATE	DESCRIPTION	BY



경고 : 본 도면은 SK HYNIX의 기업비밀 자료로서, 어떠한 경우에도 목적 외 사용, 복제, 제3자에게 공개, 누설 및 유출할 수 없으며, 회사는 유포자의 불법 사용으로 피해가 발생할 경우 유포자에게 민/형사상 책임을 요구할 수 있다.

[illegible]

INSULATION	CODE	E	CONDITION	PRESS. (kg/cm2g)	TEMP. (°C)	AREA W14						
	THICK.	25	DESIGN	6.9	60	UNIT RFA						
			OPERATING	6.2	AMB	REF. PLAN DWG. CJ-M15W14-PI-A30-R10005-A		25.03.31	REVISED AS MARKED	황래중	안남후	박동영
						REF. P & ID CJ-M15W14-PR-A20-000128		25.01.24	APPROVED FOR CONSTRUCTION	황래중	안남후	박동영
							REV. NO.	DATE	DESCRIPTION	BY	CHK	APP'D

CONTRACTOR 		PROJECT NAME M15X Ph4 Project	
COMMODITY H2SO4		JOB NO. 22330D	
LINE NO. OD25-H2SO4-PF1-E-6538	SH'T NO. 01 / 01		REV. 1