


DRAWING LIST FOR TEST PACKAGE

PROJECT NO.: 22328D

PROJECT TITLE : M15X Ph2 Project

H2SO4-626

No	PKG No	UNIT	LINE NUMBER			P&ID		REMARK
			ISO DRAWING No	SHEET	REV	P&ID No	REV	
1	626	2FA	OD25-H2SO4-PF1-N-6571-01	1 OF 2	0	CJ-M15W14-PR-A20-000147	1A	
2	626	2FA	OD25-H2SO4-PF1-N-6571-02	2 OF 2	0	CJ-M15W14-PR-A20-000121	1A	
3	626	3FA	OD25-H2SO4-PF1-N-6571-01	1 OF 1	0	CJ-M15W14-PR-A20-000147	1A	
4	626	4FA	OD25-H2SO4-PF1-N-6571-01	1 OF 2	0	CJ-M15W14-PR-A20-000121	1A	
5	626	4FA	OD25-H2SO4-PF1-N-6571-02	2 OF 2	0	CJ-M15W14-PR-A20-000147	1A	

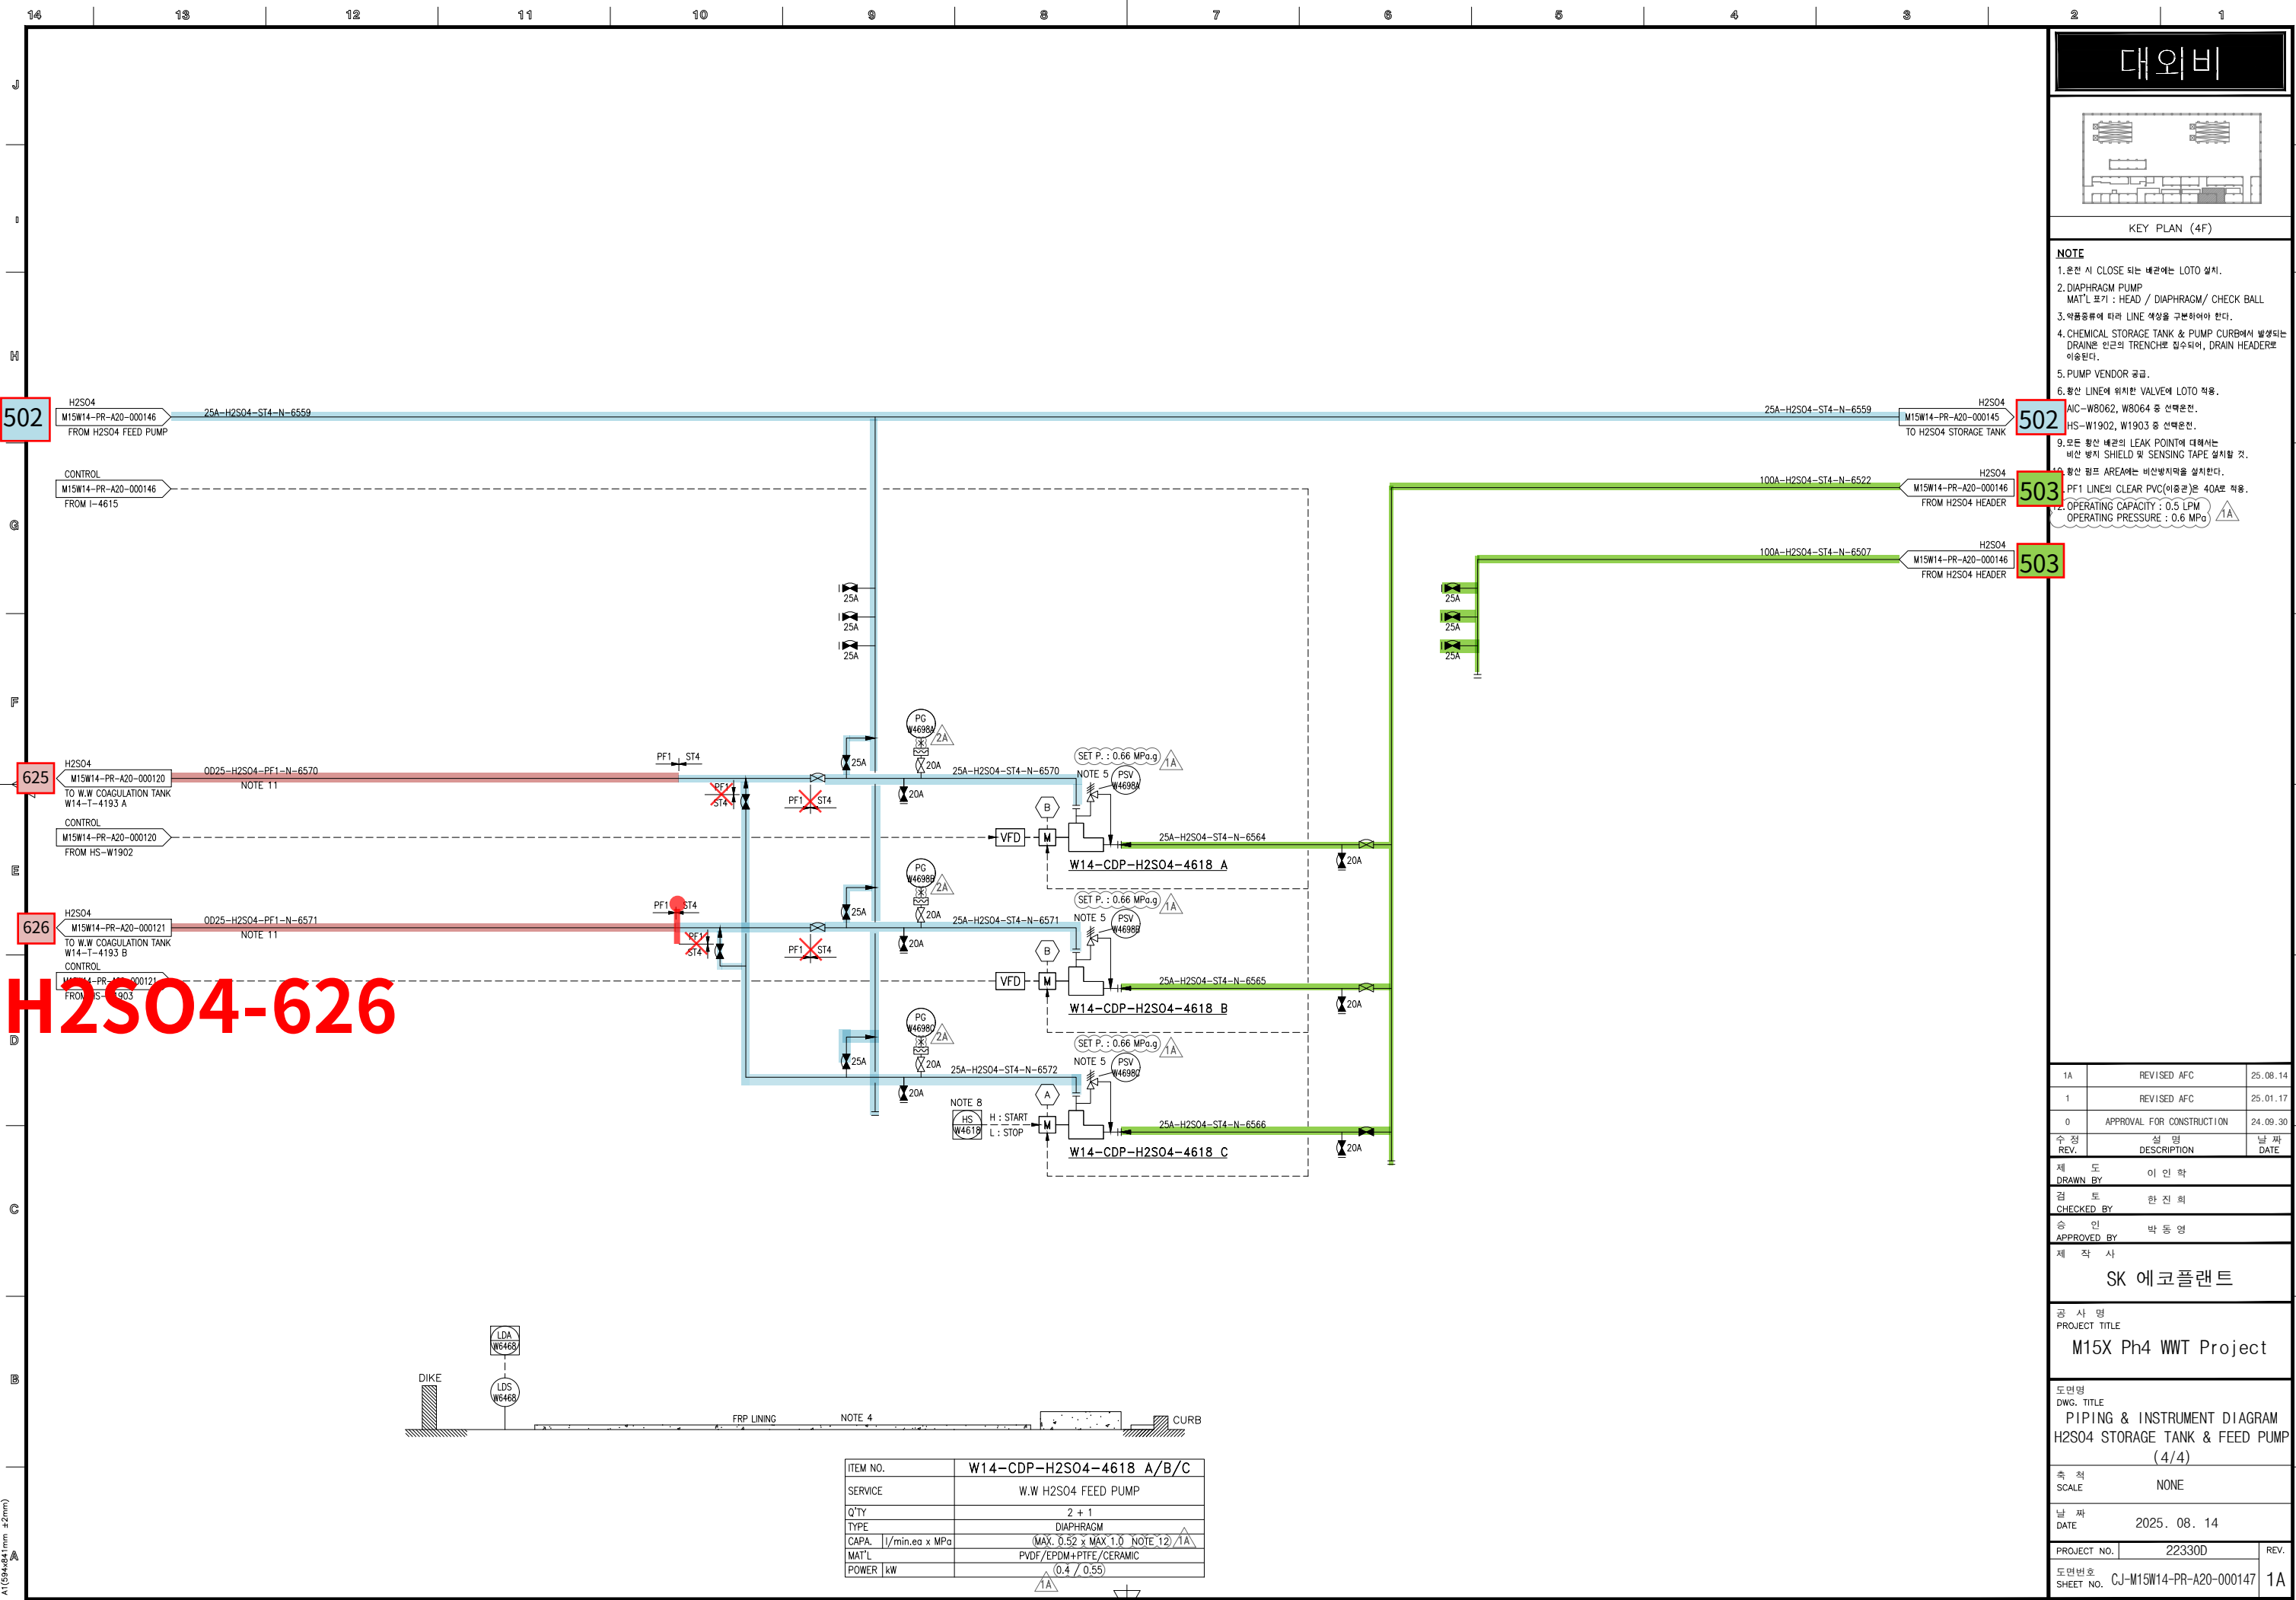

H2SO4-626


대외비

KEY PLAN (4F)

NOTE

1. 운전 시 CLOSE 되는 배관에는 LOTO 설치.
2. DIAPHRAGM PUMP
MAT'L 표기 : HEAD / DIAPHRAGM/ CHECK BALL
3. 약품종류에 따라 LINE 색상을 구분하여야 한다.
4. CHEMICAL STORAGE TANK & PUMP CURB에서 발생되는 DRAIN은 인근의 TRENCH로 집수되어, DRAIN HEADER로 이송된다.
5. PUMP VENDOR 규격.
6. 황산 LINE에 위치한 VALVE에 LOTO 적용.
AIC-W8062, W8064 중 선택은전.
7. HS-W1902, W1903 중 선택은전.
8. 모든 황산 배관의 LEAK POINT에 대해서는 비산 방지 SHIELD 및 SENSING TAPE 설치할 것.
9. 황산 침트 AREA에는 비산방지막을 설치한다.
10. PF1 LINE의 CLEAR PVC(이중관)은 40A로 적용.
11. OPERATING CAPACITY : 0.5 LPM
12. OPERATING PRESSURE : 0.6 MPa

1A	REVISED AFC	25.08.14
1	REVISED AFC	25.01.17
0	APPROVAL FOR CONSTRUCTION	24.09.30
수정 REV.	실명 DESCRIPTION	날짜 DATE
제 도	이 인 학	
DRAWN BY		
검 토	한 진 희	
CHECKED BY		
승 인	박 동 영	
APPROVED BY		
제 작 사		
SK 에코플랜트		
공 사 명	PROJECT TITLE	
M15X Ph4 WWT Project		
도면명	DWG. TITLE	
PIPING & INSTRUMENT DIAGRAM		
H2SO4 STORAGE TANK & FEED PUMP		
(4/4)		
축 척	SCALE	
NONE		
날 짜	DATE	
2025. 08. 14		
PROJECT NO.	22330D	REV.
도면번호	SHEET NO. CJ-M15W14-PR-A20-000147	
		1A

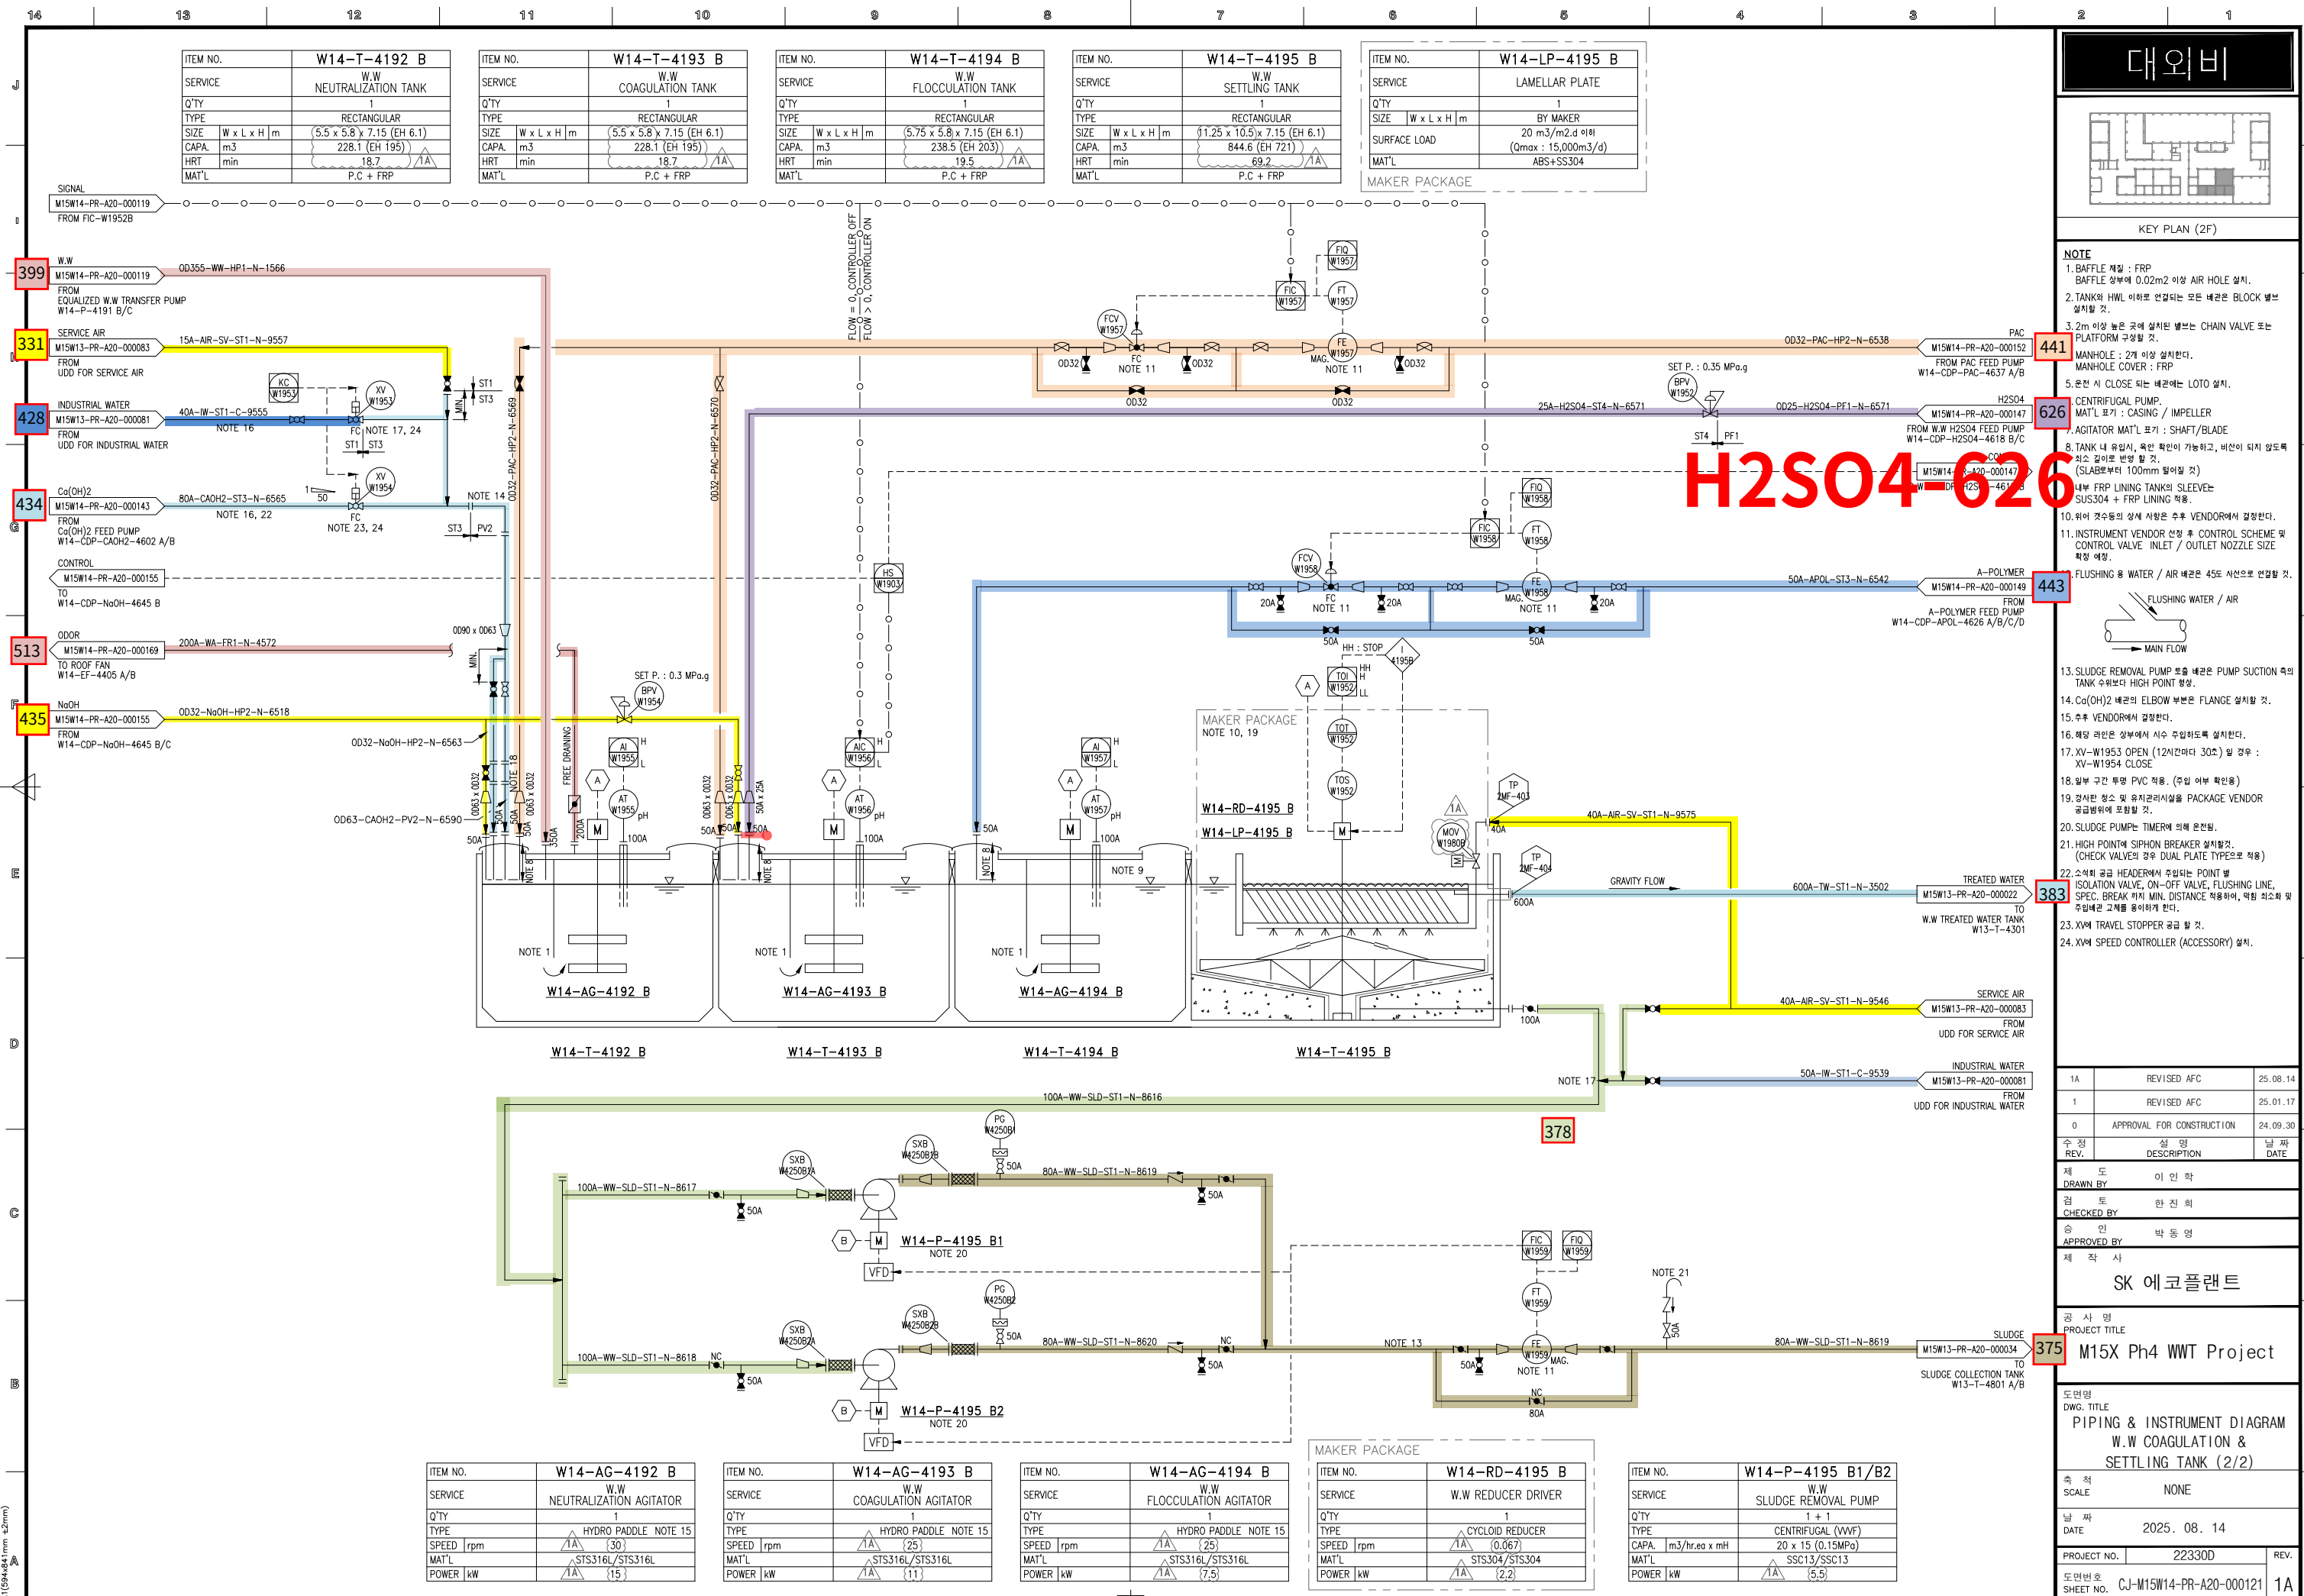

대외비

KEY PLAN (2F)

NOTE

1. Baffle 제형 : FRP
Baffle 상부에 0.02m2 이상 AIR HOLE 설치.

2. TANK의 HWL 이하로 연결되는 모든 배관은 BLOCK 밸브 설치할 것.

3. 2m 이상 높은 곳에 설치된 밸브는 CHAIN VALVE 또는 PLATFORM 구성할 것.

4. MANHOLE : 2개 이상 설치한다.
MANHOLE COVER : FRP

5. 운전 시 CLOSE 되는 배관에는 LOTO 설치.

6. CENTRIFUGAL PUMP
MAT'L 표기 : CASING / IMPELLER

7. AGITATOR MAT'L 표기 : SHAFT/BLADE

8. TANK 내 유입시, 폭탄 현상 가능하고, 비산이 되지 않도록 최소 길이로 반영 할 것.
(SLAB로부터 100mm 떨어질 것)

9. 내부 FRP LINING TANK의 SLEEVE는 SUS304 + FRP LINING 적용.

10. 위와 같은 등의 상세 사항은 추후 VENDOR에서 결정한다.

11. INSTRUMENT VENDOR 선정 후 CONTROL SCHEME 및 CONTROL VALVE INLET / OUTLET NOZZLE SIZE 확정 예정.

12. FLUSHING 용 WATER / AIR 배관은 45도 시선으로 연결할 것.

13. SLUDGE REMOVAL PUMP 배관을 PUMP SUCTION 속의 TANK 수위보다 HIGH POINT 형성.

14. Ca(OH)2 배관의 ELBOW 부분은 FLANGE 설치할 것.

15. 추후 VENDOR에서 결정한다.

16. 해당 라인은 상부에서 시스 주입하도록 설치한다.

17. XV-W1953 OPEN (12시간마다 30초) 일 경우 : XV-W1954 CLOSE

18. 일부 구간 투명 PVC 적용. (주입 여부 확인용)

19. 경사한 창고 및 유체관리시설을 PACKAGE VENDOR 공급범위에 포함할 것.

20. SLUDGE PUMP는 TIMER에 의해 운전됨.

21. HIGH POINT에 SIPHON BREAKER 설치할 것.
(CHECK VALVE의 경우 DUAL PLATE TYPE로 적용)

22. 소액의 공금 HEADER에서 주입되는 POINT 별 ISOLATION VALVE, ON-OFF VALVE, FLUSHING LINE, SPEC. BREAK 까지 MIN. DISTANCE 적용하여, 역행 회소 및 주입배관 고체를 용이하게 한다.

23. X에 TRAVEL STOPPER 공급 할 것.

24. X에 SPEED CONTROLLER (ACCESSORY) 설치.

1A

REVISED AFC

25.08.14

1

REVISED AFC

25.01.17

0

APPROVAL FOR CONSTRUCTION

24.09.30

수정

실명

날짜

REV.

DESCRIPTION

DATE

제 도

이 인 학

DRAWN BY

검 토

한 진 희

CHECKED BY

승 인

박 동 영

APPROVED BY

제 작 사

SK 에코플랜트

공 사 명

PROJECT TITLE

375

M15X Ph4 WWT Project

도면명

DWG. TITLE

PIPING & INSTRUMENT DIAGRAM

W.W COAGULATION & SETTLING TANK (2/2)

속 척

SCALE

NONE

날 짜

DATE

2025. 08. 14

PROJECT NO.

22330D

REV.

1A

도면번호

SHEET NO.

CJ-M15W14-PR-A20-000121




CLIENT		 1	
CONTRACTOR		PROJECT NAME	
		M15X Ph4 Project	
COMMODITY		JOB NO.	
H2SO4		22330D	
LINE NO.	SH'T NO.	REV.	
0D25-H2SO4-PF1-N-6571	01 / 02	0	




* PIPE : P/P1	* 90° ELBOW : E90	* 45° ELBOW : E45	* TEE : T	* RED.TEE : TR	* SUB-IN : STU	* REINFORCING PAD : RP	* CON.RED : RC	* ECC.RED : RE	* CON.SWAGE : RCS/RCS1	* ECC.SWAGE : RES/RES1	* NIPPLE : NP/NP1/NP2	* CAP : CAP/CAP1	* PLUG : PLG	* FULL COUPLING : FC	* HALF COUPLING : HF/HF1
* SUB-IN : STU	* SOCKET(HDPE/PVC) : SC	* SADDLE(HDPE) : SD	* FLANGE : F/F1	* GASKET : G/G1/G2	* BOLT & NUT : B/B1	* BLIND FLANGE : FB/FB1	* GATE VA. : VG/VG1/VG2	* BALL VA. : VB/VBLO/VB1/VBLO/VB2/VB2LO	* BUTTERFLY VA. : VF/VF4	* CHECK VA. : VC/VC1/VC2/VC3/VC4/VC5/VC6/VC7					
* GLOBE VA. : VL/VL1/VL2	* DIAPHRAGM VA. : VD/VDLO	* DAMPER : VP	* QUICK COUPLING : SQC	* FLEXIBLE JOINT(STEEL) : FLXB	* FLEXIBLE JOINT(RUBBER) : FLXR	* FLEXIBLE JOINT(STEEL PTFE LINED) : FLXL	* FLEXIBLE HOSE : FLXH	* STEAM TRAP : ST	* SPRAY NOZZLE : SPN	* EMERGENCY SHOWER : SSH					
* STRAINER(Y-TYPE) : YSTR	* STRAINER(T-TYPE) : TSTR	* STRAINER(BUCKET-TYPE) : BSTR	* ANCHOR PLATE : STOP	* BIRD SCREEN : BS	* ISOLATION KIT : IK	* UNLOADING BOX : UB	* AIR TRAP : AT	* LOTO : LOTO	* SIGHT GLASS : SG	* PRESSURE GAUGE : PG	* SHILED : SH	* SPECIAL BOLT & NUT : BL/BL1			

경고 : 본 도면은 SK HYNIX의 기밀비밀 자료로서, 어떠한 경우에도 목적 외 사용, 복제, 제3자에게 공개, 누설 및 유출할 수 없으며, 회사는 유포자의 불법 사용으로 피해가 발생할 경우 유포자에게 민/형사상 책임을 요구할 수 있음.

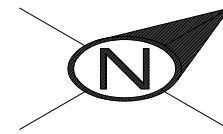

	CONTRACTOR		PROJECT NAME	
			M15X Ph4 Project	
	COMMODITY	H2SO4	JOB NO.	
02			22330D	
D	LINE NO.	0D25-H2SO4-PF1-N-6571	SH'T NO. 01 / 02	REV. 0

INSULATION	CODE	N	CONDITION	PRESS. (kg/cm2g)	TEMP. (°C)	AREA W14						
	THICK.	-	DESIGN	6.7	60	UNIT 4FA						
			OPERATING	6.1	AMB	REF. PLAN DWG. CJ-M15W14-PI-A30-040012-A						
						REF. P & ID CJ-M15W14-PR-A20-000145		25.01.24	APPROVED FOR CONSTRUCTION	황래중	안남후	박동
							REV. NO.	DATE	DESCRIPTION	BY	CHK	APP

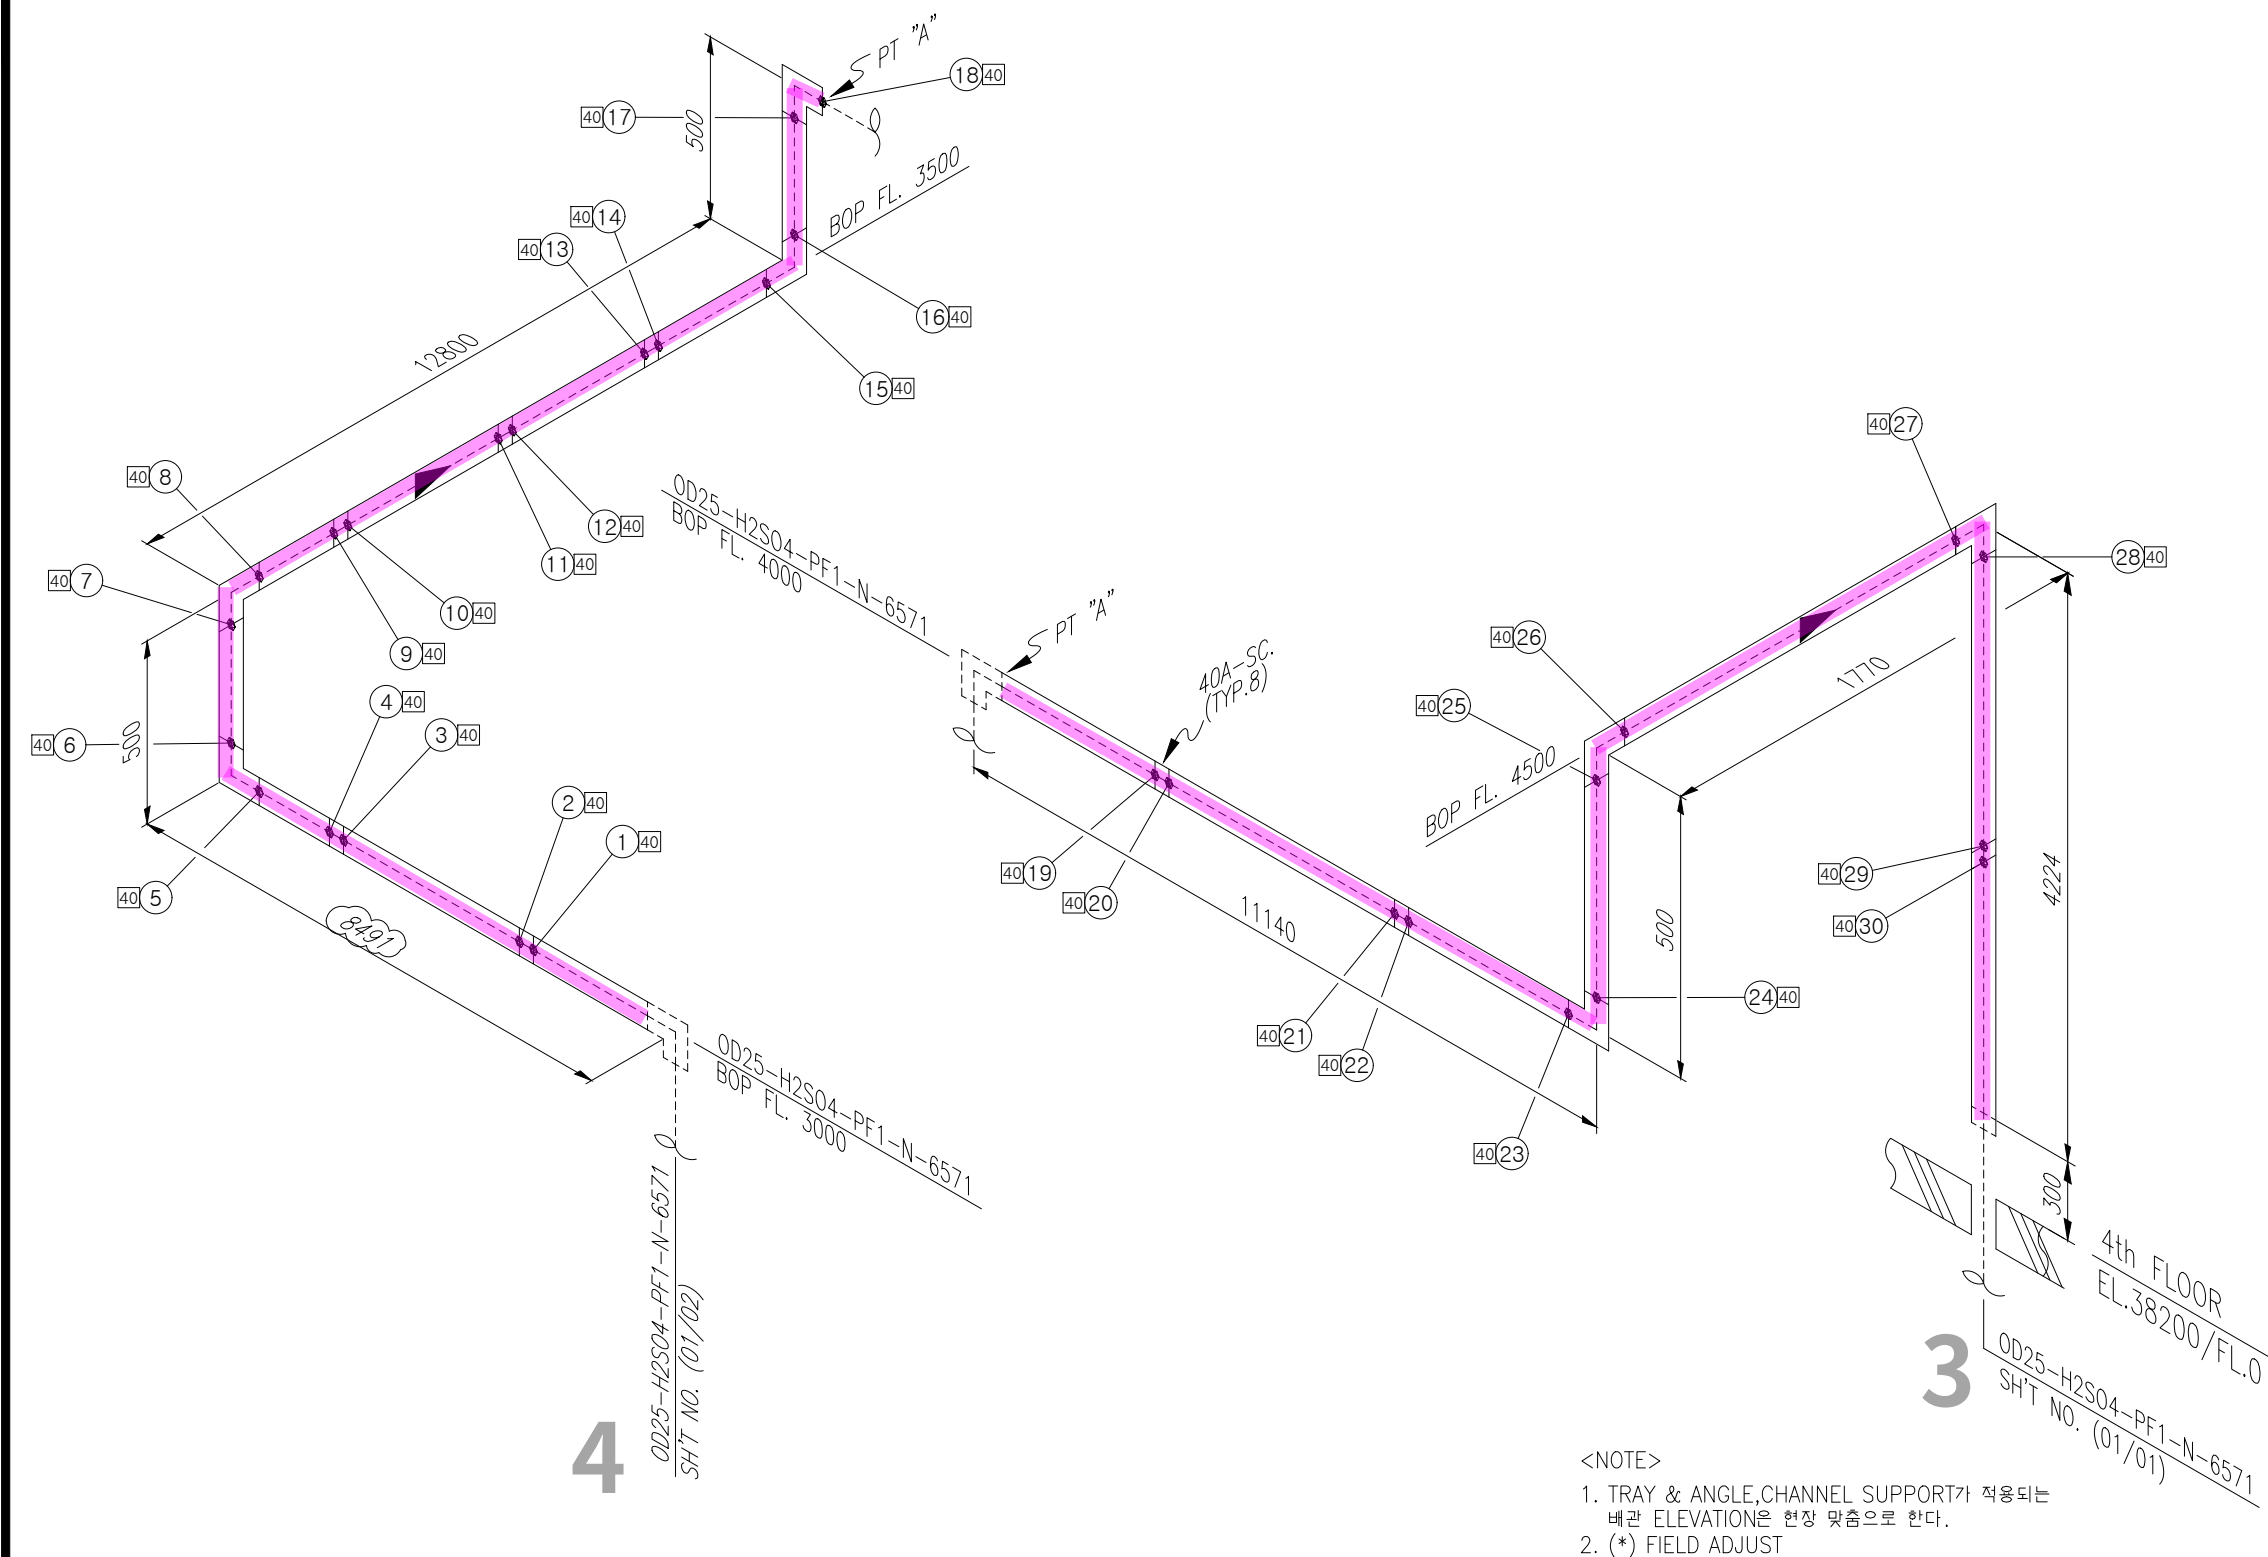

CLIENT  5

경고 : 본 도면은 SK HYNIX의 기업비밀 자료로서, 어떠한 경우에도 목적 외 사용, 복제, 제3자에게 공개, 누설 및 유출할 수 없으며, 회사는 유포자의 불법 사용으로 피해가 발생할 경우 유포자에게 민/형사상 책임을 요구할 수 있음