

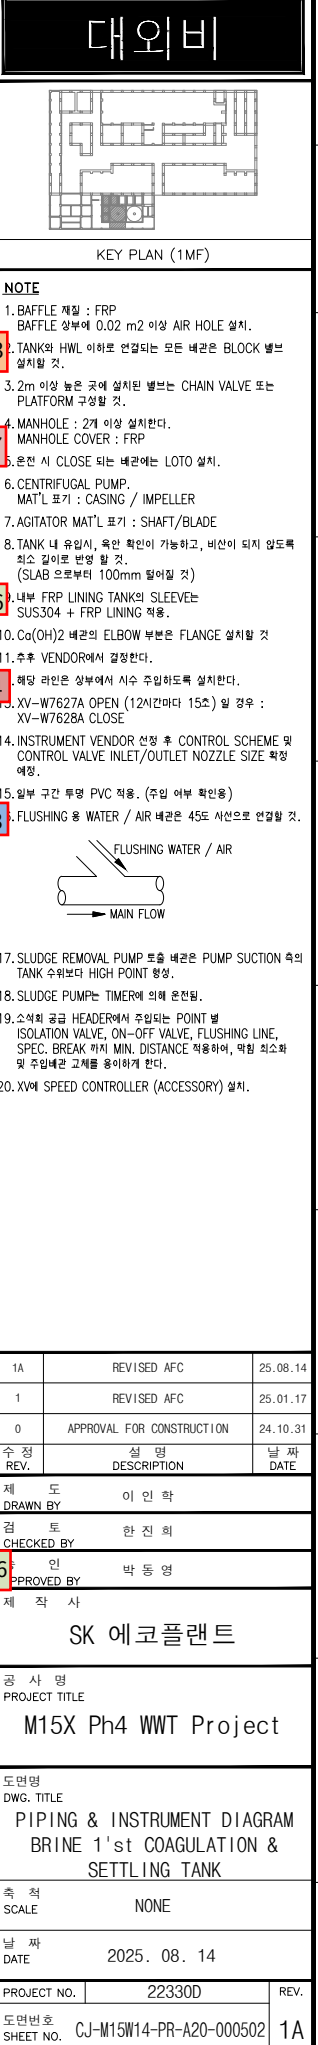


PROJECT TITLE : M15X Ph2 Project[illegible]

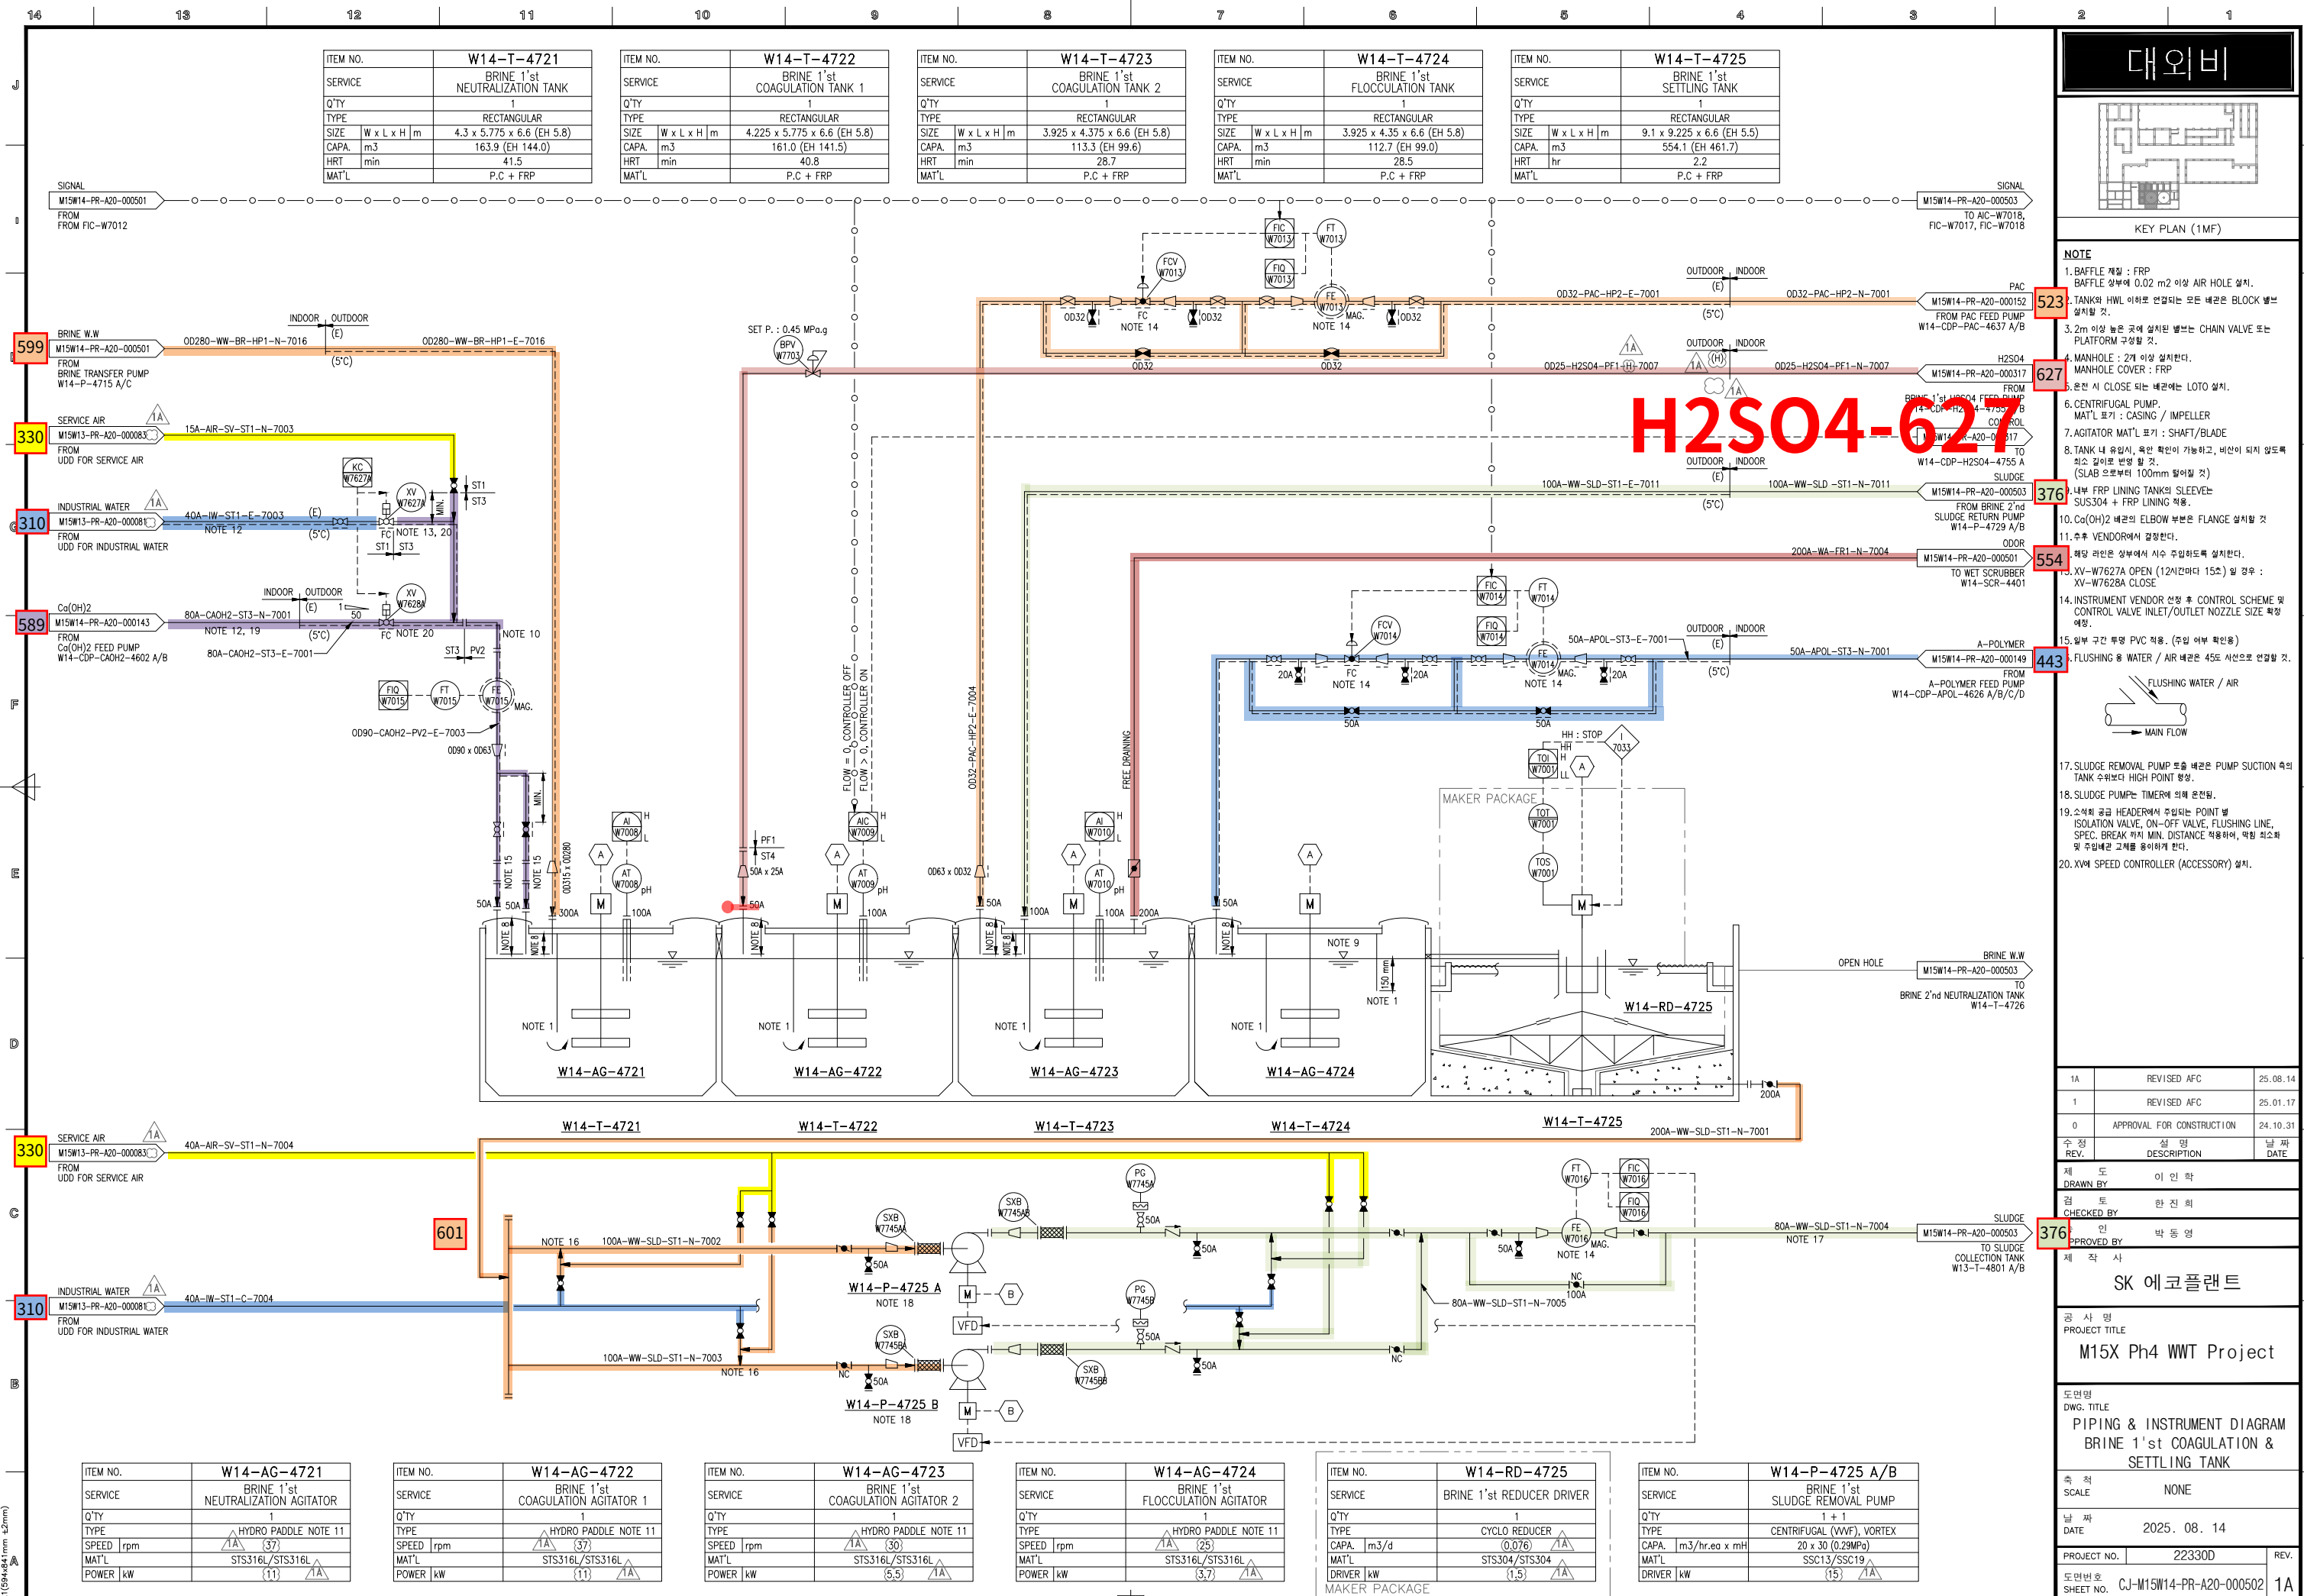

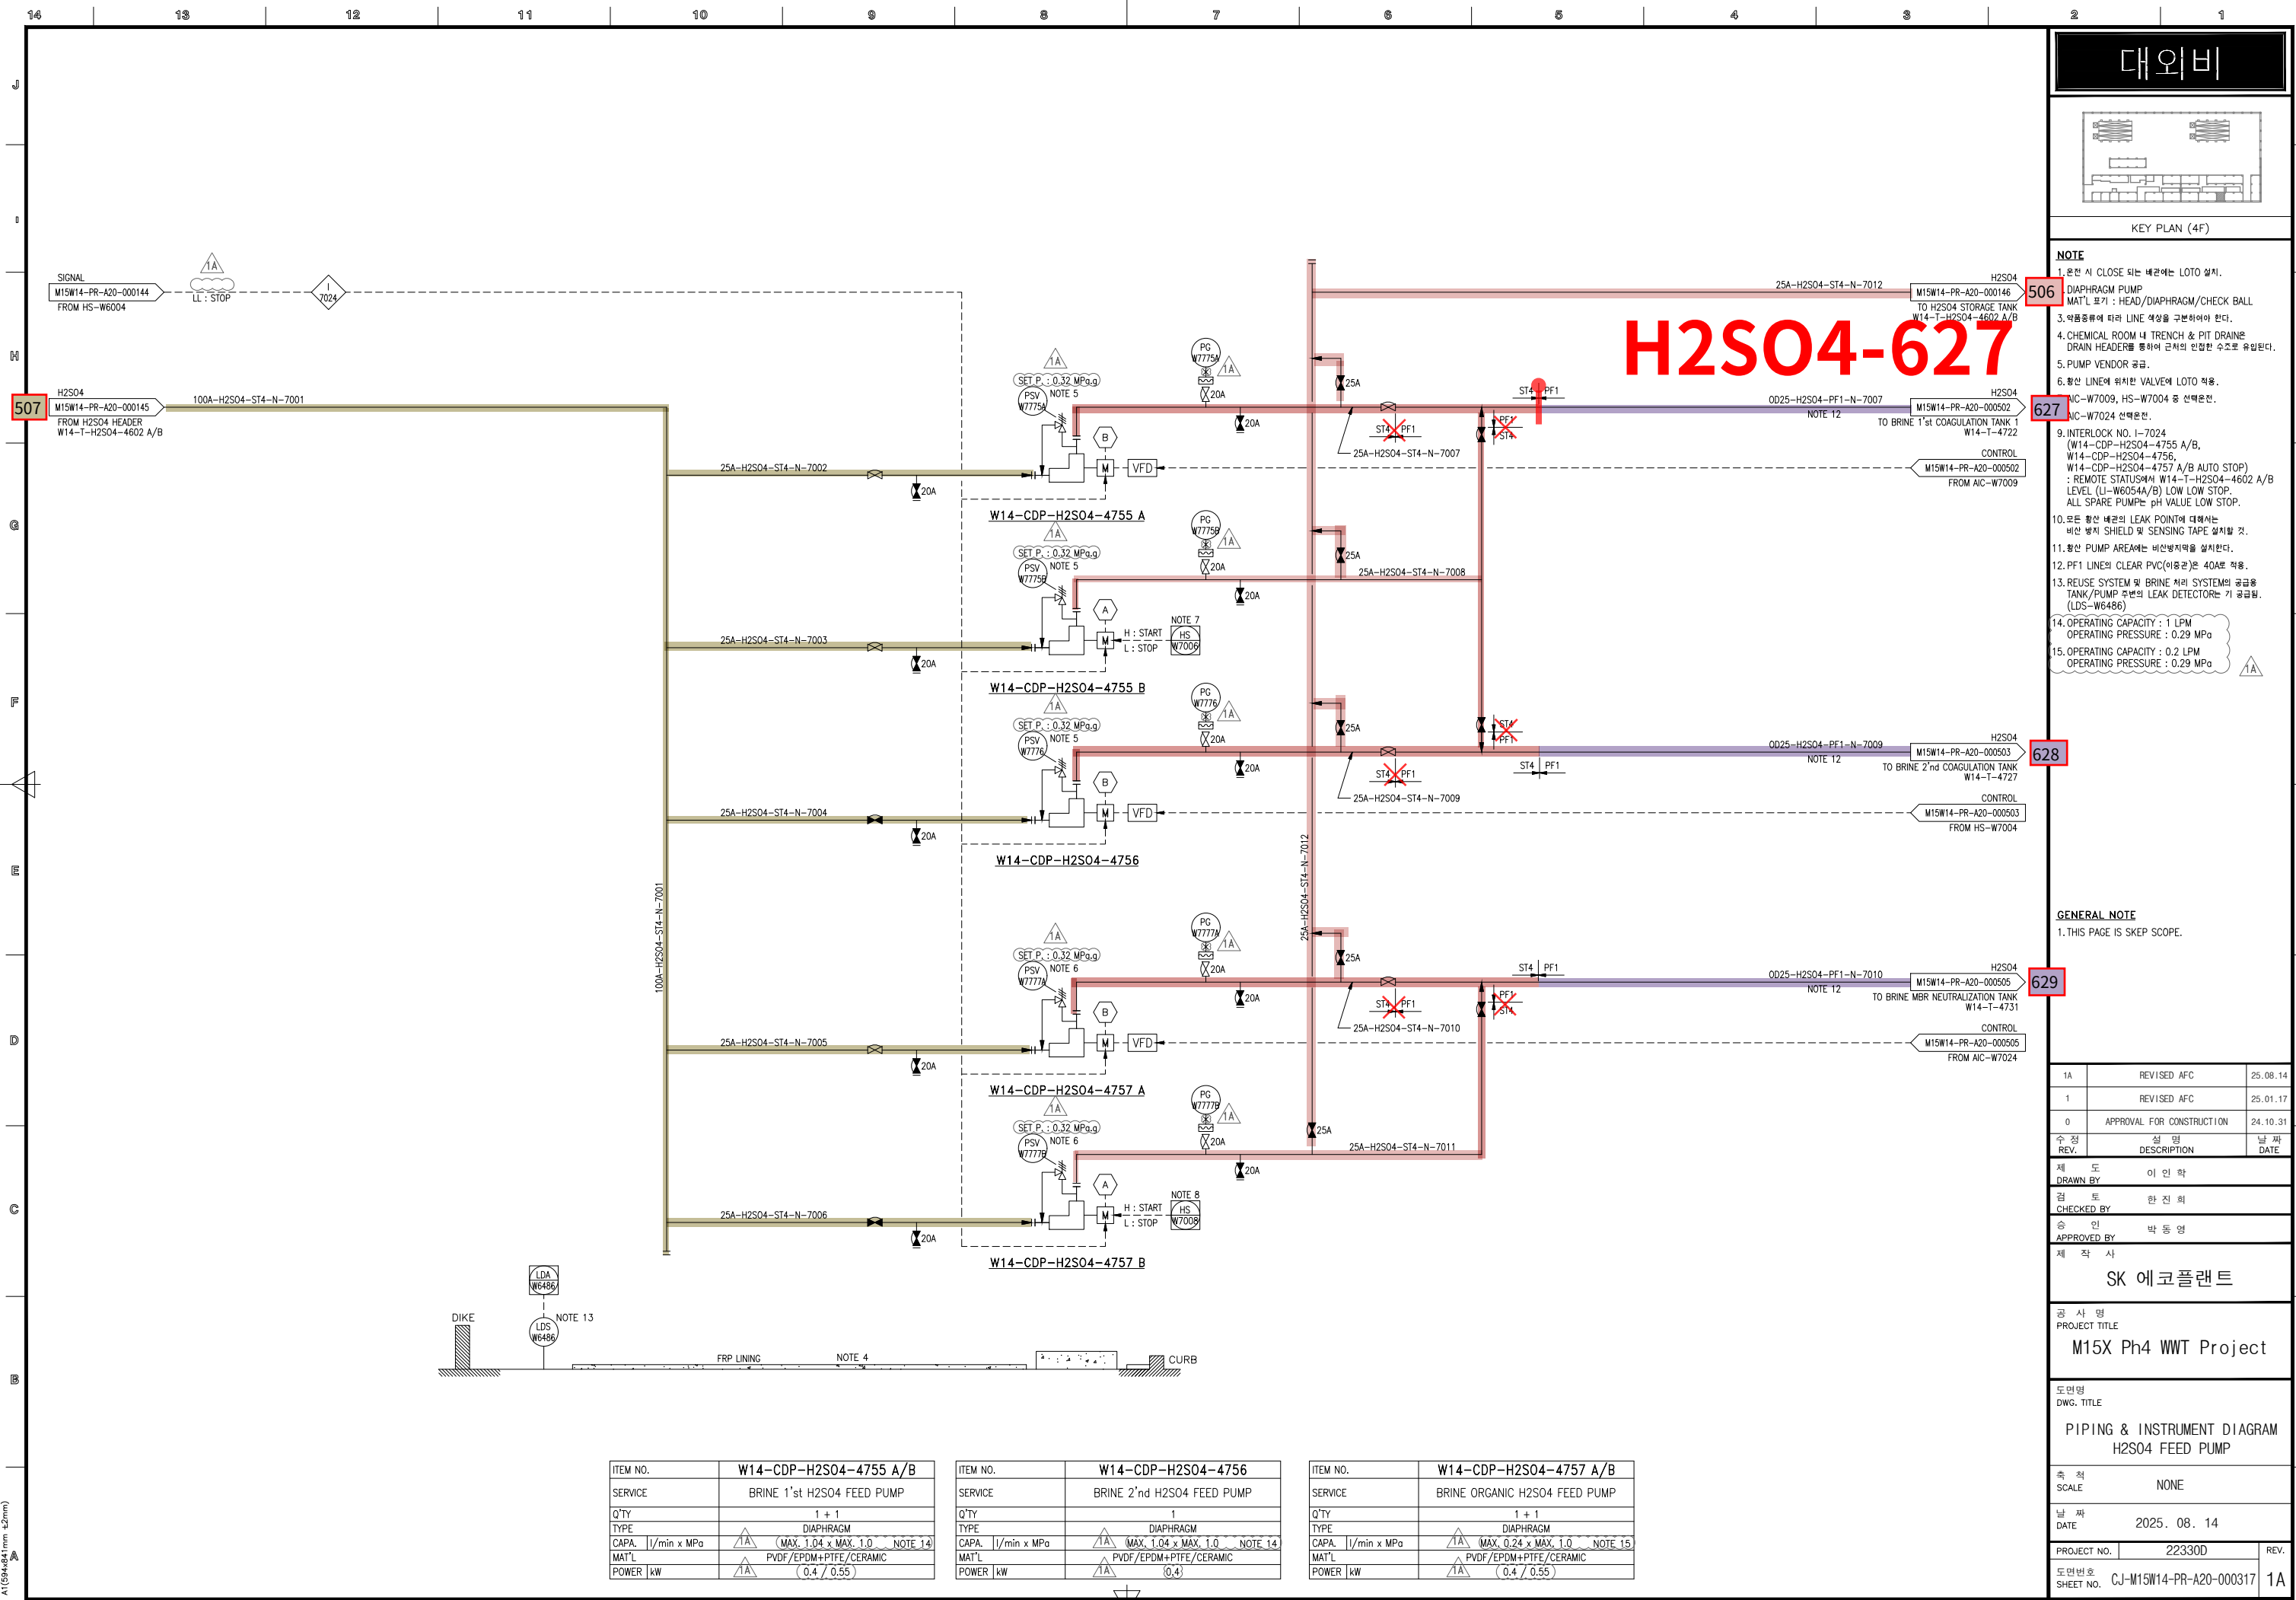

대외비

KEY PLAN (4F)

- NOTE**
1. 운전 시 CLOSE 되는 배관에는 LOTO 설치.
 2. DIAPHRAGM PUMP MAT'L 표기 : HEAD/DIAPHRAGM/CHECK BALL
 3. 약품종류에 따라 LINE 역상을 구분하여야 한다.
 4. CHEMICAL ROOM 내 TRENCH & PIT DRAIN은 DRAIN HEADER를 통하여 근처의 인접한 수조로 유입된다.
 5. PUMP VENDOR 공급.
 6. 황산 LINE에 위치한 VALVE에 LOTO 적용.
 7. AIC-W7009, HS-W7004 중 선택운전.
 8. AIC-W7024 선택운전.
 9. INTERLOCK NO. I-7024 (W14-CDP-H2SO4-4755 A/B, W14-CDP-H2SO4-4756, W14-CDP-H2SO4-4757 A/B AUTO STOP) : REMOTE STATUS에서 W14-T-H2SO4-4602 A/B LEVEL (LI-W6054A/B) LOW LOW STOP. ALL SPARE PUMP는 pH VALUE LOW STOP.
 10. 모든 황산 배관의 LEAK POINT에 대해서는 비산 방지 SHIELD 및 SENSING TAPE 설치할 것.
 11. 황산 PUMP AREA에는 비산방지막을 설치한다.
 12. PF1 LINE의 CLEAR PVC(이음관)은 40A를 적용.
 13. REUSE SYSTEM 및 BRINE 처리 SYSTEM의 공급용 TANK/PUMP 주변에 LEAK DETECTOR는 기 공급됨. (LDS-W6486)
 14. OPERATING CAPACITY : 1 LPM
OPERATING PRESSURE : 0.29 MPa
 15. OPERATING CAPACITY : 0.2 LPM
OPERATING PRESSURE : 0.29 MPa

GENERAL NOTE

1. THIS PAGE IS SKEP SCOPE.

1A	REVISED AFC	25.08.14
1	REVISED AFC	25.01.17
0	APPROVAL FOR CONSTRUCTION	24.10.31
수정 REV.	설명 DESCRIPTION	날짜 DATE

제 도 이 인 학
DRAWN BY
검 토 한 진 희
CHECKED BY
승 인 박 동 명
APPROVED BY

제 작 사
SK 에코플랜트

공 사 명
PROJECT TITLE
M15X Ph4 WWT Project

도면명
DWG. TITLE
PIPING & INSTRUMENT DIAGRAM
H2SO4 FEED PUMP

속 척
SCALE
NONE


날 짜
DATE
2025. 08. 14


PROJECT NO. 22330D
도면번호
SHEET NO. CJ-M15W14-PR-A20-000317
REV. 1A

ITEM NO.	W14-CDP-H2SO4-4755 A/B
SERVICE	BRINE 1 st H2SO4 FEED PUMP
Q'TY	1 + 1
TYPE	DIAPHRAGM
CAPA. l/min x MPa	1A (MAX. 1.04 x MAX. 1.0) NOTE 14
MAT'L	PVDF/EPDM+PTFE/CERAMIC
POWER kW	1A (0.4 / 0.55)

ITEM NO.	W14-CDP-H2SO4-4756
SERVICE	BRINE 2 nd H2SO4 FEED PUMP
Q'TY	1
TYPE	DIAPHRAGM
CAPA. l/min x MPa	1A (MAX. 1.04 x MAX. 1.0) NOTE 14
MAT'L	PVDF/EPDM+PTFE/CERAMIC
POWER kW	1A (0.4)

ITEM NO.	W14-CDP-H2SO4-4757 A/B
SERVICE	BRINE ORGANIC H2SO4 FEED PUMP
Q'TY	1 + 1
TYPE	DIAPHRAGM
CAPA. l/min x MPa	1A (MAX. 0.24 x MAX. 1.0) NOTE 15
MAT'L	PVDF/EPDM+PTFE/CERAMIC
POWER kW	1A (0.4 / 0.55)

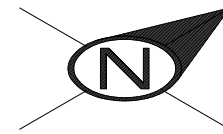

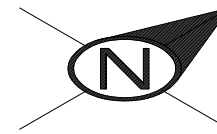

1. TRAY & ANGLE, CHANNEL SUPPORT가 적용되는 배관 ELEVATION은 현장 맞춤으로 한다.
2. (*) FIELD ADJUST

CLIENT  3

경고 : 본 도면은 SK HYNIX의 기밀비밀 자료로서, 어떠한 경우에도 무단의 사용, 복제, 제3자에게 공개, 누설 및 유출할 수 없으며, 회사는 유포자의 무단 사용으로 피해가 발생할 경우 유포자에게 민/형사상 책임을 요구할 수 있음.



<NOTE>

1. TRAY & ANGLE, CHANNEL SUPPORT가 적용되는 배관 ELEVATION은 현장 맞춤으로 한다.
2. H2SO4 배관의 입상/윙관에는 비산/낙수 방지를 위한 투명 PVC 보호판(5T)을 설치하고 누출방지를 위해 Silicon 마감처리를 한다.
3. (*) FIELD ADJUST

* PIPE : P/P1	* 90° ELBOW : E90	* 45° ELBOW : E45	* TEE : T	* RED.TEE : TR	* STUB-IN : STU	* REINFORCING PAD : RP	* CON.RED : RC	* ECC.RED : RE	* CON.SWAGE : RCS/RCS1	* ECC.SWAGE : RES/RES1	* NIPPLE : NP/NP1/NP2	* CAP : CAP/CAP1	* PLUG : PLG	* FULL COUPLING : FC	* HALF COUPLING : HF/HF1
* STUB-IN : STU	* SOCKET(HDPE/PVC) : SC	* SADDLE(HDPE) : SD	* FLANGE : F/F1	* GASKET : G/G1/G2	* BOLT & NUT : B/B1	* BLIND FLANGE : FB/FB1	* GATE VA. : VG/VG1/VG2	* BALL VA. : VB/VB1/VB10/VB2/VB210	* BUTTERFLY VA. : VF/VF4	* CHECK VA. : VC/VC1/VC2/VC3/VC4/VC5/VC6/VC7					
* GLOBE VA. : VL/VL1/VL2	* DIAPHRAGM VA. : VD/VD10	* DAMPER : VP	* QUICK COUPLING : SQC	* FLEXIBLE JOINT(STEEL) : FLXB	* FLEXIBLE JOINT(RUBBER) : FLXR	* FLEXIBLE JOINT(STEEL PTFE LINED) : FLXL	* FLEXIBLE HOSE : FLXH	* STEAM TRAP : ST	* SPRAY NOZZLE : SPN	* EMERGENCY SHOWER : SSH					
* STRAINER(Y-TYPE) : YSTR	* STRAINER(T-TYPE) : TSTR	* STRAINER(BUCKET-TYPE) : BSTR	* ANCHOR PLATE : STOP	* BIRD SCREEN : BS	* ISOLATION KIT : IK	* UNLOADING BOX : UB	* AIR TRAP : AT	* LOTO : LOTO	* SIGHT GLASS : SG	* PRESSURE GAUGE : PG	* SHILED : SH	* SPECIAL BOLT & NUT : BL/BL1			

INSULATION	CODE	E	CONDITION	PRESS. (kg/cm ² g)	TEMP. (*C)	AREA W14							CONTRACTOR 	PROJECT NAME	
	THICK.	-	DESIGN	6.4	60	UNIT R2FA								M15X Ph4 Project	
			OPERATING	4	AMB	REF. PLAN DWG. CJ-M15W14-PI-A30-020016-C		25.03.31	REVISED AS MARKED	황래중	안남후	박동영	COMMODITY H2SO4	JOB NO.	
						REF. P & ID CJ-M15W14-PR-A20-000502		25.01.24	APPROVED FOR CONSTRUCTION	황래중	안남후	박동영	LINE NO. OD25-H2S04-PF1-E-7007	22330D	
							REV. NO.	DATE	DESCRIPTION	BY	CHK	APP'D		SH'T NO. 01 / 01	REV. 1

경고 : 본 도면은 SK HYNIX의 기밀비밀 자료로서, 어떠한 경우에도 목적 외 사용, 복제, 제3자에게 공개, 누설 및 유출할 수 없으며, 회사는 유포자의 불법 사용으로 피해가 발생할 경우 유포자에게 민/형사상 책임을 요구할 수 있음