


DRAWING LIST FOR TEST PACKAGE

PROJECT NO.: 22328D

PROJECT TITLE : M15X Ph2 Project

H2SO4-628

No	PKG No	UNIT	LINE NUMBER			P&ID		REMARK
			ISO DRAWING No	SHEET	REV	P&ID No	REV	
1	628	2FA	OD25-H2SO4-PF1-N-7009-01	1 OF 1	0	CJ-M15W14-PR-A20-000317/503	1A/1A	
2	628	3FA	OD25-H2SO4-PF1-N-7009-01	1 OF 1	0	CJ-M15W14-PR-A20-000317/503	1A/1A	
3	628	4FA	OD25-H2SO4-PF1-N-7009-01	1 OF 2	0	CJ-M15W14-PR-A20-000317/503	1A/1A	
4	628	4FA	OD25-H2SO4-PF1-N-7009-02	2 OF 2	0	CJ-M15W14-PR-A20-000317/503	1A/1A	
5	628	R2FA	OD25-H2SO4-PF1-E-7009-01	1 OF 1	1	CJ-M15W14-PR-A20-000317/503	1A/1A	

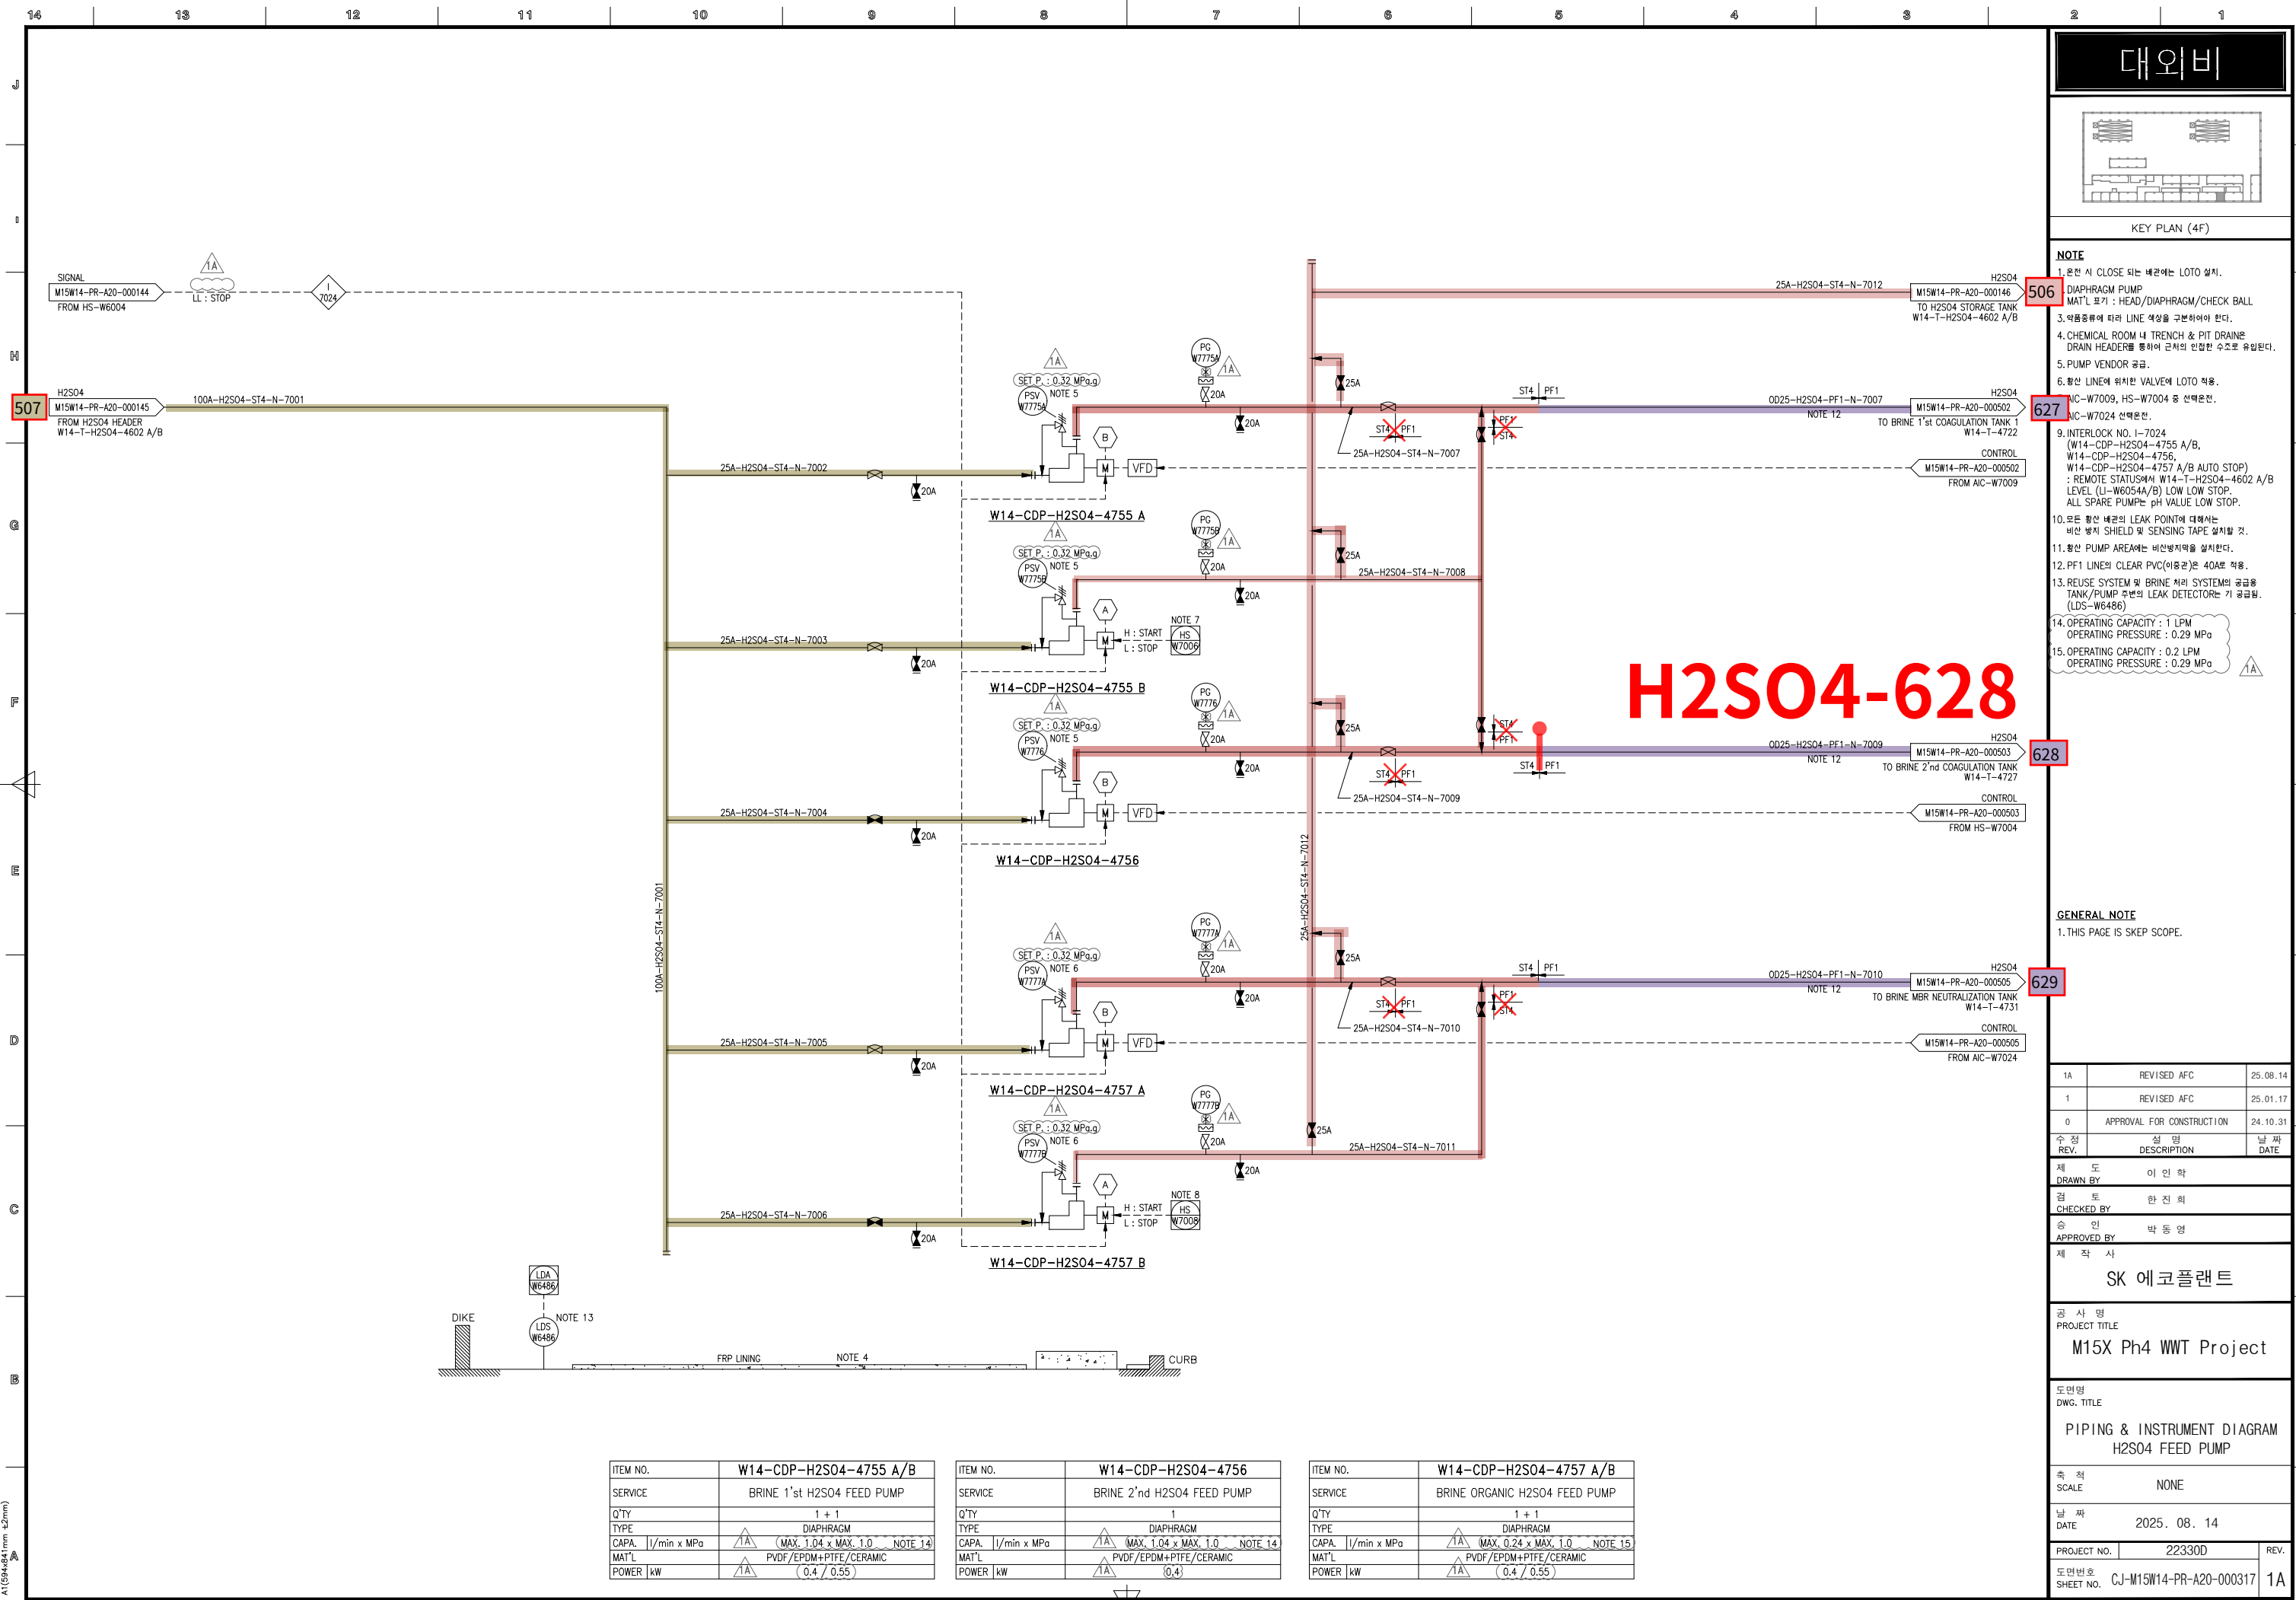

대외비

KEY PLAN (4F)

NOTE


1. 운전 시 CLOSE 되는 배관에는 LOTO 설치.
2. DIAPHRAGM PUMP MAT'L 표기 : HEAD/DIAPHRAGM/CHECK BALL
3. 약품종류에 따라 LINE 역상을 구분하여야 한다.
4. CHEMICAL ROOM 내 TRENCH & PIT DRAIN은 DRAIN HEADER를 통하여 근처의 인접한 수조로 유입된다.
5. PUMP VENDOR 공급.
6. 황산 LINE에 위치한 VALVE에 LOTO 적용.
7. AIC-W7009, HS-W7004 중 선택운전.
8. AIC-W7024 선택운전.
9. INTERLOCK NO. I-7024 (W14-CDP-H2SO4-4755 A/B, W14-CDP-H2SO4-4756, W14-CDP-H2SO4-4757 A/B AUTO STOP) : REMOTE STATUS에서 W14-T-H2SO4-4602 A/B LEVEL (LI-W6054A/B) LOW LOW STOP. ALL SPARE PUMP는 pH VALUE LOW STOP.
10. 모든 황산 배관의 LEAK POINT에 대해서는 비산 방지 SHIELD 및 SENSING TAPE 설치할 것.
11. 황산 PUMP AREA에는 비산방지막을 설치한다.
12. PF1 LINE의 CLEAR PVC(이음관)은 40A를 적용.
13. REUSE SYSTEM 및 BRINE 처리 SYSTEM의 공급용 TANK/PUMP 주변의 LEAK DETECTOR는 기 공급됨. (LDS-W6486)
14. OPERATING CAPACITY : 1 LPM
OPERATING PRESSURE : 0.29 MPa
15. OPERATING CAPACITY : 0.2 LPM
OPERATING PRESSURE : 0.29 MPa

GENERAL NOTE


1. THIS PAGE IS SKEP SCOPE.

1A	REVISED AFC	25.08.14
1	REVISED AFC	25.01.17
0	APPROVAL FOR CONSTRUCTION	24.10.31
수정 REV.	설명 DESCRIPTION	날짜 DATE
제 DRAWN BY	이인학	
검 CHECKED BY	한진희	
승 APPROVED BY	박동명	
제 작 사	SK 에코플랜트	
공 사 명 PROJECT TITLE	M15X Ph4 WWT Project	
도면명 DWG. TITLE	PIPING & INSTRUMENT DIAGRAM H2SO4 FEED PUMP	
속 척 SCALE	NONE	
날 짜 DATE	2025. 08. 14	
PROJECT NO.	22330D	REV.
도면번호 SHEET NO.	CJ-M15W14-PR-A20-000317	1A

ITEM NO.	W14-CDP-H2SO4-4755 A/B	ITEM NO.	W14-CDP-H2SO4-4756	ITEM NO.	W14-CDP-H2SO4-4757 A/B
SERVICE	BRINE 1'st H2SO4 FEED PUMP	SERVICE	BRINE 2'nd H2SO4 FEED PUMP	SERVICE	BRINE ORGANIC H2SO4 FEED PUMP
Q'TY	1 + 1	Q'TY	1	Q'TY	1 + 1
TYPE	DIAPHRAGM	TYPE	DIAPHRAGM	TYPE	DIAPHRAGM
CAPA. l/min x MPa	1A (MAX. 1.04 x MAX. 1.0 NOTE 14)	CAPA. l/min x MPa	1A (MAX. 1.04 x MAX. 1.0 NOTE 14)	CAPA. l/min x MPa	1A (MAX. 0.24 x MAX. 1.0 NOTE 15)
MAT'L	PVDF/EPDM+PTFE/CERAMIC	MAT'L	PVDF/EPDM+PTFE/CERAMIC	MAT'L	PVDF/EPDM+PTFE/CERAMIC
POWER kW	1A (0.4 / 0.55)	POWER kW	1A (0.4)	POWER kW	1A (0.4 / 0.55)

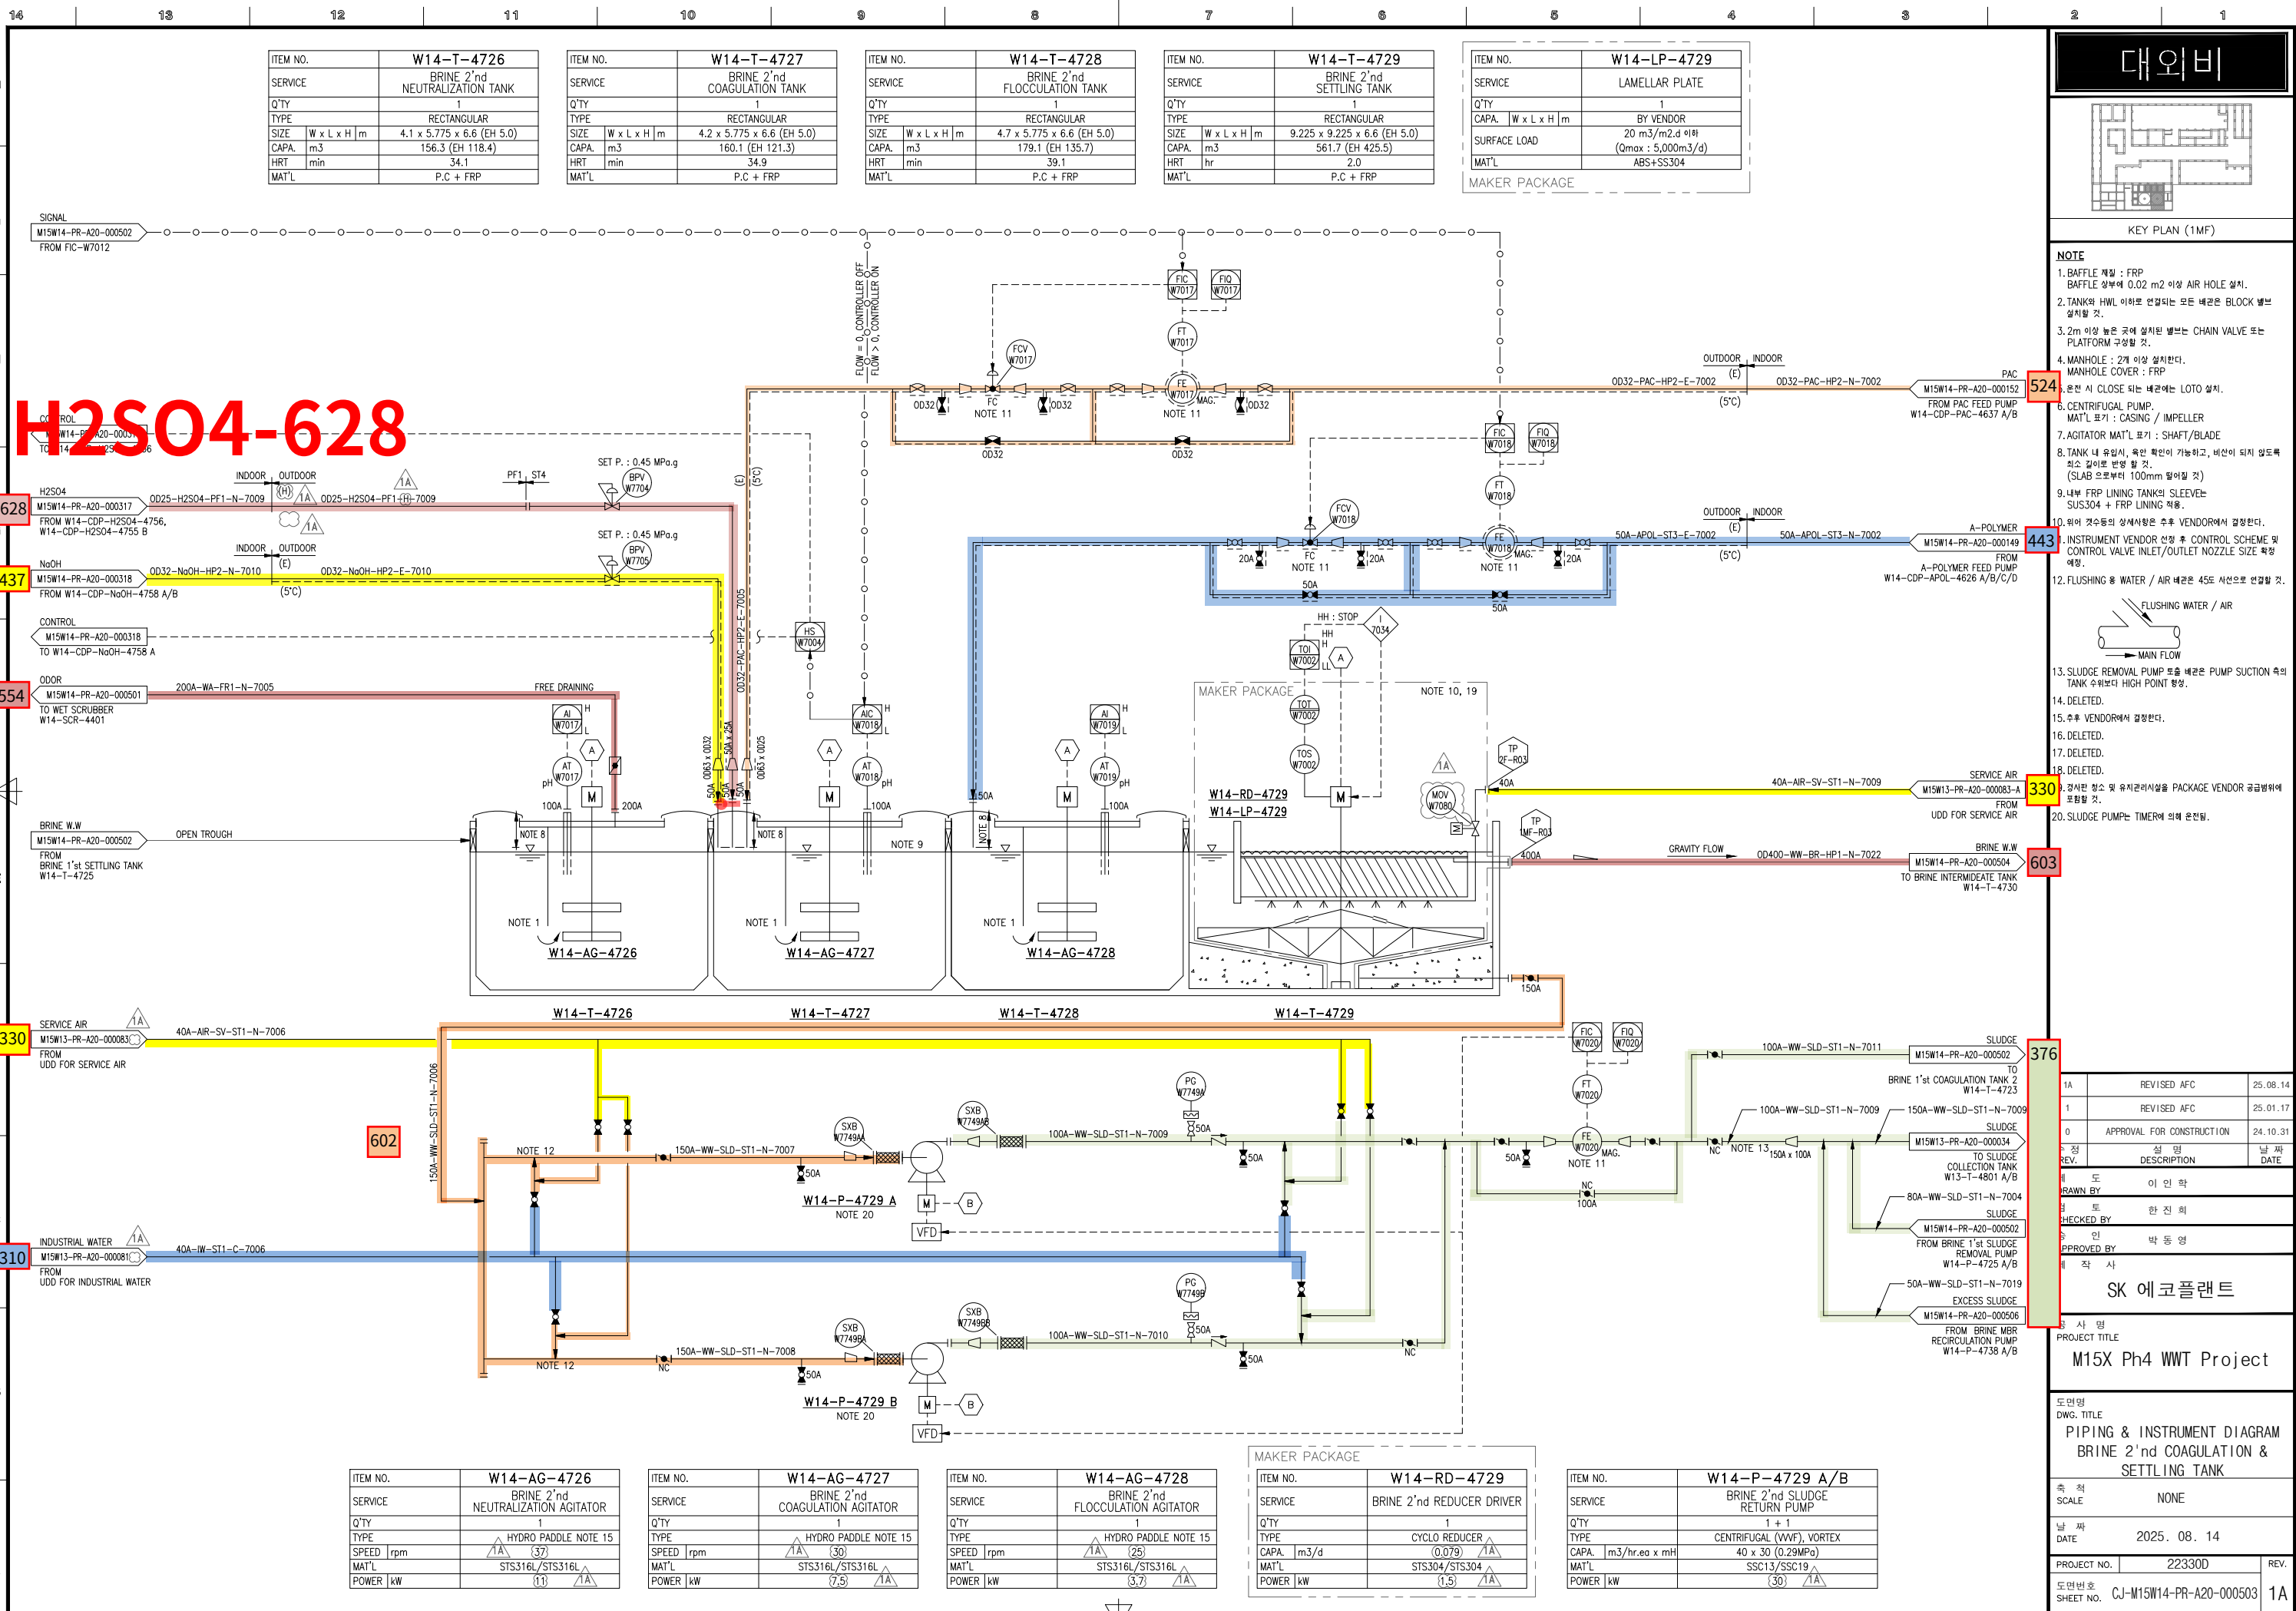


대외비

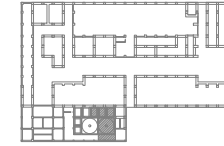

KEY PLAN (1MF)

- NOTE
1. Baffle 제형 : FRP
Baffle 상부에 0.02 m2 이상 AIR HOLE 설치.
 2. TANK와 HWL 이하로 연결되는 모든 배관은 BLOCK 밸브 설치할 것.
 3. 2m 이상 높은 곳에 설치된 밸브는 CHAIN VALVE 또는 PLATFORM 구성할 것.
 4. MANHOLE : 2개 이상 설치한다.
MANHOLE COVER : FRP
 5. 온천 시 CLOSE 되는 배관은 LOTO 설치.
 6. CENTRIFUGAL PUMP.
MAT'L 표기 : CASING / IMPELLER
 7. AGITATOR MAT'L 표기 : SHAFT/BLADE
 8. TANK 내 유입시, 육안 확인이 가능하고, 비산이 되지 않도록 최소 길이로 반영 할 것.
(SLAB 으로부터 100mm 떨어질 것)
 9. 내부 FRP LINING TANK의 SLEEVE는 SUS304 + FRP LINING 적용.
 10. 뒤어 것수등의 상세사상은 추후 VENDOR에서 결정한다.
 11. INSTRUMENT VENDOR 선정 후 CONTROL SCHEME 및 CONTROL VALVE INLET/OUTLET NOZZLE SIZE 확정 예정.
 12. FLUSHING 용 WATER / AIR 배관은 45도 서언으로 연결할 것.
 13. SLUDGE REMOVAL PUMP 또는 배관은 PUMP SUCTION 속의 TANK 수위보다 HIGH POINT 향상.
 14. DELETED.
 15. 추후 VENDOR에서 결정한다.
 16. DELETED.
 17. DELETED.
 18. DELETED.
 19. DELETED.
 20. SLUDGE PUMP는 TIMER에 의해 운전됨.

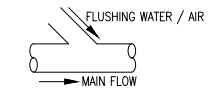

1A	REVISED AFC	25.08.14
1	REVISED AFC	25.01.17
0	APPROVAL FOR CONSTRUCTION	24.10.31

수정	REV.	실명	실명	날짜	DATE
도	DRAWN BY	이인학			
검	TO	한진희			
확인	CHECKED BY				
승인	APPROVED BY	박동명			
작	작사				

SK 에코플랜트


작성명 PROJECT TITLE
M15X Ph4 WWT Project


도면명 DWG. TITLE
PIPING & INSTRUMENT DIAGRAM
BRINE 2'nd COAGULATION & SETTLING TANK

축척 SCALE
NONE

날짜 DATE
2025. 08. 14

PROJECT NO. 22330D REV. A
도면번호 SHEET NO. CJ-M15W14-PR-A20-000503 1A

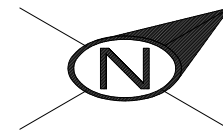


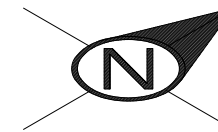

1. TRAY & ANGLE, CHANNEL SUPPORT가 적용되는 배관 ELEVATION은 현장 맞춤으로 한다.
2. (*) FIELD ADJUST

CLIENT		3
--------	---	---

경고: 본 도면은 SK HYNIX의 기밀비밀 자료로서, 어떠한 경우에도 목적 외 사용, 복제, 제3자에게 공개, 누설 및 유통할 수 없으며, 회사는 유포자의 불법 사용으로 피해가 발생할 경우 유포자에게 민/형사상 책임을 요구할 수 있음

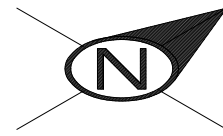

1. TRAY & ANGLE, CHANNEL SUPPORT가 적용되는
배관 ELEVATION은 현장 맞춤으로 한다.
2. H2SO4 배관의 입상/황관에는 비산/낙수 방지를 위한 투명 PVC 보호판(5T)을 설치하고
누출방지를 위해 Silicon 마감처리를 한다.
3. (*) FIELD ADJUST

CLIENT  5

	CONTRACTOR 	PROJECT NAME M15X Ph4 Project	
영	COMMODITY H2SO4	JOB NO. 22330D	
영	LINE NO. 0D25-H2SO4-PF1-E-7009	SH'T NO. 01 / 01	REV. 1
D			