

DRAWING LIST FOR TEST PACKAGE PROJECT NO.: 22328D PROJECT TITLE : M15X Ph2 Project		D-630
---	--	--------------

PROJECT NO.: 22328D

PROJECT TITLE : M15X Ph2 Project

[illegible]

ITEM NO.	W14-SU-4701
SERVICE	SUMP PIT
Q'TY	1
TYPE	RECTANGULAR
SIZE	W x L x H m1.8 x 0.75 x 1.0 (EH 0.8)
CAPA	m31.35 (EH 1.1)
MAT'L	R.C + EPOXY

ITEM NO.	W14-SPP-4701
SERVICE	SUMP PUMP
Q'TY	1
TYPE	SUBMERSIBLE
CAPA	m3/hr x mH3 x 25 (0.25Mpa) 1A
MAT'L	SSC13/SSC13
POWER	2.2 1A


대외비

KEY PLAN (1F)

NOTE

1. SUMP PUMP 의 모습배관은 상부로 연결한다. (역류방지)
2. INTERLOCK NO. I-7036
(W14-SPP-4701 AUTO START/STOP)
: REMOTE STATUS에서 W14-SU-4701 LEVEL
(LA-W7051) HIGH START / LOW STOP.
3. 운전 시 CLOSE 되는 배관에는 LOTO 설치.


1A	REVISED AFC	25.08.14
1	REVISED AFC	25.01.17
0	APPROVAL FOR CONSTRUCTION	24.10.31
수정 REV.	설명 DESCRIPTION	날짜 DATE
제 DRAWN BY	이인학	
검 CHECKED BY	한진희	
승 APPROVED BY	박동영	
제 작 사	SK 에코플랜트	
공 사 명 PROJECT TITLE	M15X Ph4 WWT Project	
도면명 DWG. TITLE	PIPING & INSTRUMENT DIAGRAM SUMP PIT & SUMP PUMP	
속 척 SCALE	NONE	
날 짜 DATE	2025. 08. 14	
PROJECT NO.	22330D	REV.
도면번호 SHEET NO.	CJ-M15W14-PR-A20-000511	1A

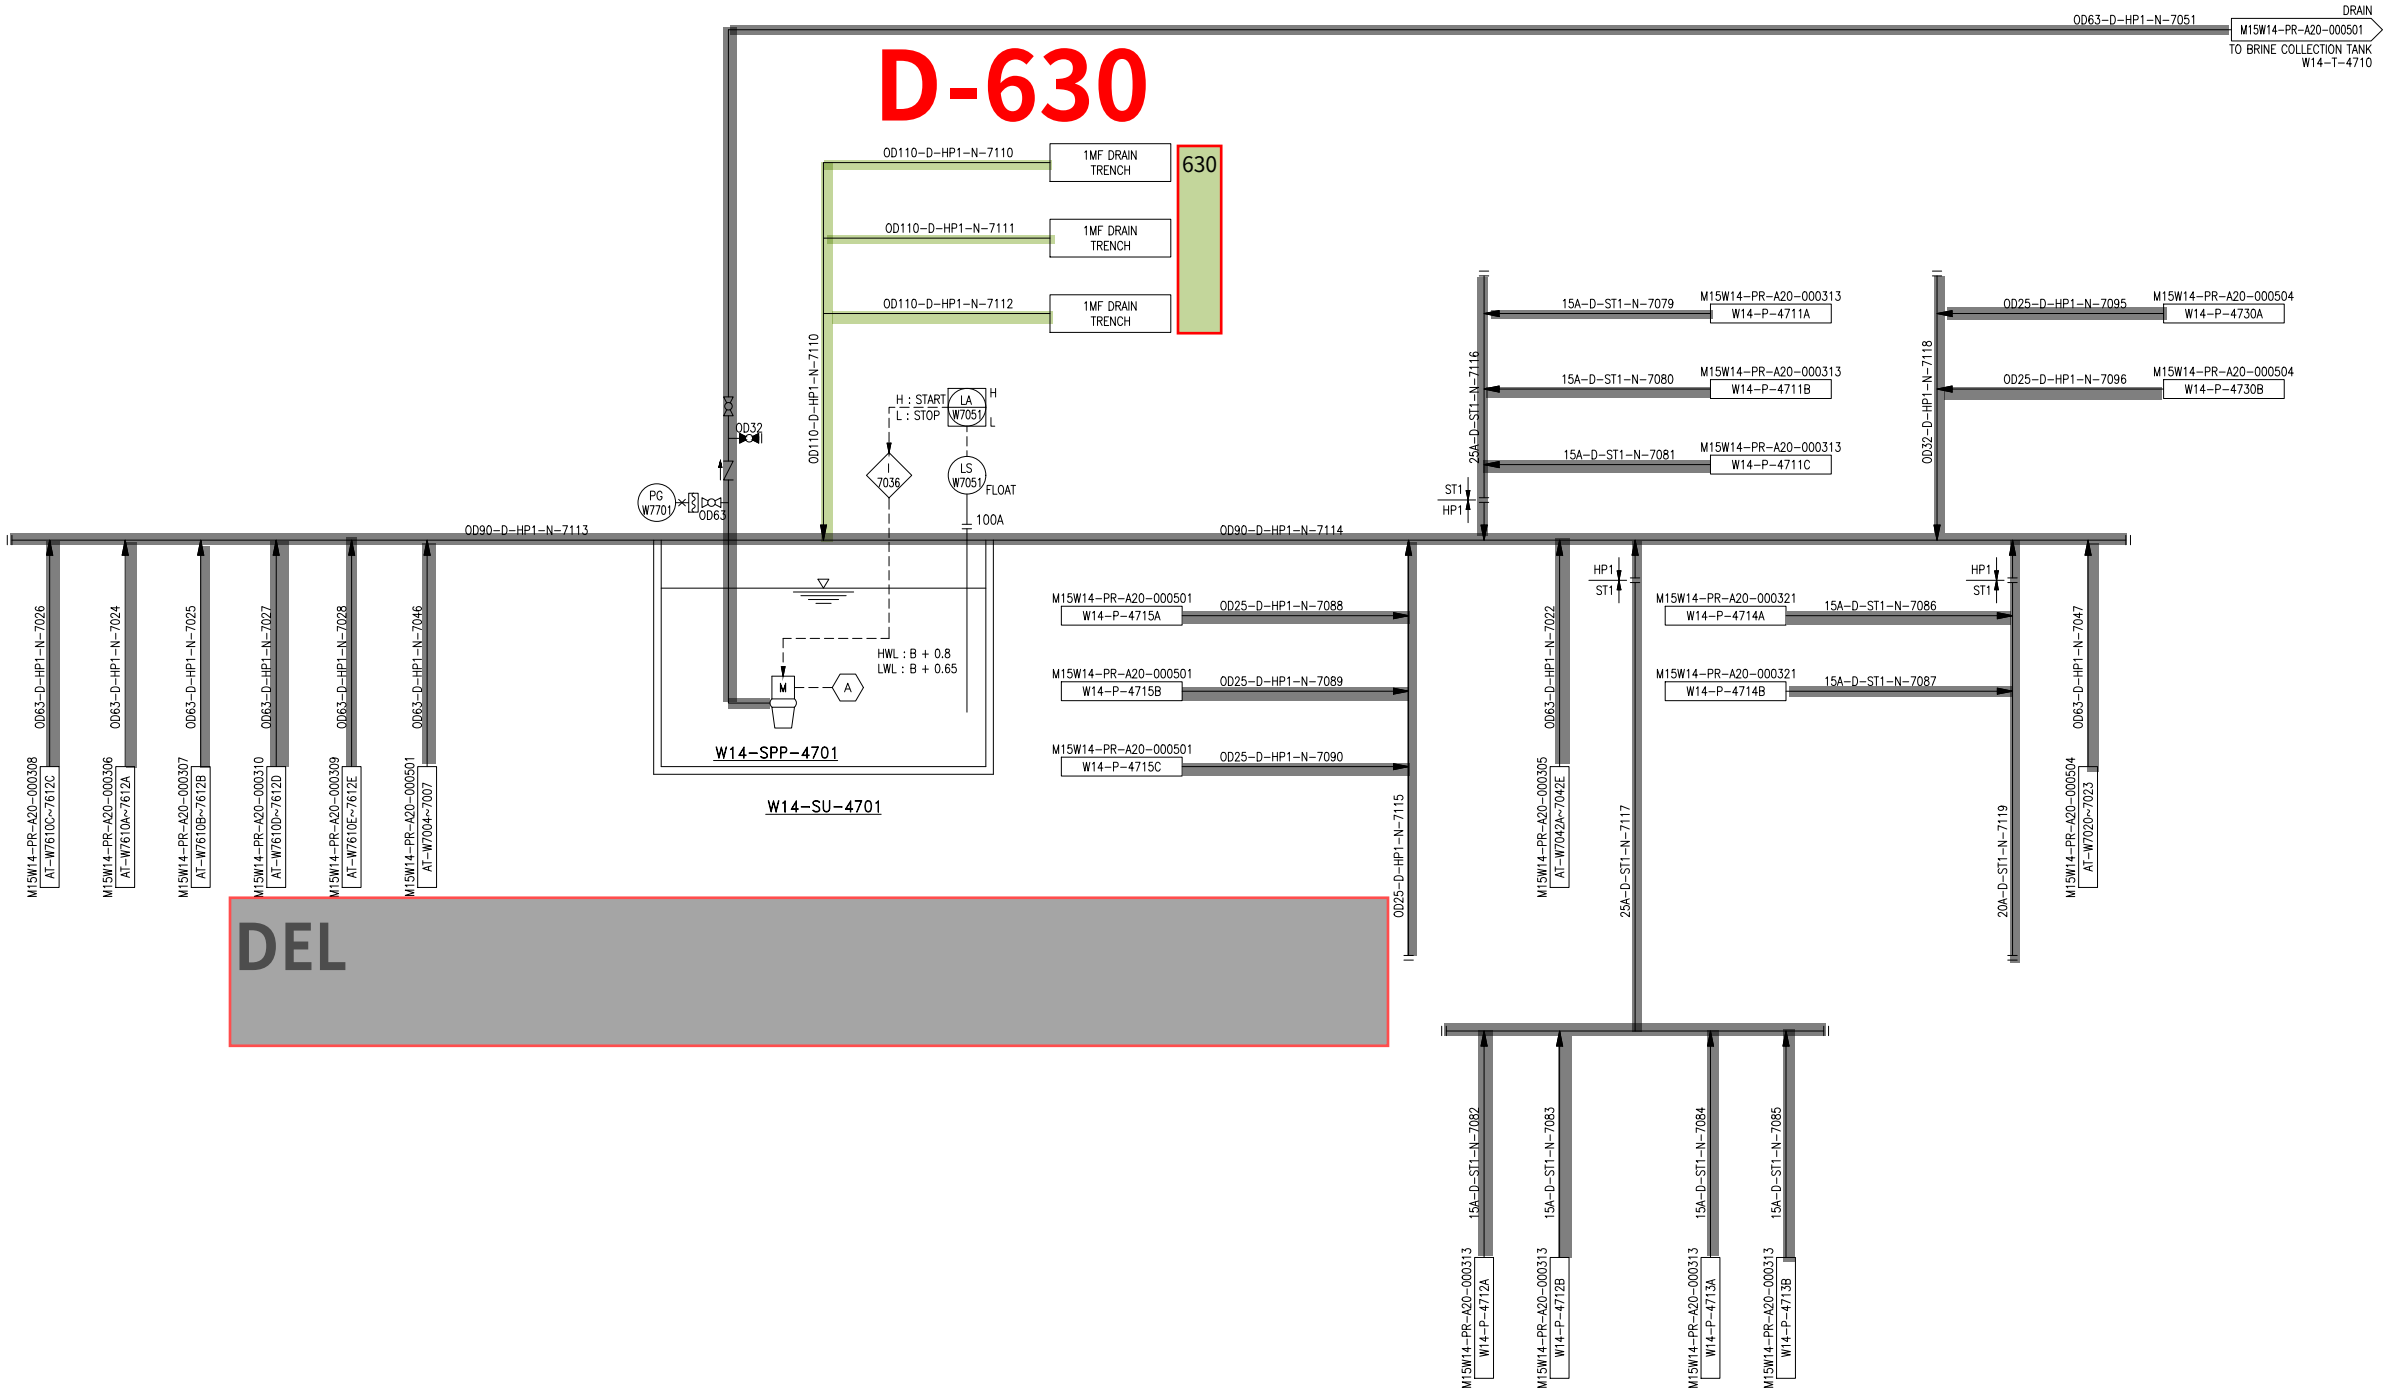



ITEM	SIZE	Q'TY	DESCRIPTION
HP1			
P	OD110	26.4M	PIPE, HDPE PE100, PE, BUTT FUSION, PN16/SDR11
E90	OD110	6EA	ELBOW 90 DEG, HDPE PE100, PE, BUTT FUSION, PN16/SDR11
T	OD110	2EA	TEE EQUAL, HDPE PE100, PE, BUTT FUSION X SOCKET FUSION, PN16/SDR11

1MF Drain Trench

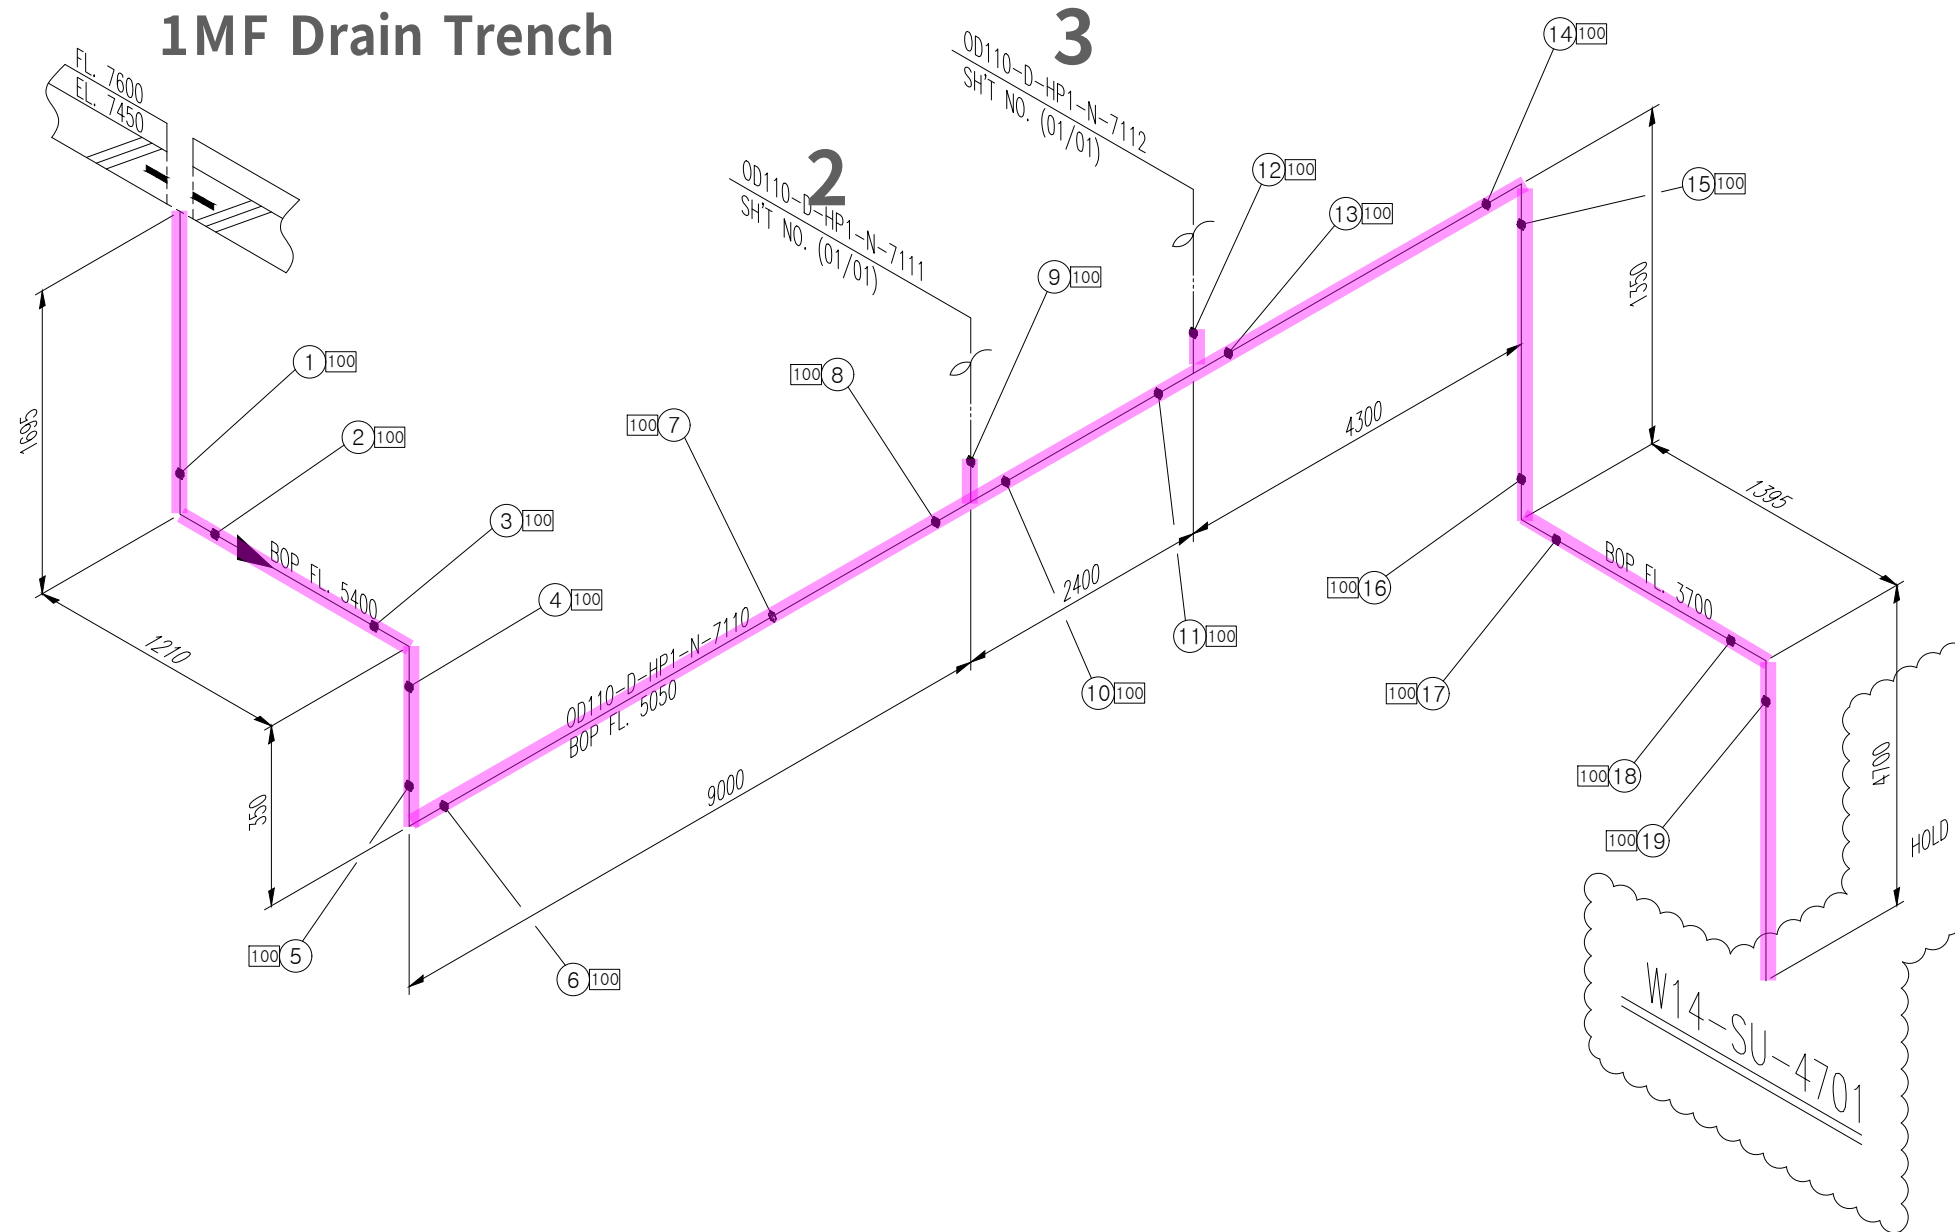


<NOTE>

1. TRAY & ANGLE, CHANNEL SUPPORT가 적용되는 배관 ELEVATION은 현장 맞춤으로 한다.
2. (*) FIELD ADJUST

* PIPE : P/P1	* 90° ELBOW : E90	* 45° ELBOW : E45	* TEE : T	* RED.TEE : TR	* STUB-IN : STU	* REINFORCING PAD : RP	* CON.RED : RC	* ECC.RED : RE	* CON.SWAGE : RCS/RCS1	* ECC.SWAGE : RES/RES1	* NIPPLE : NP/NP1/NP2	* CAP : CAP/CAP1	* PLUG : PLG	* FULL COUPLING : FC	* HALF COUPLING : HF/HF1
* STUB-IN : STU	* SOCKET(HDPE/PVC) : SC	* SADDLE(HDPE) : SD	* FLANGE : F/F1	* GASKET : G/G1/G2	* BOLT & NUT : B/B1	* BLIND FLANGE : FB/FB1	* GATE VA. : VG/G1/VG2	* BALL VA. : VB/VBLO/VB1/VB1O/VB2/VB2LO	* BUTTERFLY VA. : VF/VF4	* CHECK VA. : VC/VC1/VC2/VC3/VC4/VC5/VC6/VC7					
* GLOBE VA. : VL/VL1/VL2	* DIAPHRAGM VA. : VD/VDLO	* DAMPER : VP	* QUICK COUPLING : SQC	* FLEXIBLE JOINT(STEEL) : FLXB	* FLEXIBLE JOINT(RUBBER) : FLXR	* FLEXIBLE JOINT(STEEL PTFE LINED) : FLXL	* FLEXIBLE HOSE : FLXH	* STEAM TRAP : ST	* SPRAY NOZZLE : SPN	* EMERGENCY SHOWER : SSH					
* STRAINER(Y-TYPE) : YSTR	* STRAINER(T-TYPE) : TSTR	* STRAINER(BUCKET-TYPE) : BSTR	* ANCHOR PLATE : STOP	* BIRD SCREEN : BS	* ISOLATION KIT : IK	* UNLOADING BOX : UB	* AIR TRAP : AT	* LOTO : LOTO	* SIGHT GLASS : SG	* PRESSURE GAUGE : PG	* SHILED : SH	* SPECIAL BOLT & NUT : BL/BL1			

INSULATION	CODE	N	CONDITION	PRESS. (kg/cm2g)	TEMP. (°C)	AREA W14						CONTRACTOR	PROJECT NAME		
	THICK.	—	DESIGN	6.4	60	UNIT R1FA							M15X Ph4 Project		
			OPERATING	4	AMB	REF. PLAN DWG. CJ-M15W14-PI-A30-010017-A/B/C		25.01.24	APPROVED FOR CONSTRUCTION	황래중	안남후		박동영	COMMODITY D	
						REF. P & ID CJ-M15W14-PR-A20-000511						REV. NO.		DATE	DESCRIPTION

경고 : 본 도면은 SK HYNIX의 기업비밀 자료로서, 어떠한 경우에도 목적 외 사용, 복제, 제3자에게 공개, 누설 및 유출할 수 없으며, 회사는 유포자의 불법 사용으로 피해가 발생할 경우 유포자에게 민/형사상 책임을 요구할 수 있음

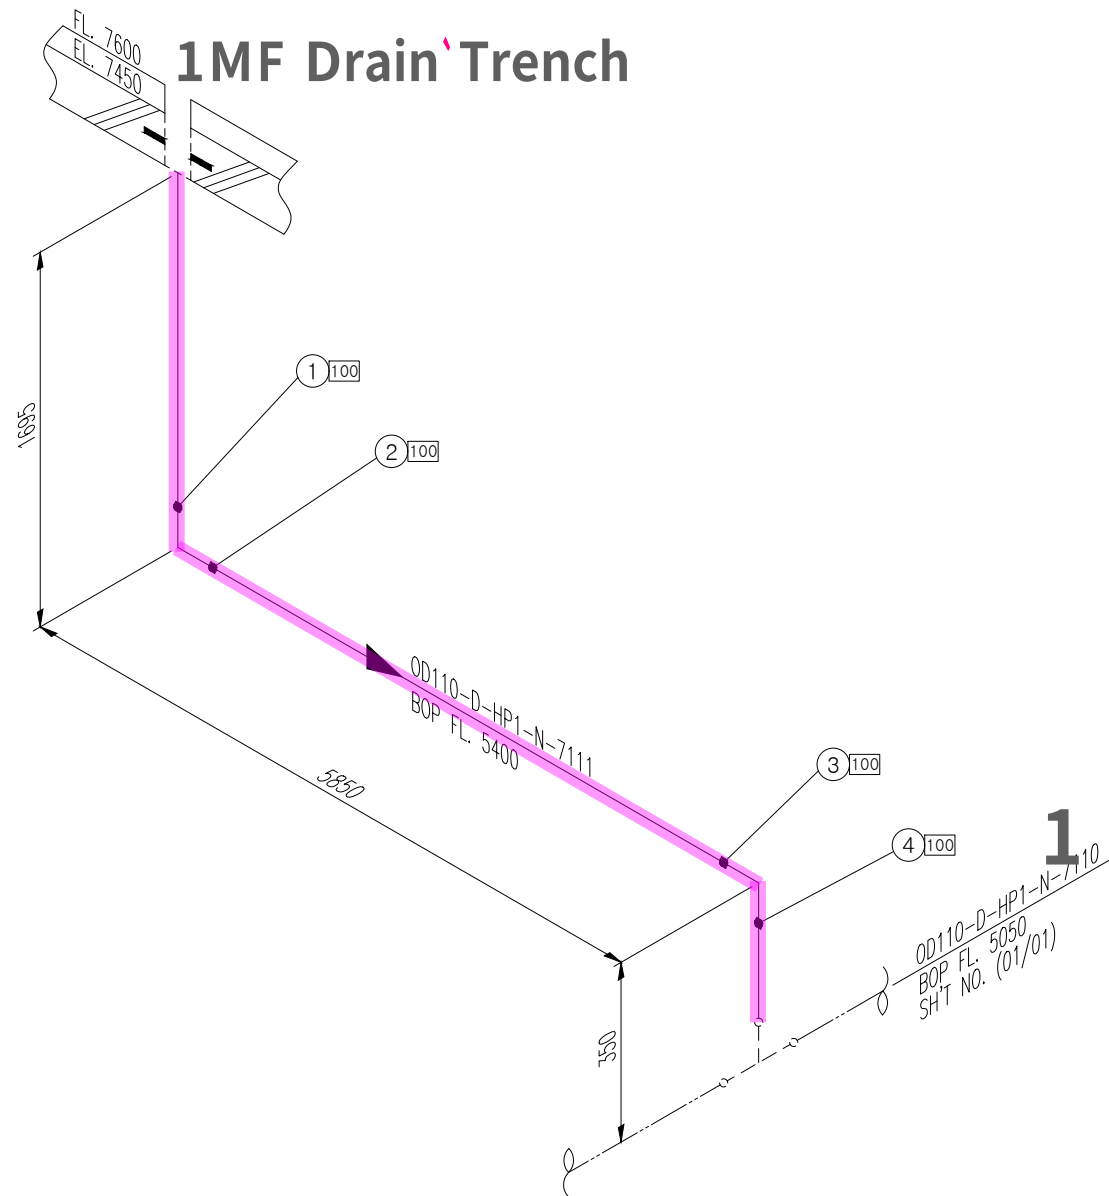
[illegible]

<NOTE>

1. TRAY & ANGLE, CHANNEL SUPPORT가 적용되는 배관 ELEVATION은 현장 맞춤으로 한다.
2. (*) FIELD ADJUST

* PIPE : P/P1	* 90° ELBOW : E90	* 45° ELBOW : E45	* TEE : T	* RED.TEE : TR	* STUB-IN : STU	* REINFORCING PAD : RP	* CON.RED : RC	* ECC.RED : RE	* CON.SWAGE : RCS/RCS1	* ECC.SWAGE : RES/RES1	* NIPPLE : NP/NP1/NP2	* CAP : CAP/CAP1	* PLUG : PLG	* FULL COUPLING : FC	* HALF COUPLING : HF/HF1
* STUB-IN : STU	* SOCKET(HDPE/PVC) : SC	* SADDLE(HDPE) : SD	* FLANGE : F/F1	* GASKET : G/G1/G2	* BOLT & NUT : B/B1	* BLIND FLANGE : FB/FB1	* GATE VA. : VG/VG1/VG2	* BALL VA. : VB/VBLO/VB1/VB1LO/VB2/VB2LO	* BUTTERFLY VA. : VF/VF4	* CHECK VA. : VC/VC1/VC2/VC3/VC4/VC5/VC6/VC7					
* GLOBE VA. : VL/VL1/VL2	* DIAPHRAGM VA. : VD/VDLO	* DAMPER : VP	* QUICK COUPLING : SQC	* FLEXIBLE JOINT(STEEL) : FLXB	* FLEXIBLE JOINT(RUBBER) : FLXR	* FLEXIBLE JOINT(STEEL PTFE LINED) : FLXL	* FLEXIBLE HOSE : FLXH	* STEAM TRAP : ST	* SPRAY NOZZLE : SPN	* EMERGENCY SHOWER : SSH					
* STRAINER(Y-TYPE) : YSTR	* STRAINER(T-TYPE) : TSTR	* STRAINER(BUCKET-TYPE) : BSTR	* ANCHOR PLATE : STOP	* BIRD SCREEN : BS	* ISOLATION KIT : IK	* UNLOADING BOX : UB	* AIR TRAP : AT	* LOTO : LOTO	* SIGHT GLASS : SG	* PRESSURE GAUGE : PG	* SHILED : SH	* SPECIAL BOLT & NUT : BL/BL1			

INSULATION	CODE	N	CONDITION	PRESS. (kg/cm ² g)	TEMP. (°C)	AREA W14							CONTRACTOR 	PROJECT NAME	
	THICK.	-	DESIGN	6.4	60	UNIT R1FA								M15X Ph4 Project	
			OPERATING	4	AMB	REF. PLAN DWG. CJ-M15W14-PI-A30-010017-C							COMMODITY D	JOB NO.	
						REF. P & ID CJ-M15W14-PR-A20-000511		25.01.24	APPROVED FOR CONSTRUCTION	황래중	안남후	박동영	LINE NO. OD110-D-HP1-N-7111	SH'T NO. 01 / 01	REV. 0
							REV. NO.	DATE	DESCRIPTION	BY	CHK	APP'D			

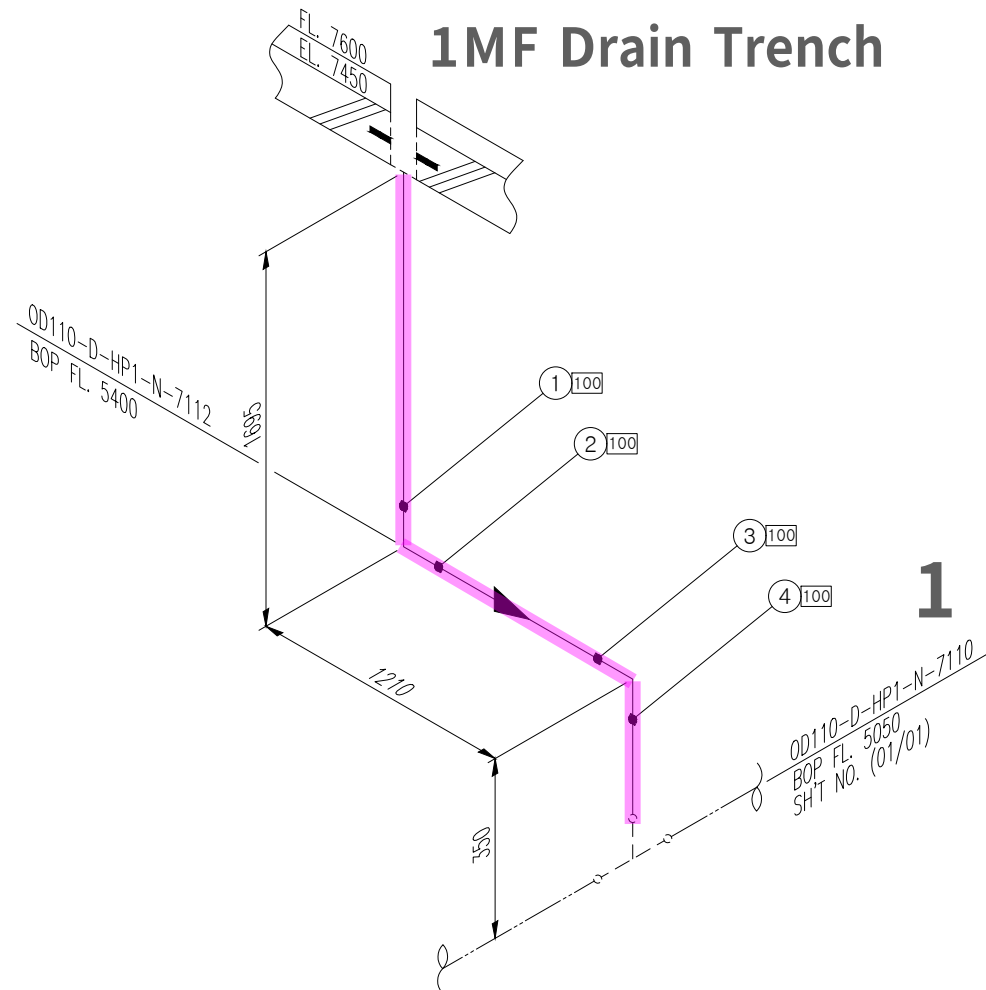[illegible]

<NOTE>
1. TRAY & ANGLE, CHANNEL SUPPORT가 적용되는
배관 ELEVATION은 현장 맞춤으로 한다.
2. (*) FIELD ADJUST

* PIPE : P/P1	* 90° ELBOW : E90	* 45° ELBOW : E45	* TEE : T	* RED.TEE : TR	* STUB-IN : STU	* REINFORCING PAD : RP	* CON.RED : RC	* ECC.RED : RE	* CON.SWAGE : RCS/RCS1	* ECC.SWAGE : RES/RES1	* NIPPLE : NP/NP1/NP2	* CAP : CAP/CAP1	* PLUG : PLG	* FULL COUPLING : FC	* HALF COUPLING : HF/HF1
* STUB-IN : STU	* SOCKET(HDPE/PVC) : SC	* SADDLE(HDPE) : SD	* FLANGE : F/F1	* GASKET : G/G1/G2	* BOLT & NUT : B/B1	* BLIND FLANGE : FB/FB1	* GATE VA. : VG/VG1/VG2	* BALL VA. : VB/VB1/VB10/VB2/VB2LO	* BUTTERFLY VA. : VF/VF4	* CHECK VA. : VC/VC1/VC2/VC3/VC4/VC5/VC6/VC7					
* GLOBE VA. : VL/VL1/VL2	* DIAPHRAGM VA. : VD/VDLO	* DAMPER : VP	* QUICK COUPLING : SQC	* FLEXIBLE JOINT(STEEL) : FLXB	* FLEXIBLE JOINT(RUBBER) : FLXR	* FLEXIBLE JOINT(STEEL PTFE LINED) : FLXL	* FLEXIBLE HOSE : FLXH	* STEAM TRAP : ST	* SPRAY NOZZLE : SPN	* EMERGENCY SHOWER : SSH					
* STRAINER(Y-TYPE) : YSTR	* STRAINER(T-TYPE) : TSTR	* STRAINER(BUCKET-TYPE) : BSTR	* ANCHOR PLATE : STOP	* BIRD SCREEN : BS	* ISOLATION KIT : IK	* UNLOADING BOX : UB	* AIR TRAP : AT	* LOTO : LOTO	* SIGHT GLASS : SG	* PRESSURE GAUGE : PG	* SHILED : SH	* SPECIAL BOLT & NUT : BL/BL1			

CLIENT  3

INSULATION	CODE	N	CONDITION	PRESS. (kg/cm2g)	TEMP. (°C)	AREA	W14							CONTRACTOR	PROJECT NAME		
	THICK.	-	DESIGN	6.4	60	UNIT	R1FA								M15X Ph4 Project		
			OPERATING	4	AMB	REF. PLAN DWG.	CJ-M15W14-PI-A30-010017-C							COMMODITY	D	JOB NO.	
						REF. P & ID	CJ-M15W14-PR-A20-000511		25.01.24	APPROVED FOR CONSTRUCTION	황래중	안남후	박동영	LINE NO.	0D110-D-HP1-N-7112	SH'T NO. 01 / 01	REV. 0
								REV. NO.	DATE	DESCRIPTION	BY	CHK	APP'D				