

DRAWING LIST FOR TEST PACKAGE

PROJECT NO.: 22328D

PROJECT TITLE : M15X Ph2 Project

WWW-REW-642

No	PKG No	UNIT	LINE NUMBER			P&ID		REMARK
			ISO DRAWING No	SHEET	REV	P&ID No	REV	
1	642	1FA	200A-WW-REW-ST1-N-7042-02	2 OF 2	1	CJ-M15W14-PR-A20-000313	1A	
2	642	2FA	200A-WW-REW-ST1-E-7042-01	1 OF 1	0	CJ-M15W13-PR-A20-000081	2	

WW-REW-642

642

464

317

318

319

310

418

419

428

313

315

314


316

323

324

312

대외비

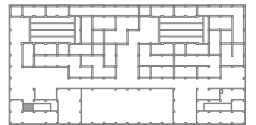


KEY PLAN (3F)

NOTE
1. PUMP EXTERNAL SEAL FLUID LINES ON UDD TO BE DEVELOPED.
2. FOR FUTURE CONNECTION NOZZLE.

2A	REVISED AFC	25.08.14
2	REVISED AFC	25.01.17
1	REVISED AFC	24.10.31
수정 REV.	설명 DESCRIPTION	날짜 DATE
제 DRAWN BY	이인학	
검 CHECKED BY	한진희	
승 APPROVED BY	박동영	
제 작 사	SK 에코플랜트	
공 사 명 PROJECT TITLE	M15X Ph4 WWT Project	
PROJ. NO.	22330D	


2	REVISED AFC	24.06.21
1	REVISED AFC	23.02.28
0	APPROVAL FOR CONSTRUCTION	22.09.23
수정 REV.	설명 DESCRIPTION	날짜 DATE
제 DRAWN BY	한진희	
검 CHECKED BY	심우영	
승 APPROVED BY	김태영	
제 작 사	SK 에코플랜트	
공 사 명 PROJECT TITLE	M15X Ph3 WWT Project	
도면명 DWG. TITLE	UTILITY DISTRIBUTION DIAGRAM INDUSTRIAL WATER SUPPLY SYSTEM (1/3)	
속 척 SCALE	NONE	
날 짜 DATE	2024. 10. 31	
PROJECT NO.	22330D	REV.
도면번호 SHEET NO.	CJ-M15W13-PR-A20-000081	2

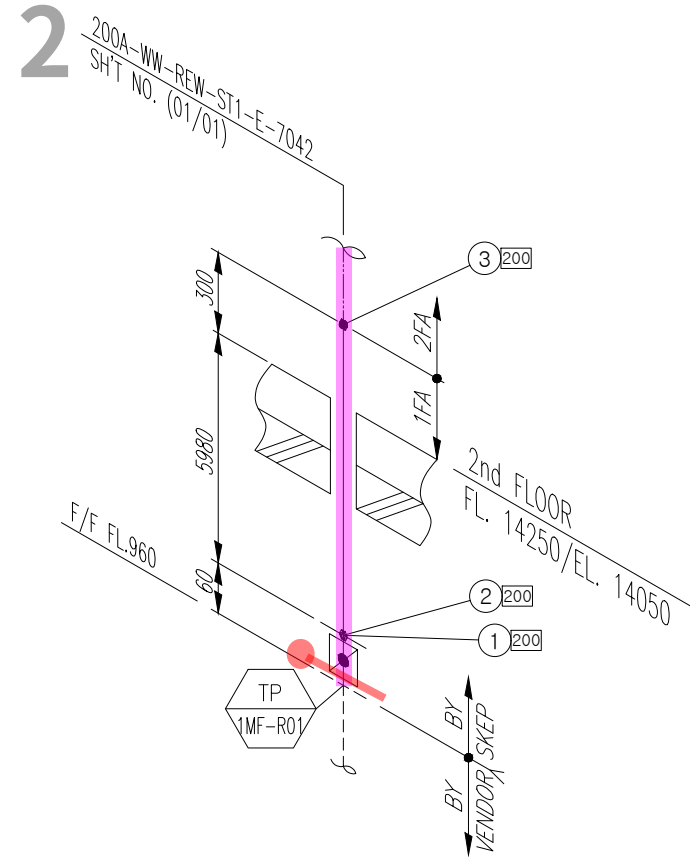[illegible]

<NOTE>
1. (*) FIELD ADJUST

* PIPE : P/P1	* 90° ELBOW : E90	* 45° ELBOW : E45	* TEE : T	* RED.TEE : TR	* STUB-IN : STU	* REINFORCING PAD : RP	* CON.RED : RC	* ECC.RED : RE	* CON.SWAGE : RCS/RCS1	* ECC.SWAGE : RES/RES1	* NIPPLE : NP/NP1/NP2	* CAP : CAP/CAP1	* PLUG : PLG	* FULL COUPLING : FC	* HALF COUPLING : HF/HF1
* STUB-IN : STU	* SOCKET(HDPE/PVC) : SC	* SADDLE(HDPE) : SD	* FLANGE : F/F1	* GASKET : G/G1/G2	* BOLT & NUT : B/B1	* BLIND FLANGE : FB/FB1	* GATE VA. : VG/VG1/VG2	* BALL VA. : VB/VBLO/VB1/VB1LO/VB2/VB2LO	* BUTTERFLY VA. : VF/VF4	* CHECK VA. : VC/VC1/VC2/VC3/VC4/VC5/VC6/VC7					
* GLOBE VA. : VL/VL1/VL2	* DIAPHRAGM VA. : VD/VDLO	* DAMPER : VP	* QUICK COUPLING : SQC	* FLEXIBLE JOINT(STEEL) : FLXB	* FLEXIBLE JOINT(RUBBER) : FLXR	* FLEXIBLE JOINT(STEEL PTFE LINED) : FLXL	* FLEXIBLE HOSE : FLXH	* STEAM TRAP : ST	* SPRAY NOZZLE : SPN	* EMERGENCY SHOWER : SSH					
* STRAINER(Y-TYPE) : YSTR	* STRAINER(T-TYPE) : TSTR	* STRAINER(BUCKET-TYPE) : BSTR	* ANCHOR PLATE : STOP	* BIRD SCREEN : BS	* ISOLATION KIT : IK	* UNLOADING BOX : UB	* AIR TRAP : AT	* LOTO : LOTO	* SIGHT GLASS : SG	* PRESSURE GAUGE : PG	* SHILED : SH	* SPECIAL BOLT & NUT : BL/BL1			

INSULATION	CODE	N	CONDITION	PRESS. (kg/cm ² g)	TEMP. (*C)	AREA W14							CONTRACTOR 	PROJECT NAME
	THICK.	-	DESIGN	6.4	60	UNIT R1FA								M15X Ph4 Project
			OPERATING	4	AMB	REF. PLAN DWG. CJ-M15W14-PI-A30-010017-B	 1	25.03.31	REVISED AS MARKED	황래중	안남후	박동영	COMMODITY WW-REW	JOB NO.
						REF. P & ID CJ-M15W14-PR-A20-000313	 0	25.01.24	APPROVED FOR CONSTRUCTION	황래중	안남후	박동영	22330D	
							REV. NO.	DATE	DESCRIPTION	BY	CHK	APP'D	LINE NO. 200A-WW-REW-ST1-N-7042	SH'T NO. 02 / 02 REV. 1

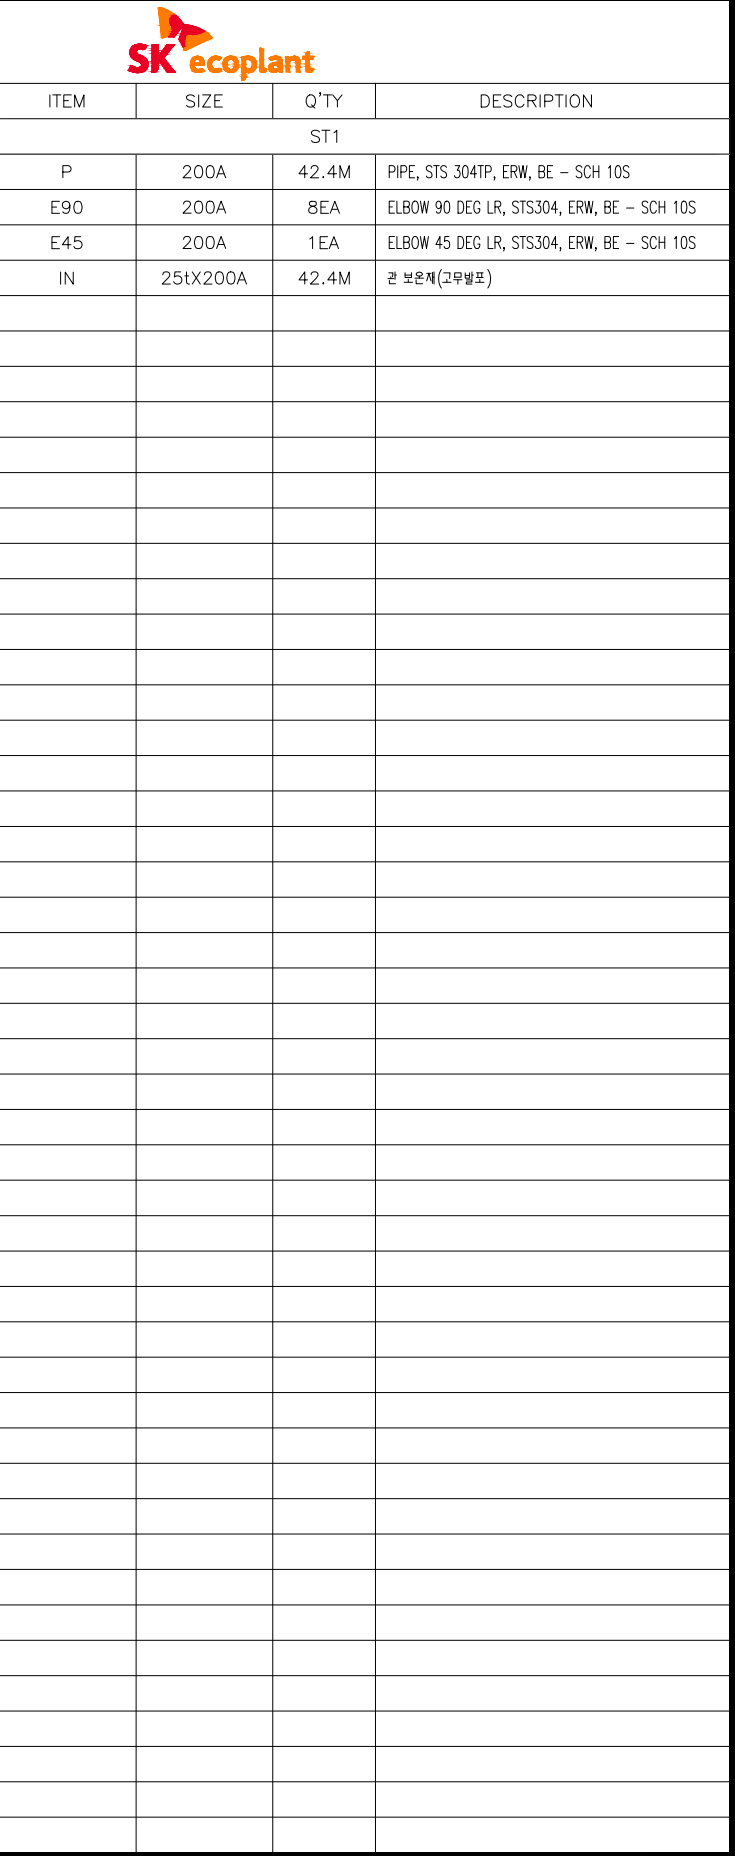

CONTRACTOR 		PROJECT NAME M15X Ph4 Project	
COMMODITY WW—REW		JOB NO. 22330D	
LINE NO. 200A-WW-REW-ST1-E-7042	SH'T NO. 01 / 01	REV. 0	

INSULATION	CODE	E	CONDITION	PRESS. (kg/cm2g)	TEMP. (°C)	AREA W14						
	THICK.	—	DESIGN	6.4	60	UNIT R2FA						
			OPERATING	4	AMB	REF. PLAN DWG. CJ-M15W14-PI-A30-020016-A						
						REF. P & ID CJ-M15W14-PR-A20-000313		25.01.24	APPROVED FOR CONSTRUCTION	황래중	안남후	박동영
							REV. NO.	DATE	DESCRIPTION	BY	CHK	APP