

DRAWING LIST FOR TEST PACKAGE PROJECT NO.: 22328D PROJECT TITLE : M15X Ph2 Project		MBW-645
---	--	----------------


PROJECT NO.: 22328D

PROJECT TITLE : M15X Ph2 Project

[illegible]

MBW-645

C:\Users\WTOP\Desktop\WP&ID\251013\W13-M15X Ph-4 for 인허가\CAD FILE\0910\WCJ-M15W13-PR-A20-000019 R2 P&ID FOR EQUA

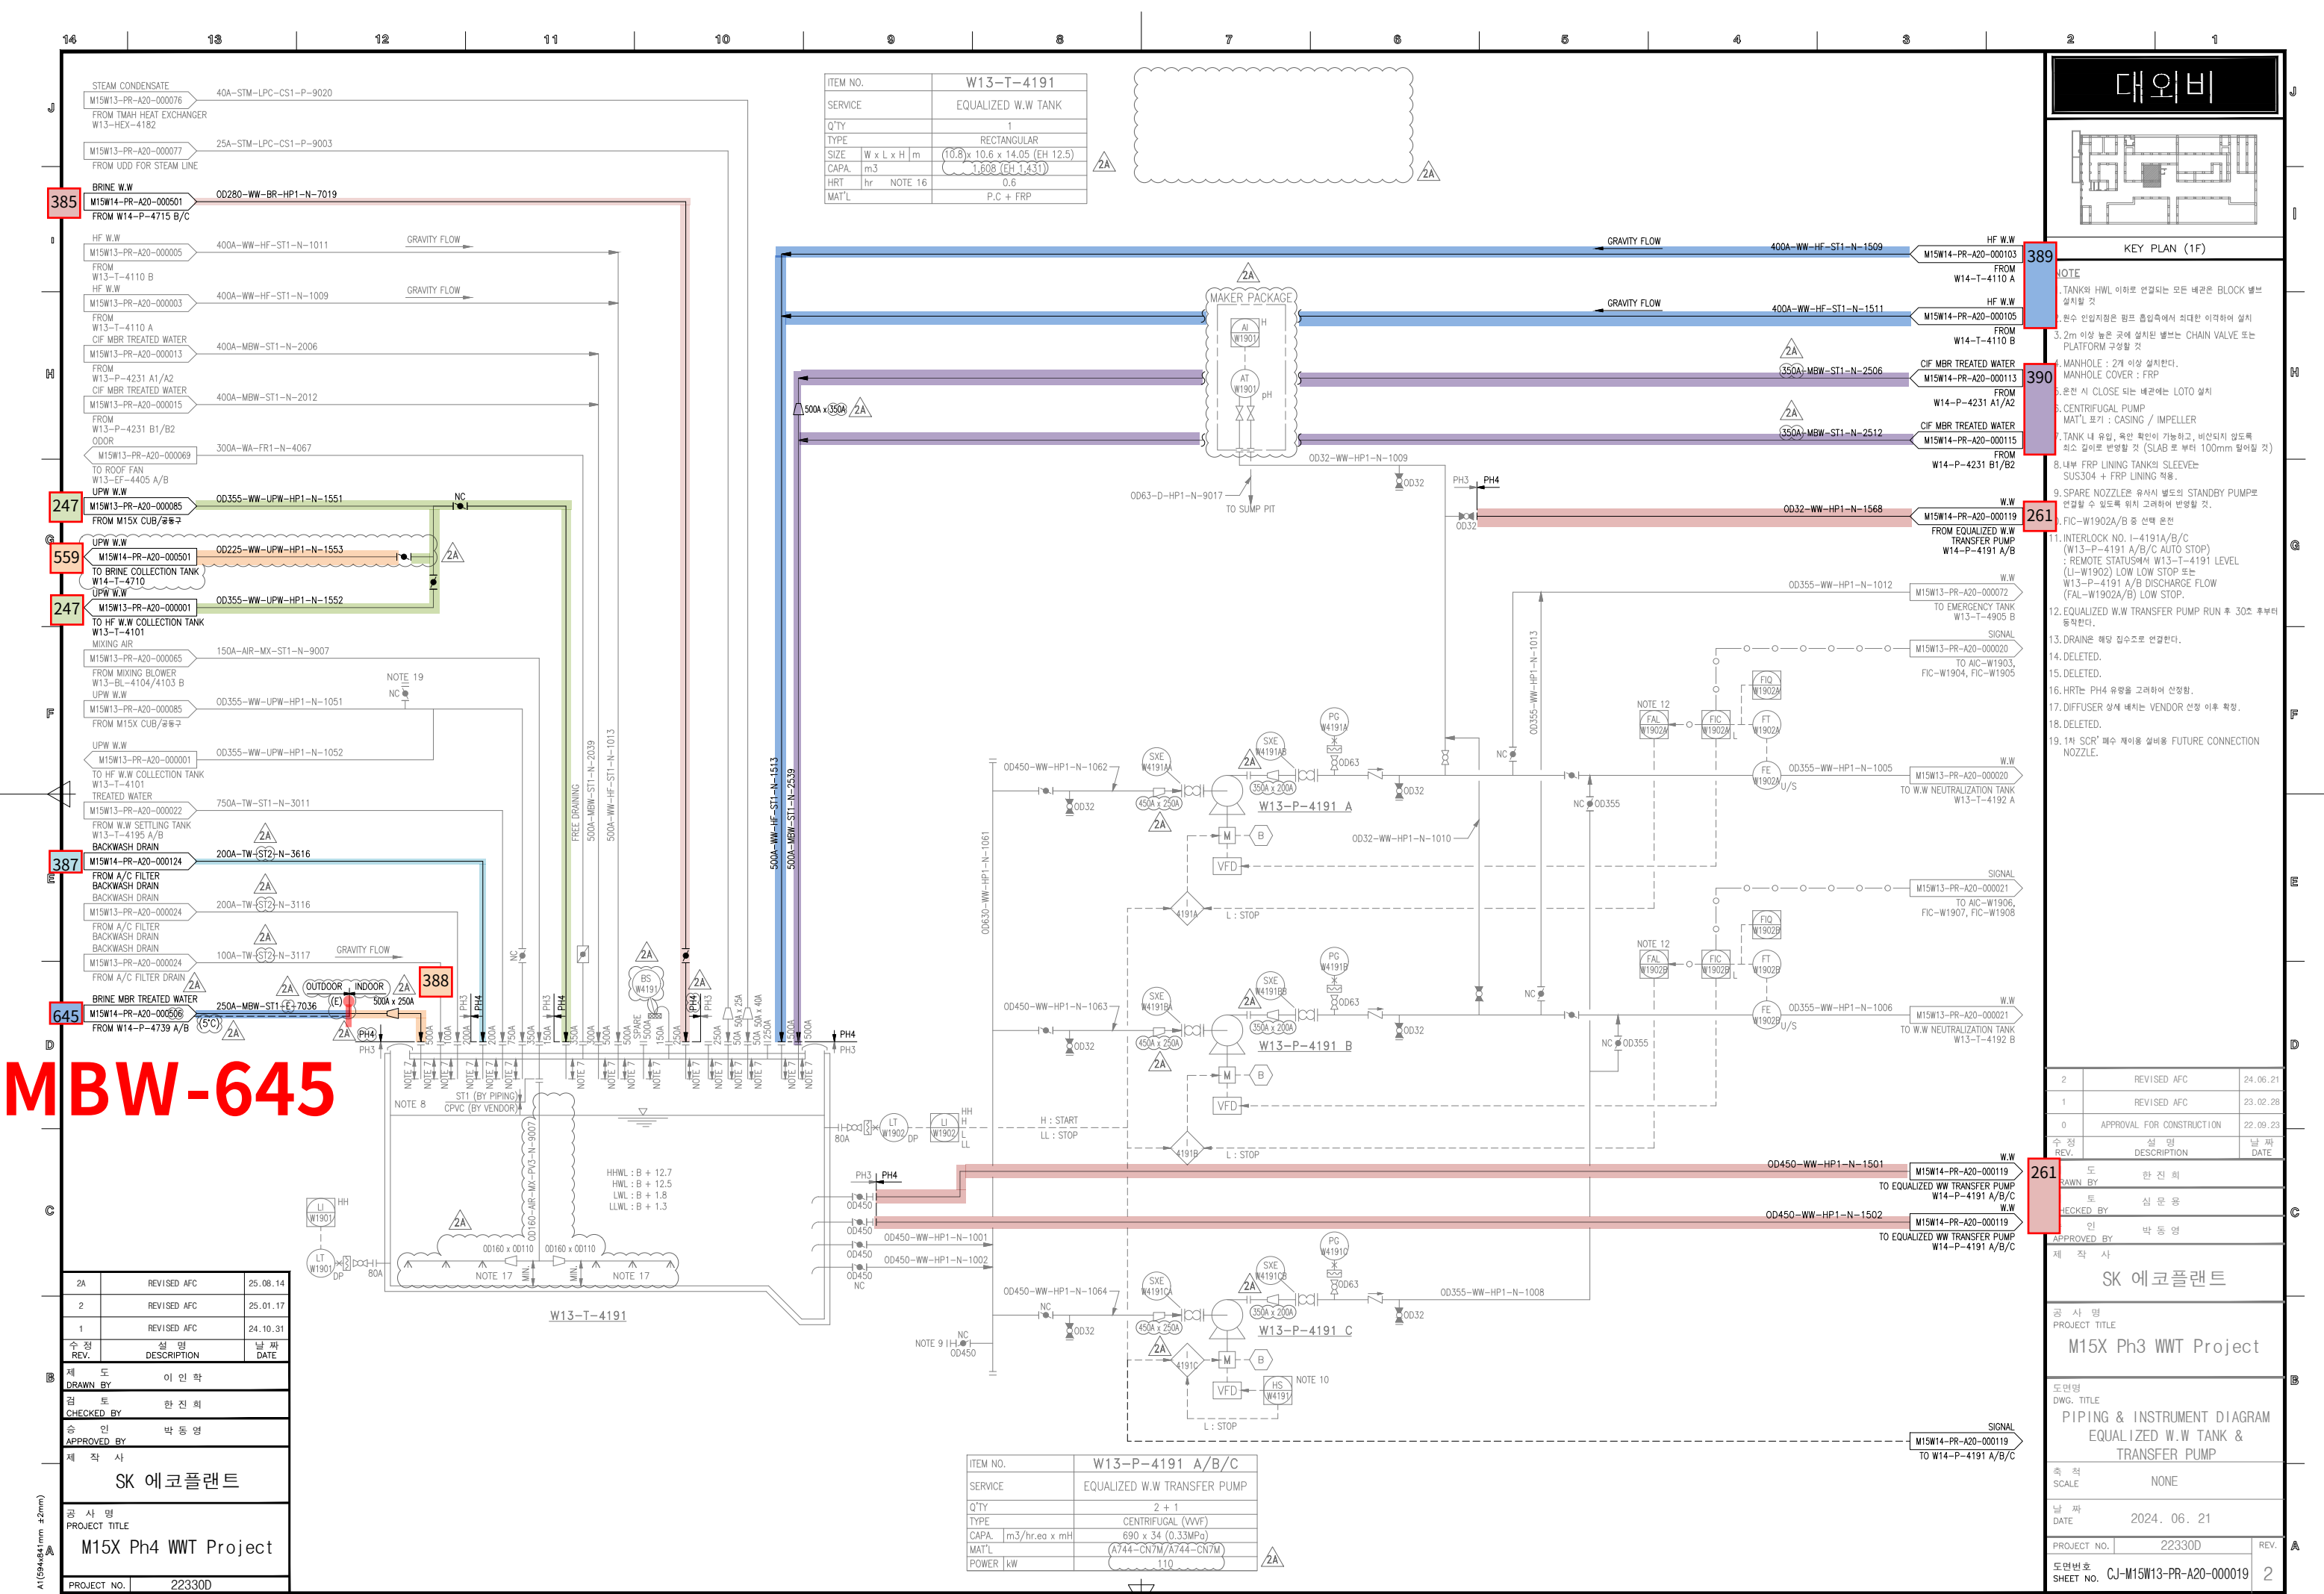

STEAM CONDENSATE
M15W13-PR-A20-000076
FROM TMAH HEAT EXCHANGER
W13-HEX-4182

M15W13-PR-A20-000077
FROM UDD FOR STEAM LINE

BRINE W.W.
M15W14-PR-A20-000501
FROM W14-P-4715 B/C

HF W.W.
M15W13-PR-A20-000005
FROM W13-T-4110 B

HF W.W.
M15W13-PR-A20-000003
FROM W13-T-4110 A

CIF MBR TREATED WATER
M15W13-PR-A20-000013
FROM W13-P-4231 A1/A2

CIF MBR TREATED WATER
M15W13-PR-A20-000015
FROM W13-P-4231 B1/B2

ODOR
M15W13-PR-A20-000069
TO ROOF FAN
W13-FF-4405 A/B

UPW W.W.
M15W13-PR-A20-000065
FROM M15X CUB/887

UPW W.W.
M15W14-PR-A20-000501
TO BRINE COLLECTION TANK
W14-T-4710

UPW W.W.
M15W13-PR-A20-000001
TO HF W.W. COLLECTION TANK
W13-T-4101

MIXING AIR
M15W13-PR-A20-000065
FROM MIXING BLOWER
W13-BL-4104/4103 B

UPW W.W.
M15W13-PR-A20-000065
FROM M15X CUB/887

UPW W.W.
M15W13-PR-A20-000001
TO HF W.W. COLLECTION TANK
W13-T-4101

TREATED WATER
M15W13-PR-A20-000022
FROM W.W. SETTLING TANK
W13-T-4195 A/B

BACKWASH DRAIN
M15W13-PR-A20-000024
FROM A/C FILTER

BACKWASH DRAIN
M15W13-PR-A20-000024
FROM A/C FILTER

BACKWASH DRAIN
M15W13-PR-A20-000024
FROM A/C FILTER

BRINE MBR TREATED WATER
M15W14-PR-A20-000506
FROM W14-P-4739 A/B

NOTE 19
NC

NOTE 8
ST1 (BY PIPING)
CPVC (BY VENDOR)

NOTE 17
HHWL : B + 12.7
HWL : B + 12.5
LWL : B + 1.8
LLWL : B + 1.3

2A	REVISED AFC	25.08.14
2	REVISED AFC	25.01.17
1	REVISED AFC	24.10.31
수정 REV.	설명 DESCRIPTION	날짜 DATE
제 DRAWN BY	이인학	
검 CHECKED BY	한진희	
승 APPROVED BY	박동영	
제 작 사	SK 에코플랜트	
공 사 명 PROJECT TITLE	M15X Ph4 WWT Project	
프로젝트 PROJECT NO.	22330D	

ITEM NO.	W13-T-4191
SERVICE	EQUALIZED W.W. TANK
Q'TY	1
TYPE	RECTANGULAR
SIZE	W x L x H m (10.8 x 10.6 x 14.05 (EH 12.5))
CAPA.	m3 1,608 (EH 1,431)
HRT	hr NOTE 16 0.6
MAT'L	P.C + FRP

ITEM NO.	W13-P-4191 A/B/C
SERVICE	EQUALIZED W.W. TRANSFER PUMP
Q'TY	2 + 1
TYPE	CENTRIFUGAL (VVVF)
CAPA.	m3/hr.ea x mH 690 x 34 (0.33MPa)
MAT'L	A744-CN7M/A744-CN7M
POWER	kW 110

대외비

KEY PLAN (1F)


NOTE

- TANK의 HWL 이하로 연결되는 모든 배관은 BLOCK 별본 설치할 것
- 관수 인입지점은 펌프 흡입측에서 최대한 아래쪽에 설치
- 3.2m 이상 높은 곳에 설치된 별본은 CHAIN VALVE 또는 PLATFORM 구성할 것
- MANHOLE : 2개 이상 설치한다.
MANHOLE COVER : FRP
- 관전 시 CLOSE 되는 배관에는 LOTO 설치
- CENTRIFUGAL PUMP
MAT'L 표기 : CASING / IMPELLER
- TANK 내 유입, 유출 확인이 가능하고, 비산되지 않도록 최소 길이로 반영할 것 (SLAB로부터 100mm 떨어질 것)
- 내부 FRP LINING TANK의 SLEEVE는 SUS304 + FRP LINING 적용
- SPARE NOZZLE은 유체시 별도의 STANDBY PUMP로 연결할 수 있도록 위치 고려하여 반영할 것.
- FIC-W1902A/B 등 선택 운전
- INTERLOCK NO. I-4191A/B/C (W13-P-4191 A/B/C AUTO STOP) : REMOTE STATUS에서 W13-T-4191 LEVEL (LI-W1902) LOW LOW STOP 또는 W13-P-4191 A/B DISCHARGE FLOW (FAL-W1902A/B) LOW STOP.
- EQUALIZED W.W. TRANSFER PUMP RUN 후 30초 후부터 동작한다.
- DRAIN은 해당 장소로 연결한다.
- DELETED.
- DELETED.
- HRT는 PH4 유량을 고려하여 선정함.
- DIFFUSER 상에 배치는 VENDOR 선정 이후 확정.
- DELETED.
- 1차 SCR 배수 제어용 설비용 FUTURE CONNECTION NOZZLE.

2	REVISED AFC	24.06.21
1	REVISED AFC	23.02.28
0	APPROVAL FOR CONSTRUCTION	22.09.23
수정 REV.	설명 DESCRIPTION	날짜 DATE

261	도 DRAWN BY	한진희
261	토 CHECKED BY	심문용
261	인 APPROVED BY	박동영
261	제 작 사	SK 에코플랜트

공 사 명 PROJECT TITLE	M15X Ph3 WWT Project
도면명 DWG. TITLE	PIPING & INSTRUMENT DIAGRAM EQUALIZED W.W. TANK & TRANSFER PUMP
축 척 SCALE	NONE
날 짜 DATE	2024. 06. 21
PROJECT NO.	22330D
도면번호 SHEET NO.	CJ-M15W13-PR-A20-000019
REV.	2

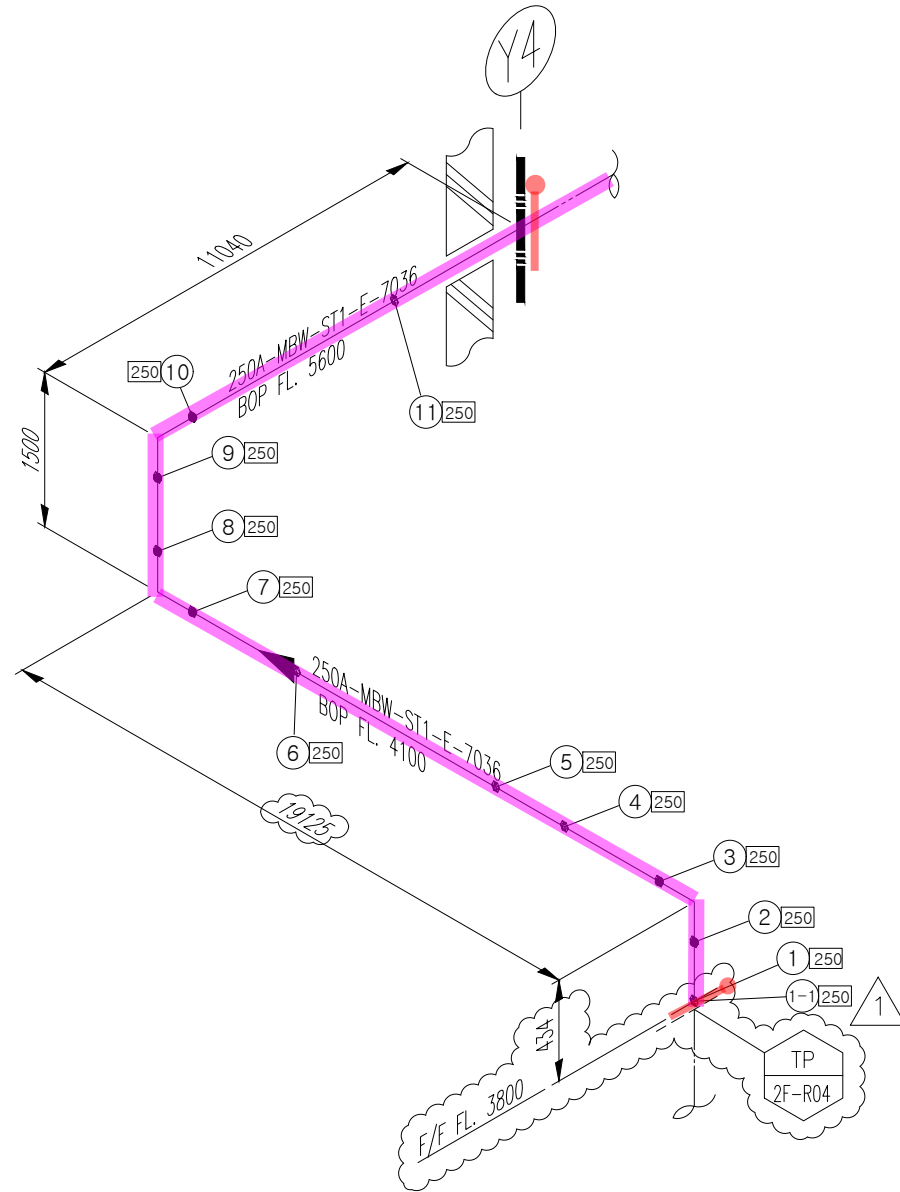[illegible]

<NOTE>
1. (*) FIELD ADJUST

* PIPE : P/P1	* 90° ELBOW : E90	* 45° ELBOW : E45	* TEE : T	* RED.TEE : TR	* STUB-IN : STU	* REINFORCING PAD : RP	* CON.RED : RC	* ECC.RED : RE	* CON.SWAGE : RCS/RCS1	* ECC.SWAGE : RES/RES1	* NIPPLE : NP/NP1/NP2	* CAP : CAP/CAP1	* PLUG : PLG	* FULL COUPLING : FC	* HALF COUPLING : HF/HF1
* STUB-IN : STU	* SOCKET(HDPE/PVC) : SC	* SADDLE(HDPE) : SD	* FLANGE : F/F1	* GASKET : G/G1/G2	* BOLT & NUT : B/B1	* BLIND FLANGE : FB/FB1	* GATE VA. : VG/VG1/VG2	* BALL VA. : VB/VB1/VB10/VB2/VB210	* BUTTERFLY VA. : VF/VF4	* CHECK VA. : VC/VC1/VC2/VC3/VC4/VC5/VC6/VC7					
* GLOBE VA. : VL/VL1/VL2	* DIAPHRAGM VA. : VD/VD10	* DAMPER : VP	* QUICK COUPLING : SQC	* FLEXIBLE JOINT(STEEL) : FLXB	* FLEXIBLE JOINT(RUBBER) : FLXR	* FLEXIBLE JOINT(STEEL PTFE LINED) : FLXL	* FLEXIBLE HOSE : FLXH	* STEAM TRAP : ST	* SPRAY NOZZLE : SPN	* EMERGENCY SHOWER : SSH					
* STRAINER(Y-TYPE) : YSTR	* STRAINER(T-TYPE) : TSTR	* STRAINER(BUCKET-TYPE) : BSTR	* ANCHOR PLATE : STOP	* BIRD SCREEN : BS	* ISOLATION KIT : IK	* UNLOADING BOX : UB	* AIR TRAP : AT	* LOTO : LOTO	* SIGHT GLASS : SG	* PRESSURE GAUGE : PG	* SHILED : SH	* SPECIAL BOLT & NUT : BL/BL1			

INSULATION	CODE	N	CONDITION	PRESS. (kg/cm2g)	TEMP. (°C)	AREA W14								CONTRACTOR	PROJECT NAME	
	THICK.	—	DESIGN	6.4	60	UNIT R2FA									M15X Ph4 Project	
			OPERATING	4	AMB	REF. PLAN DWG. CJ-M15W14-PI-A30-020014-C		25.03.31	REVISED AS MARKED	황래중	안남후	박동영	COMMODITY	MBW	JOB NO.	
						REF. P & ID CJ-M15W14-PR-A20-000506		25.01.24	APPROVED FOR CONSTRUCTION	황래중	안남후	박동영			22330D	
							REV. NO.	DATE	DESCRIPTION	BY	CHK	APP'D	LINE NO.	250A-MBW-ST1-E-7036	SH'T NO. 01 / 01	REV. 1

경고: 본 문서는 SK HYNIX의 기밀비밀 자료로서, 어떠한 경우에도 무단 사용, 복제, 제3자에게 공개, 누설, 변조, 유통, 기타 무단 사용, 또는 기타 행위를 금지합니다. 무단 사용, 또는 기타 행위를 한 자에 대해서는 법적 조치를 취할 수 있습니다. 본 문서는 SK HYNIX의 기밀비밀 자료로서, 어떠한 경우에도 무단 사용, 복제, 제3자에게 공개, 누설, 변조, 유통, 기타 무단 사용, 또는 기타 행위를 금지합니다. 무단 사용, 또는 기타 행위를 한 자에 대해서는 법적 조치를 취할 수 있습니다.