

DRAWING LIST FOR TEST PACKAGE

AIR-DRY-648

PROJECT NO.: 22328D

PROJECT TITLE : M15X Ph2 Project

No	PKG No	UNIT	LINE NUMBER			P&ID		REMARK
			ISO DRAWING No	SHEET	REV	P&ID No	REV	
1	648	1MF	50A-AIR-DRY-ST1-N-7019-01	1 OF 1	0	CJ-M15W13-PR-A20-000082-B		
2	648	2FA	15A-AIR-DRY-ST1-N-7020-01	1 OF 1	0	CJ-M15W13-PR-A20-000082-B		
3	648	2FA	15A-AIR-DRY-ST1-N-7021-01	1 OF 1	0	CJ-M15W13-PR-A20-000082-B		
4	648	2FA	15A-AIR-DRY-ST1-N-7022-01	1 OF 1	0	CJ-M15W13-PR-A20-000082-B		
5	648	2FA	15A-AIR-DRY-ST1-N-7023-01	1 OF 1	0	CJ-M15W13-PR-A20-000082-B		
6	648	2FA	15A-AIR-DRY-ST1-N-7024-01	1 OF 1	0	CJ-M15W13-PR-A20-000082-B		
7	648	2FA	15A-AIR-DRY-ST1-N-7025-01	1 OF 1	0	CJ-M15W13-PR-A20-000082-B		
8	648	2FA	50A-AIR-DRY-ST1-N-7005-01	1 OF 1	0	CJ-M15W14-PR-A20-000506		
9	648	2FA	50A-AIR-DRY-ST1-N-7019-01	1 OF 4	0	CJ-M15W13-PR-A20-000082-B		
10	648	2FA	50A-AIR-DRY-ST1-N-7019-02	2 OF 4	0	CJ-M15W13-PR-A20-000082-B		
11	648	2FA	50A-AIR-DRY-ST1-N-7019-03	3 OF 4	0	CJ-M15W13-PR-A20-000082		
12	648	2FA	50A-AIR-DRY-ST1-N-7019-04	4 OF 4	0	CJ-M15W13-PR-A20-000082		
13								
14								
15								
16								
17								
18								
19								
20								

14

13

12

11

10

9

8

7

6

5

4

3

2

1

648

CLEAN DRY AIR
M15W13-PR-A20-000082
FROM CLEAN DRY AIR HEADER

50A-AIR-DRY-ST1-N-7019

CELAN DRY AIR
M15W14-PR-A20-000506
TO W14-EJ-4739

50A-AIR-DRY-ST1-N-7005

M15W14-PR-A20-000502
FCV-W7013

M15W14-PR-A20-000502
FCV-W7014

M15W14-PR-A20-000502
XV-W7627A

M15W14-PR-A20-000502
XV-W7628A

M15W14-PR-A20-000503
FCV-W7017

M15W14-PR-A20-000503
FCV-W7018

M15W14-PR-A20-000310
XV-W7617E

M15W14-PR-A20-000309
XV-W7617D

M15W14-PR-A20-000308
XV-W7617C

M15W14-PR-A20-000307
XV-W7617B

M15W14-PR-A20-000306
XV-W7617A

M15W14-PR-A20-000309
XV-W7613D

M15W14-PR-A20-000309
XV-W7606D

M15W14-PR-A20-000309
XV-W7660D

M15W14-PR-A20-000309
XV-W7611D

M15W14-PR-A20-000309
XV-W7609D

M15W14-PR-A20-000309
XV-W7608D

M15W14-PR-A20-000309
FCV-W7610D

M15W14-PR-A20-000309
XV-W7610D

M15W14-PR-A20-000309
XV-W7607D

M15W14-PR-A20-000309
XV-W7604D

M15W14-PR-A20-000308
XV-W7613C

M15W14-PR-A20-000308
XV-W7606C

M15W14-PR-A20-000308
XV-W7605C

M15W14-PR-A20-000308
XV-W7611C

M15W14-PR-A20-000308
XV-W7609C

M15W14-PR-A20-000308
XV-W7608C

M15W14-PR-A20-000308
FCV-W7610C

M15W14-PR-A20-000308
XV-W7610C

M15W14-PR-A20-000308
XV-W7607C

M15W14-PR-A20-000308
XV-W7604C

50A-AIR-DRY-ST1-N-7067

M15W14-PR-A20-000501
AT-W7004~7007

15A-AIR-DRY-ST1-N-7003

TP
IF-R34

SKEP
VENDOR

15A-AIR-DRY-ST1-N-7027

15A-AIR-DRY-ST1-N-7028

M15W14-PR-A20-000305
XV-W7601A

M15W14-PR-A20-000305
XV-W7601B

50A-AIR-DRY-ST1-N-7029

50A-AIR-DRY-ST1-N-7030

15A-AIR-DRY-ST1-N-7031

15A-AIR-DRY-ST1-N-7032

15A-AIR-DRY-ST1-N-7033

15A-AIR-DRY-ST1-N-7033

15A-AIR-DRY-ST1-N-7035

15A-AIR-DRY-ST1-N-7036

15A-AIR-DRY-ST1-N-7037

15A-AIR-DRY-ST1-N-7039

15A-AIR-DRY-ST1-N-7104

15A-AIR-DRY-ST1-N-7038

15A-AIR-DRY-ST1-N-7040

M15W14-PR-A20-000305
XV-W7602E

M15W14-PR-A20-000305
XV-W7603E

M15W14-PR-A20-000305
XV-W7602D

M15W14-PR-A20-000305
XV-W7603D

M15W14-PR-A20-000305
XV-W7602C

M15W14-PR-A20-000305
XV-W7603C

M15W14-PR-A20-000305
XV-W7602B

M15W14-PR-A20-000305
XV-W7602A

M15W14-PR-A20-000305
XV-W7602F

M15W14-PR-A20-000305
XV-W7603B

M15W14-PR-A20-000305
XV-W7603A

50A-AIR-DRY-ST1-N-7030

15A-AIR-DRY-ST1-N-7002

15A-AIR-DRY-ST1-N-7004

M15W14-PR-A20-000504
AT-7002~7023

M15W14-PR-A20-000504
AT-7002~7023

15A-AIR-DRY-ST1-N-7041

15A-AIR-DRY-ST1-N-7042

15A-AIR-DRY-ST1-N-7043

15A-AIR-DRY-ST1-N-7044

15A-AIR-DRY-ST1-N-7045

15A-AIR-DRY-ST1-N-7055

15A-AIR-DRY-ST1-N-7054

15A-AIR-DRY-ST1-N-7053

15A-AIR-DRY-ST1-N-7052

15A-AIR-DRY-ST1-N-7051

15A-AIR-DRY-ST1-N-7050

15A-AIR-DRY-ST1-N-7049

15A-AIR-DRY-ST1-N-7048

15A-AIR-DRY-ST1-N-7047

15A-AIR-DRY-ST1-N-7046

15A-AIR-DRY-ST1-N-7065

15A-AIR-DRY-ST1-N-7064

15A-AIR-DRY-ST1-N-7063

15A-AIR-DRY-ST1-N-7062

15A-AIR-DRY-ST1-N-7061

15A-AIR-DRY-ST1-N-7060

15A-AIR-DRY-ST1-N-7059

15A-AIR-DRY-ST1-N-7058

15A-AIR-DRY-ST1-N-7057

15A-AIR-DRY-ST1-N-7056

15A-AIR-DRY-ST1-N-7066

M15W14-PR-A20-000310
XV-W7616E

M15W14-PR-A20-000309
XV-W7616D

M15W14-PR-A20-000308
XV-W7616C

M15W14-PR-A20-000307
XV-W7616B

M15W14-PR-A20-000306
XV-W7616A

M15W14-PR-A20-000307
XV-W7613B

M15W14-PR-A20-000307
XV-W7606B

M15W14-PR-A20-000307
XV-W7605B

M15W14-PR-A20-000307
XV-W7611B

M15W14-PR-A20-000307
XV-W7609B

M15W14-PR-A20-000307
XV-W7608B

M15W14-PR-A20-000307
FCV-W7610B

M15W14-PR-A20-000307
XV-W7610B

M15W14-PR-A20-000307
XV-W7607B

M15W14-PR-A20-000307
XV-W7604B

M15W14-PR-A20-000306
XV-W7613A

M15W14-PR-A20-000306
XV-W7606A

M15W14-PR-A20-000306
XV-W7605A

M15W14-PR-A20-000306
XV-W7611A

M15W14-PR-A20-000306
XV-W7609A

M15W14-PR-A20-000306
XV-W7608A

M15W14-PR-A20-000306
FCV-W7610A

M15W14-PR-A20-000306
XV-W7610A

M15W14-PR-A20-000306
XV-W7607A

M15W14-PR-A20-000306
XV-W7604A

M15W14-PR-A20-000506
FCV-W7025

50A-AIR-DRY-ST1-N-7026

AIR-DRY-648


대외비

KEY PLAN



NOTE

1. CLEAN DRY AIR LINES FOR XV AND FCV TO BE DEVELOPED.

0A	REVISED AFC	25.08.14
0	REVISED AFC	25.01.17
수정 REV.	실명 DESCRIPTION	날짜 DATE
제 DRAWN BY	이인학	
검 CHECKED BY	한진희	
승 APPROVED BY	박동영	
제 PROJECT TITLE	SK 에코플랜트	
공 PROJECT TITLE	M15X Ph4 WWT Project	
도면명 DWG. TITLE	UTILITY DISTRIBUTION DIAGRAM CLEAN DRY AIR DISTRIBUTION SYSTEM (3/3)	
축 SCALE	NONE	
날 DATE	2025. 08. 14	
PROJECT NO.	22330D	REV.
도면번호 SHEET NO.	CJ-M15W13-PR-A20-000082-B	0A

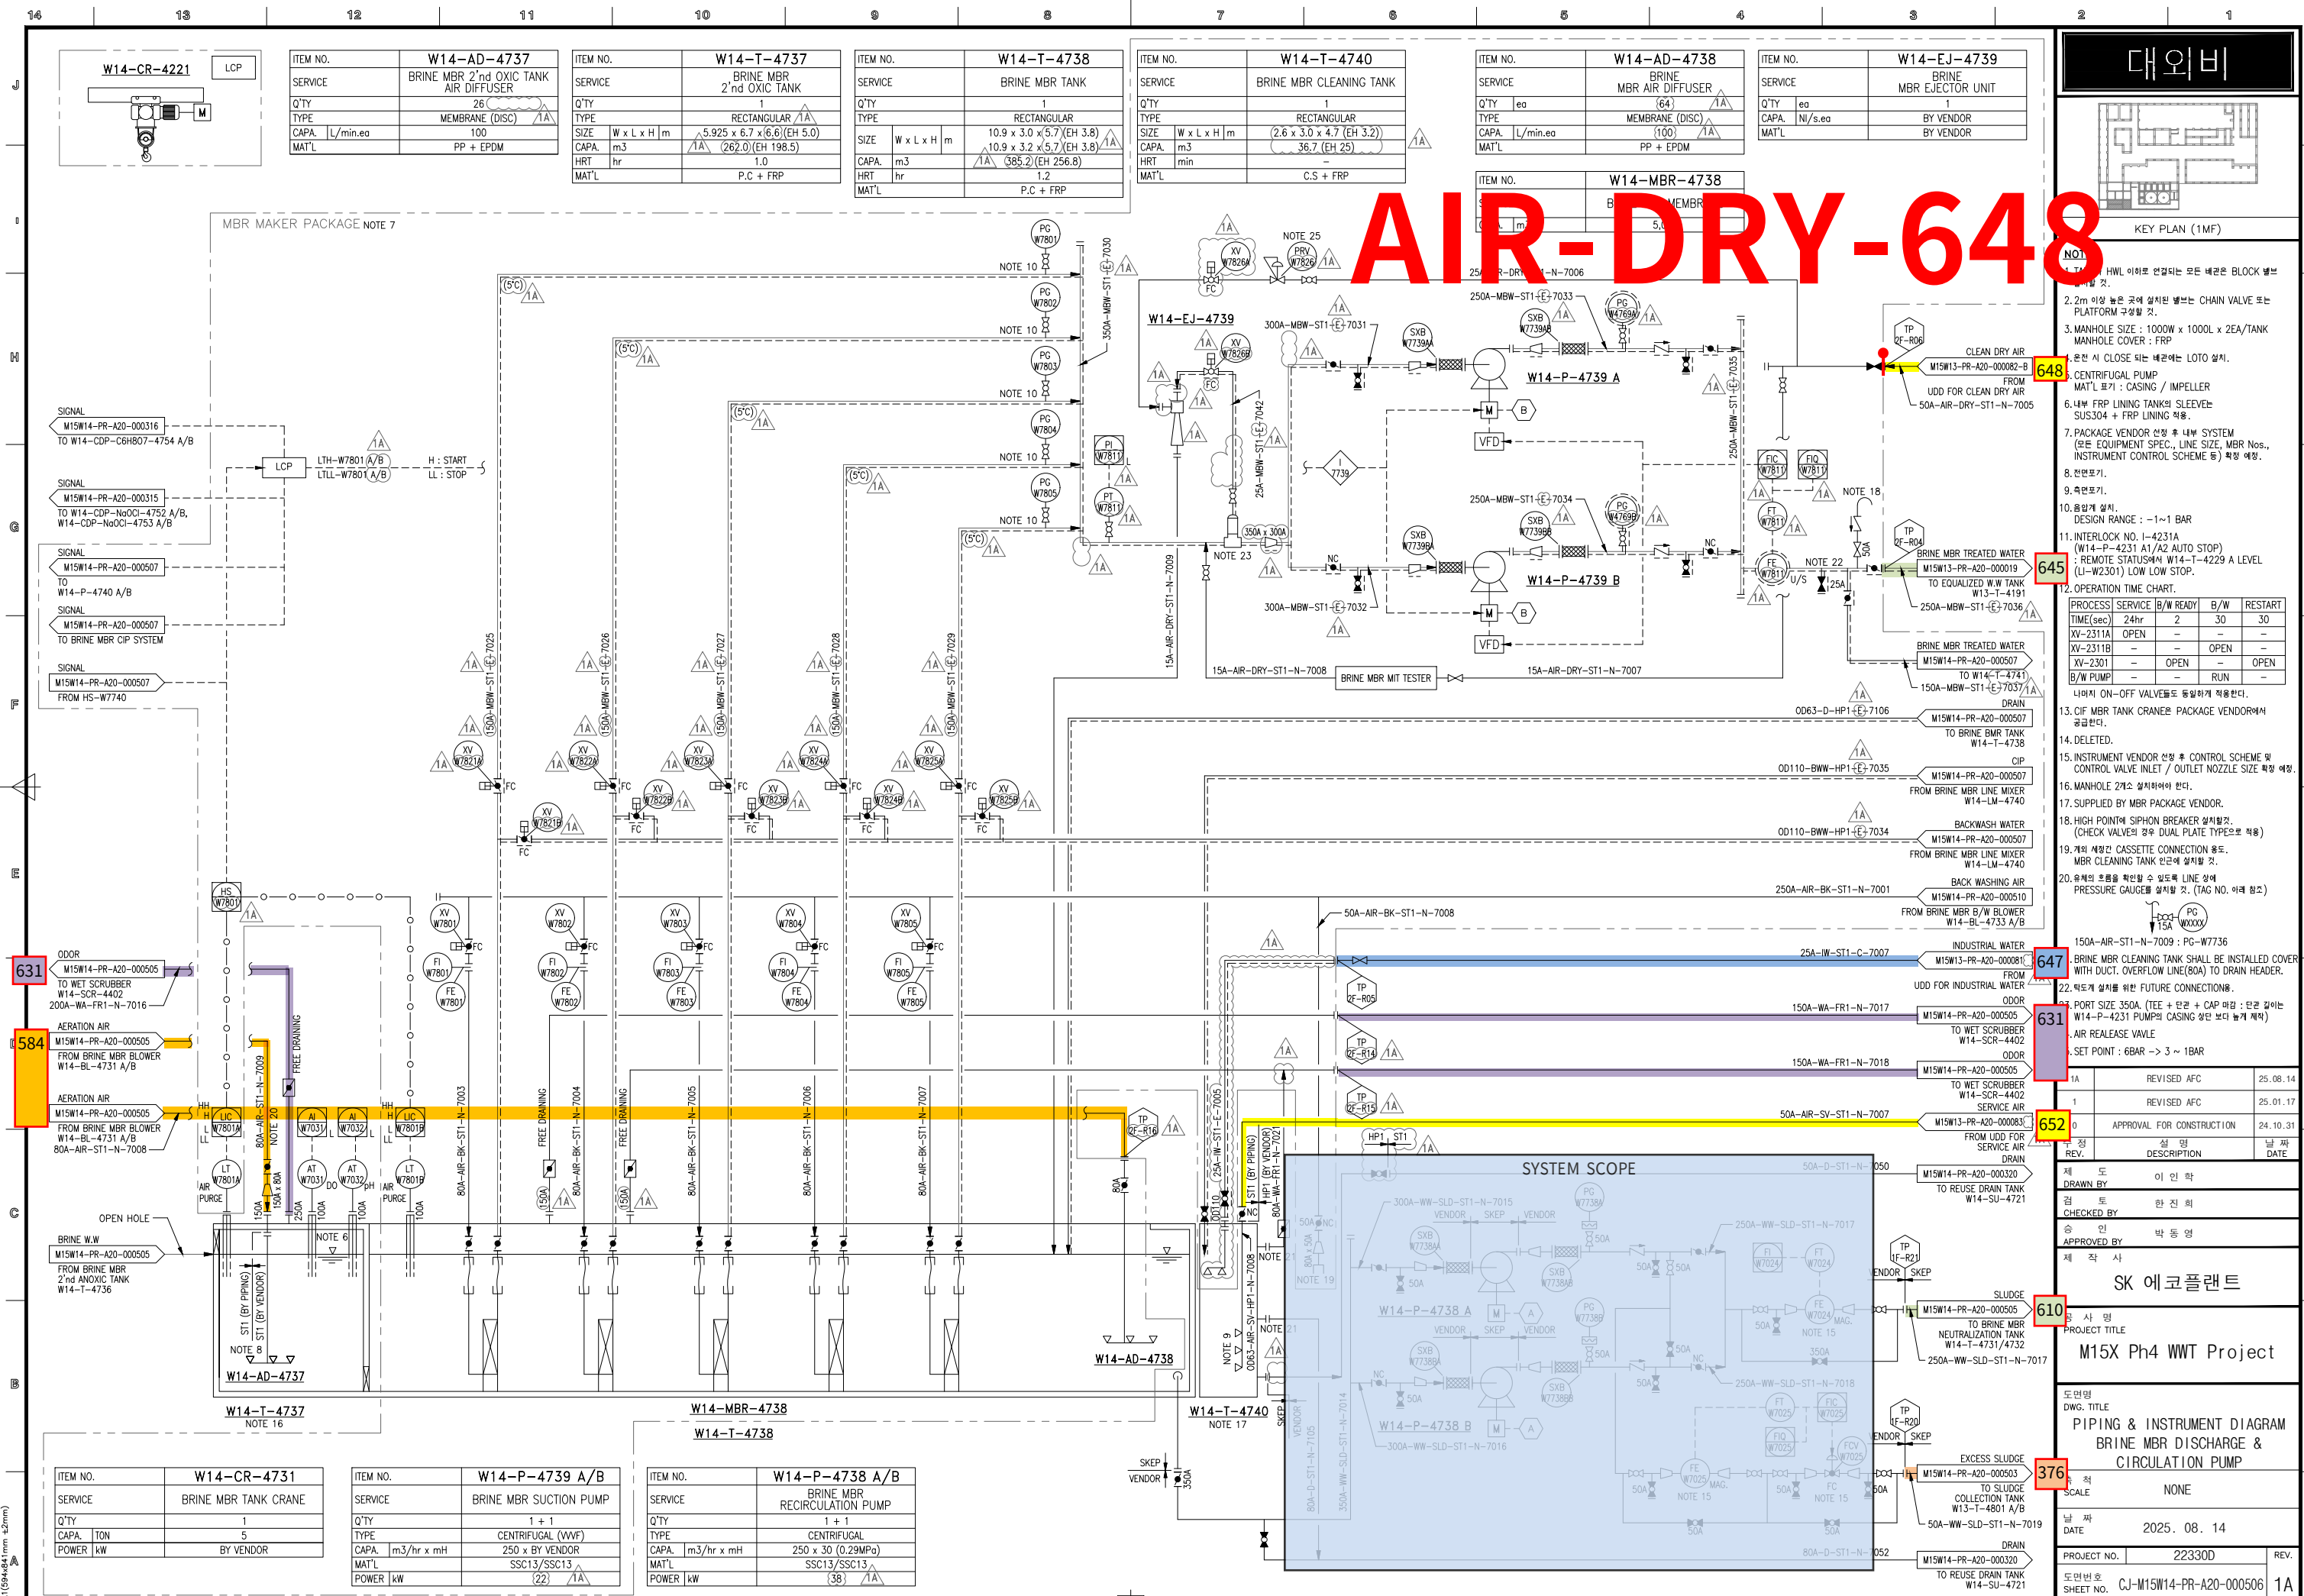

대외비

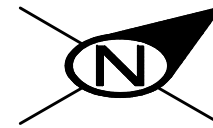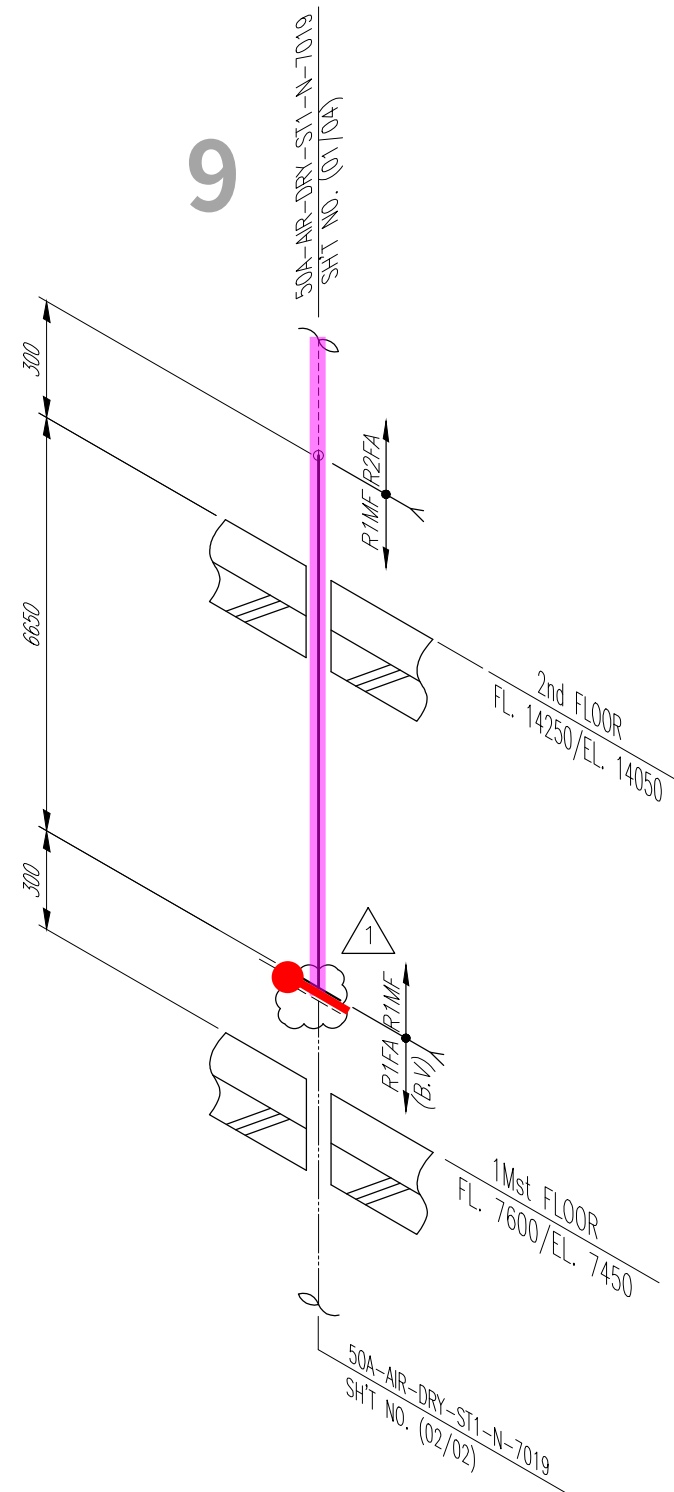A triangle with the number 1 inside.[illegible]

<NOTE>
1. (*) FIELD ADJUST

* PIPE : P/P1	* 90° ELBOW : E90	* 45° ELBOW : E45	* TEE : T	* RED.TEE : TR	* STUB-IN : STU	* REINFORCING PAD : RP	* CON.RED : RC	* ECC.RED : RE	* CON.SWAGE : RCS/RCS1	* ECC.SWAGE : RES/RES1	* NIPPLE : NP/NP1/NP2	* CAP : CAP/CAP1	* PLUG : PLG	* FULL COUPLING : FC	* HALF COUPLING : HF/HF1
* STUB-IN : STU	* SOCKET(HDPE/PVC) : SC	* SADDLE(HDPE) : SD	* FLANGE : F/F1	* GASKET : G/G1/G2	* BOLT & NUT : B/B1	* BLIND FLANGE : FB/FB1	* GATE VA. : VG/VG1/VG2	* BALL VA. : VB/VB10/VB1/VB10/VB2/VB20	* BUTTERFLY VA. : VF/VF4	* CHECK VA. : VC/VC1/VC2/VC3/VC4/VC5/VC6/VC7					
* GLOBE VA. : VL/VL1/VL2	* DIAPHRAGM VA. : VD/VD10	* DAMPER : VP	* QUICK COUPLING : SQC	* FLEXIBLE JOINT(STEEL) : FLXB	* FLEXIBLE JOINT(RUBBER) : FLXR	* FLEXIBLE JOINT(STEEL PTFE LINED) : FLXL	* FLEXIBLE HOSE : FLXH	* STEAM TRAP : ST	* SPRAY NOZZLE : SPN	* EMERGENCY SHOWER : SSH					
* STRAINER(Y-TYPE) : YSTR	* STRAINER(T-TYPE) : TSTR	* STRAINER(BUCKET-TYPE) : BSTR	* ANCHOR PLATE : STOP	* BIRD SCREEN : BS	* ISOLATION KIT : IK	* UNLOADING BOX : UB	* AIR TRAP : AT	* LOTO : LOTO	* SIGHT GLASS : SG	* PRESSURE GAUGE : PG	* SHILED : SH	* SPECIAL BOLT & NUT : BL/BL1			



CLIENT



1

INSULATION	CODE	N	CONDITION	PRESS. (kg/cm2g)	TEMP. (°C)	AREA	W14							CONTRACTOR	PROJECT NAME	
	THICK.	—	DESIGN	10	60	UNIT	R1MF								M15X Ph4 Project	
			OPERATING	7.5	AMB	REF. PLAN DWG.			25.03.31	REVISED AS MARKED	황래중	안남후	박동영	COMMODITY	JOB NO.	
						CJ-M15W14-PI-A30-010017-D			25.01.24	APPROVED FOR CONSTRUCTION	황래중	안남후	박동영	AIR-DRY	22330D	
					REF. P & ID			REV. NO.	DATE	DESCRIPTION	BY	CHK	APP'D	LINE NO.	SH'T NO.	REV.
					CJ-M15W14-PR-A20-000082-B									50A-AIR-DRY-ST1-N-7019	01 / 01	1

경고 : 본 도면은 SK HYNIX의 기밀비밀 자료로서, 어떠한 경우에도 목적 외 사용, 복제, 제3자에게 공개, 누설 및 유출할 수 없으며, 회사는 유표자의 불법 사용으로 피해가 발생할 경우 유표자에게 민/형사상 책임을 요구할 수 있음.

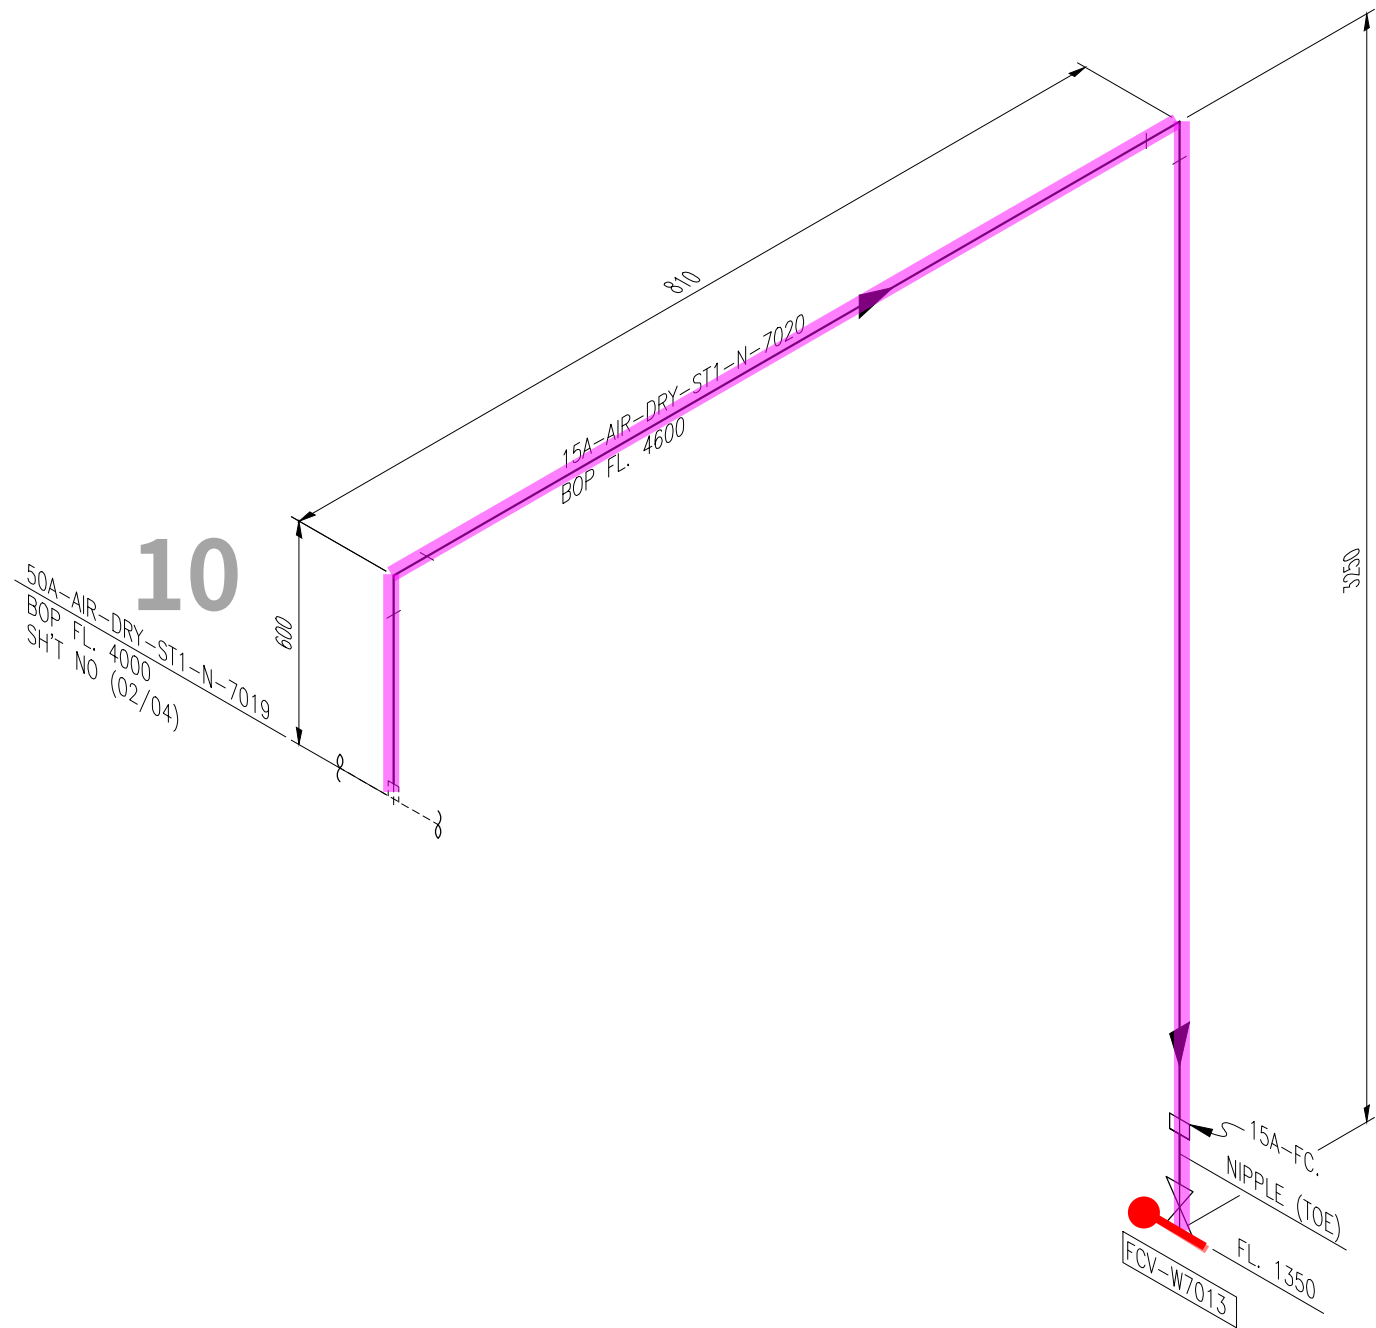
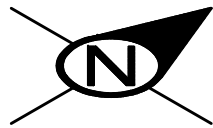


<NOTE>
1. (*) FIELD ADJUST

* PIPE : P/P1 * 90° ELBOW : E90 * 45° ELBOW : E45 * TEE : T * RED.TEE : TR * STUB-IN : STU * REINFORCING PAD : RP * CON.RED : RC * ECC.RED : RE * CON.SWAGE : RCS/RCS1 * ECC.SWAGE : RES/RES1 * NIPPLE : NP/NP1/NP2 * CAP : CAP/CAP1 * PLUG : PLG * FULL COUPLING : FC * HALF COUPLING : HF/HF1
* STUB-IN : STU * SOCKET(HDPE/PVC) : SC * SADDLE(HDPE) : SD * FLANGE : F/F1 * GASKET : G/G1/G2 * BOLT & NUT : B/B1 * BLIND FLANGE : FB/FB1 * GATE VA. : VG/VG1/VG2 * BALL VA. : VB/VBLO/VB1/VB1LO/VB2/VB2LO * BUTTERFLY VA. : VF/VF4 * CHECK VA. : VC/VC1/VC2/VC3/VC4/VC5/VC6/VC7
* GLOBE VA. : VL/VL1/VL2 * DIAPHRAGM VA. : VD/VDLO * DAMPER : VP * QUICK COUPLING : SQC * FLEXIBLE JOINT(STEEL) : FLXB * FLEXIBLE JOINT(RUBBER) : FLXR * FLEXIBLE JOINT(STEEL PTFE LINED) : FLXL * FLEXIBLE HOSE : FLXH * STEAM TRAP : ST * SPRAY NOZZLE : SPN * EMERGENCY SHOWER : SSH
* STRAINER(Y-TYPE) : YSTR * STRAINER(T-TYPE) : TSTR * STRAINER(BUCKET-TYPE) : BSTR * ANCHOR PLATE : STOP * BIRD SCREEN : BS * ISOLATION KIT : IK * UNLOADING BOX : UB * AIR TRAP : AT * LOTO : LOTO * SIGHT GLASS : SG * PRESSURE GAUGE : PG * SHILED : SH * SPECIAL BOLT & NUT : BL/BL1

INSULATION	CODE	N	CONDITION	PRESS. (kg/cm2g)	TEMP. (°C)	AREA	W14									CONTRACTOR	PROJECT NAME
	THICK.	-	DESIGN	10	60	UNIT	R2FA									SK ecoplant	M15X Ph4 Project
			OPERATING	7.5	AMB	REF. PLAN DWG.										COMMODITY	JOB NO.
						CJ-M15W14-PI-A30-020015-A										AIR-DRY	22330D
						REF. P & ID										LINE NO.	SH'T NO.
						CJ-M15W14-PR-A20-000082-B										15A-AIR-DRY-ST1-N-7020	01 / 01
																	REV.
																	0

경고 : 본 도면은 SK HYNIX의 기밀비밀 자료로서, 어떠한 경우에도 목적 외 사용, 복제, 제3자에게 공개, 누설 및 유출할 수 없으며, 회사는 유포자의 불법 사용으로 피해가 발생할 경우 유포자에게 민/형사상 책임을 요구할 수 있음.

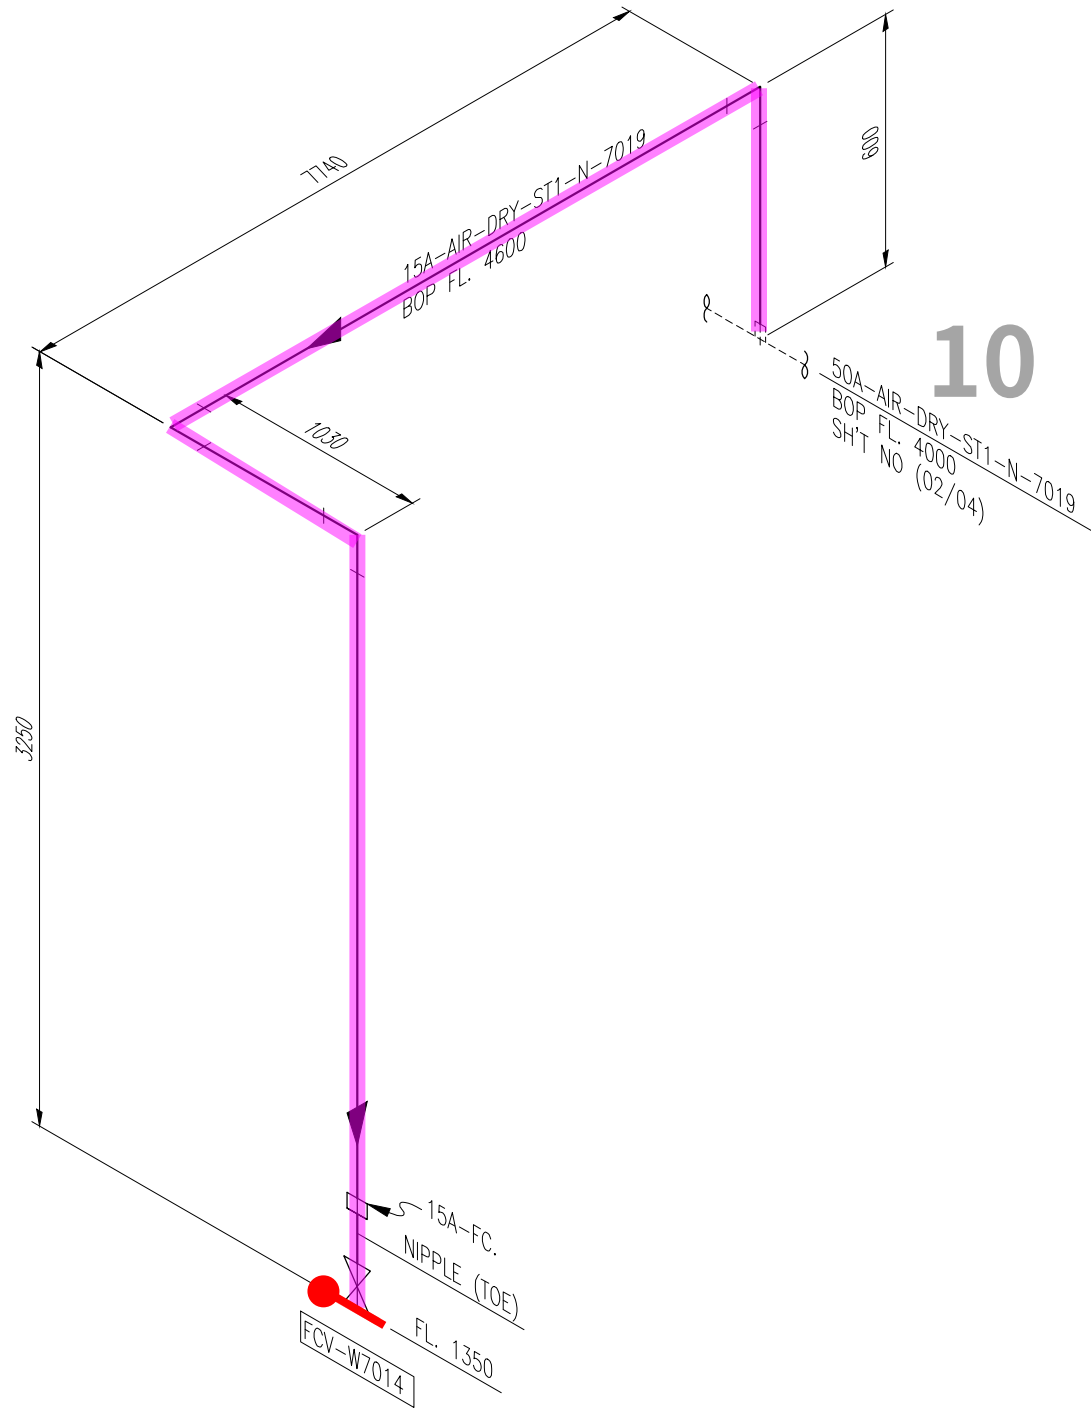
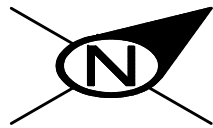


<NOTE>
1. (*) FIELD ADJUST

* PIPE : P/P1 * 90° ELBOW : E90 * 45° ELBOW : E45 * TEE : T * RED.TEE : TR * STUB-IN : STU * REINFORCING PAD : RP * CON.RED : RC * ECC.RED : RE * CON.SWAGE : RCS/RCS1 * ECC.SWAGE : RES/RES1 * NIPPLE : NP/NP1/NP2 * CAP : CAP/CAP1 * PLUG : PLG * FULL COUPLING : FC * HALF COUPLING : HF/HF1
* STUB-IN : STU * SOCKET(HDPE/PVC) : SC * SADDLE(HDPE) : SD * FLANGE : F/F1 * GASKET : G/G1/G2 * BOLT & NUT : B/B1 * BLIND FLANGE : FB/FB1 * GATE VA. : VG/VG1/VG2 * BALL VA. : VB/VBLO/VB1/VB1LO/VB2/VB2LO * BUTTERFLY VA. : VF/VF4 * CHECK VA. : VC/VC1/VC2/VC3/VC4/VC5/VC6/VC7
* GLOBE VA. : VL/VL1/VL2 * DIAPHRAGM VA. : VD/VDLO * DAMPER : VP * QUICK COUPLING : SQC * FLEXIBLE JOINT(STEEL) : FLXB * FLEXIBLE JOINT(RUBBER) : FLXR * FLEXIBLE JOINT(STEEL PTFE LINED) : FLXL * FLEXIBLE HOSE : FLXH * STEAM TRAP : ST * SPRAY NOZZLE : SPN * EMERGENCY SHOWER : SSH
* STRAINER(Y-TYPE) : YSTR * STRAINER(T-TYPE) : TSTR * STRAINER(BUCKET-TYPE) : BSTR * ANCHOR PLATE : STOP * BIRD SCREEN : BS * ISOLATION KIT : IK * UNLOADING BOX : UB * AIR TRAP : AT * LOTO : LOTO * SIGHT GLASS : SG * PRESSURE GAUGE : PG * SHILED : SH * SPECIAL BOLT & NUT : BL/BL1

INSULATION	CODE	N	CONDITION	PRESS. (kg/cm2g)	TEMP. (°C)	AREA	W14									CONTRACTOR	PROJECT NAME
	THICK.	-	DESIGN	10	60	UNIT	R2FA									SK ecoplant	M15X Ph4 Project
			OPERATING	7.5	AMB	REF. PLAN DWG.										COMMODITY	JOB NO.
						CJ-M15W14-PI-A30-020015-A										AIR-DRY	22330D
						REF. P & ID										LINE NO.	SH'T NO.
						CJ-M15W14-PR-A20-000082-B										15A-AIR-DRY-ST1-N-7019	01 / 01
																	REV.
																	0

경고 : 본 도면은 SK HYNIX의 기밀비밀 자료로서, 어떠한 경우에도 목적 외 사용, 복제, 제3자에게 공개, 누설 및 유출할 수 없으며, 회사는 유포자의 불법 사용으로 피해가 발생할 경우 유포자에게 민/형사상 책임을 요구할 수 있음.

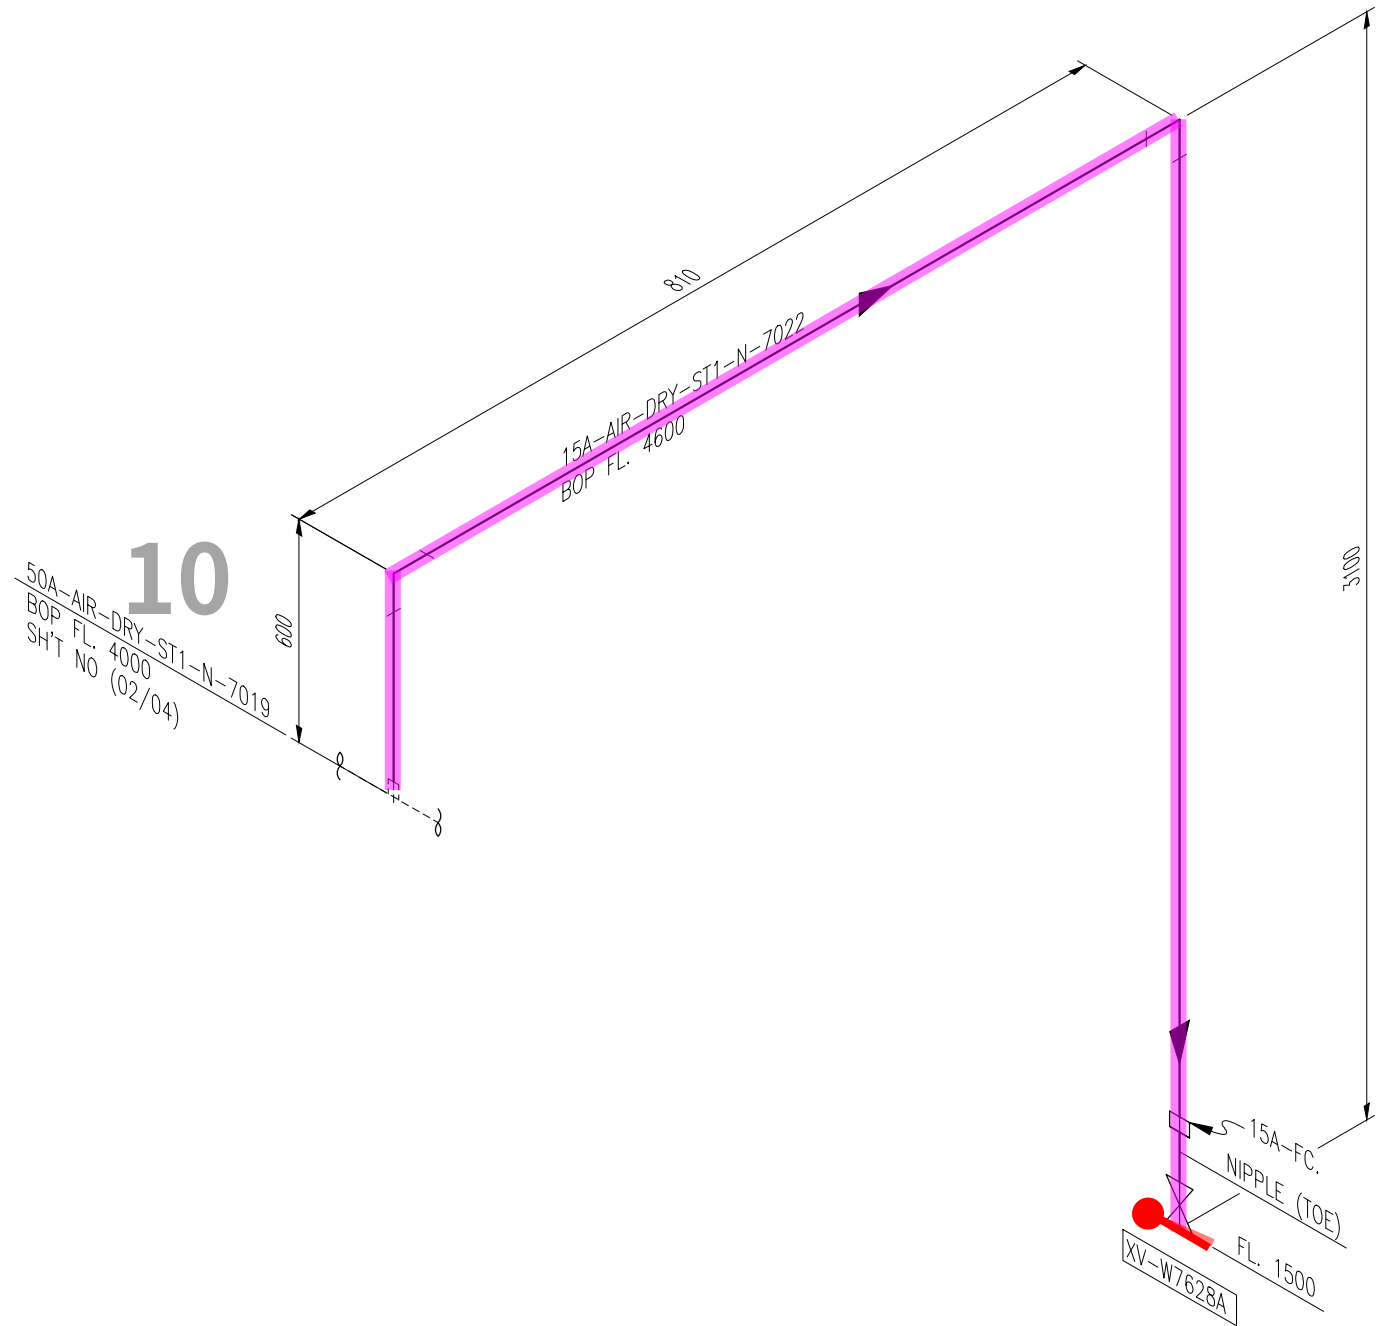
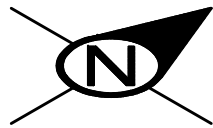


<NOTE>
1. (*) FIELD ADJUST

* PIPE : P/P1 * 90° ELBOW : E90 * 45° ELBOW : E45 * TEE : T * RED.TEE : TR * STUB-IN : STU * REINFORCING PAD : RP * CON.RED : RC * ECC.RED : RE * CON.SWAGE : RCS/RCS1 * ECC.SWAGE : RES/RES1 * NIPPLE : NP/NP1/NP2 * CAP : CAP/CAP1 * PLUG : PLG * FULL COUPLING : FC * HALF COUPLING : HF/HF1
* STUB-IN : STU * SOCKET(HDPE/PVC) : SC * SADDLE(HDPE) : SD * FLANGE : F/F1 * GASKET : G/G1/G2 * BOLT & NUT : B/B1 * BLIND FLANGE : FB/FB1 * GATE VA. : VG/VG1/VG2 * BALL VA. : VB/VBLO/VB1/VB1LO/VB2/VB2LO * BUTTERFLY VA. : VF/VF4 * CHECK VA. : VC/VC1/VC2/VC3/VC4/VC5/VC6/VC7
* GLOBE VA. : VL/VL1/VL2 * DIAPHRAGM VA. : VD/VDLO * DAMPER : VP * QUICK COUPLING : SQC * FLEXIBLE JOINT(STEEL) : FLXB * FLEXIBLE JOINT(RUBBER) : FLXR * FLEXIBLE JOINT(STEEL PTFE LINED) : FLXL * FLEXIBLE HOSE : FLXH * STEAM TRAP : ST * SPRAY NOZZLE : SPN * EMERGENCY SHOWER : SSH
* STRAINER(Y-TYPE) : YSTR * STRAINER(T-TYPE) : TSTR * STRAINER(BUCKET-TYPE) : BSTR * ANCHOR PLATE : STOP * BIRD SCREEN : BS * ISOLATION KIT : IK * UNLOADING BOX : UB * AIR TRAP : AT * LOTO : LOTO * SIGHT GLASS : SG * PRESSURE GAUGE : PG * SHILED : SH * SPECIAL BOLT & NUT : BL/BL1

INSULATION	CODE	N	CONDITION	PRESS. (kg/cm2g)	TEMP. (°C)	AREA	W14									CONTRACTOR	PROJECT NAME
	THICK.	-	DESIGN	10	60	UNIT	R2FA									SK ecoplant	M15X Ph4 Project
			OPERATING	7.5	AMB	REF. PLAN DWG.										COMMODITY	JOB NO.
						CJ-M15W14-PI-A30-020015-B										AIR-DRY	22330D
						REF. P & ID										LINE NO.	SH'T NO.
						CJ-M15W14-PR-A20-000082-B										15A-AIR-DRY-ST1-N-7022	01 / 01
																	REV.
																	0

경고 : 본 도면은 SK HYNIX의 기밀비밀 자료로서, 어떠한 경우에도 목적 외 사용, 복제, 제3자에게 공개, 누설 및 유출할 수 없으며, 회사는 유포자의 불법 사용으로 피해가 발생할 경우 유포자에게 민/형사상 책임을 요구할 수 있음.

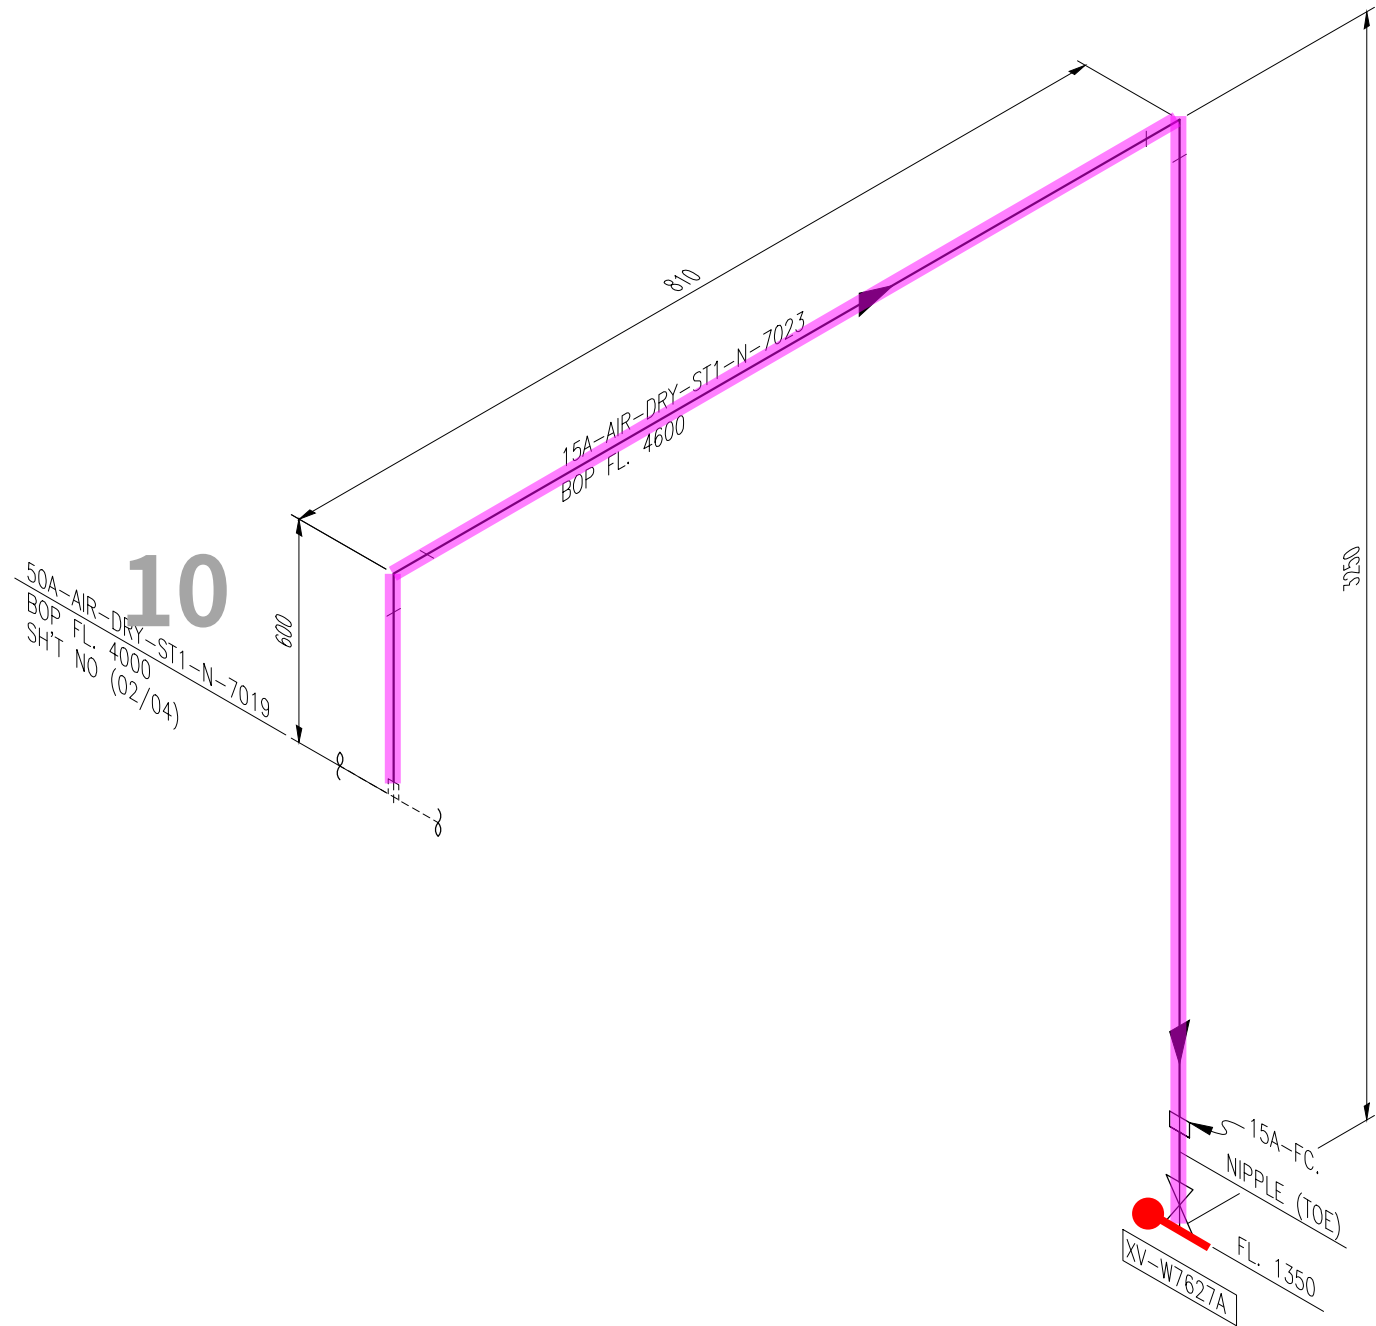
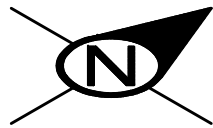


<NOTE>
1. (*) FIELD ADJUST

* PIPE : P/P1 * 90° ELBOW : E90 * 45° ELBOW : E45 * TEE : T * RED.TEE : TR * STUB-IN : STU * REINFORCING PAD : RP * CON.RED : RC * ECC.RED : RE * CON.SWAGE : RCS/RCS1 * ECC.SWAGE : RES/RES1 * NIPPLE : NP/NP1/NP2 * CAP : CAP/CAP1 * PLUG : PLG * FULL COUPLING : FC * HALF COUPLING : HF/HF1
* STUB-IN : STU * SOCKET(HDPE/PVC) : SC * SADDLE(HDPE) : SD * FLANGE : F/F1 * GASKET : G/G1/G2 * BOLT & NUT : B/B1 * BLIND FLANGE : FB/FB1 * GATE VA. : VG/VG1/VG2 * BALL VA. : VB/VBLO/VB1/VB1LO/VB2/VB2LO * BUTTERFLY VA. : VF/VF4 * CHECK VA. : VC/VC1/VC2/VC3/VC4/VC5/VC6/VC7
* GLOBE VA. : VL/VL1/VL2 * DIAPHRAGM VA. : VD/VDLO * DAMPER : VP * QUICK COUPLING : SQC * FLEXIBLE JOINT(STEEL) : FLXB * FLEXIBLE JOINT(RUBBER) : FLXR * FLEXIBLE JOINT(STEEL PTFE LINED) : FLXL * FLEXIBLE HOSE : FLXH * STEAM TRAP : ST * SPRAY NOZZLE : SPN * EMERGENCY SHOWER : SSH
* STRAINER(Y-TYPE) : YSTR * STRAINER(T-TYPE) : TSTR * STRAINER(BUCKET-TYPE) : BSTR * ANCHOR PLATE : STOP * BIRD SCREEN : BS * ISOLATION KIT : IK * UNLOADING BOX : UB * AIR TRAP : AT * LOTO : LOTO * SIGHT GLASS : SG * PRESSURE GAUGE : PG * SHILED : SH * SPECIAL BOLT & NUT : BL/BL1

INSULATION	CODE	N	CONDITION	PRESS. (kg/cm2g)	TEMP. (°C)	AREA	W14									CONTRACTOR	PROJECT NAME
	THICK.	-	DESIGN	10	60	UNIT	R2FA									SK ecoplant	M15X Ph4 Project
			OPERATING	7.5	AMB	REF. PLAN DWG.										COMMODITY	JOB NO.
						CJ-M15W14-PI-A30-020016-A										AIR-DRY	22330D
						REF. P & ID										LINE NO.	SH'T NO.
						CJ-M15W14-PR-A20-000082-B										15A-AIR-DRY-ST1-N-7023	01 / 01
																	REV.
																	0

경고 : 본 도면은 SK HYNIX의 기밀비밀 자료로서, 어떠한 경우에도 목적 외 사용, 복제, 제3자에게 공개, 누설 및 유출할 수 없으며, 회사는 유포자의 불법 사용으로 피해가 발생할 경우 유포자에게 민/형사상 책임을 요구할 수 있음.

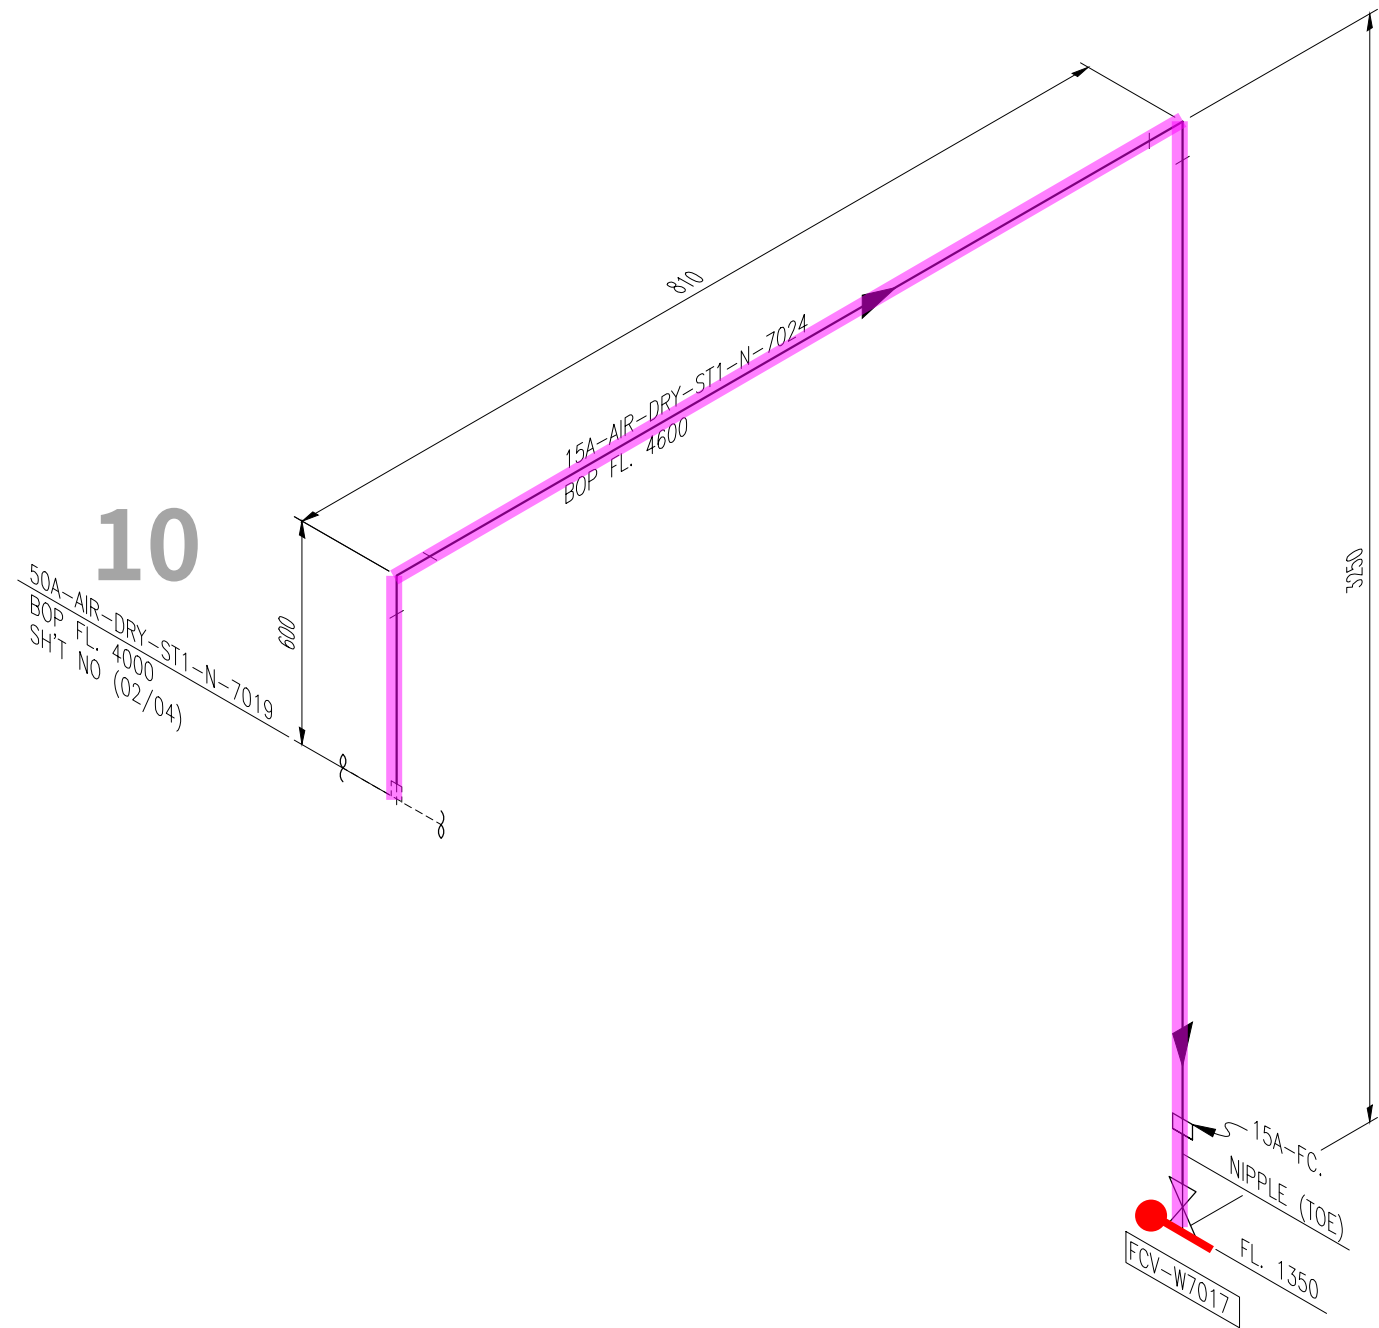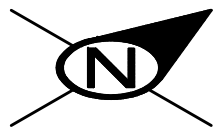


<NOTE>
1. (*) FIELD ADJUST

* PIPE : P/P1 * 90° ELBOW : E90 * 45° ELBOW : E45 * TEE : T * RED.TEE : TR * STUB-IN : STU * REINFORCING PAD : RP * CON.RED : RC * ECC.RED : RE * CON.SWAGE : RCS/RCS1 * ECC.SWAGE : RES/RES1 * NIPPLE : NP/NP1/NP2 * CAP : CAP/CAP1 * PLUG : PLG * FULL COUPLING : FC * HALF COUPLING : HF/HF1
* STUB-IN : STU * SOCKET(HDPE/PVC) : SC * SADDLE(HDPE) : SD * FLANGE : F/F1 * GASKET : G/G1/G2 * BOLT & NUT : B/B1 * BLIND FLANGE : FB/FB1 * GATE VA. : VG/VG1/VG2 * BALL VA. : VB/VBLO/VB1/VB1LO/VB2/VB2LO * BUTTERFLY VA. : VF/VF4 * CHECK VA. : VC/VC1/VC2/VC3/VC4/VC5/VC6/VC7
* GLOBE VA. : VL/VL1/VL2 * DIAPHRAGM VA. : VD/VDLO * DAMPER : VP * QUICK COUPLING : SQC * FLEXIBLE JOINT(STEEL) : FLXB * FLEXIBLE JOINT(RUBBER) : FLXR * FLEXIBLE JOINT(STEEL PTFE LINED) : FLXL * FLEXIBLE HOSE : FLXH * STEAM TRAP : ST * SPRAY NOZZLE : SPN * EMERGENCY SHOWER : SSH
* STRAINER(Y-TYPE) : YSTR * STRAINER(T-TYPE) : TSTR * STRAINER(BUCKET-TYPE) : BSTR * ANCHOR PLATE : STOP * BIRD SCREEN : BS * ISOLATION KIT : IK * UNLOADING BOX : UB * AIR TRAP : AT * LOTO : LOTO * SIGHT GLASS : SG * PRESSURE GAUGE : PG * SHILED : SH * SPECIAL BOLT & NUT : BL/BL1

INSULATION	CODE	N	CONDITION	PRESS. (kg/cm2g)	TEMP. (°C)	AREA	W14									CONTRACTOR	PROJECT NAME
	THICK.	-	DESIGN	10	60	UNIT	R2FA									SK ecoplant	M15X Ph4 Project
			OPERATING	7.5	AMB	REF. PLAN DWG.										COMMODITY	JOB NO.
						CJ-M15W14-PI-A30-020016-A										AIR-DRY	22330D
						REF. P & ID										LINE NO.	SH'T NO.
						CJ-M15W14-PR-A20-000082-B										15A-AIR-DRY-ST1-N-7024	01 / 01
																	REV.
																	0

경고 : 본 도면은 SK HYNIX의 기밀비밀 자료로서, 어떠한 경우에도 목적 외 사용, 복제, 제3자에게 공개, 누설 및 유출할 수 없으며, 회사는 유포자의 불법 사용으로 피해가 발생할 경우 유포자에게 민/형사상 책임을 요구할 수 있음.

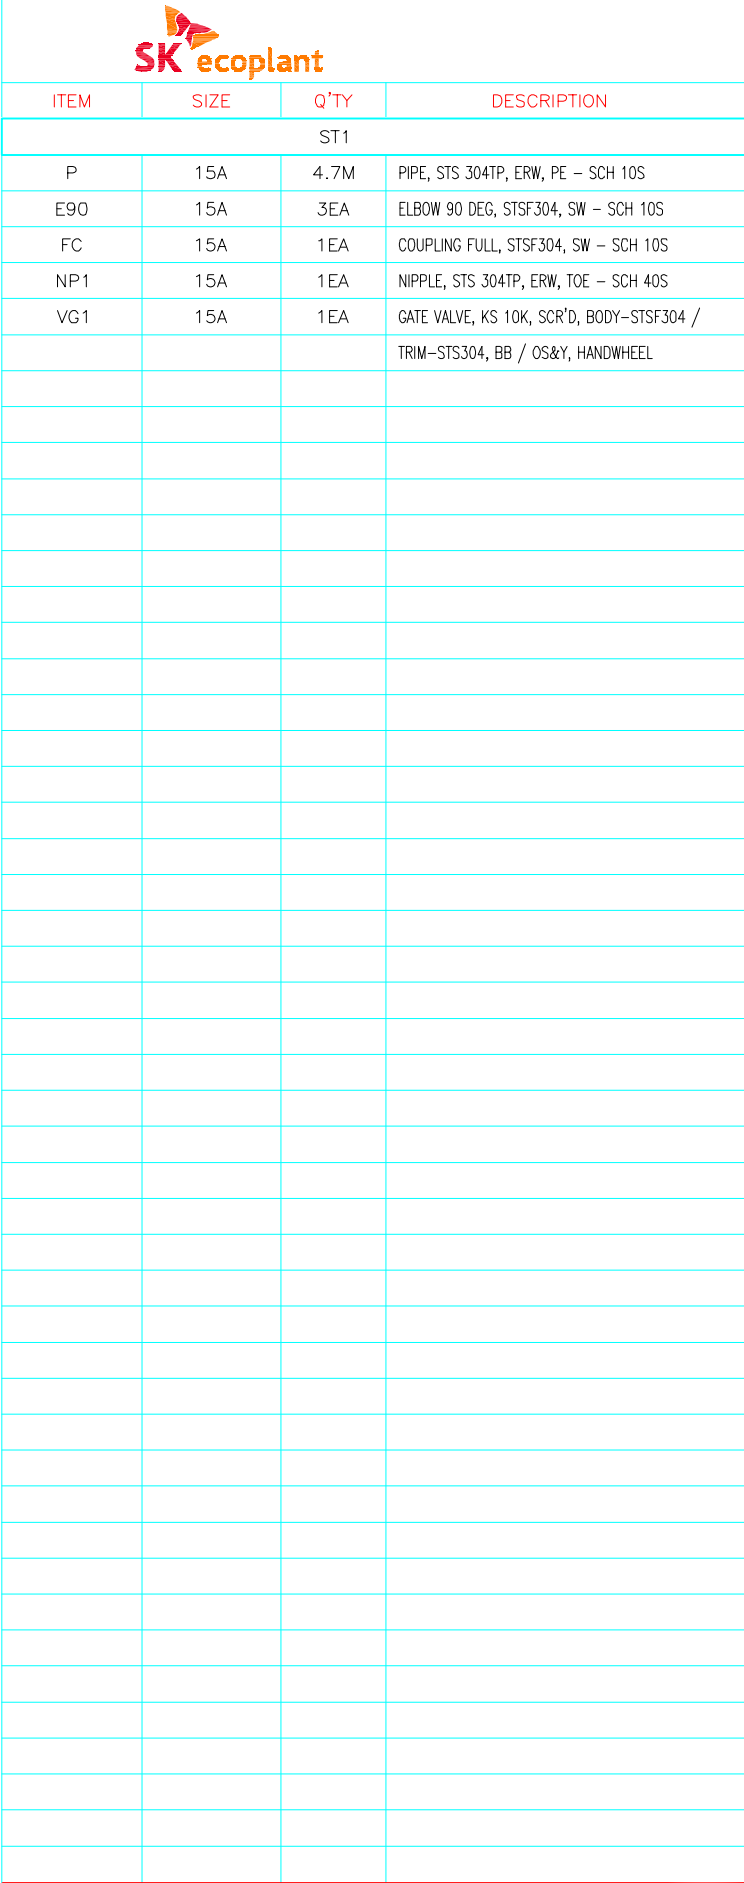

CLIENT		6	
		PROJECT NAME	
		M15X Ph4 Project	
COMMODITY		JOB NO.	
AIR-DRY		22330D	
LINE NO.	15A-AIR-DRY-ST1-N-7024	SH'T NO.	REV.
		01 / 01	0


[illegible]

<NOTE>
1. (*) FIELD ADJUST

* PIPE : P/P1	* 90° ELBOW : E90	* 45° ELBOW : E45	* TEE : T	* RED.TEE : TR	* STUB-IN : STU	* REINFORCING PAD : RP	* CON.RED : RC	* ECC.RED : RE	* CON.SWAGE : RCS/RCS1	* ECC.SWAGE : RES/RES1	* NIPPLE : NP/NP1/NP2	* CAP : CAP/CAP1	* PLUG : PLG	* FULL COUPLING : FC	* HALF COUPLING : HF/HF1
* STUB-IN : STU	* SOCKET(HDPE/PVC) : SC	* SADDLE(HDPE) : SD	* FLANGE : F/F1	* GASKET : G/G1/G2	* BOLT & NUT : B/B1	* BLIND FLANGE : FB/FB1	* GATE VA. : VG/VG1/VG2	* BALL VA. : VB/VB10/VB1/VB10/VB2/VB20	* BUTTERFLY VA. : VF/VF4	* CHECK VA. : VC/VC1/VC2/VC3/VC4/VC5/VC6/VC7					
* GLOBE VA. : VL/VL1/VL2	* DIAPHRAGM VA. : VD/VD10	* DAMPER : VP	* QUICK COUPLING : SQC	* FLEXIBLE JOINT(STEEL) : FLXB	* FLEXIBLE JOINT(RUBBER) : FLXR	* FLEXIBLE JOINT(STEEL PTFE LINED) : FLXL	* FLEXIBLE HOSE : FLXH	* STEAM TRAP : ST	* SPRAY NOZZLE : SPN	* EMERGENCY SHOWER : SSH					
* STRAINER(Y-TYPE) : YSTR	* STRAINER(T-TYPE) : TSTR	* STRAINER(BUCKET-TYPE) : BSTR	* ANCHOR PLATE : STOP	* BIRD SCREEN : BS	* ISOLATION KIT : IK	* UNLOADING BOX : UB	* AIR TRAP : AT	* LOTO : LOTO	* SIGHT GLASS : SG	* PRESSURE GAUGE : PG	* SHILED : SH	* SPECIAL BOLT & NUT : BL/BL1			

INSULATION	CODE	N	CONDITION	PRESS. (kg/cm2g)	TEMP. (°C)	AREA W14						CONTRACTOR	PROJECT NAME	
	THICK.	—	DESIGN	10	60	UNIT R2FA							M15X Ph4 Project	
			OPERATING	7.5	AMB	REF. PLAN DWG.						COMMODITY	JOB NO.	
						CJ-M15W14-PI-A30-020016-A		25.01.24	APPROVED FOR CONSTRUCTION	황래중	안남후	박동영	22330D	
					REF. P & ID	REV. NO.	DATE	DESCRIPTION	BY	CHK	APP'D	LINE NO.	SH'T NO.	REV.
					CJ-M15W14-PR-A20-000082-B							15A-AIR-DRY-ST1-N-7025	01 / 01	0

경고 : 본 도면은 SK HYNIX의 기밀비밀 자료로서, 어떠한 경우에도 목적 외 사용, 복제, 제3자에게 공개, 누설 및 유출할 수 없으며, 회사는 유포자의 불법 사용으로 피해가 발생할 경우 유포자에게 민/형사상 책임을 요구할 수 있음.

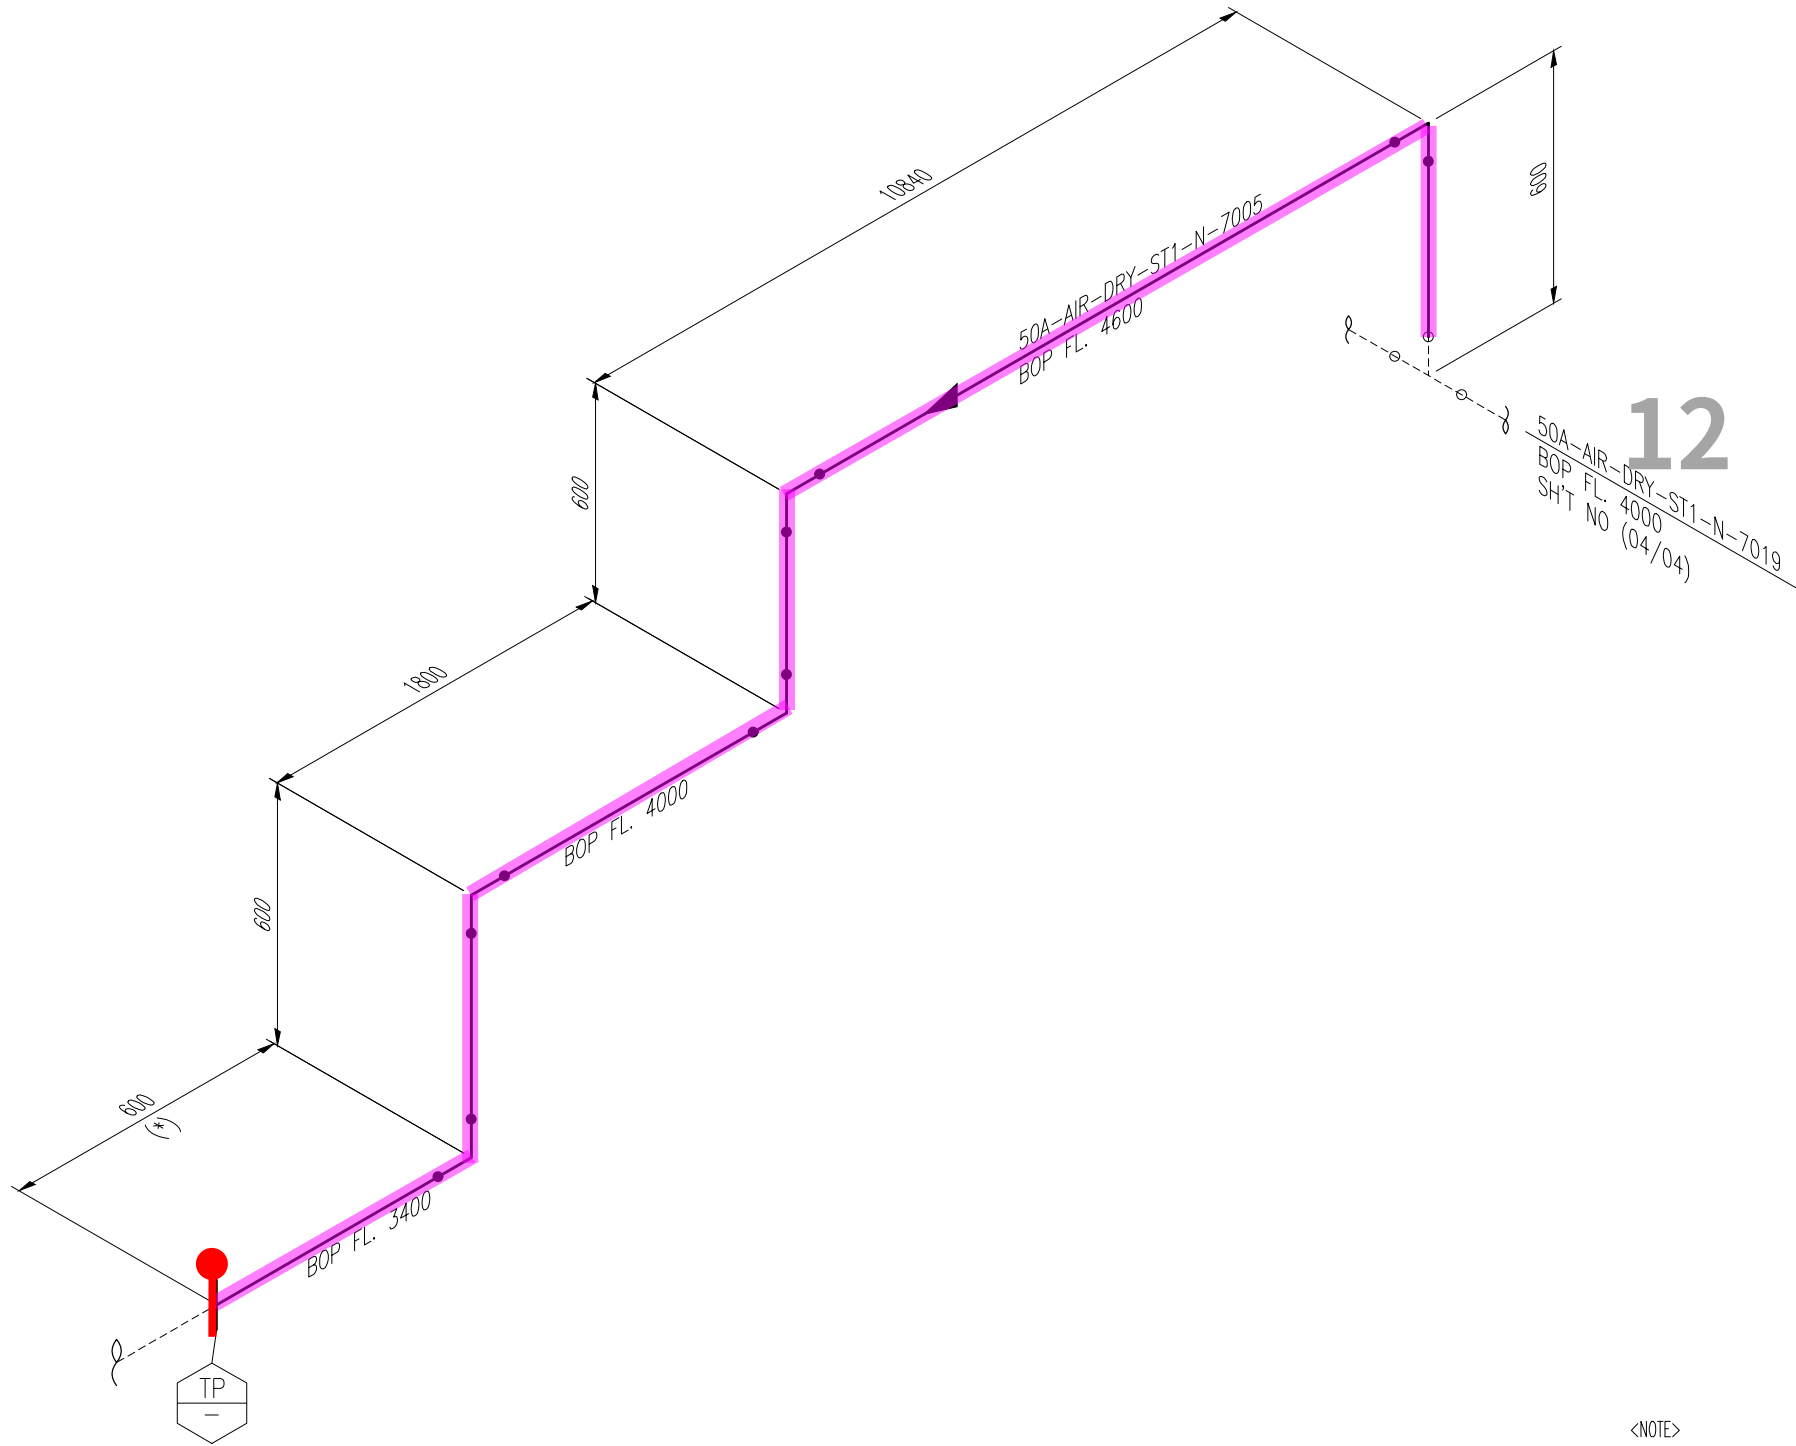


<NOTE>
1. (*) FIELD ADJUST

* PIPE : P/P1 * 90° ELBOW : E90 * 45° ELBOW : E45 * TEE : T * RED.TEE : TR * STUB-IN : STU * REINFORCING PAD : RP * CON.RED : RC * ECC.RED : RE * CON.SWAGE : RCS/RCS1 * ECC.SWAGE : RES/RES1 * NIPPLE : NP/NP1/NP2 * CAP : CAP/CAP1 * PLUG : PLG * FULL COUPLING : FC * HALF COUPLING : HF/HF1
* STUB-IN : STU * SOCKET(HDPE/PVC) : SC * SADDLE(HDPE) : SD * FLANGE : F/F1 * GASKET : G/G1/G2 * BOLT & NUT : B/B1 * BLIND FLANGE : FB/FB1 * GATE VA. : VG/VG1/VG2 * BALL VA. : VB/VBLO/VB1/VB1LO/VB2/VB2LO * BUTTERFLY VA. : VF/VF4 * CHECK VA. : VC/VC1/VC2/VC3/VC4/VC5/VC6/VC7
* GLOBE VA. : VL/VL1/VL2 * DIAPHRAGM VA. : VD/VDLO * DAMPER : VP * QUICK COUPLING : SQC * FLEXIBLE JOINT(STEEL) : FLXB * FLEXIBLE JOINT(RUBBER) : FLXR * FLEXIBLE JOINT(STEEL PTFE LINED) : FLXL * FLEXIBLE HOSE : FLXH * STEAM TRAP : ST * SPRAY NOZZLE : SPN * EMERGENCY SHOWER : SSH
* STRAINER(Y-TYPE) : YSTR * STRAINER(T-TYPE) : TSTR * STRAINER(BUCKET-TYPE) : BSTR * ANCHOR PLATE : STOP * BIRD SCREEN : BS * ISOLATION KIT : IK * UNLOADING BOX : UB * AIR TRAP : AT * LOTO : LOTO * SIGHT GLASS : SG * PRESSURE GAUGE : PG * SHILED : SH * SPECIAL BOLT & NUT : BL/BL1

INSULATION	CODE	N	CONDITION	PRESS. (kg/cm2g)	TEMP. (°C)	AREA	W14									CONTRACTOR	PROJECT NAME
	THICK.	-	DESIGN	10	60	UNIT	R2FA									SK ecoplant	M15X Ph4 Project
			OPERATING	7.5	AMB	REF. PLAN DWG.										COMMODITY	JOB NO.
						CJ-M15W14-PI-A30-010015-B										AIR-DRY	22330D
						REF. P & ID										LINE NO.	SH'T NO. REV.
						CJ-M15W14-PR-A20-000082-B										50A-AIR-DRY-ST1-N-7005	01 / 01 0

경고 : 본 도면은 SK HYNIX의 기밀비밀 자료로서, 어떠한 경우에도 목적 외 사용, 복제, 제3자에게 공개, 누설 및 유출할 수 없으며, 회사는 유포자의 불법 사용으로 피해가 발생할 경우 유포자에게 민/형사상 책임을 요구할 수 있음.

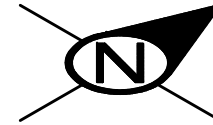[illegible]

CLIENT		11	
			
CONTRACTOR		PROJECT NAME	
AIR-DRY		M15X Ph4 Project	
COMMODITY		JOB NO.	
50A-AIR-DRY-ST1-N-7019		22330D	
LINE NO.		SH'T NO.	REV.
		03 / 04	0

