

DRAWING LIST FOR TEST PACKAGE

PROJECT NO.: 22328D

PROJECT TITLE : M15X Ph2 Project

BWW-649

No	PKG No	UNIT	LINE NUMBER			P&ID		REMARK
			ISO DRAWING No	SHEET	REV	P&ID No	REV	
1	649	1FA	OD280-BWW-HP1-N-7135-01	1 OF 1	1	CJ-M15W14-PR-A20-000312	1A	
2	649	2FA	OD280-BWW-HP1-E-7135-01	1 OF 1	1	CJ-M15W14-PR-A20-000312	1A	

ITEM NO.	W14-T-4706
SERVICE	RO CIP TANK
Q'TY	1
TYPE	VERTICAL & CYCINDRICAL
SIZE	ID x H m 2.4 x 4.0 (EH 3.2)
CAPA.	m3 18.1 (EH 14.5)
MAT'L	FRP

ITEM NO.	W14-EJ-4701
SERVICE	RO CIP TANK EJECTOR UNIT
Q'TY	1
CAPA.	NI/s.ea 6
MAT'L	STS304+ETFE

ITEM NO.	W14-STF-4707
SERVICE	RO CIP FILTER
Q'TY	1
TYPE	CARTRIDGE
SIZE	μm 5
CAPA.	m3/hr 360
MAT'L	SSC14 / PP

NOTE 10 1A


대외비



KEY PLAN (2F)

NOTE

1. 2m 이상 높은 곳에 설치된 밸브는 CHAIN VALVE 또는 PLATFORM 구성할 것.
2. 운전시 CLOSE 되는 배관에는 LOTO 설치.
3. CENTRIFUGAL PUMP
MAT'L 표기 : CASING / IMPELLER
4. (DELETED) 1A
5. CURBED AREA 및 내부 TRENCH DRAIN HOLE 적용할 것.
6. DELETED.
7. PORTABLE 계측기 공급 1SET (pH + COND.)
8. VALVE 후단에서 CHEMICAL PAIL 연결 부위는 내압호스를 사용하여 PAIL을 전부 비울 수 있어야 함.
9. 공급 : VENDOR / 설치 : SKEP
10. FILTER ELEMENT 순환 : 130EA 1A

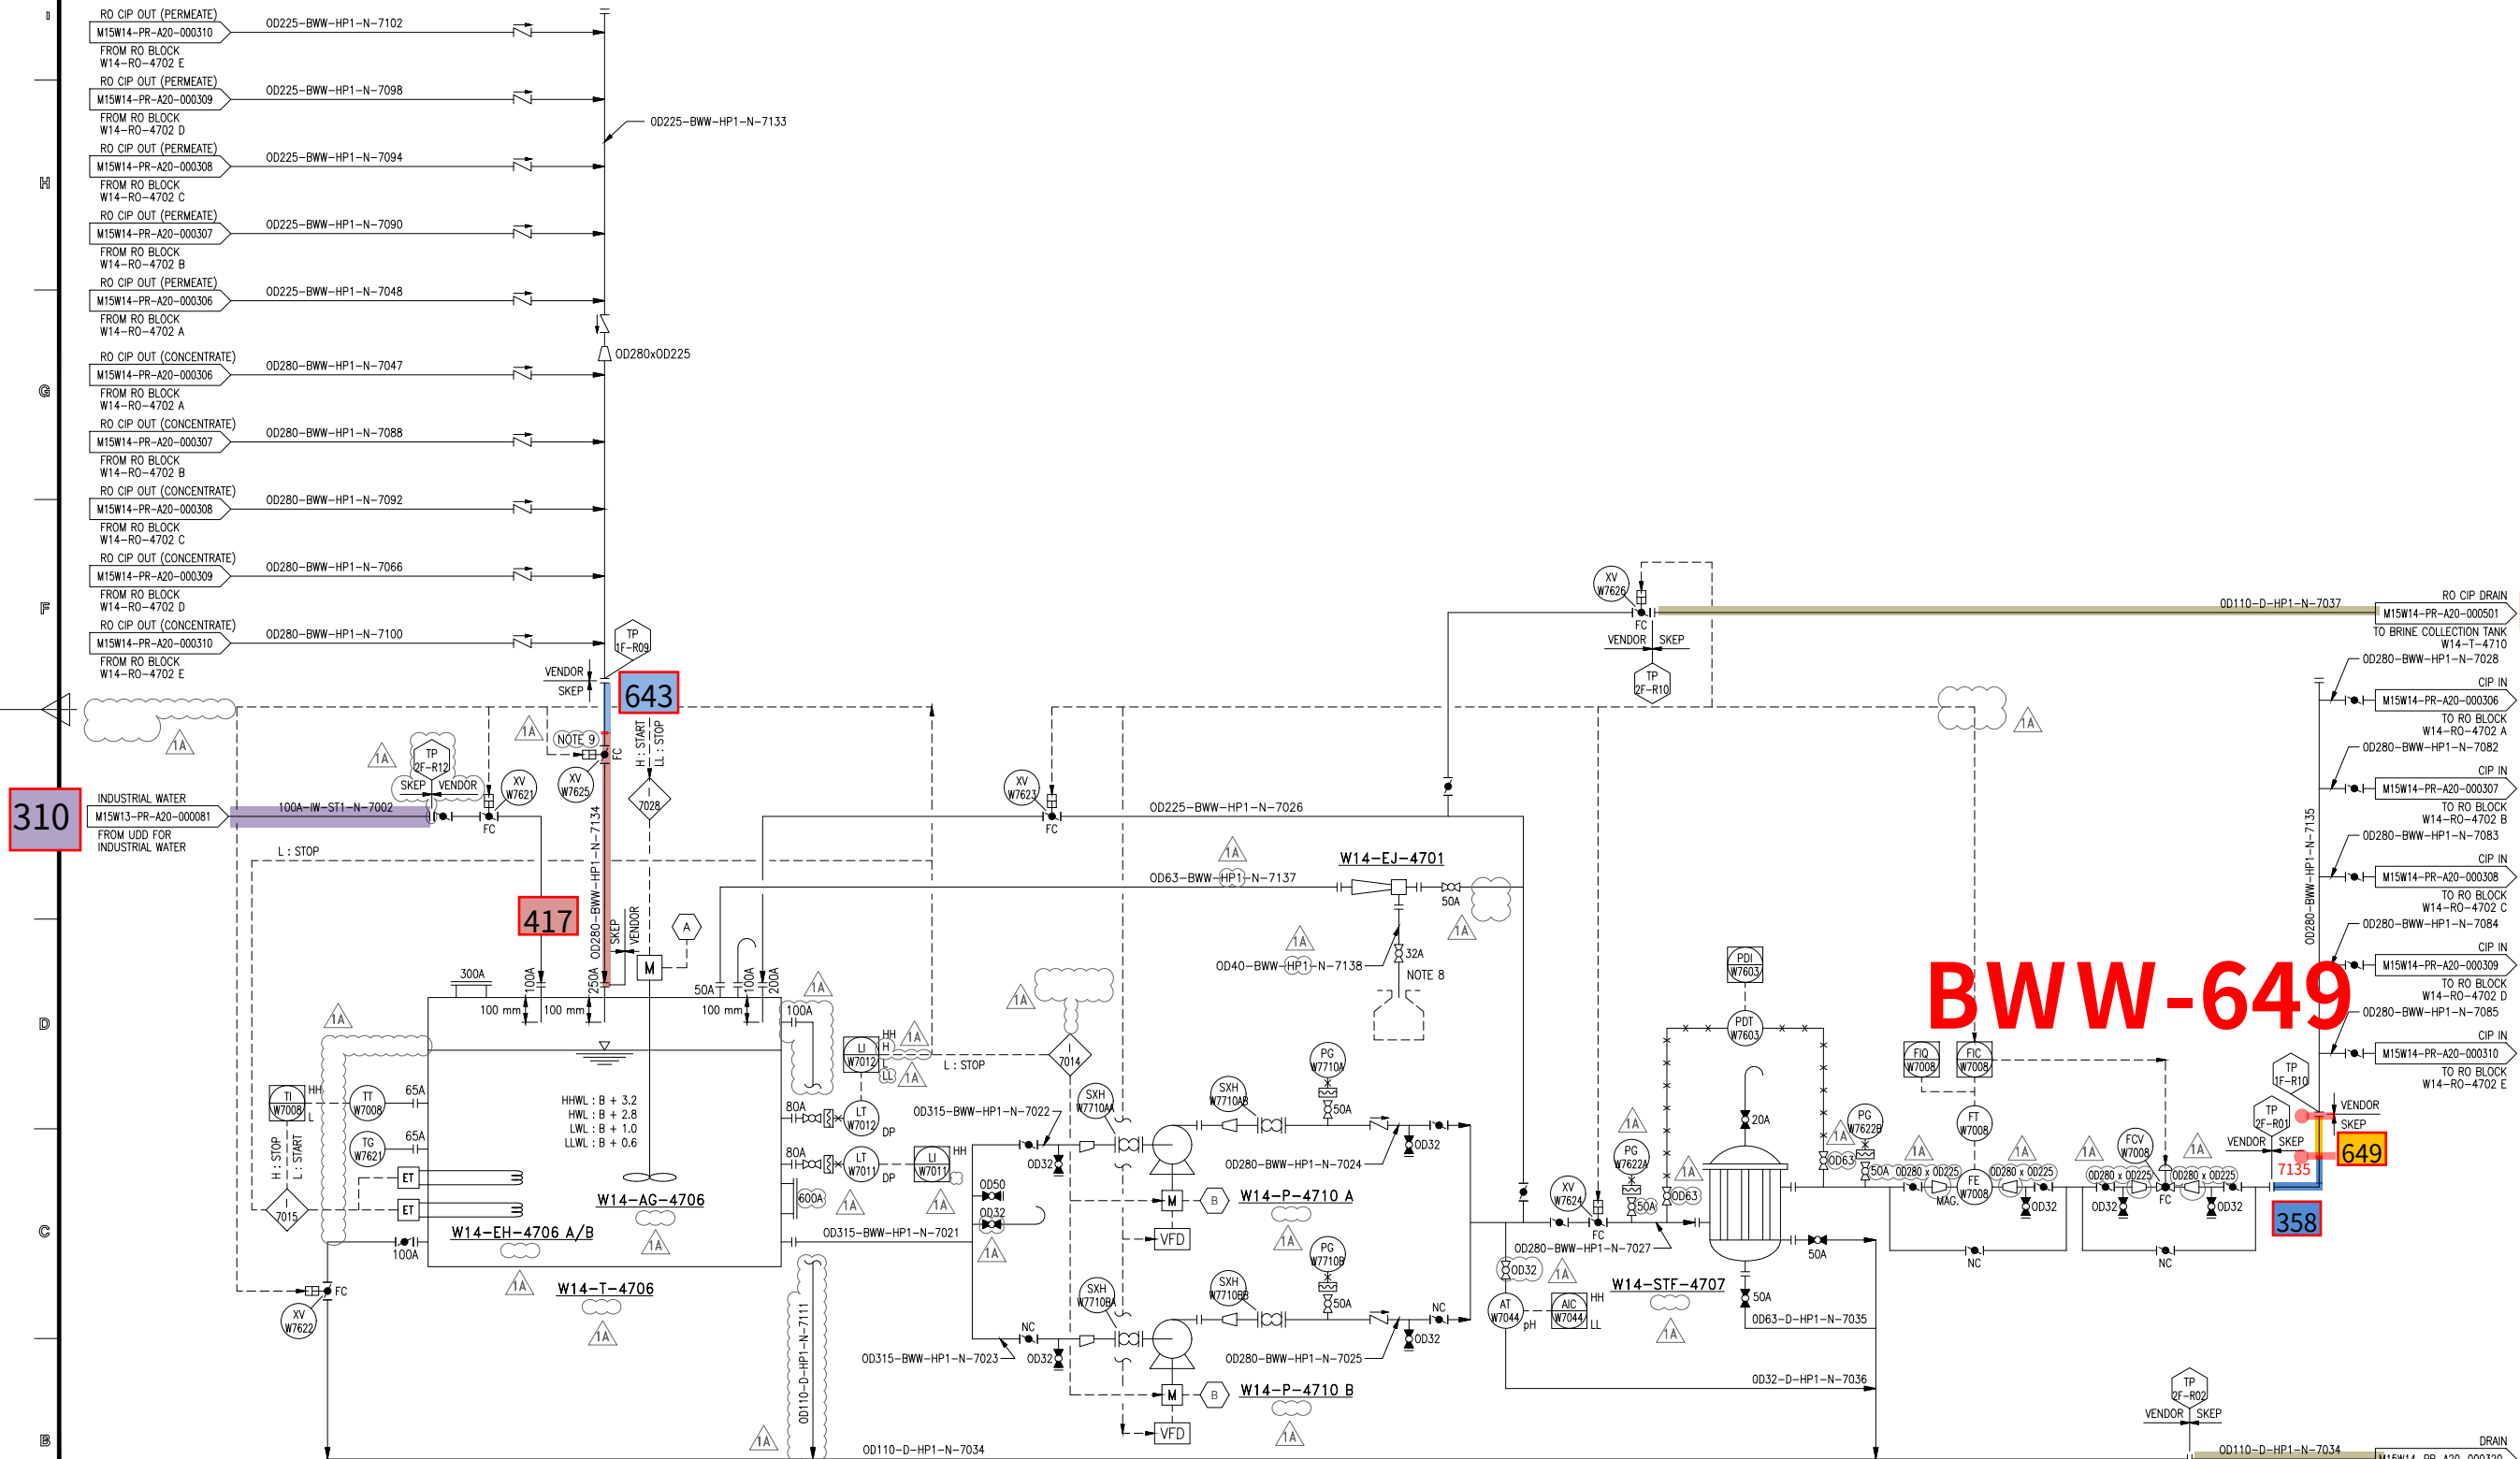

ITEM NO.	W14-EH-4706 A/B
SERVICE	RO CIP TANK ELECTRIC HEATER
Q'TY	2
MAT'L	STS316L
POWER KW	101

ITEM NO.	W14-AG-4706
SERVICE	RO CIP TANK AGITATOR
Q'TY	1
SPEED RPM	125
MAT'L	STS316
POWER KW	2.2

ITEM NO.	W14-P-4710 A/B
SERVICE	RO CIP PUMP
Q'TY	1 + 1
TYPE	CENTRIFUGAL (VWF)
CAPA.	m3/hr.ea x mH 360 x 40 (0.39MPa)
MAT'L	SSC14/SSC14
POWER kW	75

BWW-649

1A	REVISED AFC	25.08.14
1	REVISED AFC	25.01.17
0	APPROVAL FOR CONSTRUCTION	24.10.31
수정	실명	날짜
REV.	DESCRIPTION	DATE

제 도	이 인 학
DRAWN BY	
검 토	한 진 희
CHECKED BY	
승 인	박 동 영
APPROVED BY	
제 작 사	

SK 에코플랜트


공 사 명
PROJECT TITLE
M15X Ph4 WWT Project

면명
WG. TITLE
PIPING & INSTRUMENT DIAGRAM
RO CIP TANK & PUMP

속 척
SCALE
NONE


날 짜
DATE
2025. 08. 14

PROJECT NO. 22330D
도면번호
SHEET NO. CJ-M15W14-PR-A20-000312 1A

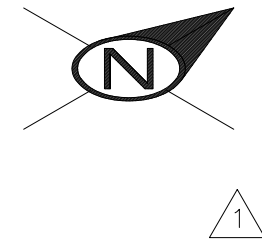

* PIPE : P/P1	* 90° ELBOW : E90	* 45° ELBOW : E45	* TEE : T	* RED.TEE : TR	* STUB-IN : STU	* REINFORCING PAD : RP	* CON.RED : RC	* ECC.RED : RE	* CON.SWAGE : RCS/RCS1	* ECC.SWAGE : RES/RES1	* NIPPLE : NP/NP1/NP2	* CAP : CAP/CAP1	* PLUG : PLG	* FULL COUPLING : FC	* HALF COUPLING : HF/HF1
* STUB-IN : STU	* SOCKET(HDPE/PVC) : SC	* SADDLE(HDPE) : SD	* FLANGE : F/F1	* GASKET : G/G1/G2	* BOLT & NUT : B/B1	* BLIND FLANGE : FB/FB1	* GATE VA. : VG/VG1/VG2	* BALL VA. : VB/VB1/VB2/VB2L	* BUTTERFLY VA. : VF/VF4	* CHECK VA. : VC/VC1/VC2/VC3/VC4/VC5/VC6/VC7					
* GLOBE VA. : VL/VL1/VL2	* DIAPHRAGM VA. : VD/VDL	* DAMPER : VP	* QUICK COUPLING : SQC	* FLEXIBLE JOINT(STEEL) : FLXB	* FLEXIBLE JOINT(RUBBER) : FLXR	* FLEXIBLE JOINT(STEEL PTFE LINED) : FLXL	* FLEXIBLE HOSE : FLXH	* STEAM TRAP : ST	* SPRAY NOZZLE : SPN	* EMERGENCY SHOWER : SSH					
* STRAINER(Y-TYPE) : YSTR	* STRAINER(T-TYPE) : TSTR	* STRAINER(BUCKET-TYPE) : BSTR	* ANCHOR PLATE : STOP	* BIRD SCREEN : BS	* ISOLATION KIT : IK	* UNLOADING BOX : UB	* AIR TRAP : AT	* LOTO : LOTO	* SIGHT GLASS : SG	* PRESSURE GAUGE : PG	* SHIELD : SH	* SPECIAL BOLT & NUT : BL/BL1			

고 : 그 요, SK HYNIX의 기업비밀 자료로서, 어떠한 경우에도 목적 외 사용, 복제, 제3자에게 공개, 누설, 무단으로 제공되는 것을 금지하고 있는 것인데, 회사 측은 공표자나 피해자를 특정할 수 없는 경우 공표자에게 민·형사상 책임을 물을 이유가 없다고 주장하는 거요?

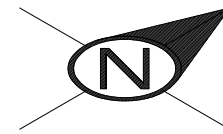

1. TRAY & ANGLE, CHANNEL SUPPORT가 적용되는 배관 ELEVATION은 현장 맞춤으로 한다.
2. (*) FIELD ADJUST



CLIENT  2



2

CONTRACTOR		PROJECT NAME	
COMMODITY	BWW	M15X Ph4 Project	
LINE NO.	0D280-BWW-HP1-E-7135	JOB NO.	22330D
		SH'T NO.	REV.
		01 / 01	1